




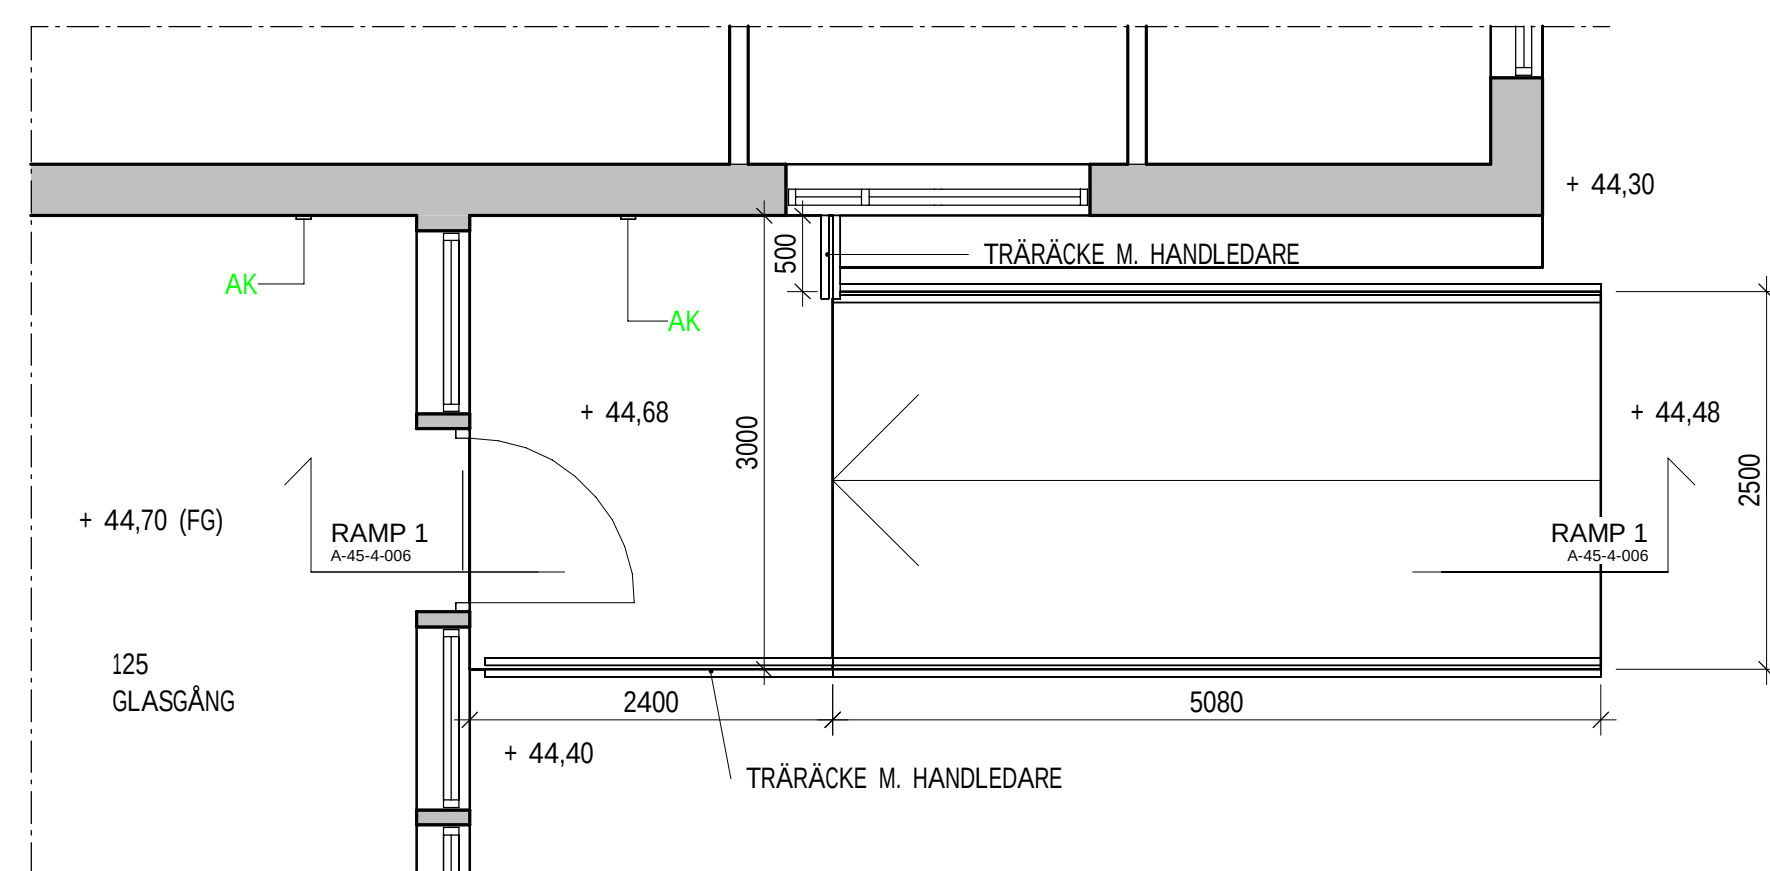


PLAN 1 - RAMP FÖRSKOLA
1 : 50

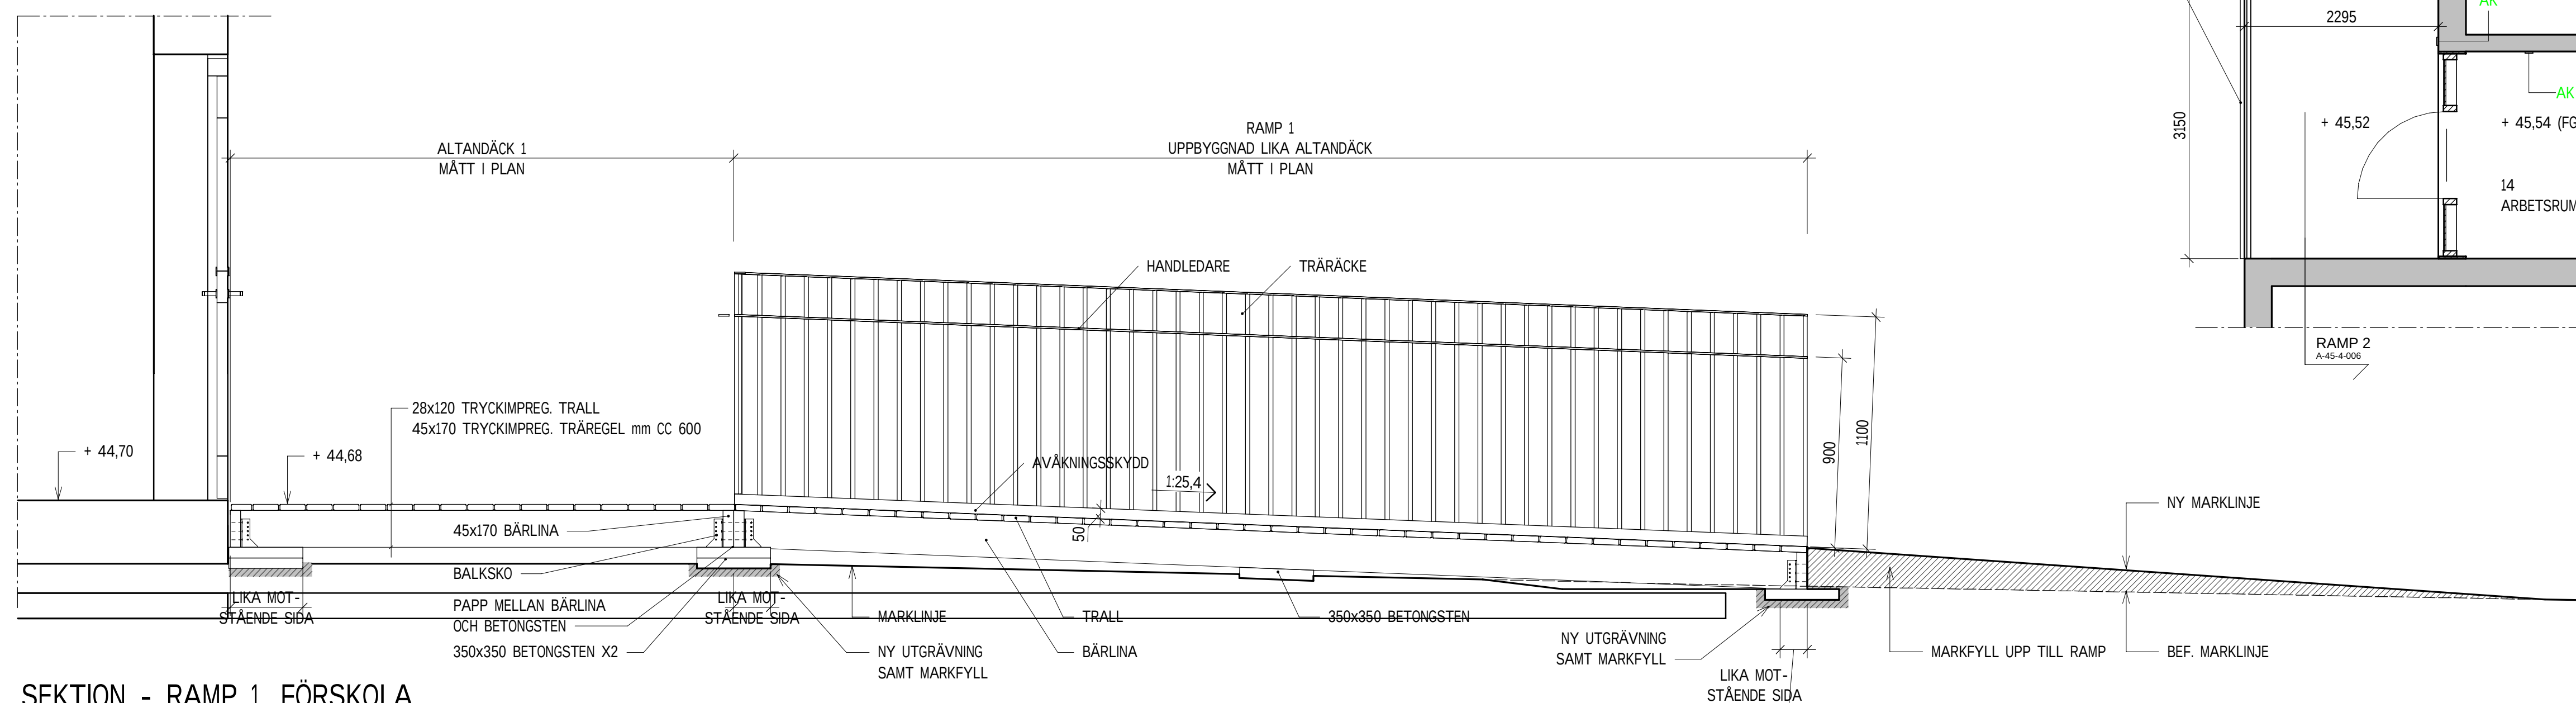


SEKTION - RAMP 1, FÖRSKOLA
1 : 20

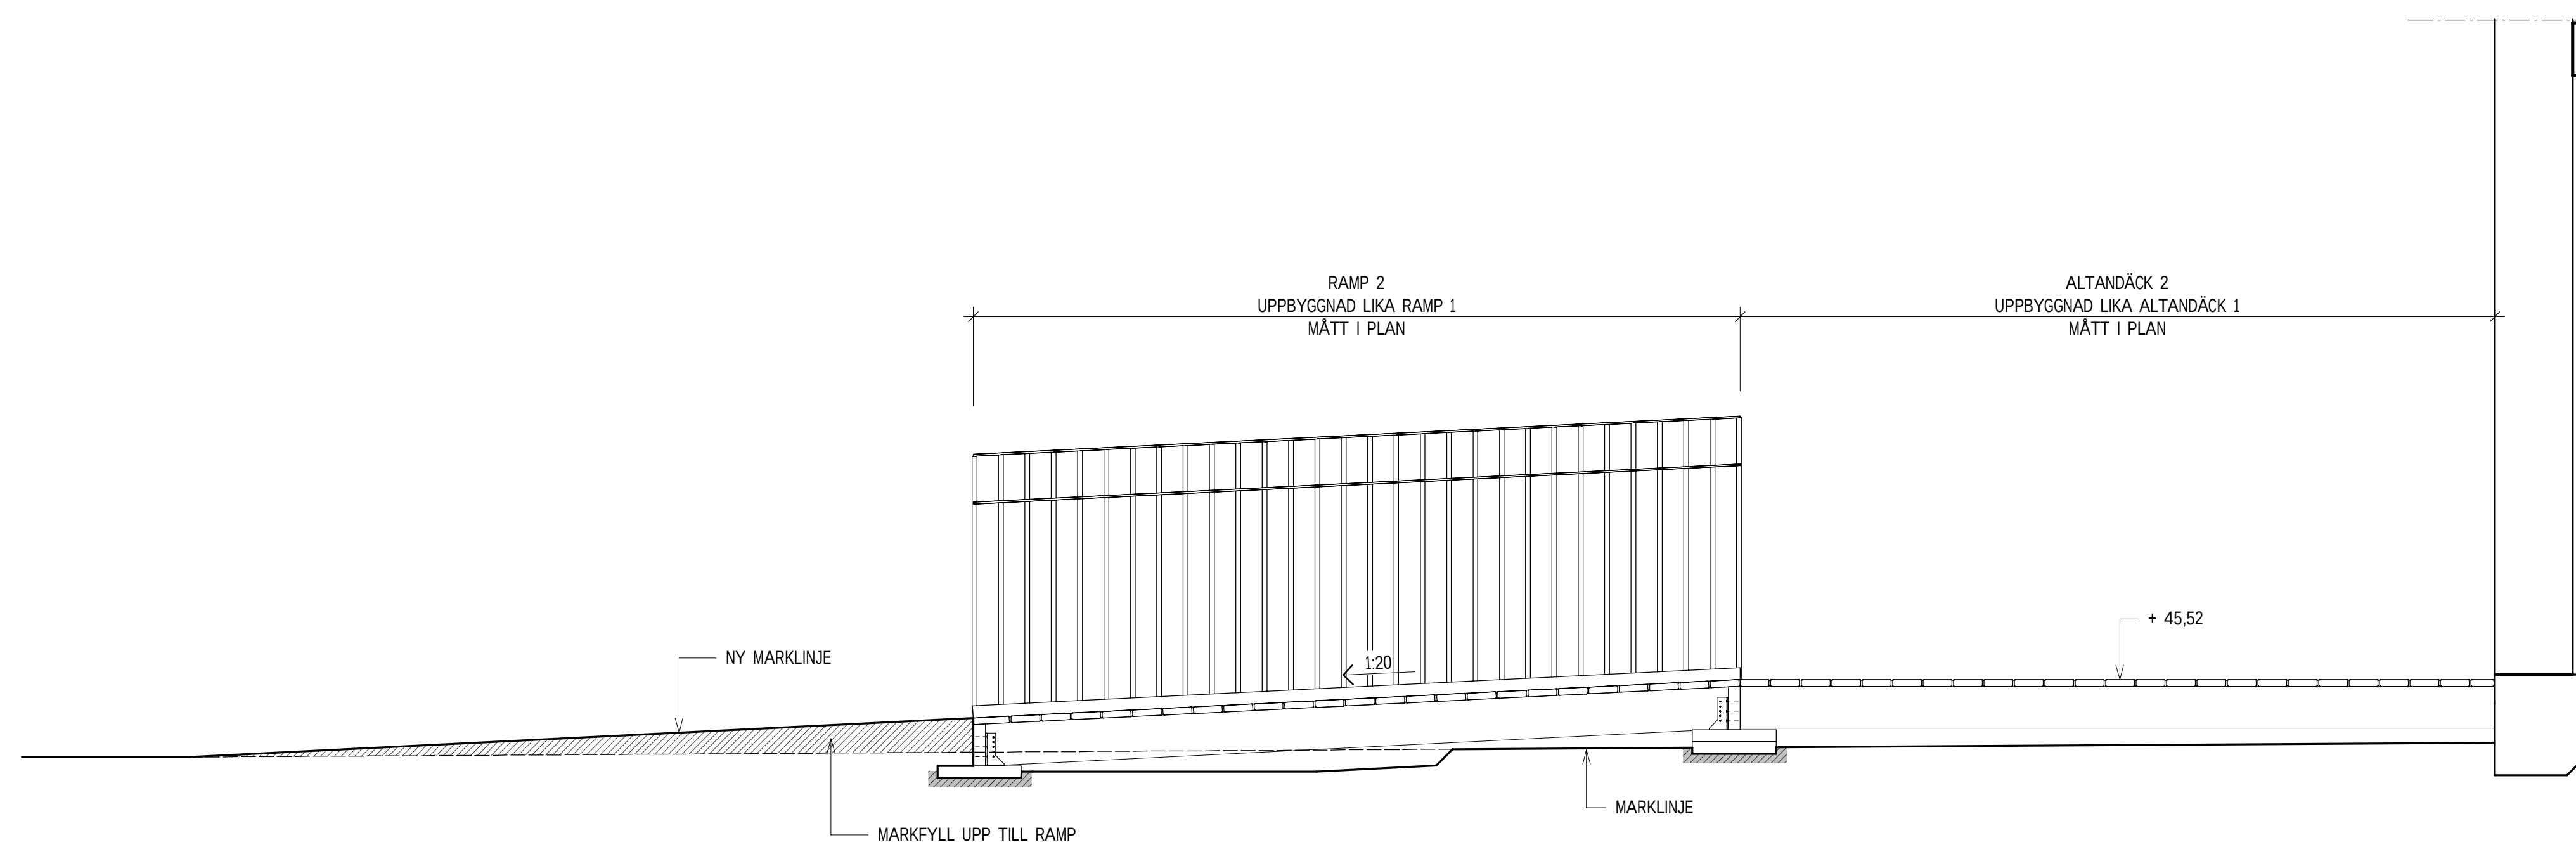

SEKTION - RAMP 2, FRITIDS
1 : 20

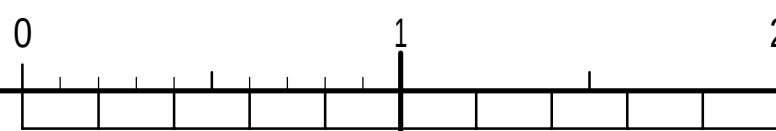

PLAN 1 - RAMP FRITIDS
1 : 50

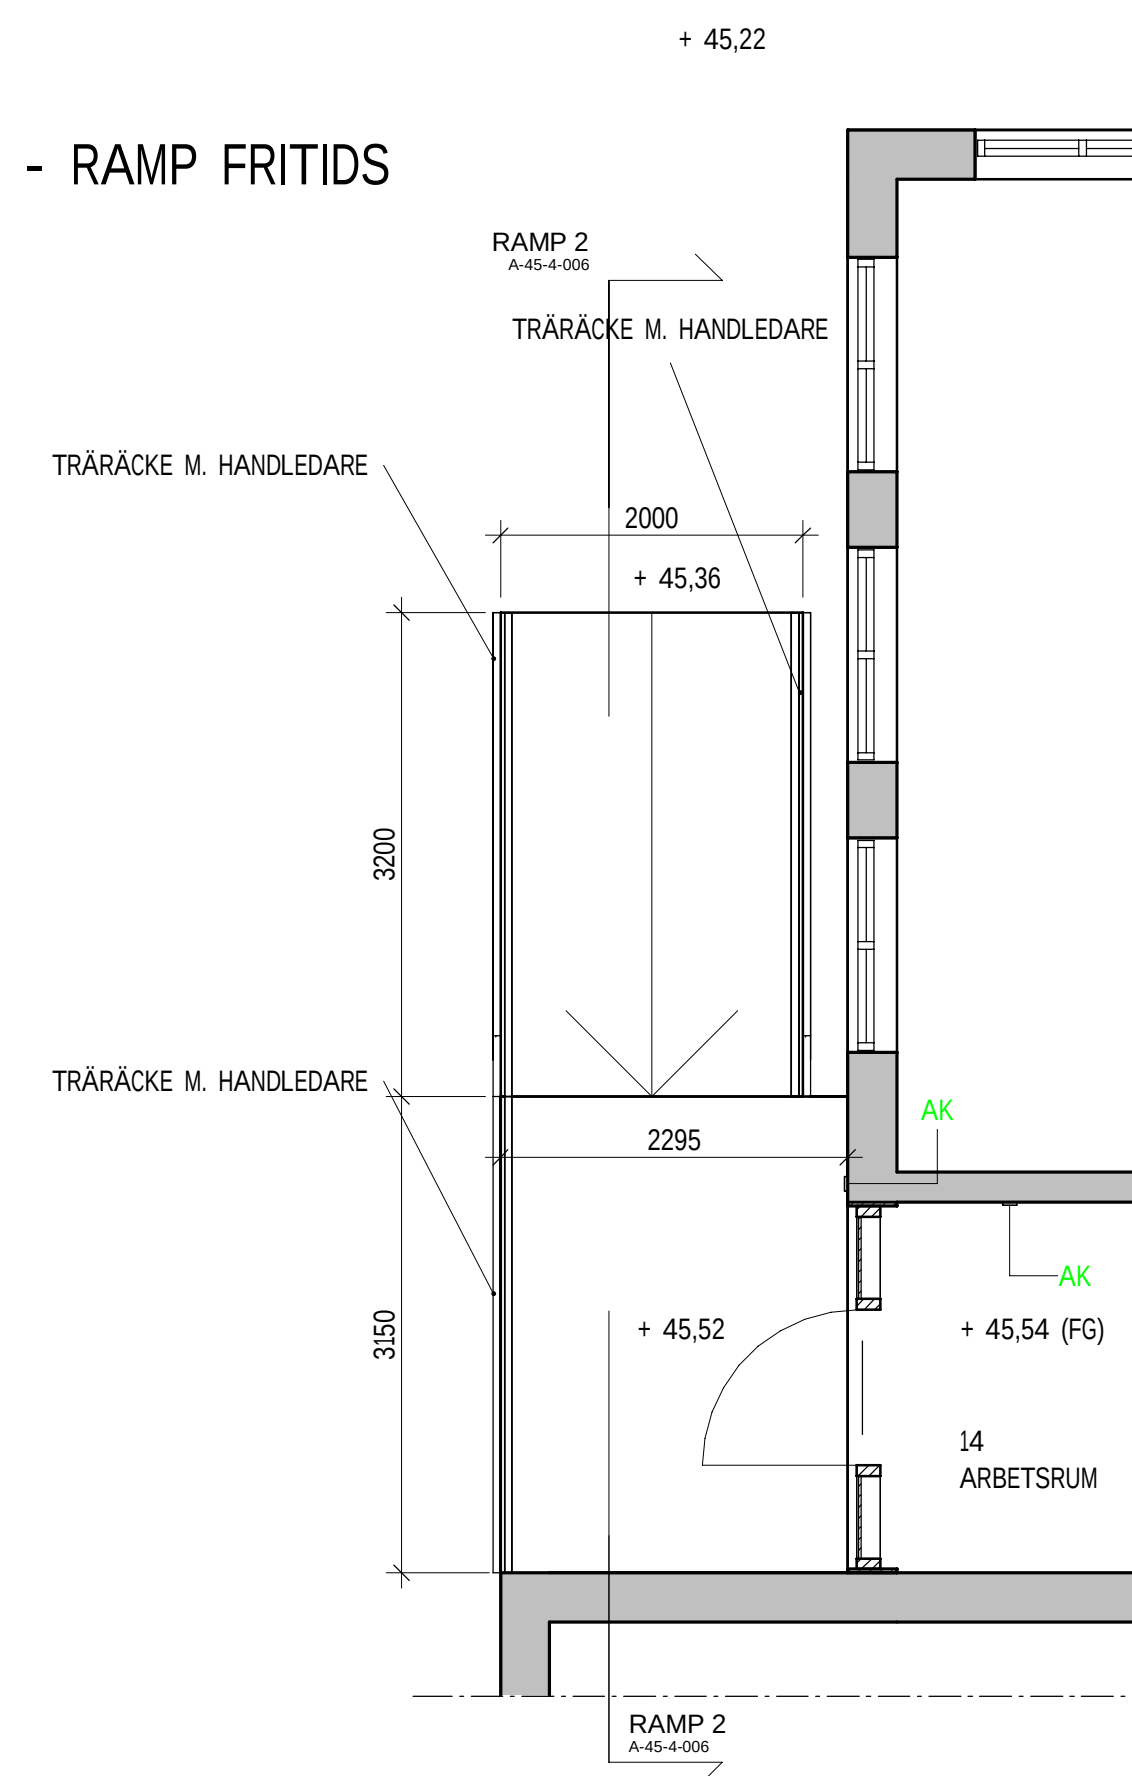

FÖRKLARINGAR

Samtliga mått anges i millimeter. Plushöjder i meter.
Mått kontrolleras på plats innan tillverkning.
Marklinjer är ungefärliga. Anpassningar mot befintlig
mark görs på plats.

FÖRESKRIFTER


Rampleverantören dimensionerar bärigheten och levererar erforderlig infästningsskruv.

Ramp och vilplan inklusive konstruktion i tryckimpregnerat trä.
Avkörningsskydd på sidorna på rampen.
Mått enl. planen.

TRALL: Rillad trall 28x120 mm
AVÅKNINGSSKYDD: 28x95 mm

HÄNVISNINGAR

ORIENTERINGSLPAN A-40-0-100

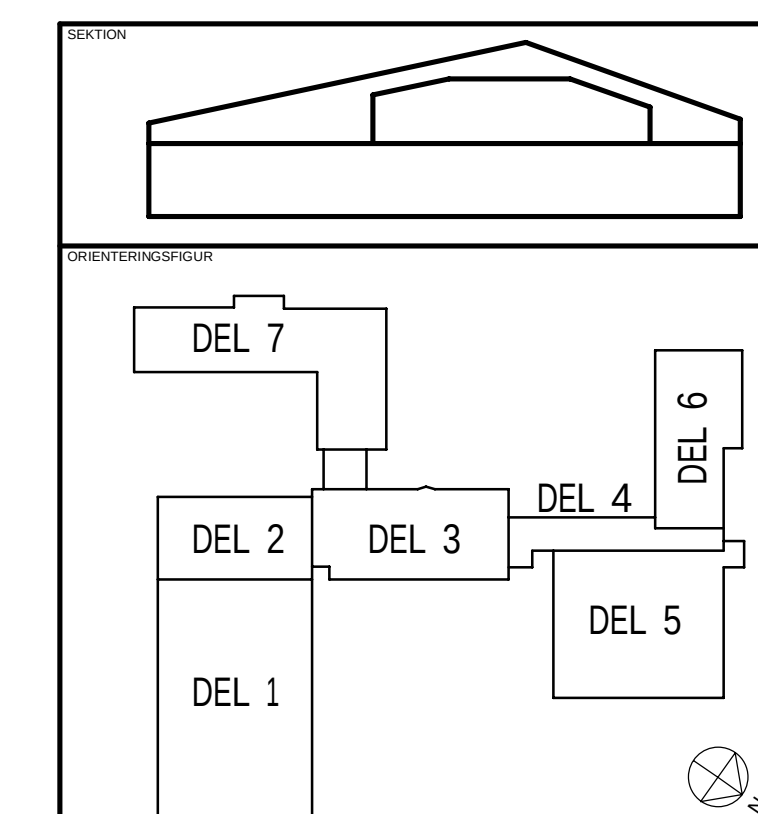

STATUS:			
FÖRFÖRÅGNINGSUNDERLAG			
HANDLING			
BYGGNINGSDOKUMENT		ANDRINGS FM	
DATUM		GÖRANINGS AV	
2024-12-20		T. ROBERTSFÖR	
BESTÄLLARE			
 ROBERTSFÖR KOMMUN			
PROJEKTNAMN			
CENTRALKÖK			
OMRÅDE			
ROBERTSFÖRS KOMMUN			
PROJEKTNUMMER		ADRESS	
		YTTR RINGVÄGEN 4	
BILAGENUMMER		PASTOCHET	
		FORDONET 1	
FÖRSTÄMMAN		NORCONSULT SVERIGE AB	
UPPGIFTSNUMMER		SKAPAD AV	
108 83 71		SBS	
TELEFON		KONTAKTPERSON	
010 144 80 00		TOMAS BERGSTROM	
BYGGNINGSVERK		FLUSLÖRD (RD 2000)	
VÄNINGSPLAN		VÄNINGSDIAG	
		DELOMRÅDE	
SYSTEM			
45 HUSKOMPLETTERINGAR			
SPECIFICATION			
RAMP I TRÄ			
RITNINGSKATEGORI		SKALA	FORMAT
PLAN, SEKTION		1:20	A1
DOKUMENTNUMMER		ANDRING	
A-54-006			