




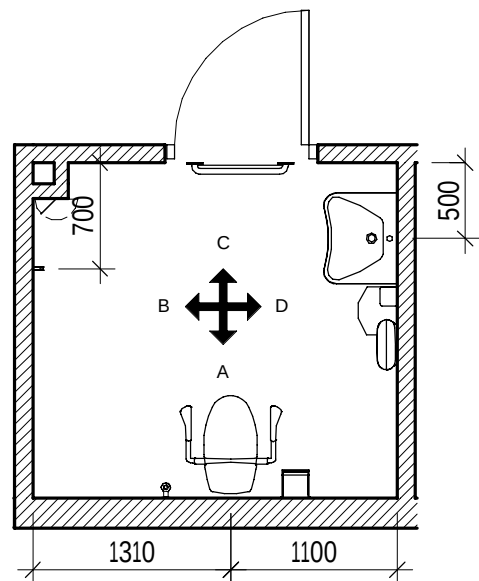


PLAN RWC 1007
1 : 50

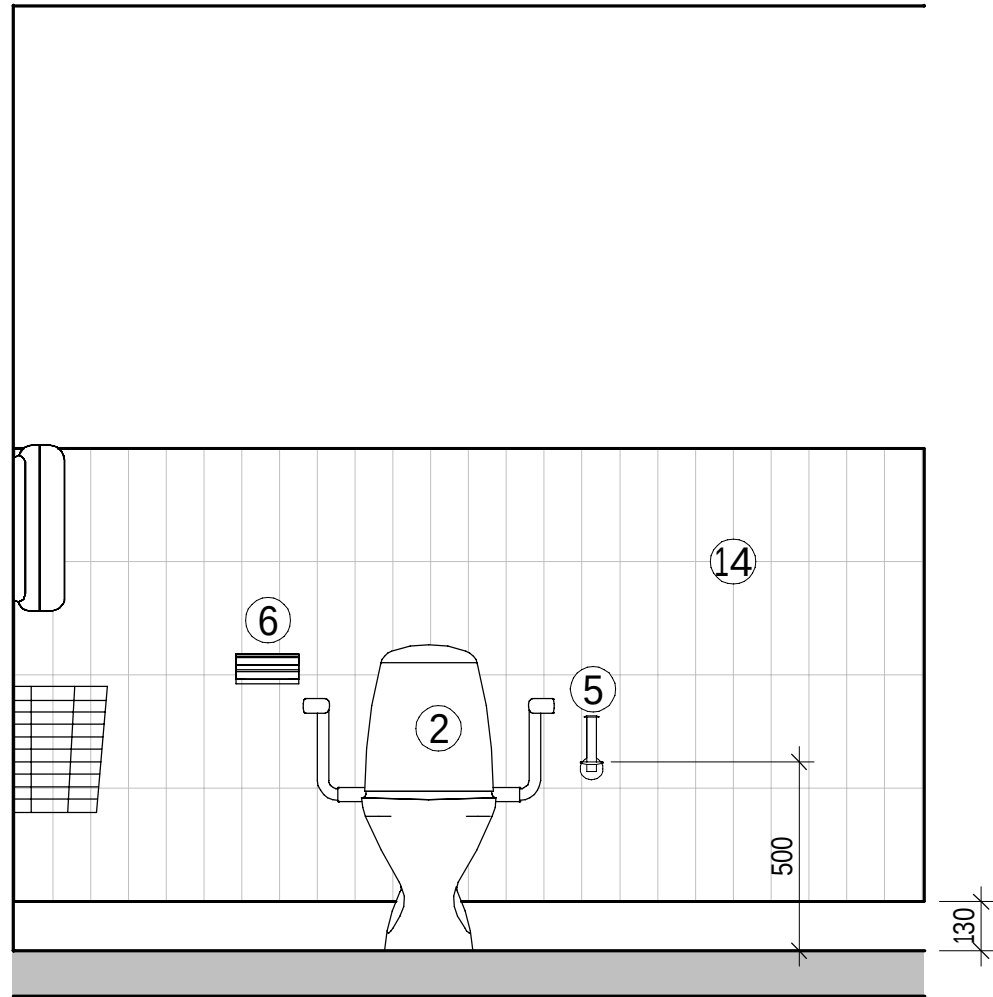


ELEVATION RWC 1007-A
1 : 20

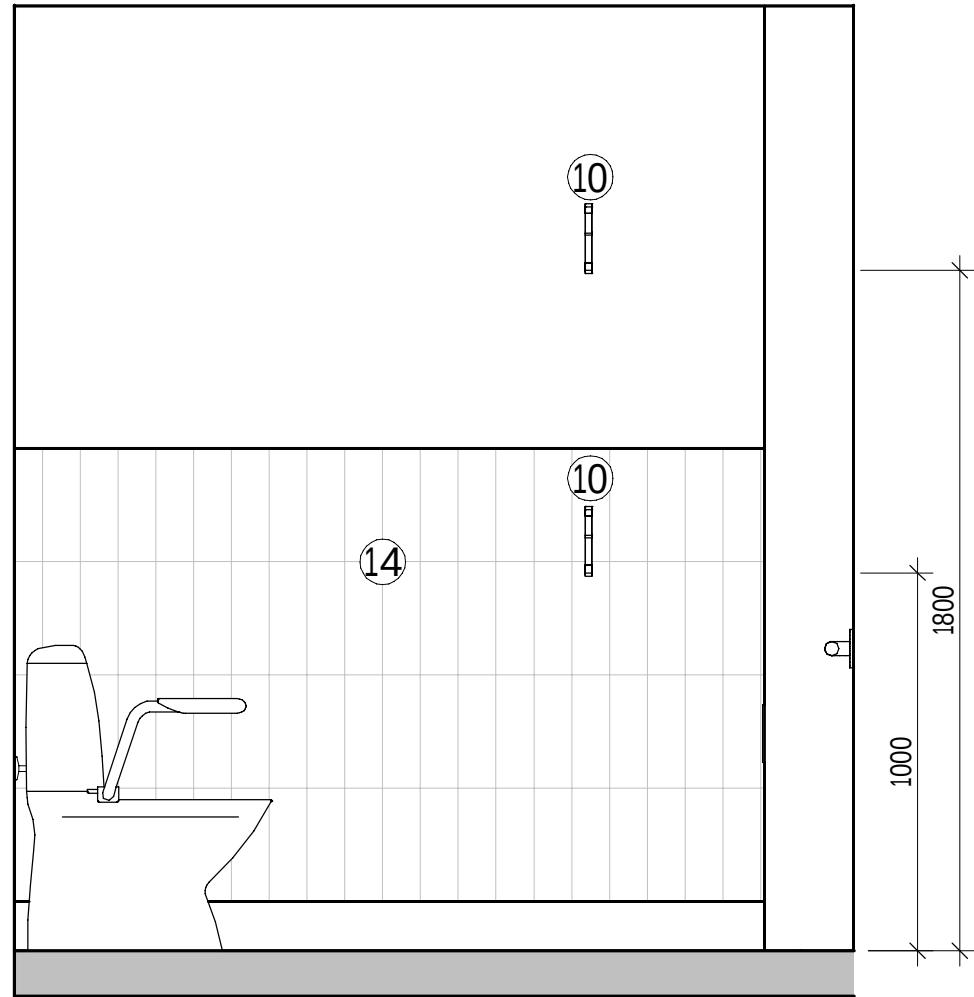


ELEVATION RWC 1007-B
1 : 20

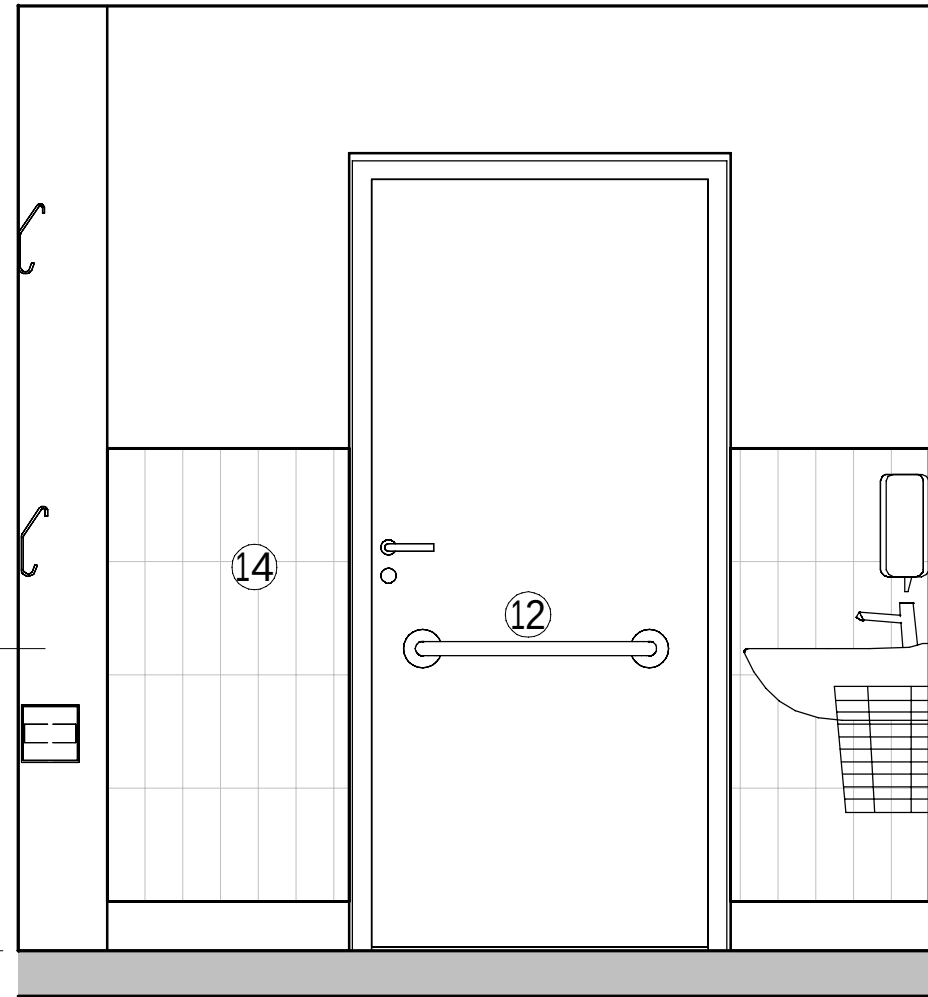


ELEVATION RWC 1007-C
1 : 20

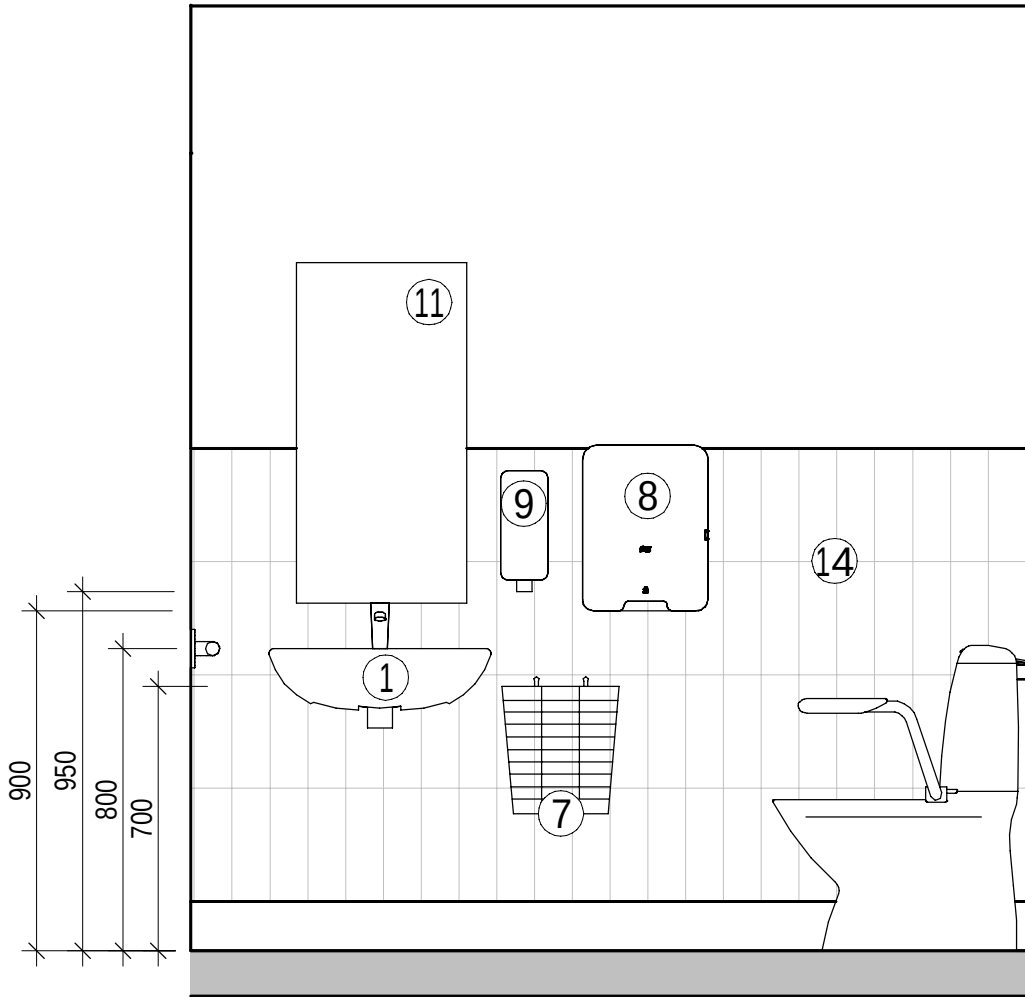


ELEVATION RWC 1007-D
1 : 20

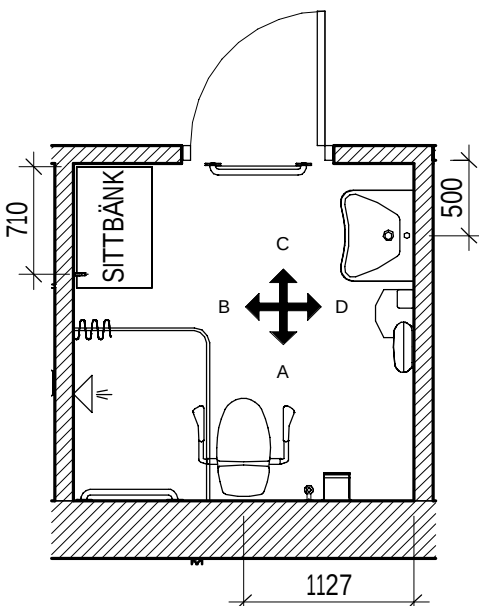


PLAN RWC/D 1016
1 : 50

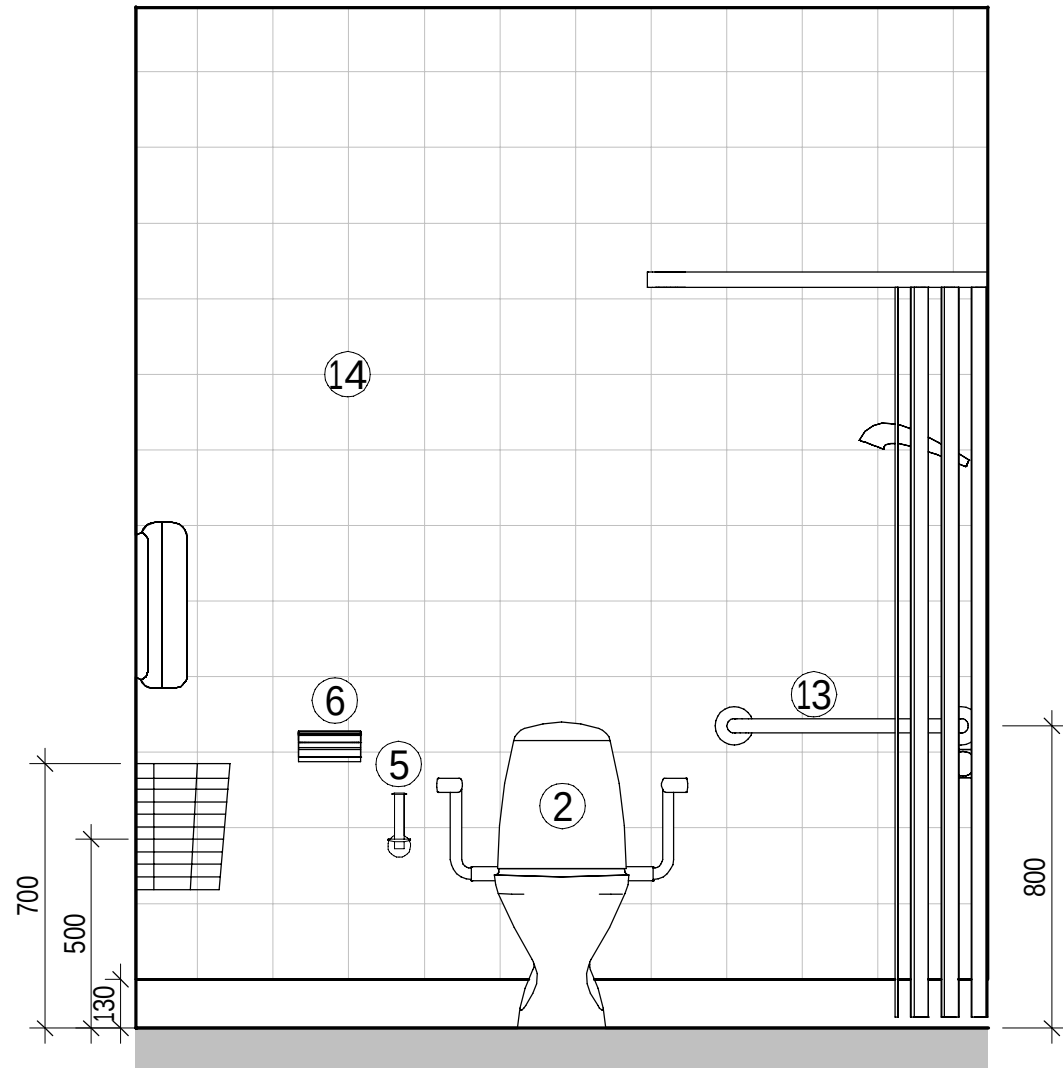


ELEVATION RWC/D 1016-A
1 : 20

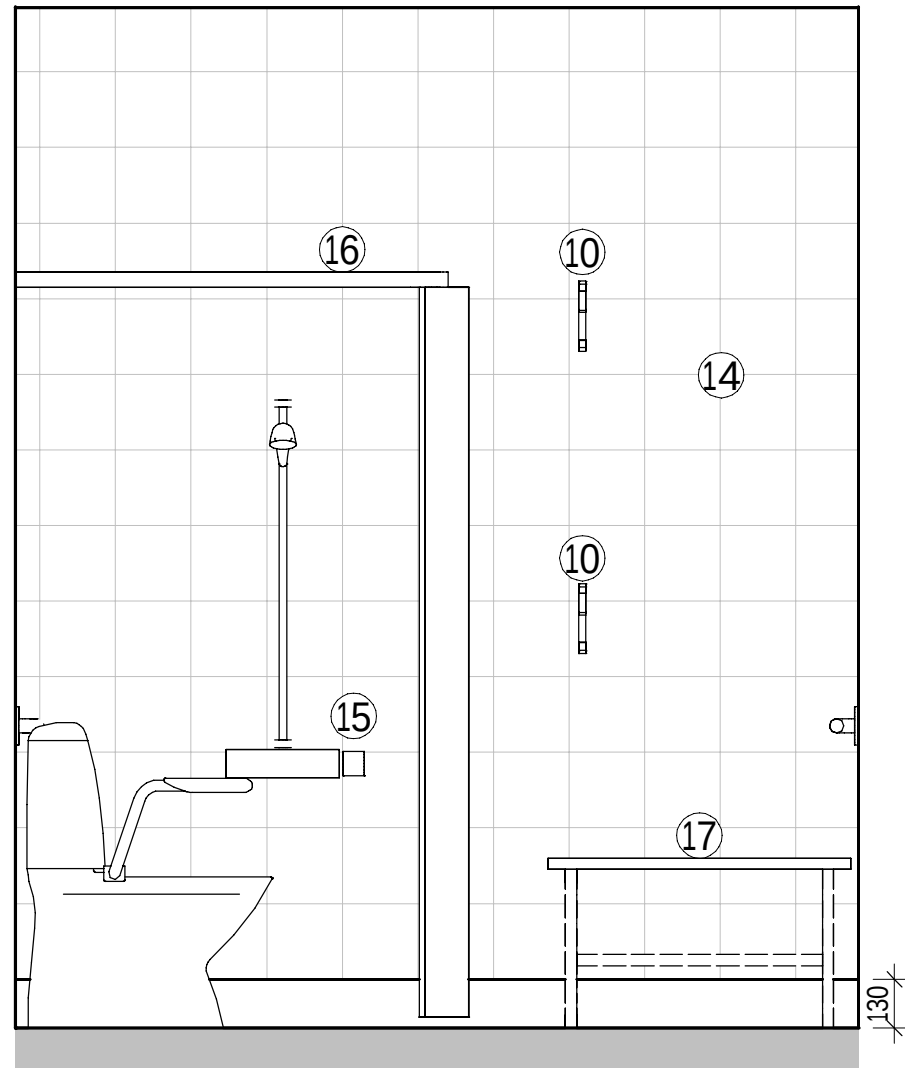

ELEVATION RWC/D 1016-B
1 : 20

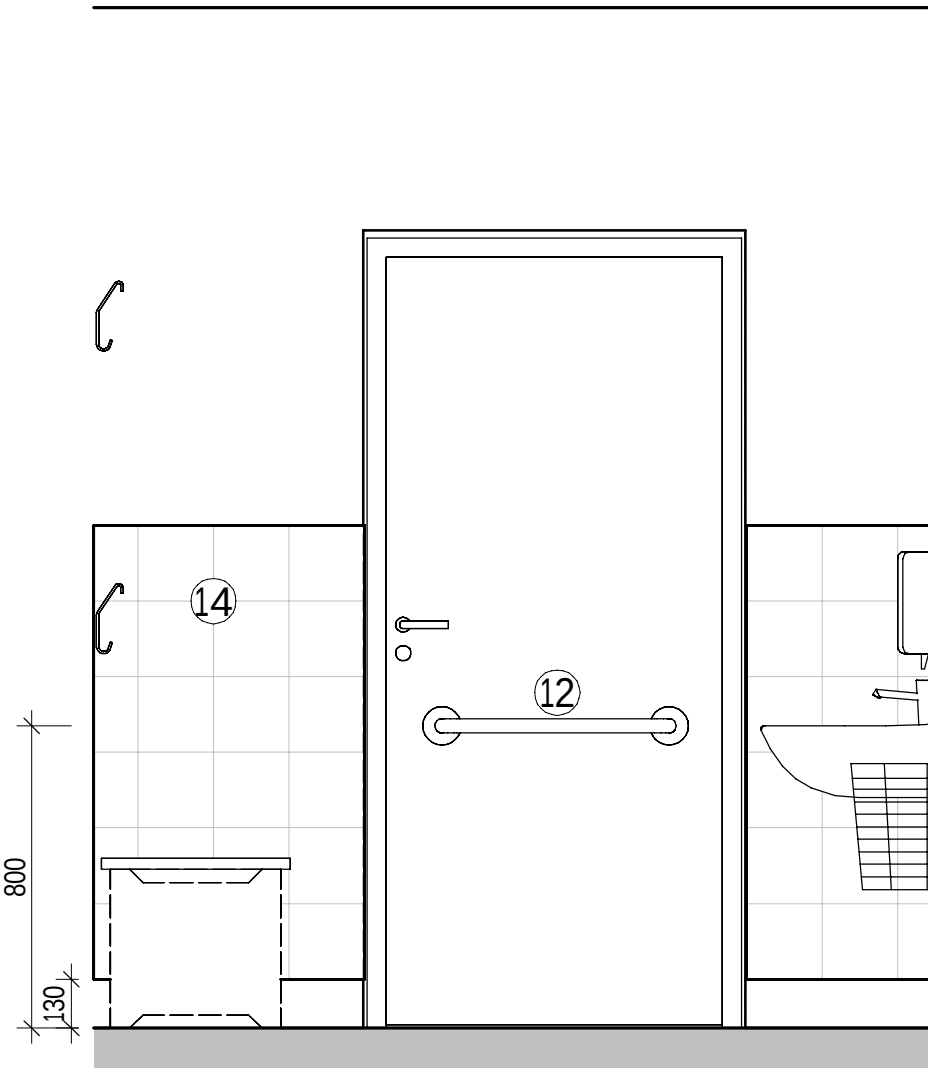

ELEVATION RWC/D 1016-C
1 : 20

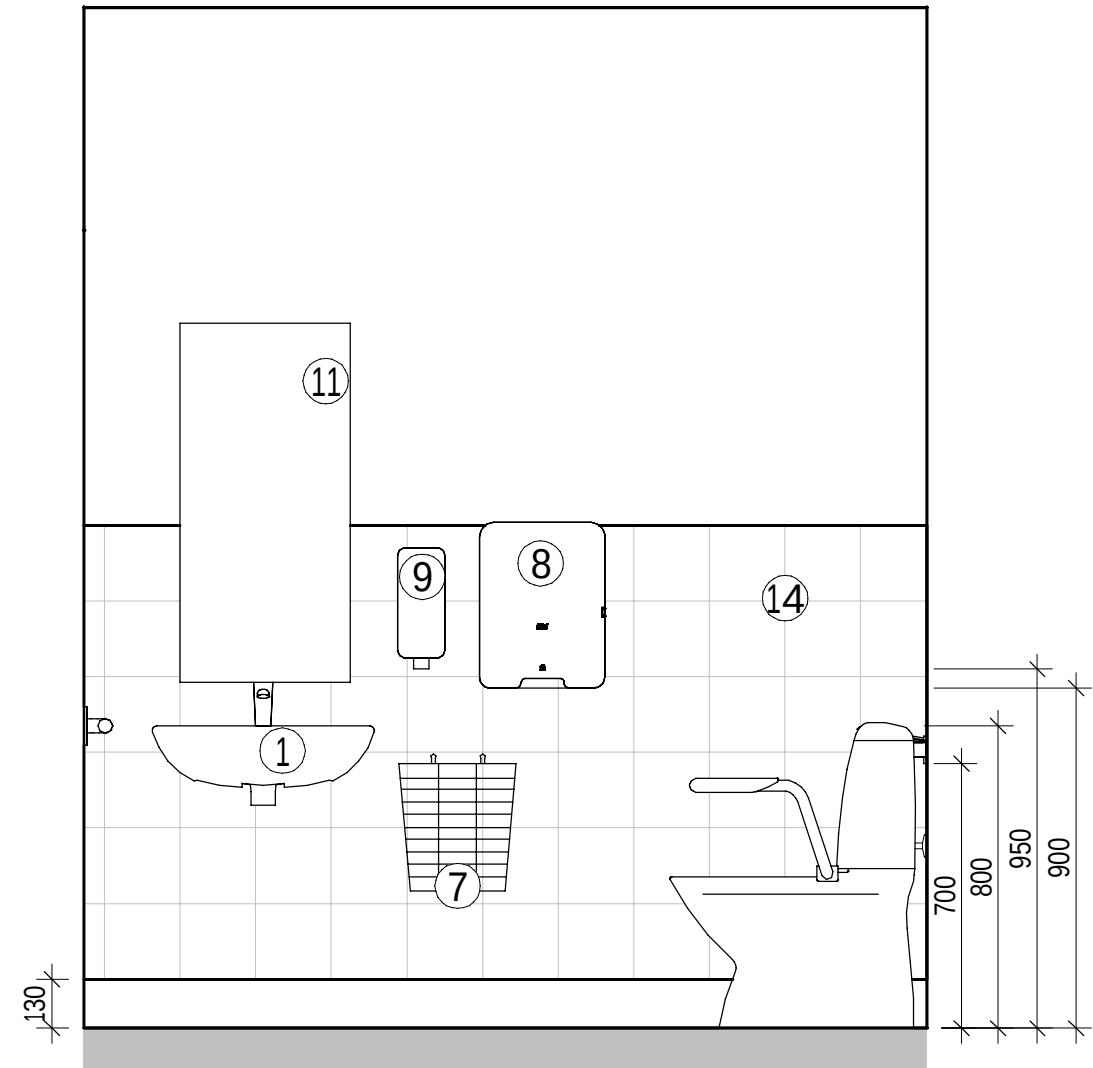

ELEVATION RWC/D 1016-D
1 : 20

FÖRKLARINGAR

Samtliga mått anges i millimeter.
Mått kontrolleras på plats innan tillverkning.

- HANDFAT ENL. RÖR
- RWC-STOL MED ARMSTÖD & TP-HÅLLARE ENL. RÖR
- WC-STOL ENL. RÖR
- TOALETTPAPPERSHÅLLARE
- RESERV TP-HÅLLARE
- SANTITETSPAPPERSHÅLLARE
- PAPPERSKÖR
- HANDDUKSSKÅP
- TVÅLSPENSER
- KLÄDKRÖK
- SPEGEL
- DRAGHANDTAG
- STÖDHANDTAG
- KAKEL ENLIGT RUMSBESKRIVNING
- DUSCHBLANDARE ENL.RÖR
- DUSCHDRAPERISTÅNG
- SITTBÄNK typ Nostalgi Bänk Essem Design el. likv. Bredd 800 mm Kulör: Svart/Svart

HÄNVISNINGAR

- PLAN - ÖVERSIKT, BRAND A-40-1-001
PLAN 1, DEL 4.2 A-40-1-142
PLAN 1, DEL 5.3 A-40-1-153

SEKTION		
ORIENTERINGSSKISS		
STATUS		
FÖRFRÅGNINGSUNDERLAG		
HANDLING		
BYGGHANDLING		
DATUM	UTARBETAD AV	ANSVARIG PM
2024-12-20	T. BERGSTRÖM	
BESTÄLLARE		
ROBERTSFORS KOMMUN		
PROJEKTNAMN		
CENTRALEKÖK		
KONTRAKT		
ROBERTSFORS KOMMUN		
PROJEKTNUMMER	ADRESS	
	YTRE RINGVÄGEN 4	
DIREKTOR	FASTIGHET	
	FORDONET 1	
DISCIPLIN	FÖRETAG	
A	NORCONSULT SVERIGE AB	
UPPDRAGSRUMMER	SKAPAD AV	
108 83 71	SBS	
TELEFON	KONTAKTPERSON	
010 141 80 00	TOMAS BERGSTRÖM	
BYGGNADSTYP	FLUSKOD (VIT 2008)	
VÄRNINGSPLAN	VÄRNINGSD	DELOMRÅDE
1		DEL 4.2, 5.3
SYSTEM		
46 RUMSKOMPLETTERINGAR		
SPECIFIKATION		
RWC & RWC/D		
BYGGNADSTYP	SKALA	FORMAT
UPPSTÄLLNING	1:20	A1
DOCUMENTNAMN	ANSVARIG	
A-46-6-001		

SKALA 1:20 0 1 2 METER

