

FÖRKLARINGAR

HP = HYLLPLAN
PB = PASSBIT
TS = TÄCKSIDA
UL = UNDERLIMMAD

FÖRESKRIFTER

FAST INREDNING, BÄNKSIVA SAMT BESLAG SKA VARA FABRIKAT MARBODAL ELLIKVÄRDIGT OCH AVSER PAUSRUM 1022.

MÄTT ANGES I MILLIMETER.
ENTREPRENÖREN SKA KONTROLLERA SAMTLIGA MÄTT PÅ PLATS INNAN BESTÄLLNING AV DEN FASTA INREDNINGEN.

FÖRESKRIFTER ENLIGT SVENSK BYGGSTANDARD.
MÄTTSAMORDNING FÖR KÖKSINREDNING OCH APPARATER ENL. SS-EN 1116:2018. SÄKERHET OCH PROVNING ENL. SS-EN 14749:2016+A1:2022

SKÅPSTOMMAR MONTERAS PÅ JUSTERBARA BEN MED LÖSTAGBRA SOCKLAR. SOCKLAR UTFÖRS UTAN SKARVAR. SKÅPINREDNING, BÄNKSIVA OCH ÖVRIGA KÖKSSNICKERIER SKA VARA KOMPLETT UTRUSTADE MED LUCKOR/FRONTER, BÄNKSIVA, BESLAG O DYL.
SAMTLIGA SKÅPINREDNINGAR SKA VARA FAST MONTERADE.

FÖRESKRIFTER

SKÅPSTOMME; SKÅPSTOMME AV VIT MFC. EXPONERAD SIDA TÄCKS MED TÄCKSIDA.

LUCKA; ARKITEKT PLUS, KULÖR SAND. SLÅT MÅLAD LUCKA AV MDF MED SVAGT RUNDAD KANT.

TÄCKSIDA/PASSBIT; KULÖR/MATERIAL LIKA LUCKA.

TAKANSLUTNING; KULÖR/MATERIAL LIKA LUCKA.

SOCKEL; KULÖR/MATERIAL LIKA LUCKA.

BESLAG; RIO, SVART CC128

BÄNKSIVA; LAMINAT RUSTIK LJUS 590. KANTLISTER LIKA LAMINAT.

STÄNKSKYDD; KAKEL ENLIGT RUMSBESKRIVNING. OMFATTNING ENLIGT RITNING.


HYLLPLAN; EKFAÑER 800x400 mm, TYP ART. NR 2422-, HYLLTEKNIK ELLER LIKV.

KONSOL; VINKELKONSOL 370 mm, TYP ART. NR 74340, MATTSVART, HYLLTEKNIK ELLER LIKV.


- ÖVERSKÅP. GÅNGJÄRN MONTERAS DOLDA MED STÄNGNINGS & DÄMPNINGSFUNKTION
- UNDERSKÅP UTFÖRS MED 1ST MJUKSTÄNGADE LÄDOR MED FULLT UTDRAG.

HÄNVISNINGAR


PLAN - ÖVERSIKT, BRAND A-40-1-001
PLAN 1, DEL 5.3 A-40-1-153
PLAN 1, DEL 5.4 A-40-1-154

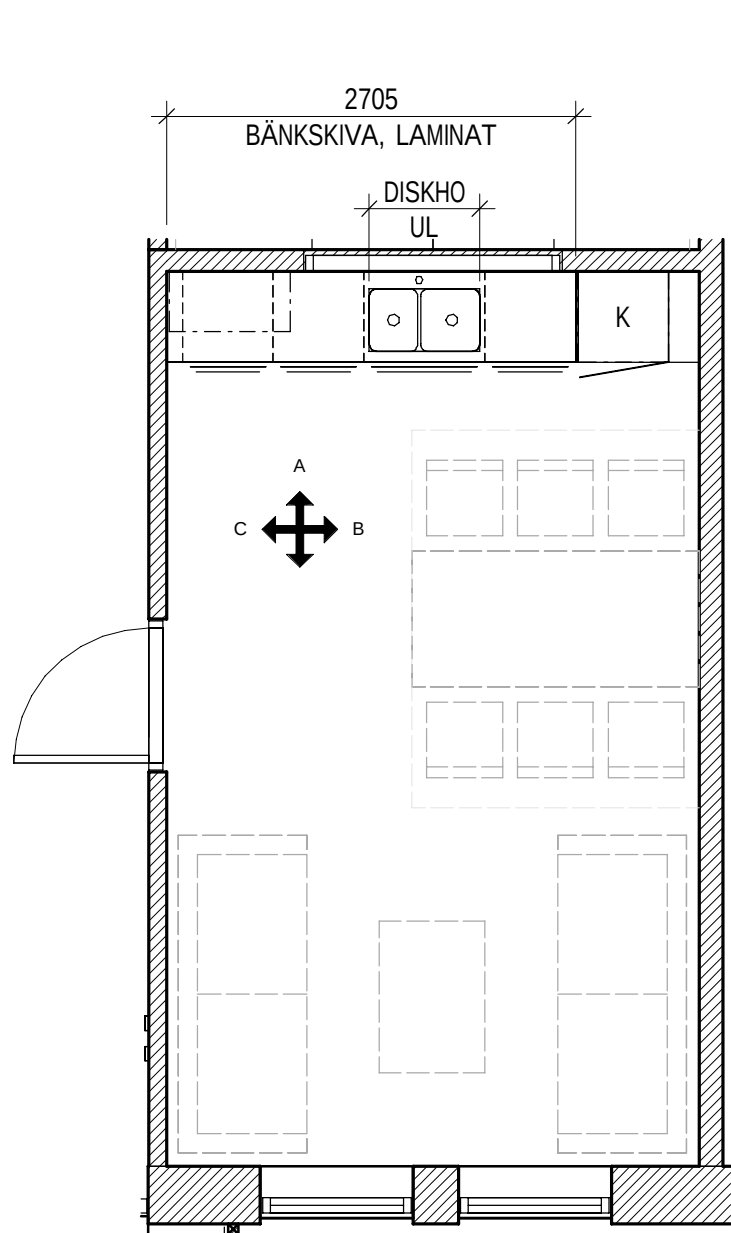


PLAN PAUSRUM 1022 - PENTRY
1 : 50

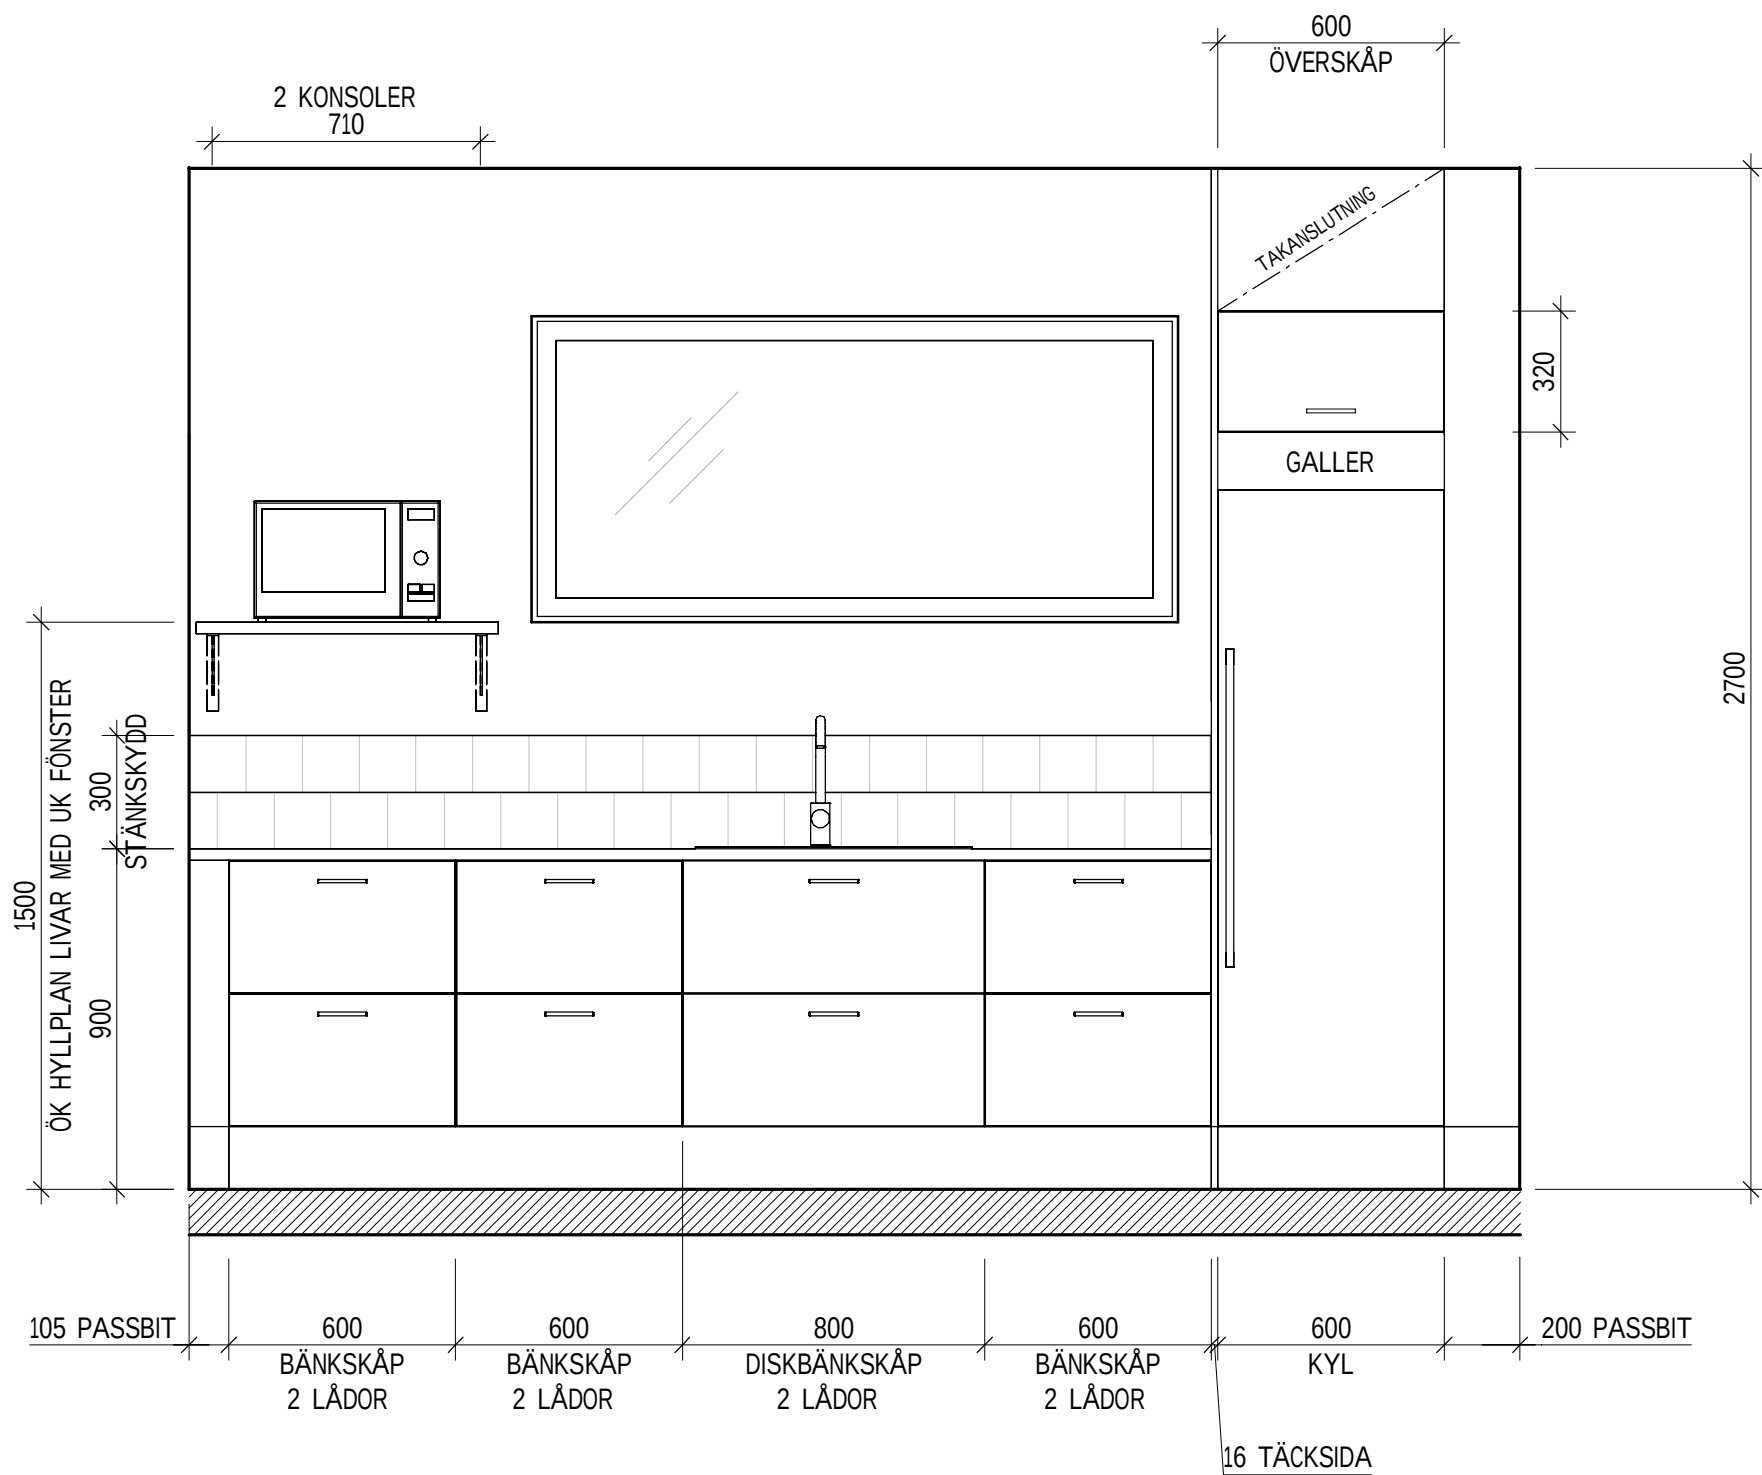

ELEVATION A PAUSRUM 1020 - PENTRY
1 : 20

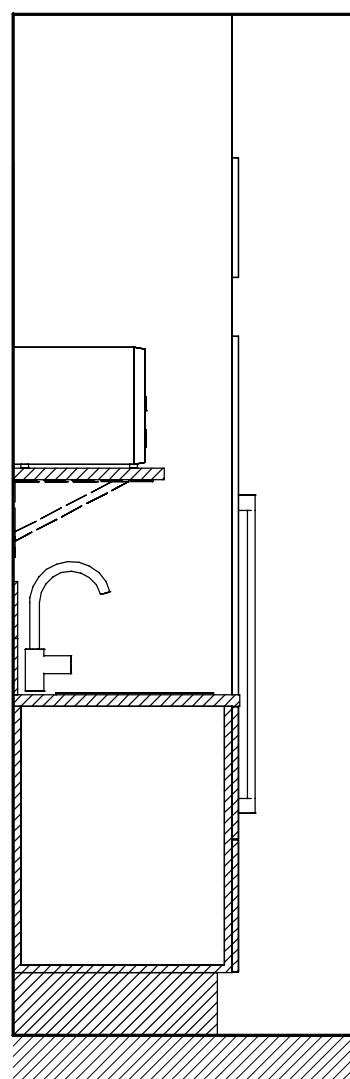

ELEVATION B PAUSRUM 1022 - PENTRY
1 : 20

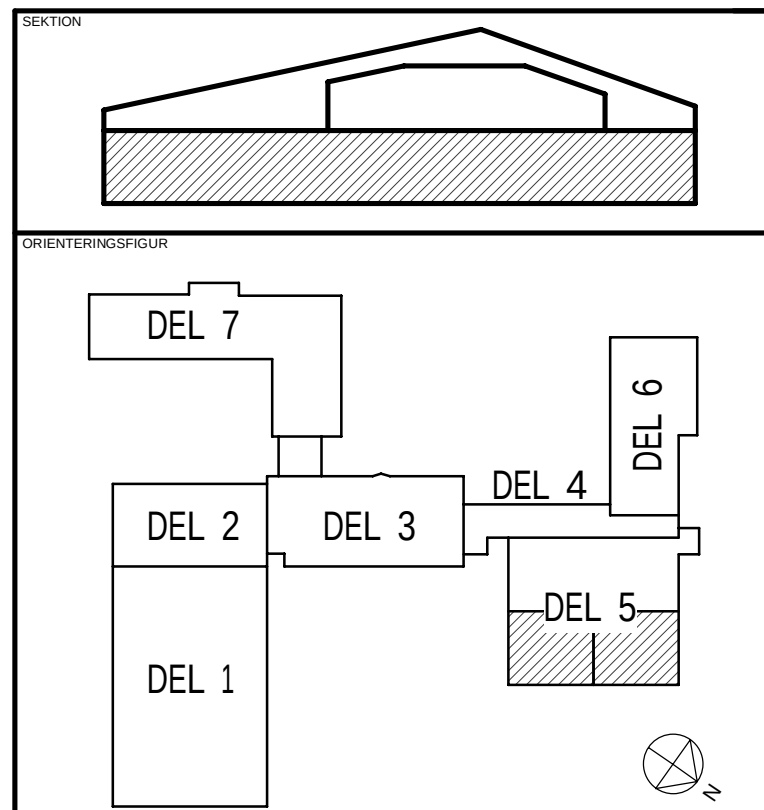

STATUS		
FÖRFRÅGNINGSUNDERLAG		
HANDLING		
BYGGHANDLING		
DATUM	2024-12-20	TEGNADE AV
	T. BERGSTRÖM	ADRESSERAD PM
BESTÄLLARE		
 ROBERTSFORS KOMMUN		
PROJEKTNAMN		
CENTRALEKÖK		
OMFÄTTE		
ROBERTSFORS KOMMUN		
PROJEKTHÄNDLIGHET	FÖRFRÅGNINGSUNDERLAG	
DIARIENUMMER	YTTRE RINGVÄGEN 4	
DISCIPLIN	FORDONET 1	
UPPRORSGRUPP	NORCONSULT SVERIGE AB	
TELEFON	SKAPAD AV	
010 141 80 00	SBS	
BYGGNADSTYP	KONTAKTPERSON	
1	TOMAS BERGSTRÖM	
VÄRNINGSPLAN	FÖRSTÄLLNING	
1	DEL 5.3, 5.4	
SYSTEM		
46 RUMSKOMPLETTERINGAR		
SPECIFIKATION		
PAUSRUM - PENTRY		
RETNINGSKATEGORI	SKALA	FORMAT
UPPSTÄLLNING	1:20	A1
DOCUMENTNUMMER	ANMÄRKNING	
A-46-6-003		

SKALA 1:20 0 1 2 METER