




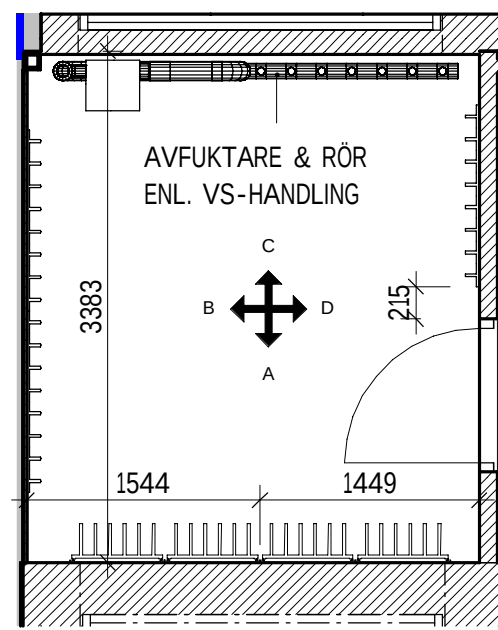


PLAN TORKRUM 1002
1 : 50

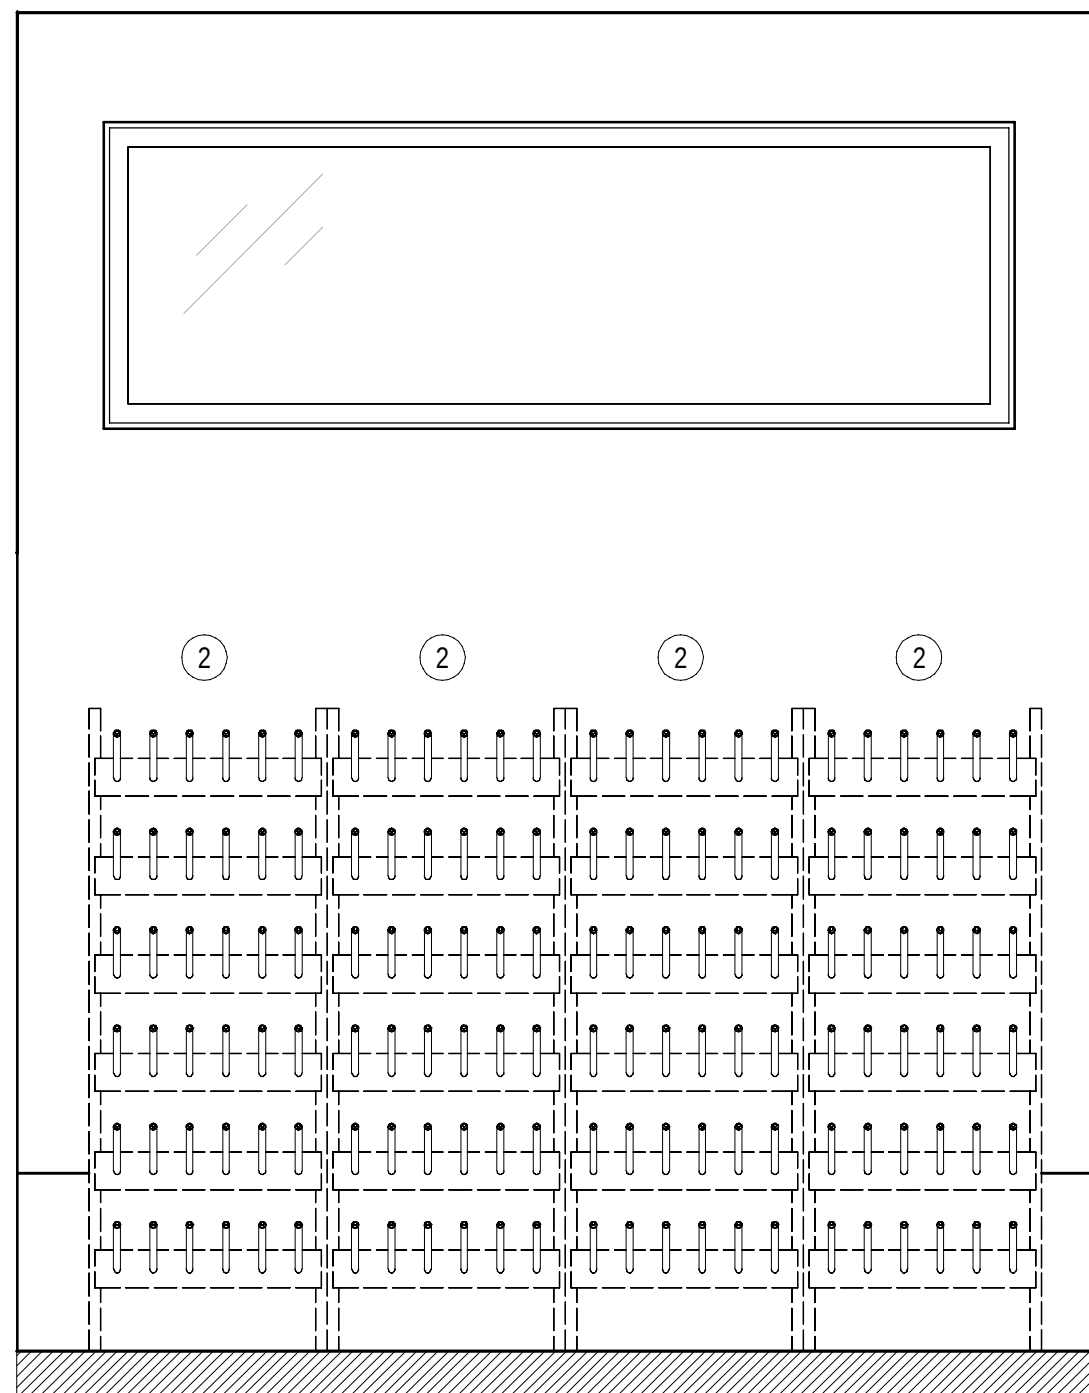


ELEVATION TOROKRUM 1002 - A
1 : 20

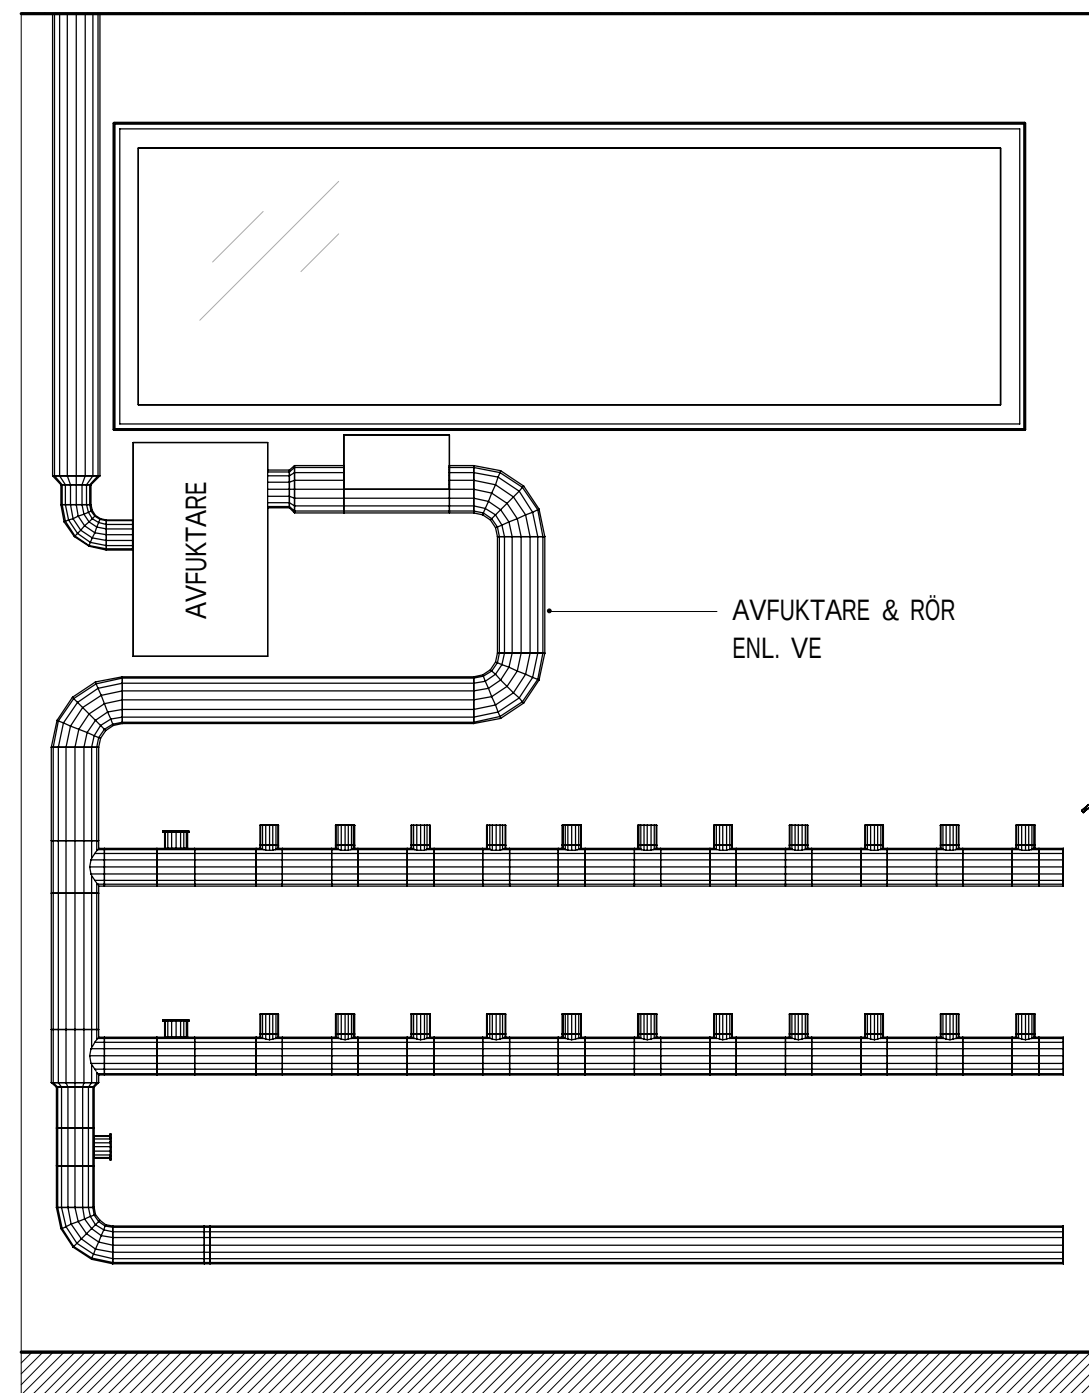

ELEVATION TORKRUM 1002 - C
1 : 20

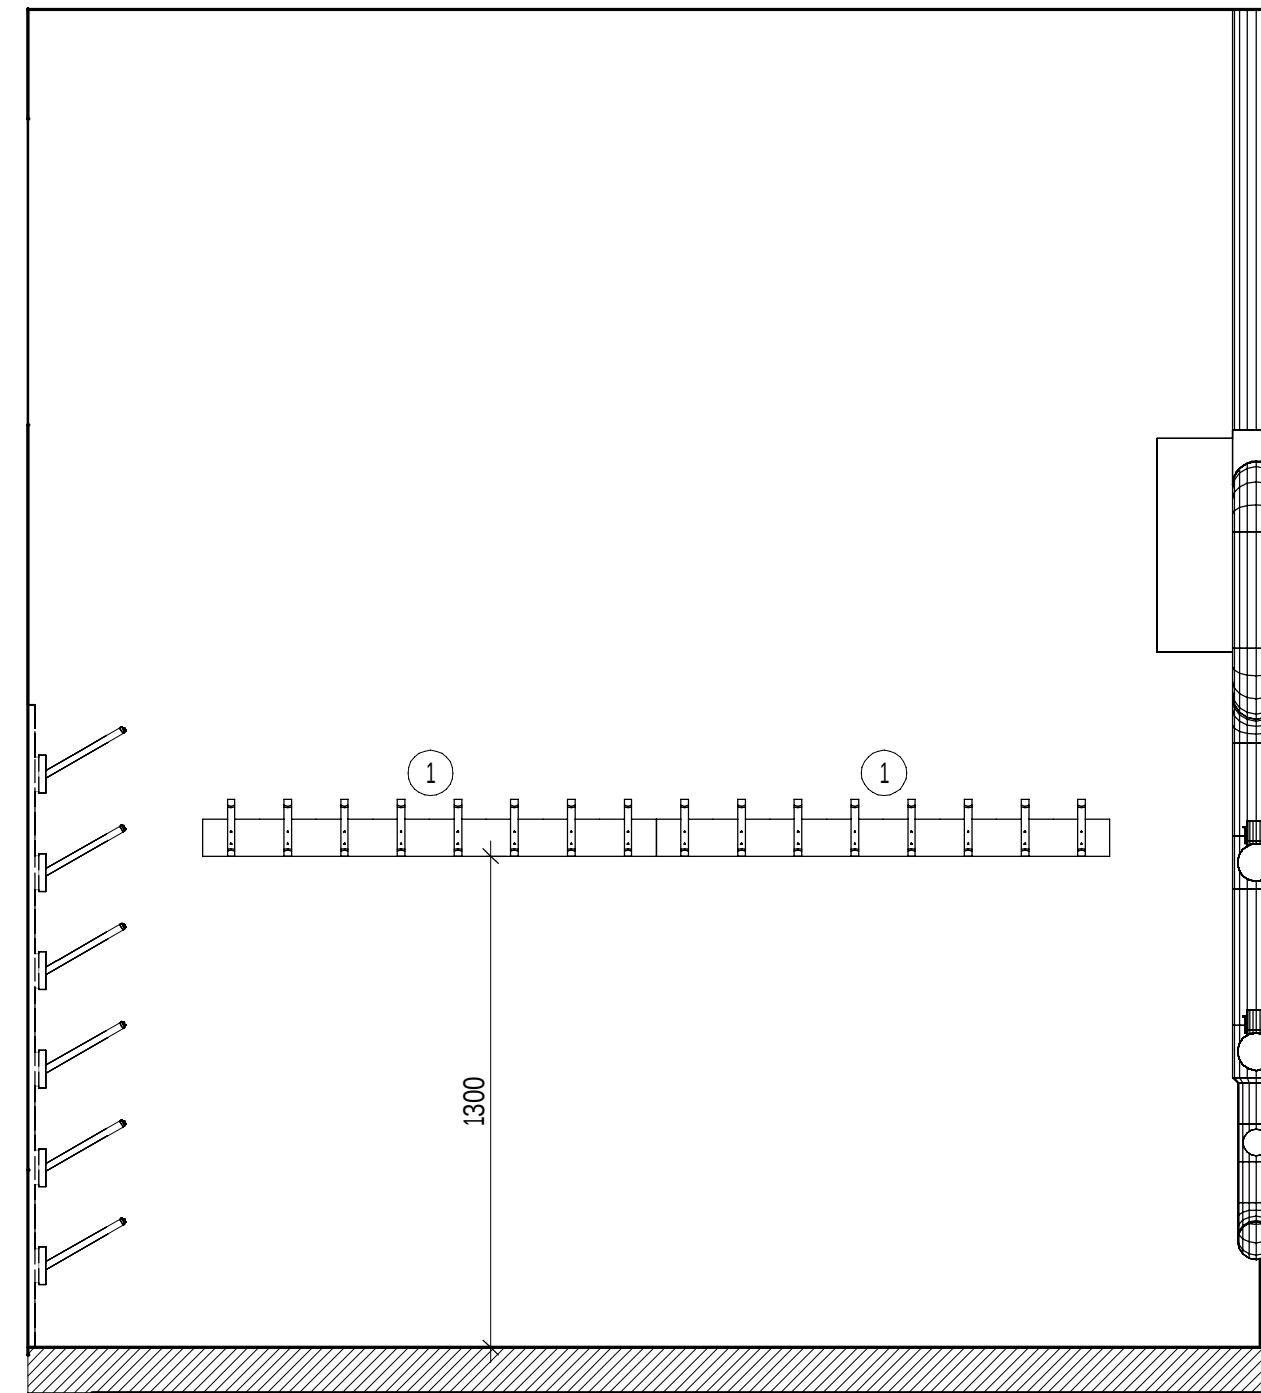

ELEVATION TORKRUM 1002 - B
1 : 20

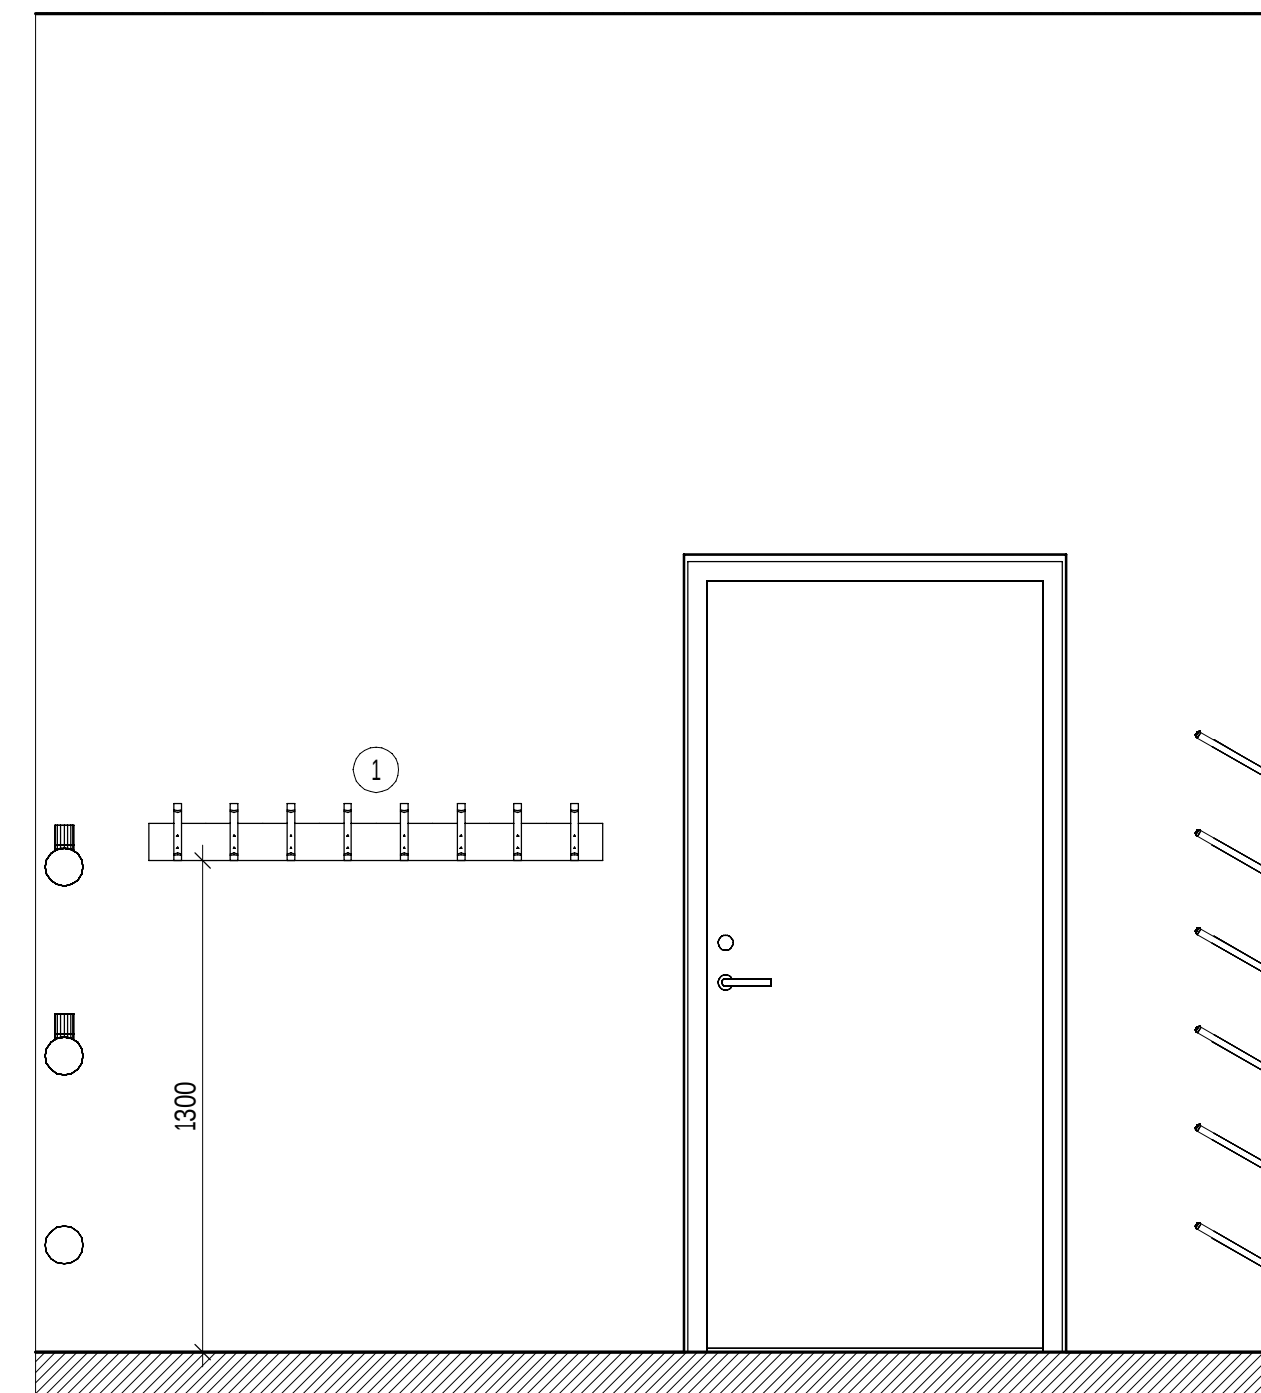

ELEVATION TORKRUM 1002-D
1 : 20

SKALA 1:20 0 1 2 METER



FÖRKLARINGAR

Samtliga mått anges i millimeter.
Mått kontrolleras på plats innan tillverkning.

1. KROKLIST typ Kroklist 2 Essem Design el. likv
Längd 1200 mm, 8 st krokär
Kulör: Ek/Svart
2. STÖVELVÄGG typ Wille Stövelvägg Lekolar el. likv
Kulör: Svart

HÄNVISNINGAR

PLAN - ÖVERSIKT, BRAND	A-40-1-001
PLAN, DEL 4.1	A-40-1-141

