# FÖRKLARINGAR

MÅTT ANGES I MILLIMETER DÄR EJ ANNAT ANGES.

= BRANDCELLSGRÄNS EI30

A = VITMÅLAD SLÄTPLÅT.
LÄNGD ANP. SÅ 50mm INFÄSTNINGNSYTA PÅ VARDERA SIDA ERHÅLLS, HÖJD LIKA KYL-/FRYSRUM

FS1 = FÖRDELARSKÅP GOLVVÄRME ENL. VS

FS2 = FÖRDELARSKÅP FÖR TAPPVATTEN ENL. VS

AK = ARMBÅGSKONTAKT

KL = KORTLÄSARE

ÖK = ÖPPNAKNAPP

HL1 = HÖRNLIST ROSTFRI ENLIGT BESKRIVNING
HL2 = HÖRNLIST PLAST ENLIGT BESKRIVNING

H1,H2=HANDLEDARE &
R1,R2=RÄCKE SE A-45-4-001

ILx = LÅSBAR INSPEKTIONSLUCKA TYP GYPROC INEO, INFÄSTNING ENL. LEVERANTÖRENS ANVISNINGAR.
STORLEK ENL. RESP. LITTRA
IL1: 150x150mm, 500mm ÖFG
IL2: 400x400mm, 500mm ÖFG

= BEFINTLIG VÄGG


= BÄRANDE INNERVÄGG ENL. K

= KYL-/FRYSRUMSVÄGG

= NY INNERVÄGG ENL. LITTERA
VX

# HÄNVISNINGAR

| | |
|---|---|
| FÖNSTER | A-42-4-001 |
| LÄTTMETALLPARTIER | A-42-4-002 |
| STÄLDÖRRAR | A-42-4-021 |
| INNERDÖRRAR AV TRÄ | A-43-4-011 |
| INVÄNDIGA GLASPARTIER | A-43-4-012 |
| INVÄNDIGA GLASFIBERDÖRRAR | A-43-4-031 |
| ELCENTRALFRONTER | A-43-4-041 |
| INNNERVÄGGSTYPER | A-43-5-001 --002 |
| INVÄNDIGA DETALJER | A-43-6-001 --003 |
| TRAPPA, HANDLEDARE, RÄCKE | A-45-4-001 |
| KONSTRUKTIONSRITNINGAR | |

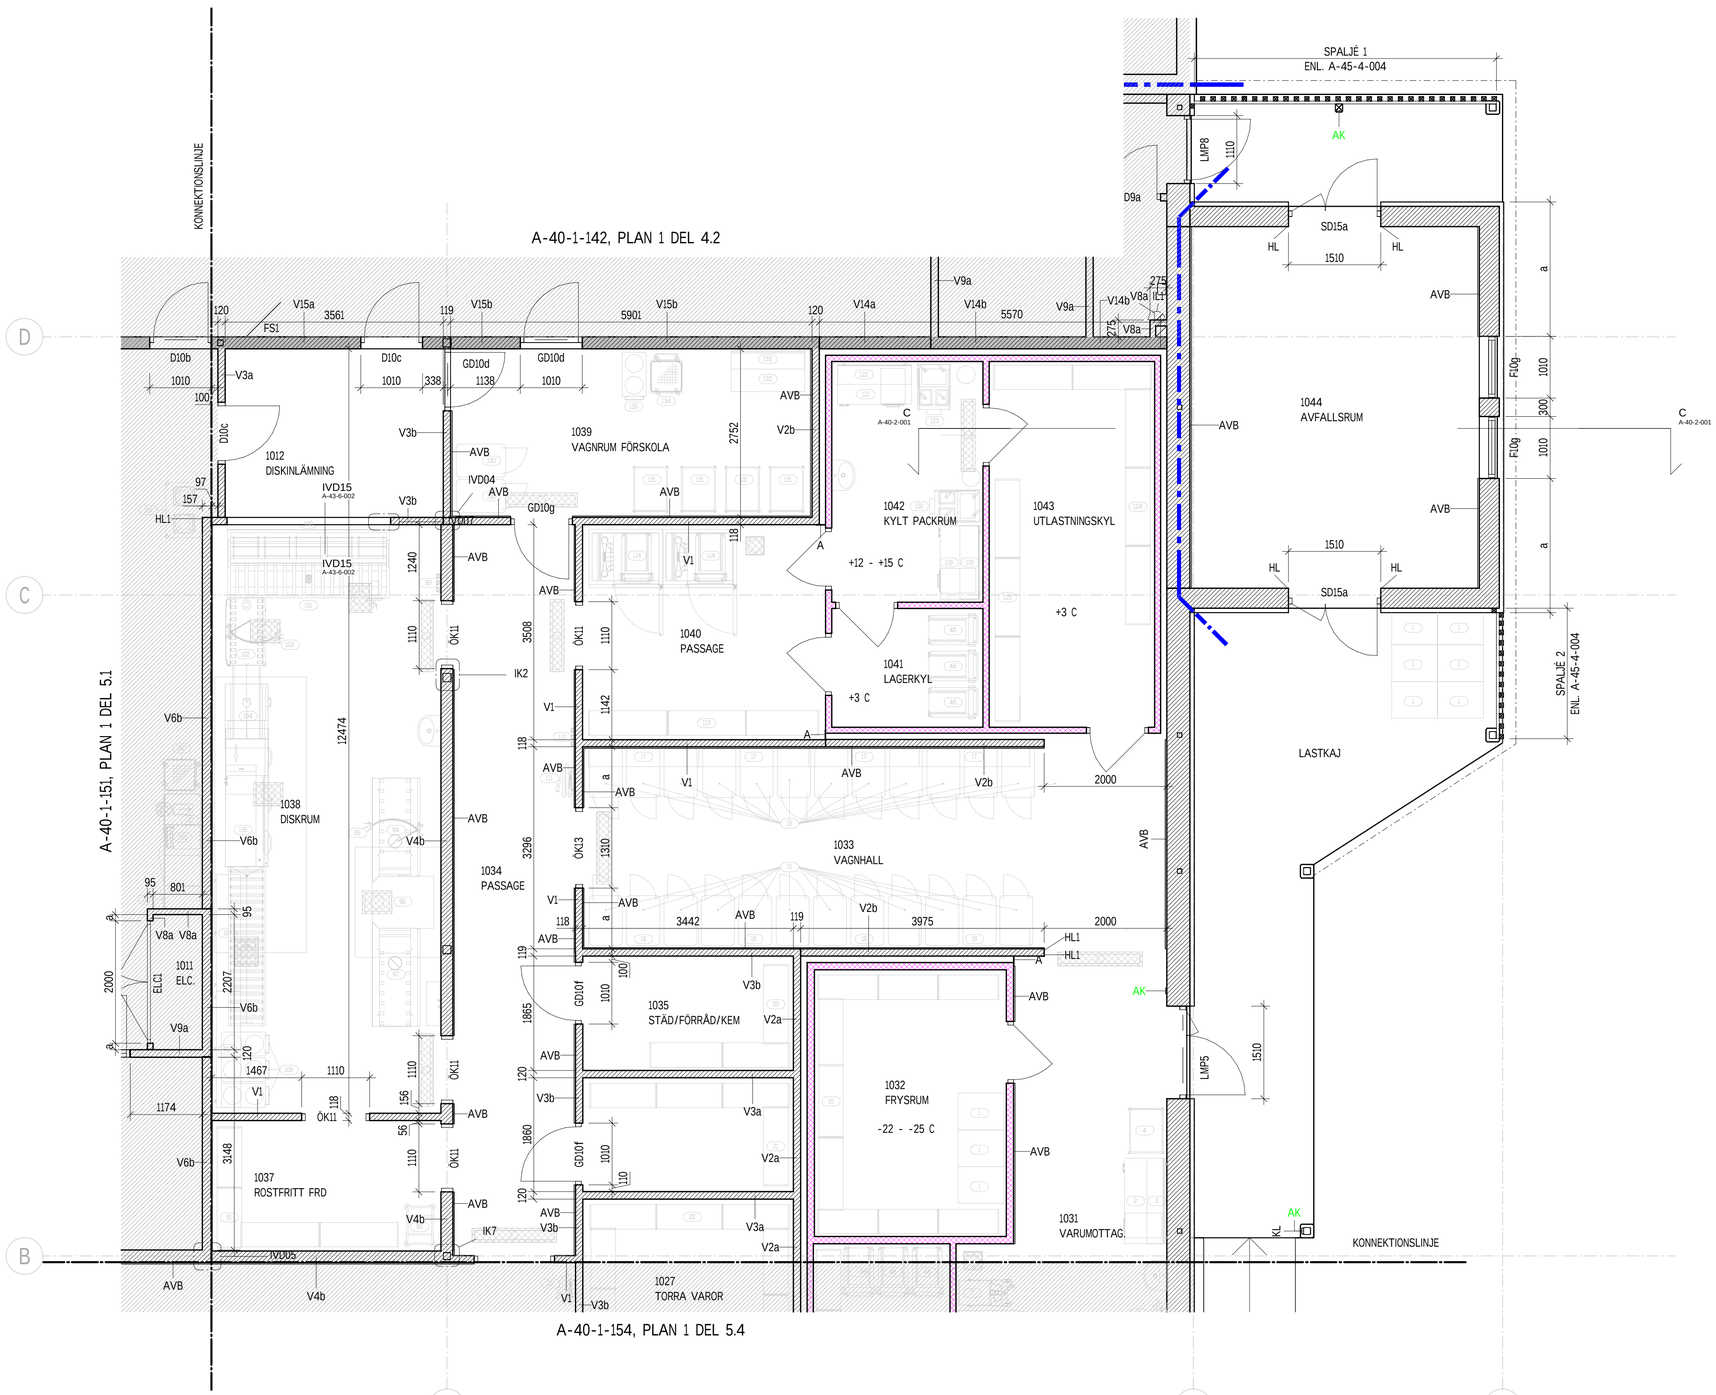



SKALA 1:50 0 1 5 METER

SEKTION



ORIENTERINGSFIGUR

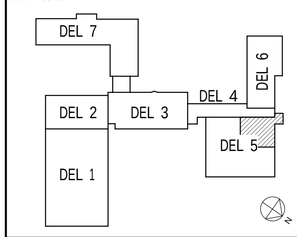


RITNING KRÄVER FÄRGUTSKRIFT FÖR KORREKT UTSEENDE

STATUS: FÖRFRÅGNINGSUNDERLAG
HANDLING: BYGGHANDLING
DATUM: 2024-12-20
GODKÄND AV: T. BERGSTRÖM
ÄNDRINGS PM:
BESTÄLLARE: ROBERTSFORS KOMMUN
PROJEKTNAMN: CENTRALKÖK
OMRÅDE: ROBERTSFORS KOMMUN
PROJEKTNUMMER: 108 83 71
ADRESS: YTTRE RINGVÄGEN 4
DIARIENUMMER:
FASTIGHET: FÖRDONET 1
DISCIPLIN: A
FÖRETAG: NORCONSULT SVERIGE AB
UPPDRAGSNUMMER: 108 83 71
SKAPAD AV: SBS
TELEFON: 010 141 80 00
KONTAKTPERSON: TOMAS BERGSTRÖM
BYGGNADSVERK:
PLUSNIVÅ RH 2000: +45,54 (FG)
VÅNINGSPLAN: 1
VÅNINGSDEL:
DELOMRÅDE: DEL 5.2
SYSTEM: 40 SAMMANSATT REDOVISNING
SPECIFIKATION: PLAN 1, DEL 5.2
RITNINGSKATEGORI: PLAN
SKALA: 1:50
FORMAT: A1
DOKUMENTNUMMER: A-40-1-152
ÄNDRING:

2024-12-20 11:22:13

FILNAMN: C:\Norconsult\Autodesk\Revit\10883371-Centralkök Robertsfors_centralli-2024_matsta.rvt