

UTVÄNDIG RAMP

ANTAL: 1 ST

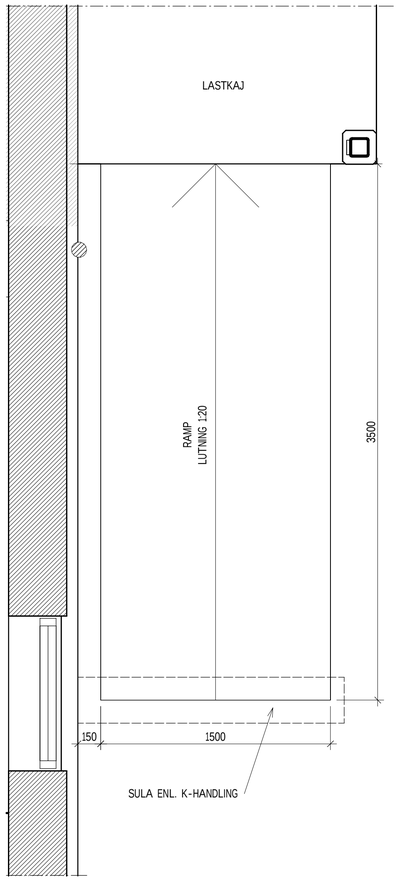

PLAN 1

1 : 20

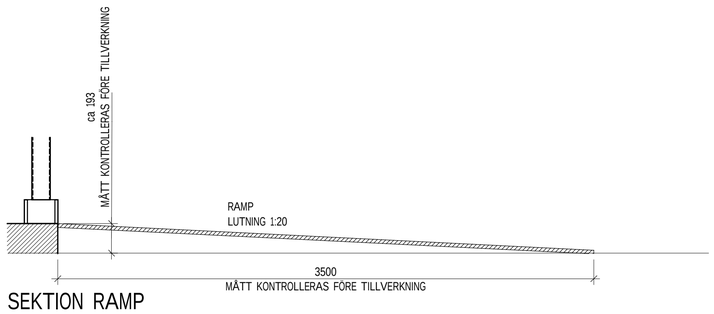

SEKTION RAMP

1 : 20

FÖRKLARINGAR

Samtliga mått anges i millimeter.
Mått kontrolleras på plats innan tillverkning.

FÖRESKRIFTER

Trappleverantören dimensionerar bärigheten och levererar erforderlig infästningsskruv.

RAMP
Welands gångbrygga flex utförs enl Weland eller likv.
Gångbana med gånggaller körbart med transport vagnar.
Avkörningsskydd på sidorna på rampen.
Allt material utom handledaren varmförzinkas enl. SS-EN ISO 1461.
Mått enl planen.


HÄNVISNINGAR

PLAN - ÖVERSIKT, BRAND A-40-1-001

SEKTION



ORIENTERINGSFIGUR

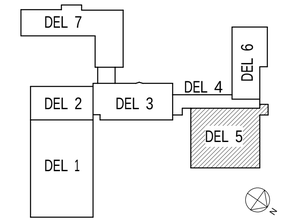

STATUS	FÖRFRÅGNINGSUNDERLAG
HANDLING	BYGGHANDLING
DATUM	2024-12-20
GODKÄND AV	T. BERGSTRÖM
ÄNDRINGS PM	
BESTÄLLARE	ROBERTSFORS KOMMUN
PROJEKTNAMN	CENTRALKÖK
OMRÅDE	ROBERTSFORS KOMMUN
PROJEKTNUMMER	
ADRESS	YTTRE RINGVÄGEN 4
DIARIENUMMER	
FASTIGHET	FORDONET 1
DISCIPLIN	A
FÖRETAG	NORCONSULT SVERIGE AB
UPPDRAGSNUMMER	108 83 71
SKAPAD AV	CHE
TELEFON	010 141 80 00
KONTAKTPERSON	TOMAS BERGSTRÖM
BYGGNADSVERK	
PLUSHÖJD (RH 2000)	
VÅNINGSPLAN	
VÅNINGSDEL	
DELOMRÅDE	
SYSTEM	45 HUSKOMPLETTERINGAR
SPECIFIKATION	RAMP
RITNINGSKATEGORI	PLAN, SEKTION
SKALA	1:20
FORMAT	A1
DOKUMENTNUMMER	A-45-4-005
ÄNDRING	

SKALA 1:20 0 1 2 METER

2024-12-20 09:07:54

FILNAMN: C:\Norconsult\Autodesk\Revit\1088371-Centralkök Robertsfors_centralli-2024_matsta.rvt