


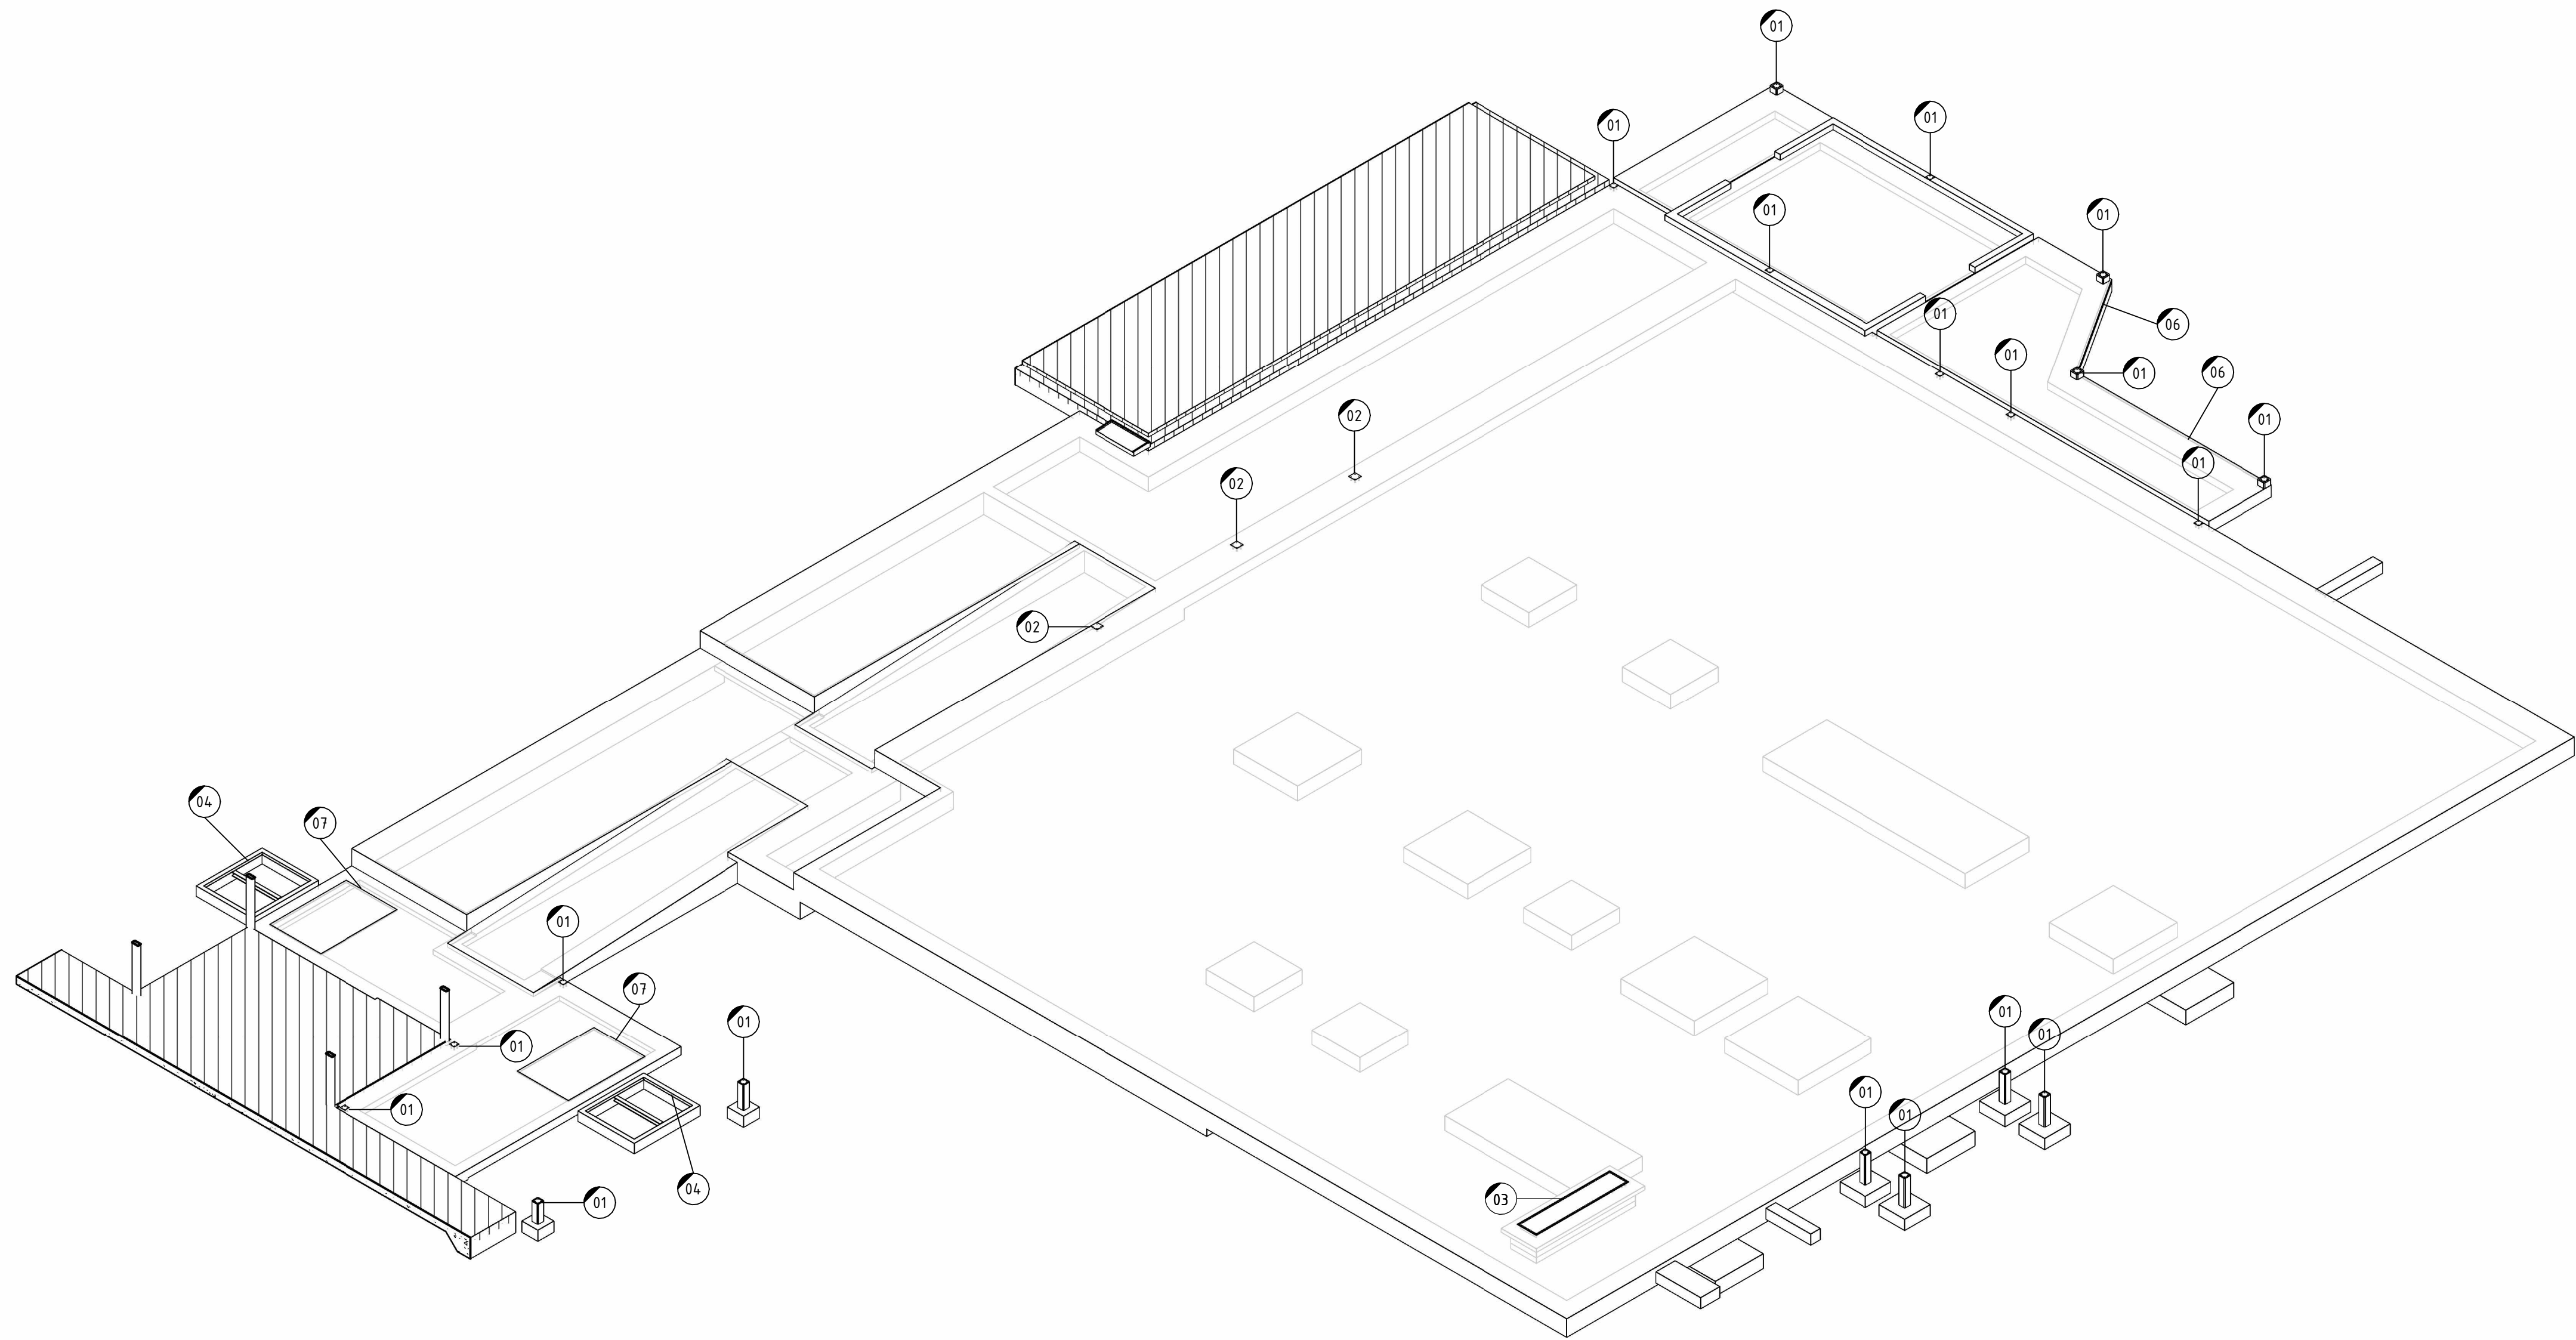

3D-VY GRUND

FÖRKLARINGAR

- BEFINTLIG BYGGNAD
- 01 INGJUTNINGSGOODS WELDA 150x150-110
- 02 INGJUTNINGSGOODS WELDA 200x200-72
- 03 INGJUTNINGSGOODS KANTSTÅL NR 2 DURKPLÅT S235JR
- 04 INGJUTNINGSRAM L35x35x5 VFZ TYP WELAND ELLER LIKVÄRDIGT. UTREDNING ENLIGT GRUNDPLAN.
- 05 INGJUTNINGSGOODS L60x60x6 S235JR VFZ MED PÅSVETSÅDE (a5) KRAMLOR Ø8s200. GJUTS IN ENLIGT 15-K-15-6-002 , ANTAL ENLIGT ANTAL DÖRRAR I YTTERVÄGG (12 ST), L = DÖRRBREDD
OBS! INGÅR EJ I STÅLLEVERANS
- 06 INGJUTNINGSGOODS L50x50x5 MED KRAMLOR Ø12x200/ 250 GALVANISERAD KANTSKONING TYP BE GROUP. LÅNGDER ENLIGT GRUNDPLAN.
OBS! INGÅR EJ I STÅLLEVERANS
- 07 INGJUTNINGSRAM FÖR SKRAPMATTOR ENLIGT BESKRIVNING.

PILMÅTT TAS FRÅN NÄRMAST LIGGANDE STÖMLINJE (MINST 1 METER)

FÖRESKRIFTER

K-01-0-001 -- 003 ALLMÄNNA FÖRESKRIFTER

HÄNVISNINGAR

- K-15-2-001 -- 002 GRUNDSEKTIONER
- K-15-6-001 -- 003 GRUNDETALJER
- K-24-1-100 GRUNDBULTAR OCH PELARPLACERING

SEKTION

ORIENTERINGSSKISS

STATUS

FÖRFRÅGNINGSUNDERLAG

HANDLING

BYGGHANDLING

DATUM

2024-12-20

ANSÖKAN AV

BJÖRN LIDSTRÖM

ÄNDRINGS PM

BESTÄLLARE

ROBERTSFORS
KOMMUN

PROJEKTNAMN

CENTRALEKÖ

KORRIGERING

ROBERTSFORS KOMMUN

PROJEKTNUMMER

108 83 71

FASTIGHET

YTTRE RINGVÄGEN 4

DIREKTOR

FORDONET 1

DISCIPLIN

K

FÖRETAG

NORCONSULT SVERIGE AB

UPPDRAGSNUMMER

108 83 71

SKAPAD AV

AWG/ATN

TELEFON

010-141 80 00

KONTAKTPERSON

BJÖRN LIDSTRÖM

BYGGKOSTNAD

+45,540 (FG)

VÄNINGSPLAN

VÄNINGSDEL

DELNING

DEL 4, 5

SYSTEM

15 GRUNDKONSTRUKTIONER

SPECIFIKATION

3D-VY GRUND

ÄNDRINGSKATEGORI

3D

SKALA

1:50

FORMAT

A1

DOKUMENTNUMMER

K-15-0-100

ÄNDRING