

FÖRKLARINGAR

300 CELLPLAST
100 CELLPLAST

ÖVRIG CELLPLAST ENLIGT GRUNDSEKTIONER OCH
GRUNDETALJER


FÖRESKRIFTER

K-01-0-001 -- 003 ALLMÄNNA FÖRESKRIFTER

HÄNVISNINGAR

K-15-2-001 -- 002 GRUNDSEKTIONER
K-15-6-001 -- 003 GRUNDETALJER

K-24-1-100 GRUNDBULTAR OCH PELARPLACERING

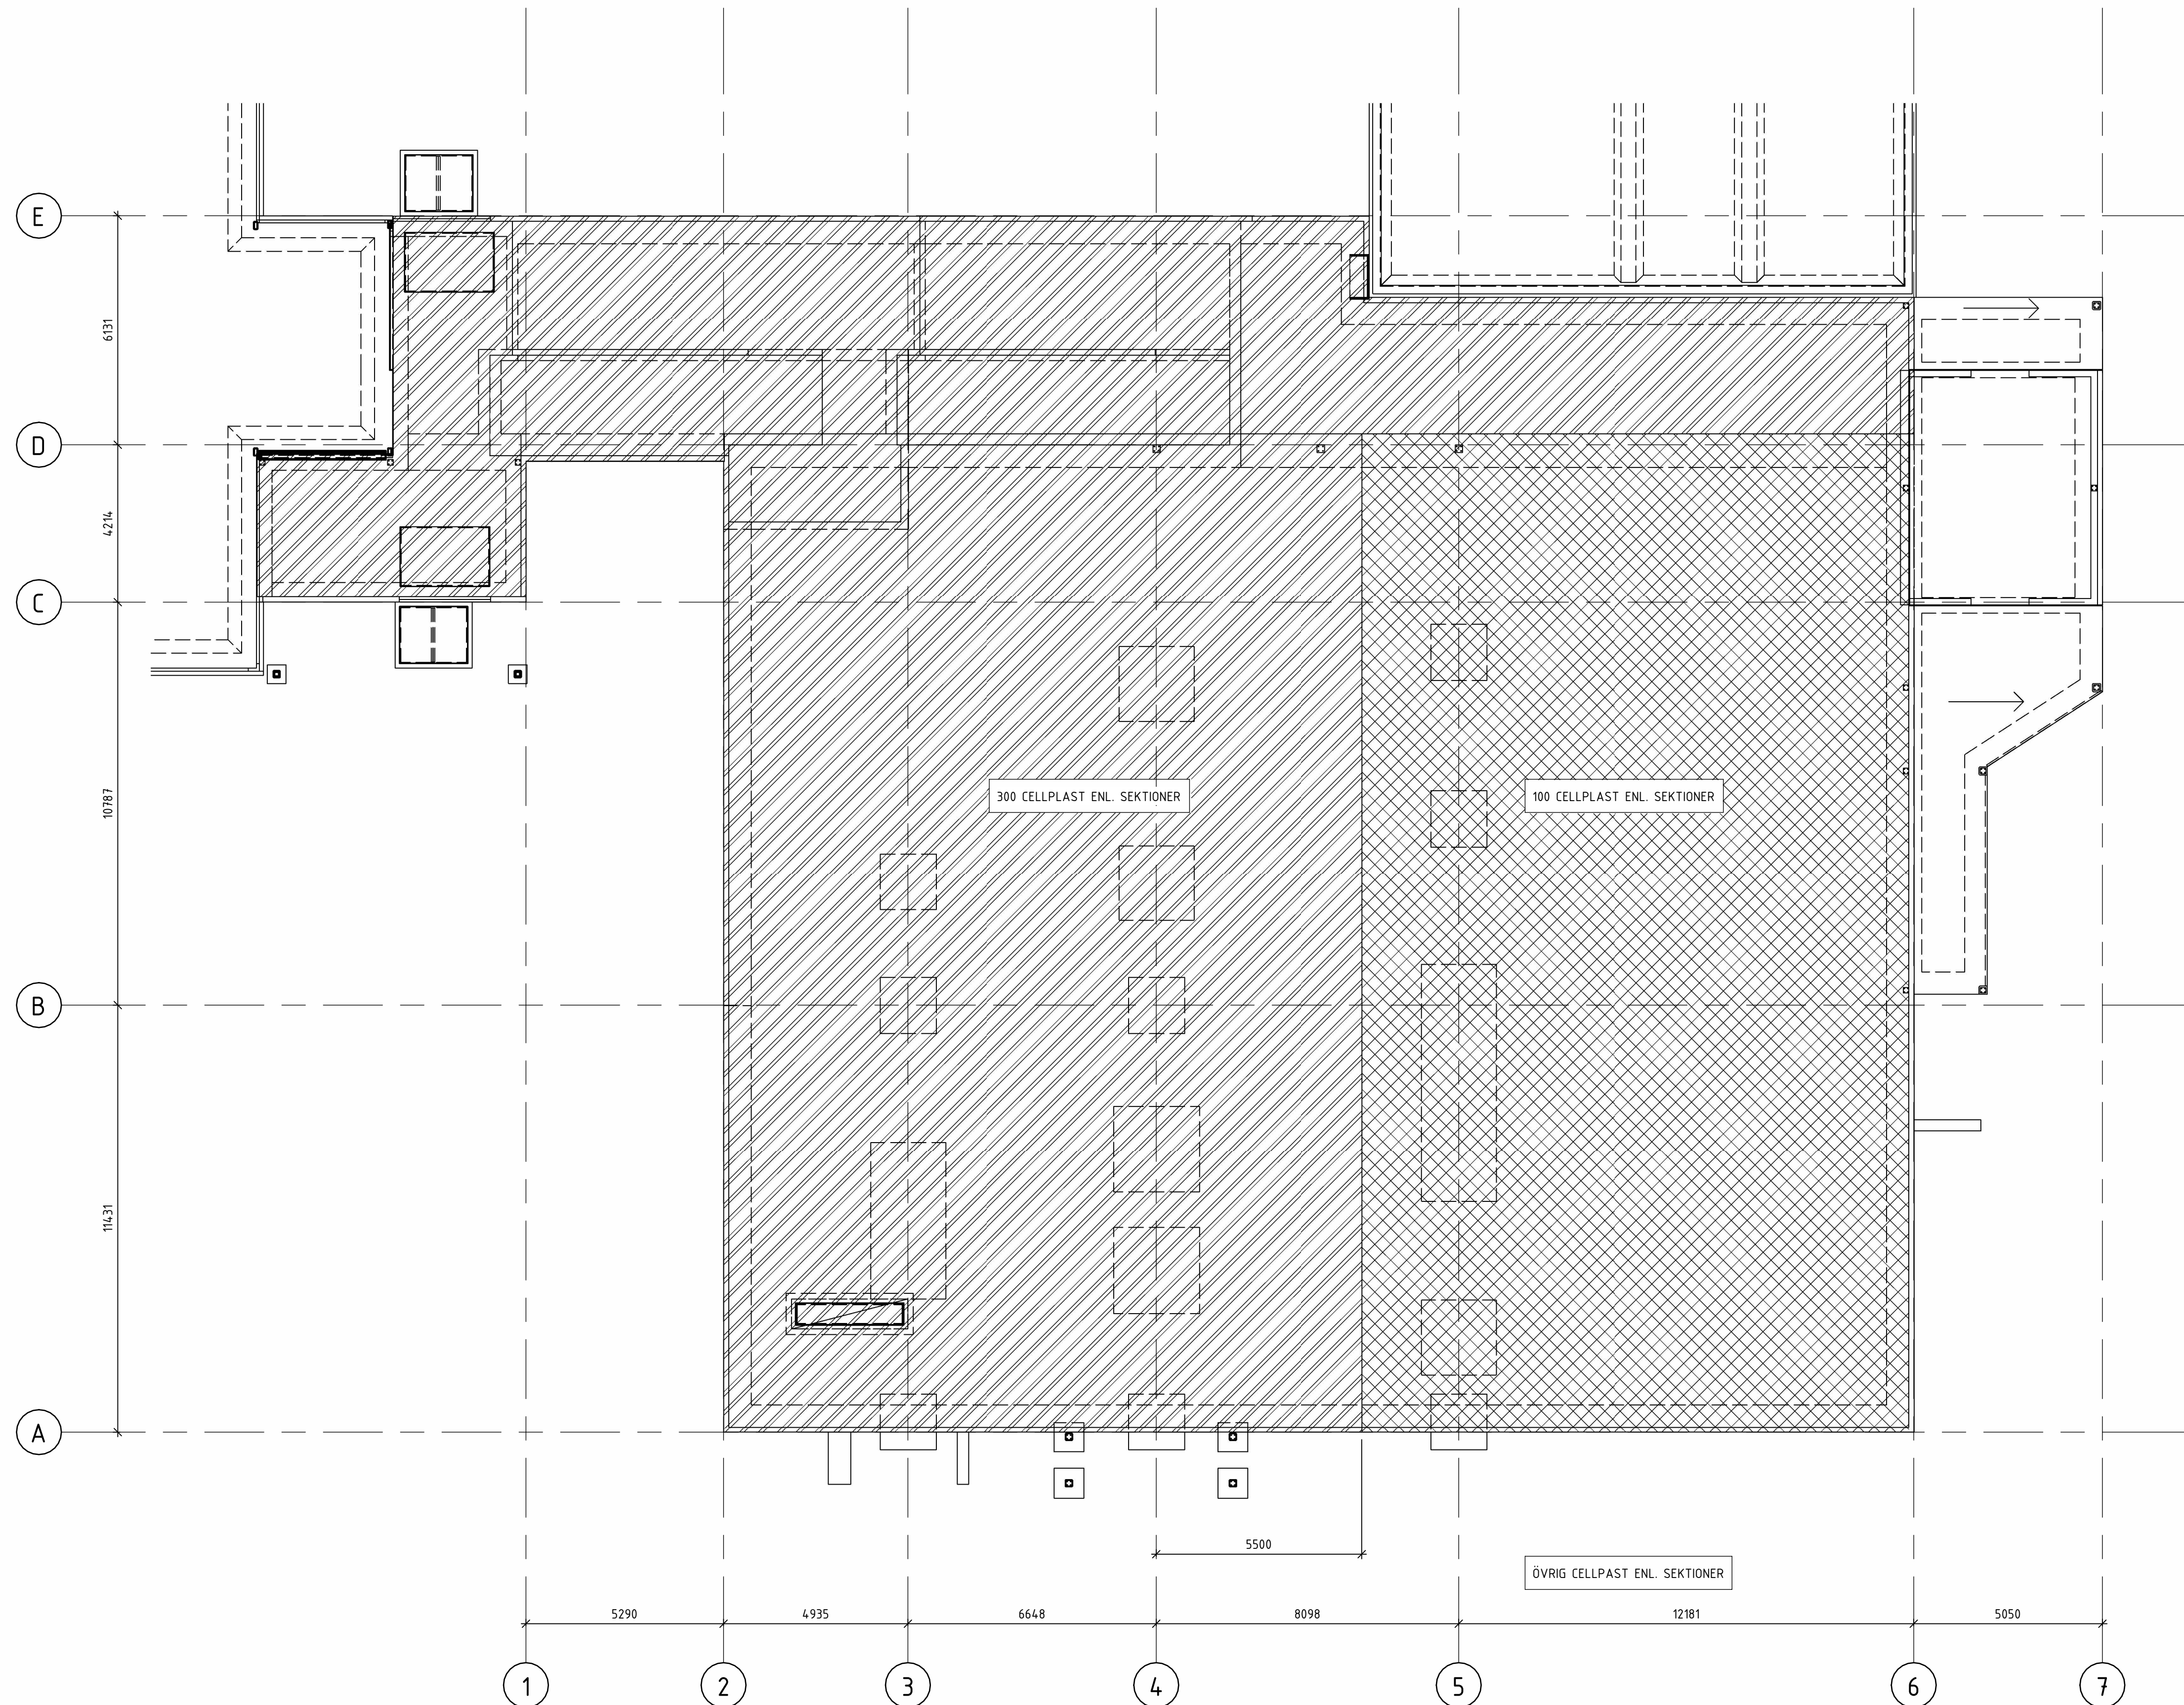

GRUNDPLAN ISOLERINGSUTBREDNING

1 : 100

SKALA 1:100 0 1 10 METER

SEKTION

ORIENTERINGSGUR

STATUS

FÖRFRÅGNINGSUNDERLAG

HANDLING

BYGGHANDLING

DATUM

2024-12-20

ANSÖKAN

BJÖRN LIDSTRÖM

ÄNDRING

PM

BESTÄLLARE

ROBERTSFORS
KOMMUN

PROJEKTNAMN

CENTRALEKÖK

KOMMUNE

ROBERTSFORS KOMMUN

PROJEKTNUMMER

108 83 71

FASTIGHET

YTTRE RINGVÄGEN 4

DIREKTOR

FORDONET 1

DISCIPLIN

FÖRETAG

NORCONSULT SVERIGE AB

UPPDRAGSNUMMER

108 83 71

SKAPAD AV

AWG/ATN

TELEFON

010-141 80 00

KONTAKTPERSON

BJÖRN LIDSTRÖM

BYGGKOSTNAD

+45,540 (FG)

YANINGSPLAN

YANINGSDEL

DELOMRÅDE

DEL 4, 5

SYSTEM

15 GRUNDKONSTRUKTIONER

SPECIFIKATION

GRUNDPLAN ISOLERINGSUTBREDNING

BYGGKOSTNAD

SKALA

1:100

FORMAT

A1

OKUMENTNUMMER

K-15-1-101

ÄNDRING