


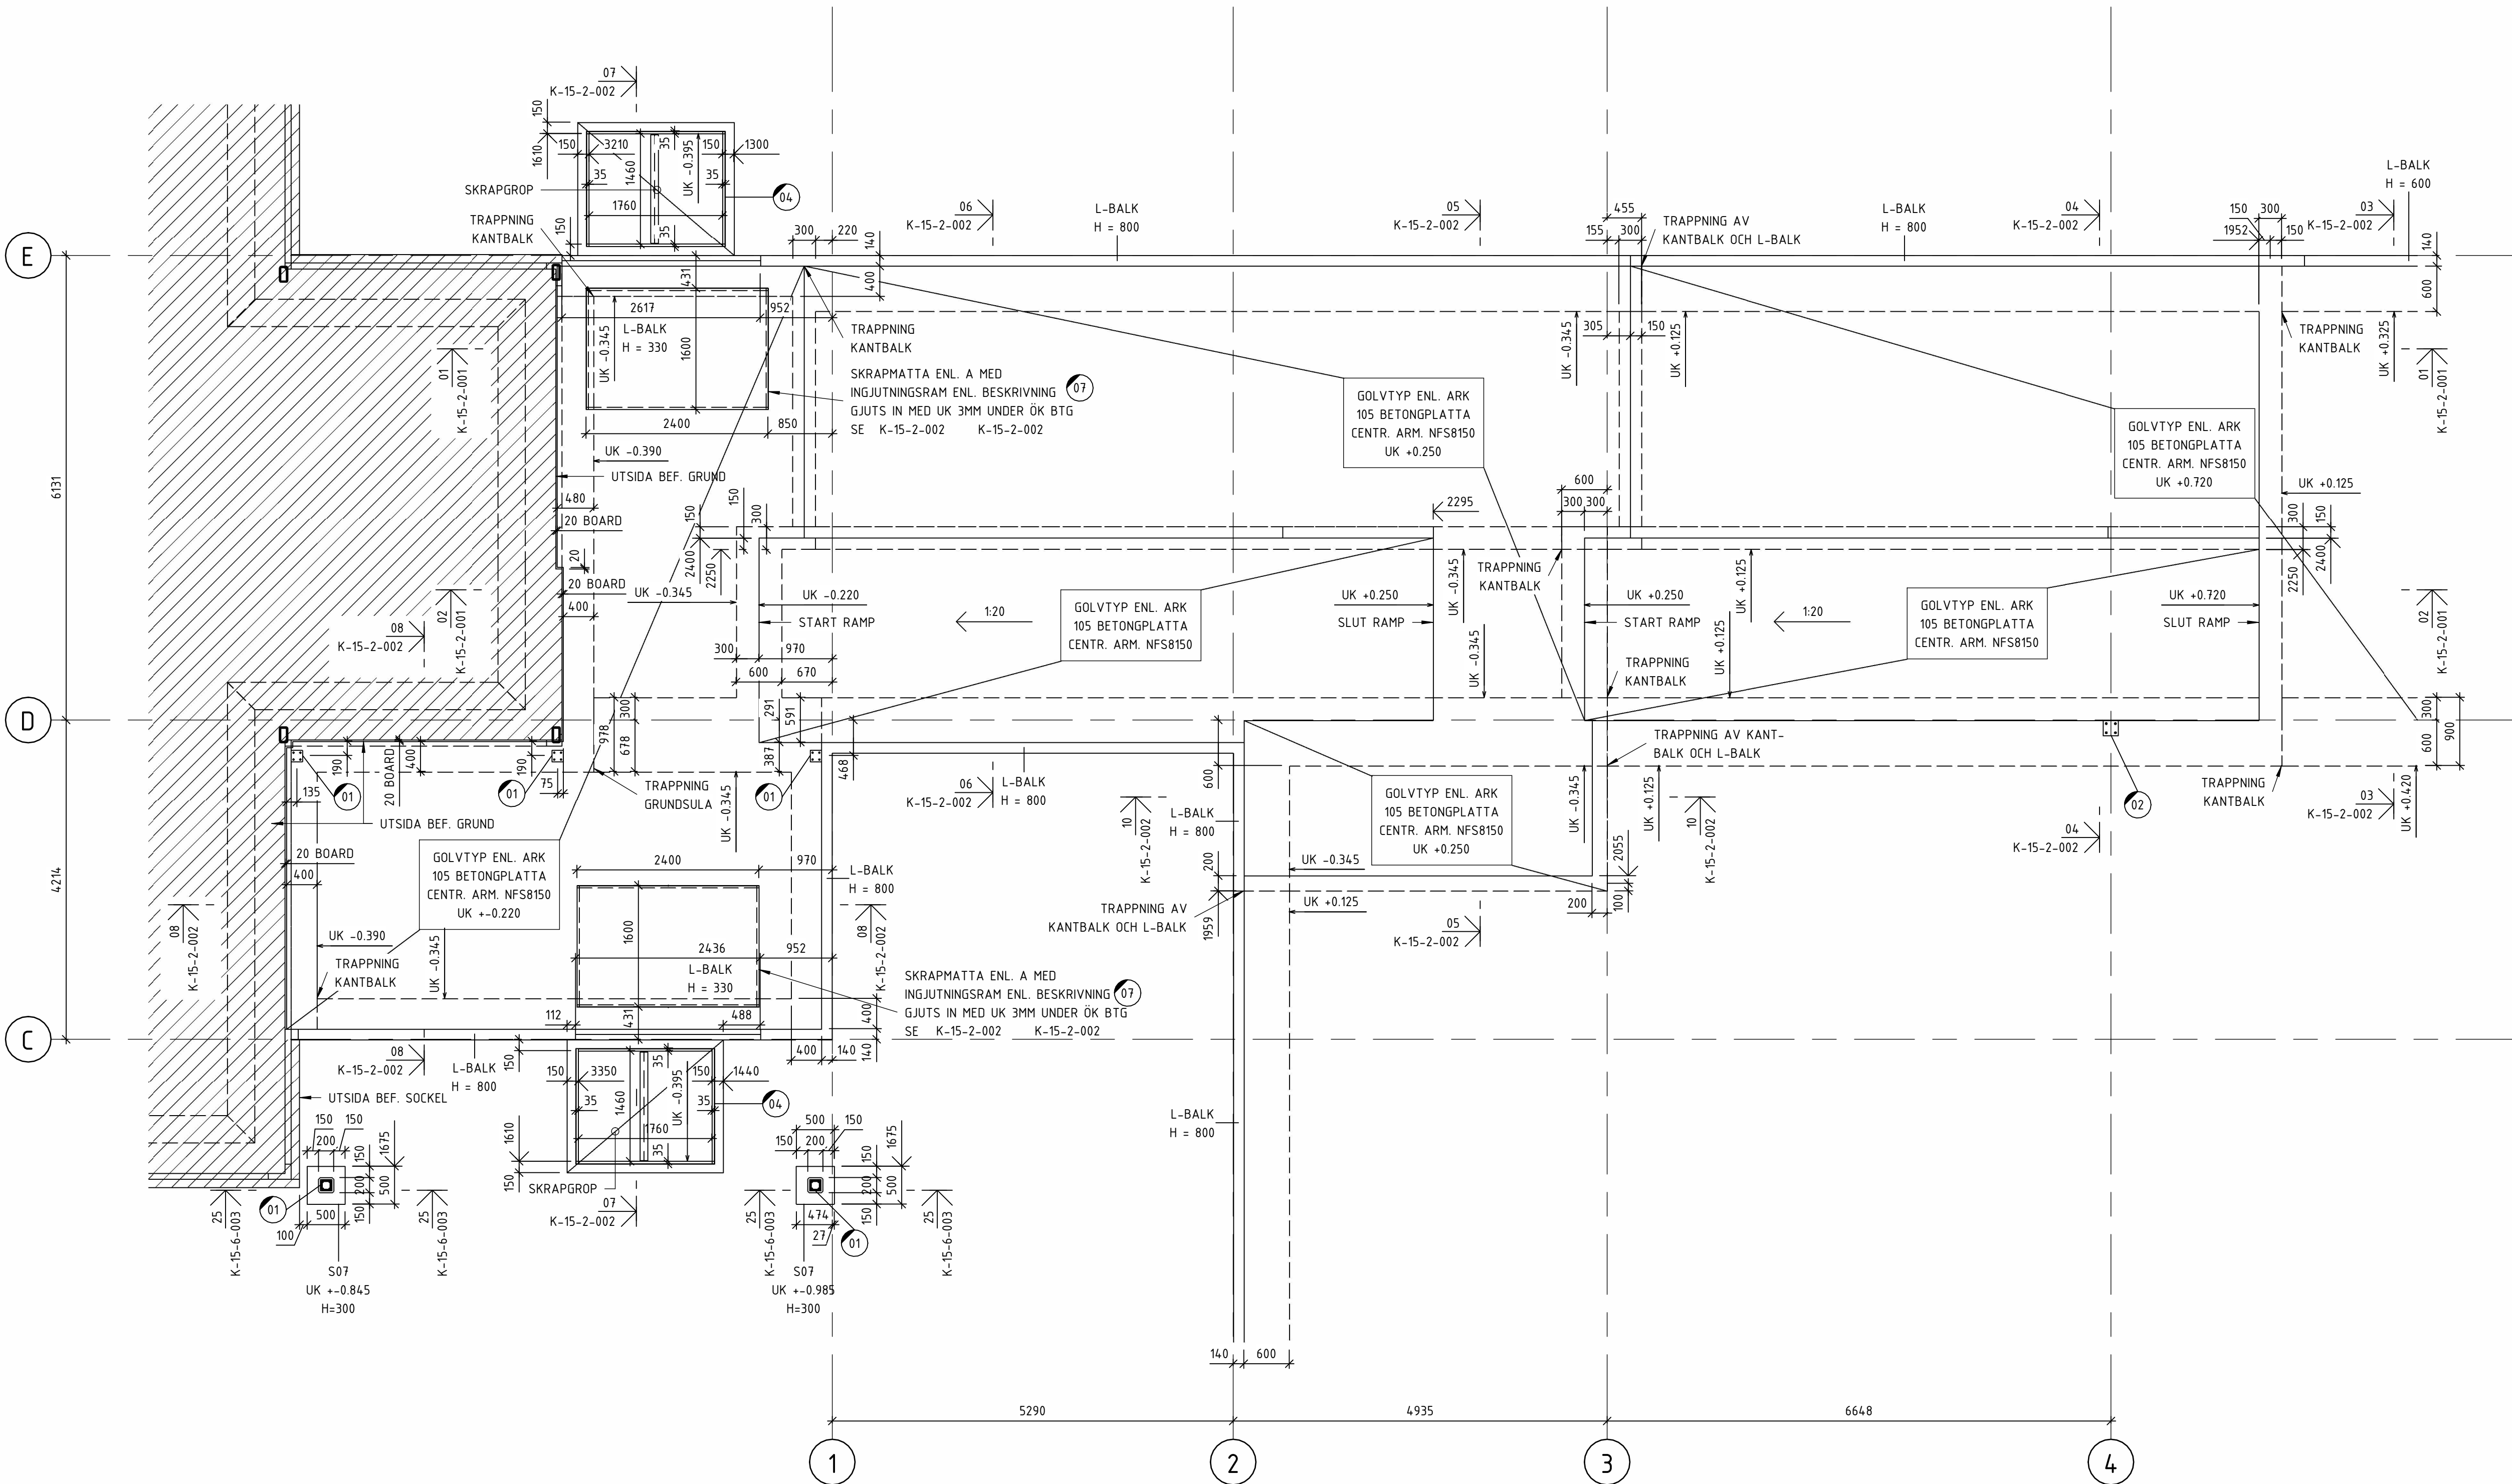

GRUNDPLAN DELPLAN LÅGDEL

1 : 50

FÖRKLARINGAR

- 01 INGJUTNINGSGOODS WELDA 150x150-110
- 02 INGJUTNINGSGOODS WELDA 200x200-72
- 03 INGJUTNINGSGOODS KANTSTÅL NR 2 DURKPLÅT S235JR
- 04 INGJUTNINGSRAM L35x35x5 VFZ TYP WELAND ELLER LIKVÄRDIGT. UTBREDNING ENLIGT GRUNDPLAN.
- 05 INGJUTNINGSGOODS L60x60x6 S235JR VFZ MED PÅSVETSDE (a5) KRAMLOR Ø8x200. GJUTS IN ENLIGT 15-K-15-6-002, ANTAL ENLIGT ANTAL DÖRRAR I YTTERVÄGG (12 ST), L = DÖRRBREDD OBS! INGÅR EJ I STÅLLEVERANS
- 06 INGJUTNINGSGOODS L50x50x5 MED KRAMLOR Ø12x200/ 250 GALVANISERAD KANTSKONING TYP BE GROUP. LÅNGDER ENLIGT GRUNDPLAN. OBS! INGÅR EJ I STÅLLEVERANS
- 07 INGJUTNINGSRAM FÖR SKRAPMATTA ENLIGT BESKRIVNING.

PILMÄTT TAS FRÅN NÄRMAST LIGGANDE STÖMLINJE (MINST 1 METER)

FÖRESKRIFTER

K-01-0-001 -- 003 ALLMÄNNA FÖRESKRIFTER

HÄNVISNINGAR

K-15-2-001 -- 002 GRUNDEKSEKTIONER

K-15-6-001 -- 003 GRUNDETALJER

K-24-1-100 GRUNDBULTAR OCH PELARPLACERING

SEKTION

ORIENTERINGSFIGUR

STATUS

FÖRFRÅGNINGSUNDERLAG

HANDLING

DATUM

2024-12-20

UTARBETAD AV

BJÖRN LIDSTRÖM

ÄNDRINGS FM

BESTÄLLARE

ROBERTSFORS KOMMUN

PROJEKTNAMN

CENTRALEKÖK

KONTRAKT

ROBERTSFORS KOMMUN

PROJEKTNUMMER

108 83 71

FASTIGHET

YTTRE RINGVÄGEN 4

DIREKTOR

K

FÖRETAG

NORCONSULT SVERIGE AB

UPPDRAGSNUMMER

108 83 71

KONTAKTPERSON

AWG/ATN

TELEFON

010-141 80 00

KONTAKTPERSON

BJÖRN LIDSTRÖM

BYGGKOSTNAD

+45,540 (FG)

VÄNINGSPLAN

VÄNINGSDEL

DEL 4, 5

SYSTEM

15 GRUNDKONSTRUKTIONER

PROJEKTION

GRUNDPLAN DELPLAN

BYGGKOSTNAD

PLAN

SKALA

1:50

FORMAT

A1

BYGGKOSTNAD

K-15-1-110

SKALA 1:50 0 1 5 METER