




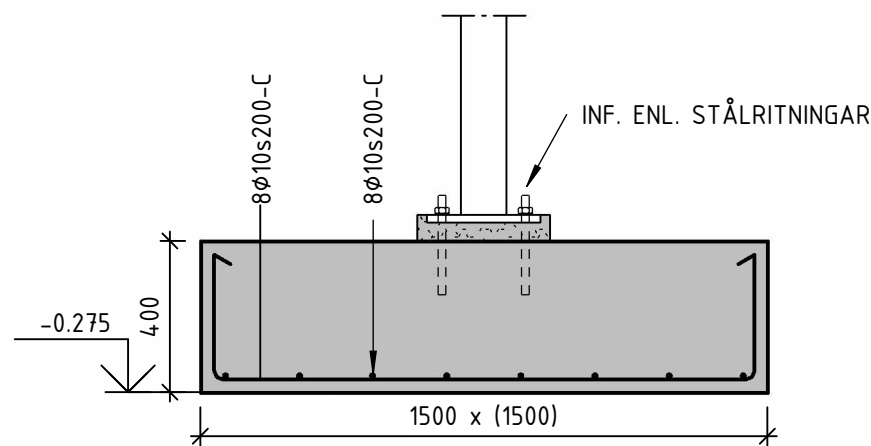


S01
1 : 20
SULA 01

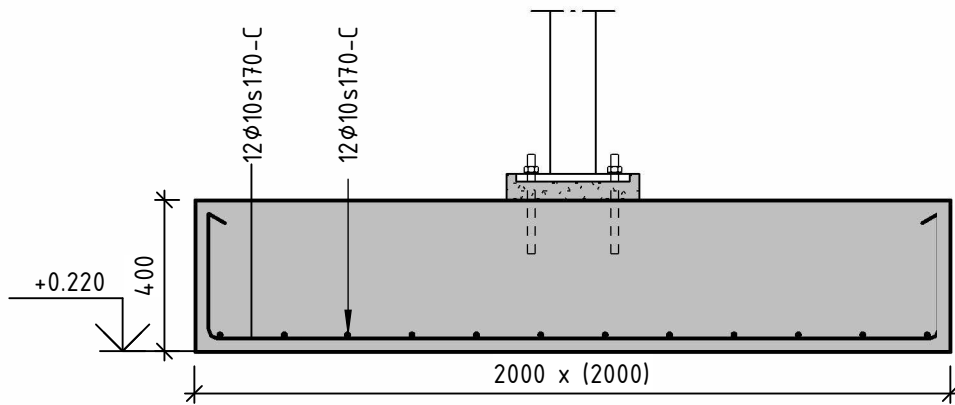


S02
1 : 20
SULA 02

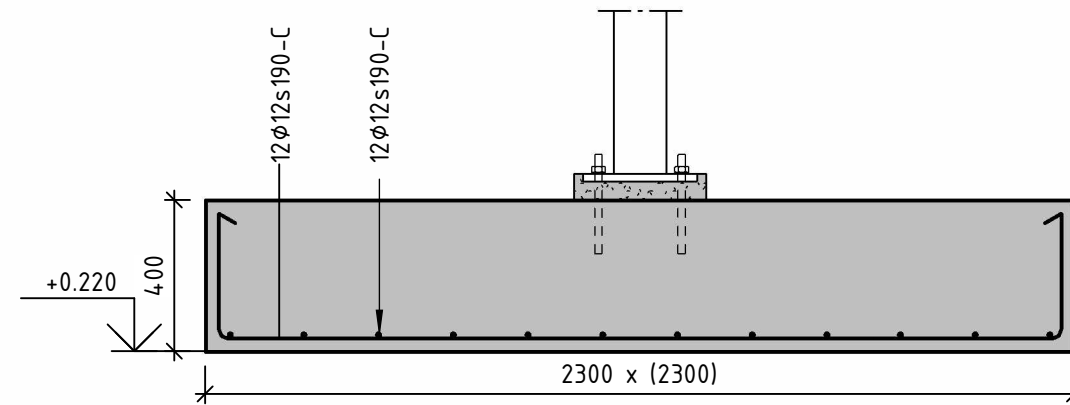


S03
1 : 20
SULA 03

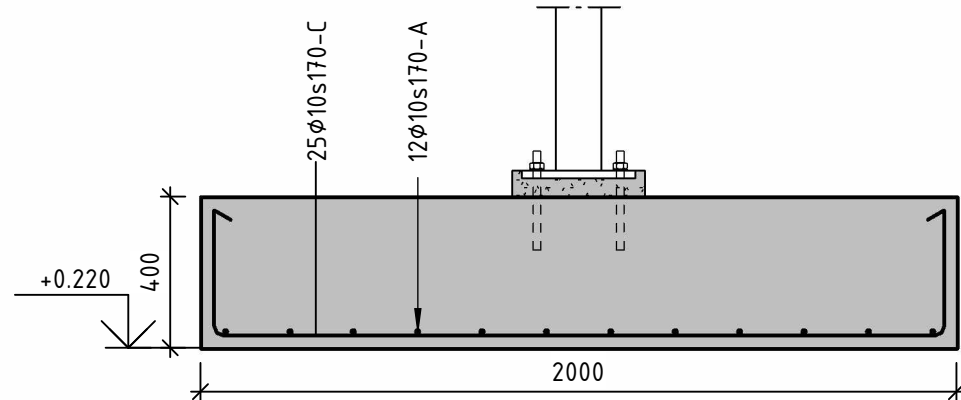


S04a
1 : 20
SULA 04, TVÄRSEKTION

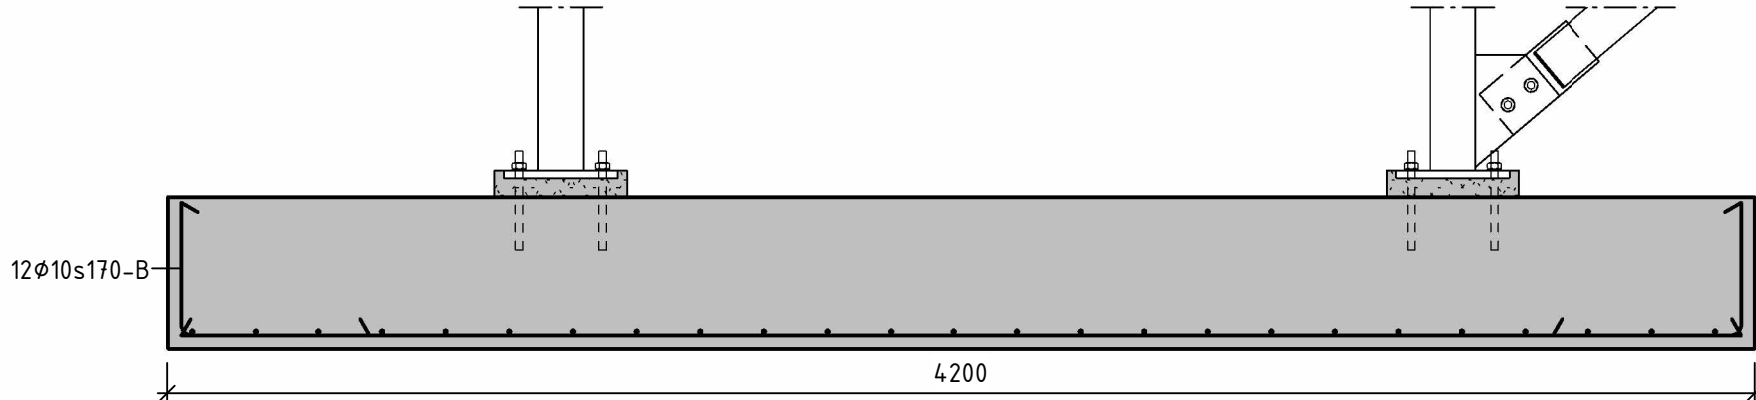


S04b
1 : 20
SULA 04, LÄNGSSEKTION

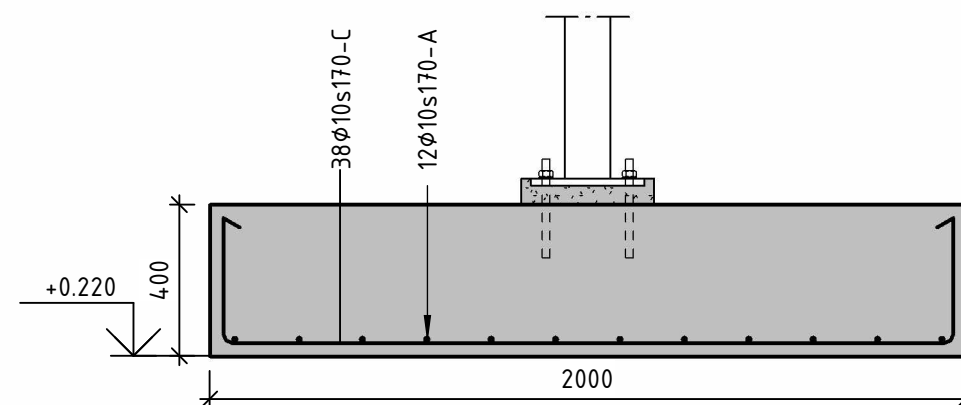


S05a
1 : 20
SULA 05, TVÄRSEKTION

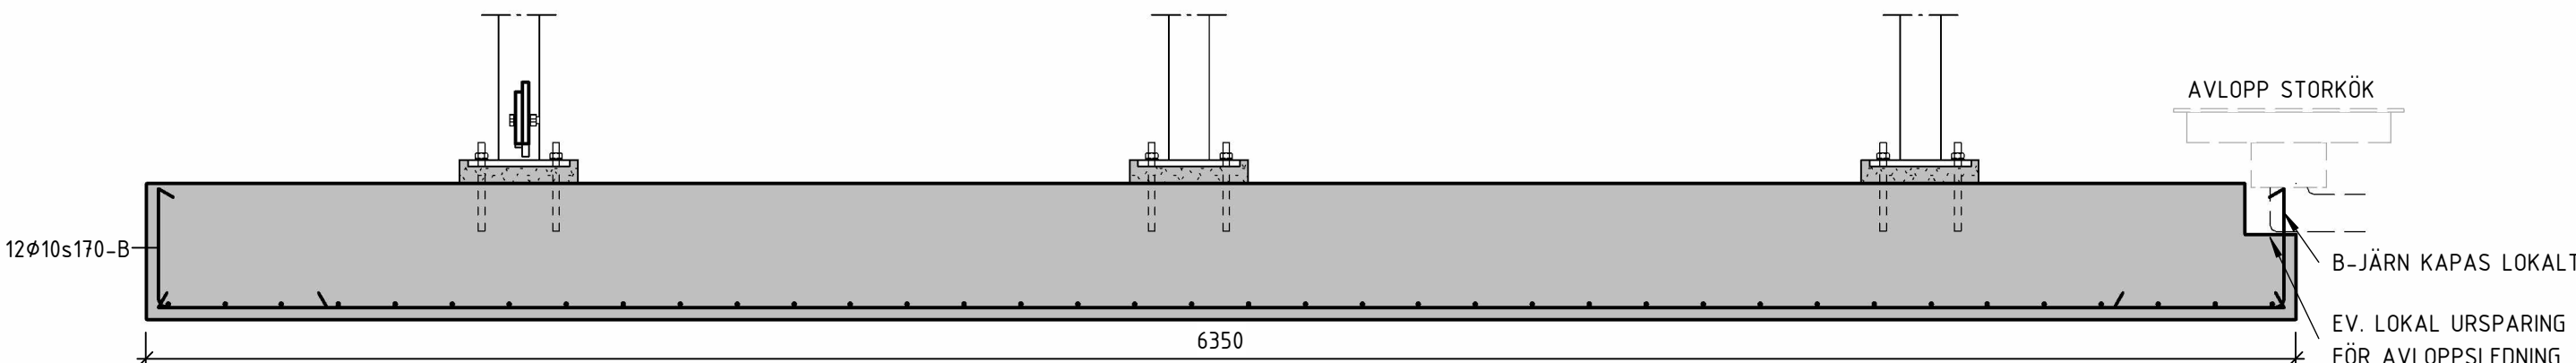


S05b
1 : 20
SULA 05, LÄNGSSEKTION

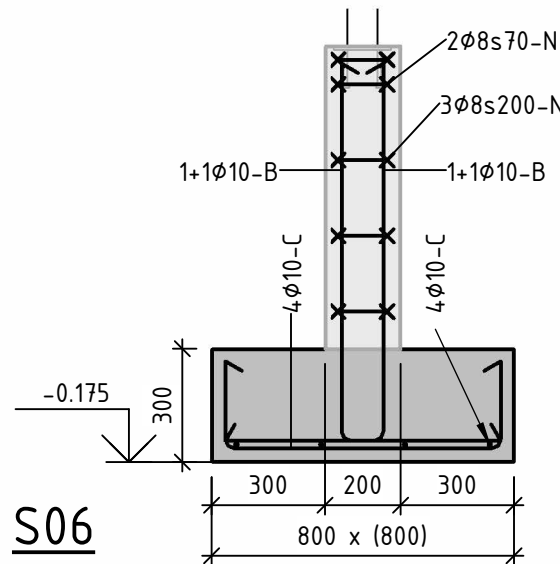


S06
1 : 20
SULA 06, VID TRAPPA TILL FLÄKTRUM

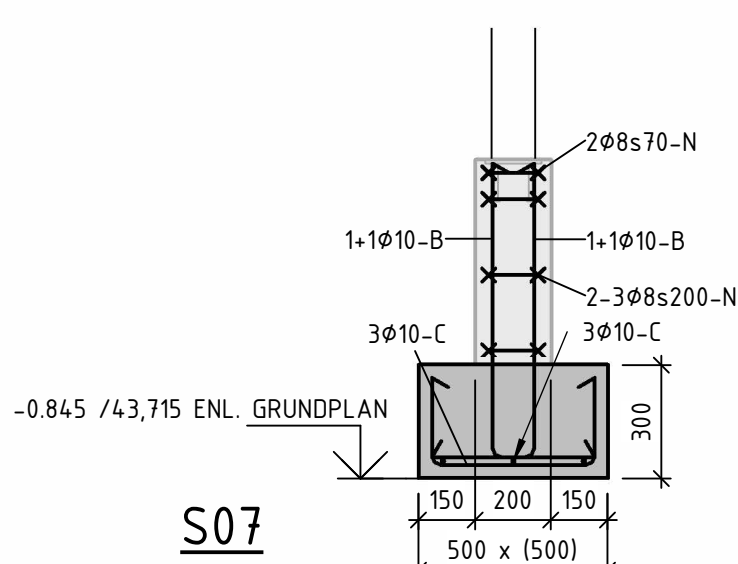

S07
1 : 20
SULA 07, VID SKÄRMTAK ENTRÉ

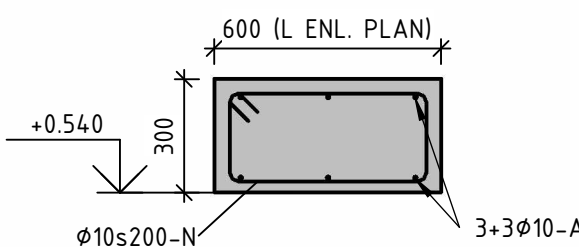

S08
1 : 20
SULA UNDER TRAPPA

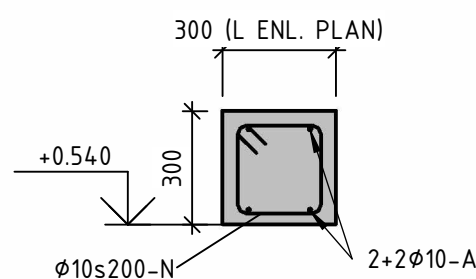

S09
1 : 20
SULA UNDER VILPLAN TRAPPA

SKALA 1:20 0 1 2 METER

FÖRKLARINGAR

- BEFINTLIG BYGGNAD
- INGJUTNINGSGOODS WELDA 150x150-110
- INGJUTNINGSGOODS WELDA 200x200-72
- INGJUTNINGSGOODS KANTSTÅL NR 2 DURKPLÅT S235JR
- INGJUTNINGSRAM L35x35x5 VFZ TYP WELAND ELLER LIKVÄRDIGT. UTBREDNING ENLIGT GRUNDPLAN
- INGJUTNINGSGOODS L60x60x6 S235JR VFZ MED PÅSVETSDE (a5) KRAMLOR Ø8s200. GJUTS IN ENLIGT 15-K-15-6-002, ANTAL ENLIGT ANTAL DÖRRAR I YTTERVÄGG (12 ST), L = DÖRRBREDD OBS! INGÅR EJ I STÅLLEVERANS
- INGJUTNINGSGOODS L50x50x5 MED KRAMLOR Ø12x200/250 GALVANISERAD KANTSKONING TYP BE GROUP. LÄNGDER ENLIGT GRUNDPLAN. OBS! INGÅR EJ I STÅLLEVERANS
- INGJUTNINGSRAM FÖR SKRAPMATTAN ENLIGT BESKRIVNING.

PILMÅTT TAS FRÅN NÄRMAST LIGGANDE STÖMLINJE (MINST 1 METER)

FÖRESKRIFTER

K-01-0-001 -- 003 ALLMÄNNA FÖRESKRIFTER

HÄNVISNINGAR

-

SEKTION		
ORIENTERINGSGRUPP		
DEL 7 DEL 2 DEL 3 DEL 1 DEL 4 DEL 5 DEL 6		
STATUS		
FÖRFRÅGNINGSUNDERLAG		
HANDLING		
BYGGHANDLING		
DATUM	LOSRÄTT	ÄNDRINGS PM
2024-12-20	BJÖRN LIDSTRÖM	
BESTÄLLARE		
ROBERTSFORS KOMMUN		
PROJEKTNAMN		
CENTRALEKÖ		
OBJEKT		
ROBERTSFORS KOMMUN		
PROJEKTNUMMER	FASTIGHET	
108 83 71	YTTERE RINGVÄGEN 4	
DOKUMENT	FÖRETAG	
	NORCONSULT SVERIGE AB	
DOKUMENT	UPPRORSGRUPP	
K	108 83 71	
UPPRORSGRUPP	AWG/ATN	
TELEFON	KONTAKTPERSON	
010-141 80 00	BJÖRN LIDSTRÖM	
BYGGGRUPP	PRIS	
	+45,540 (FG)	
VÄRDEPLAN	DELNING	
	DEL 4, 5	
SYSTEM		
15 GRUNDKONSTRUKTIONER		
SPECIFIKATION		
GRUNDSULOR		
DOKUMENT	SKALA	FORMAT
DETALJ	1:20	A1
DOKUMENT	ÄNDRING	
K-15-6-001		