




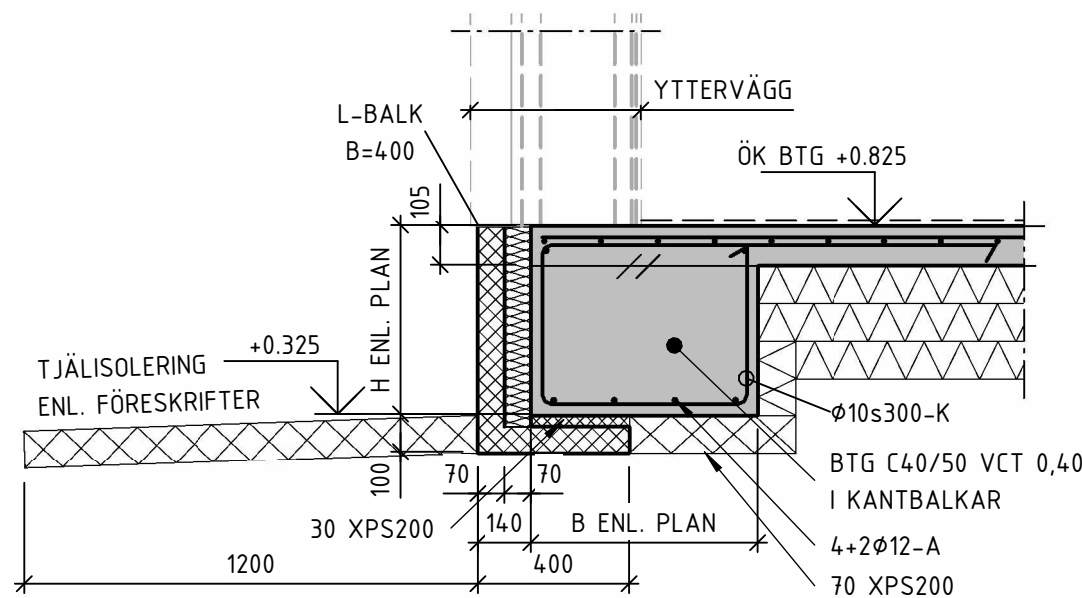


01
1 : 20
KANTBALK UNDER YTTERVÄGG

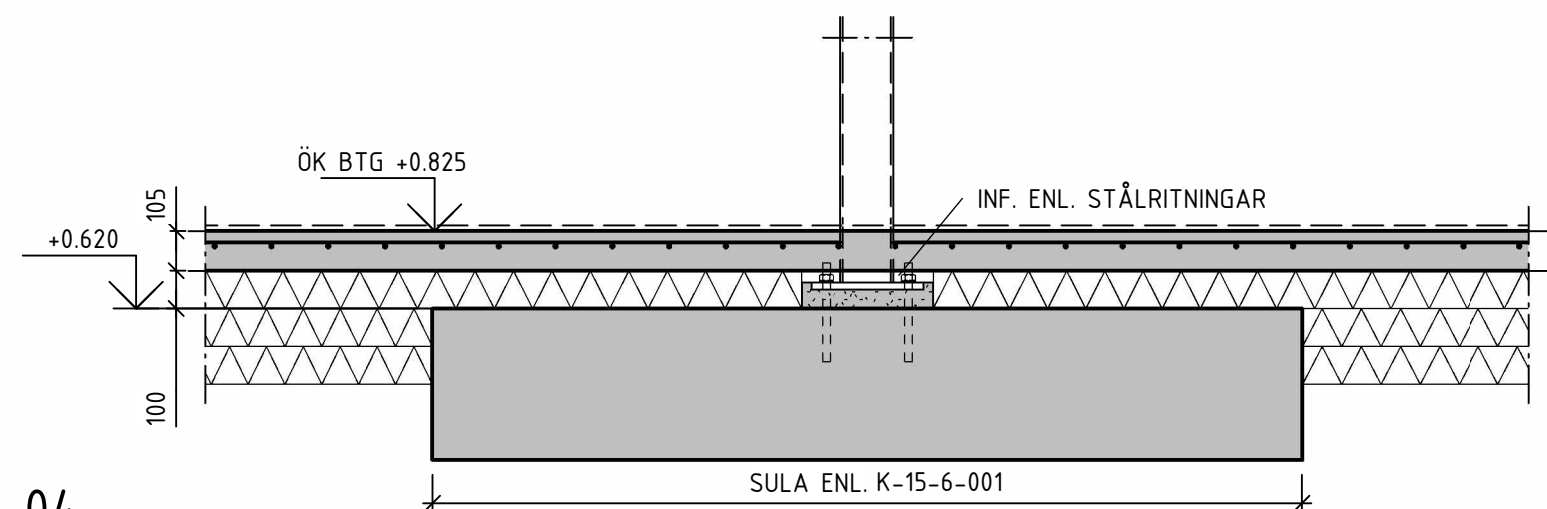


04
1 : 20
SULA UNDER GRUNDPLATTA

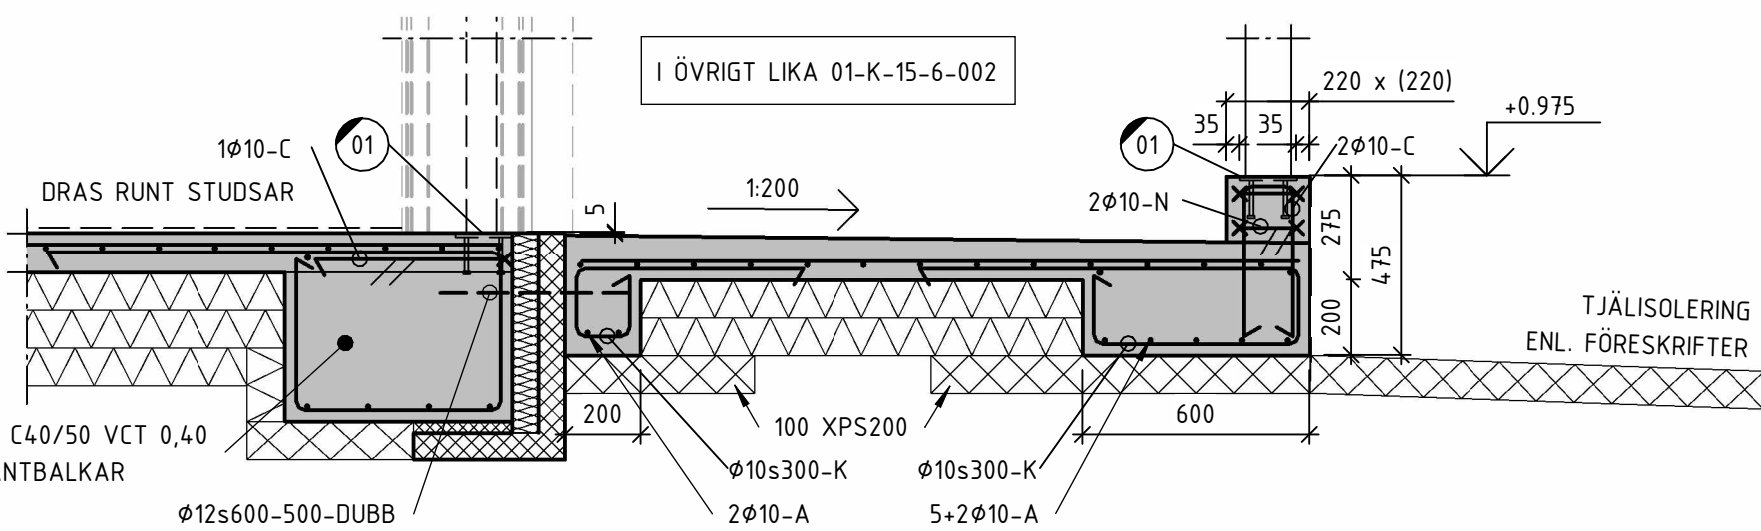


07
1 : 20
TVÄRSEKTION LASTKAJ

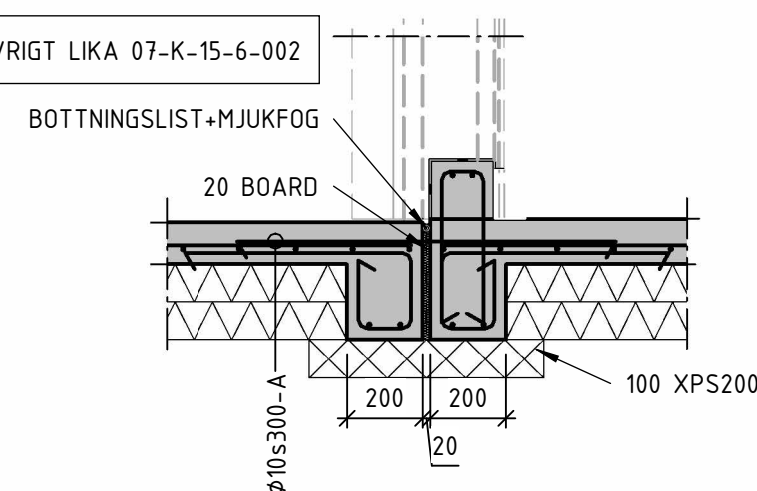


09
1 : 20
ÖVERGÅNG LASTKAJ OCH AVFALLSRUM

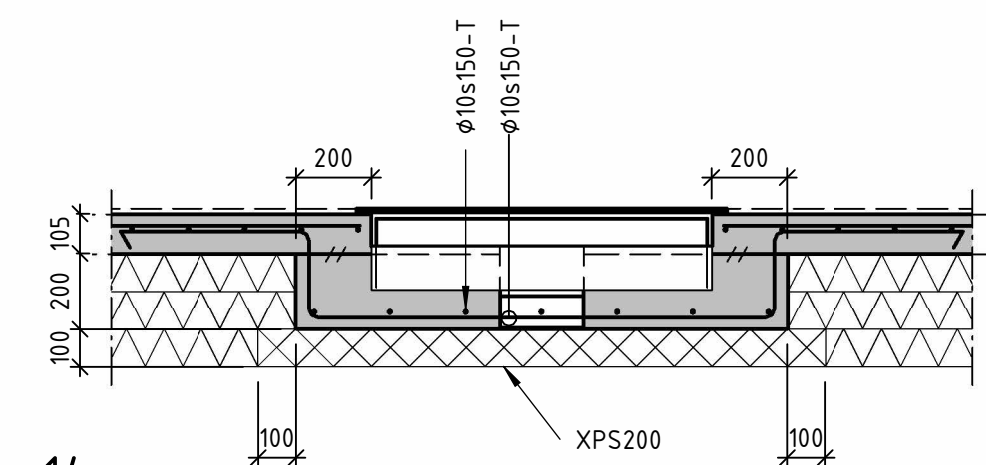


14
1 : 20
PRINCIPDETALJ AVLOPP I STORKÖK

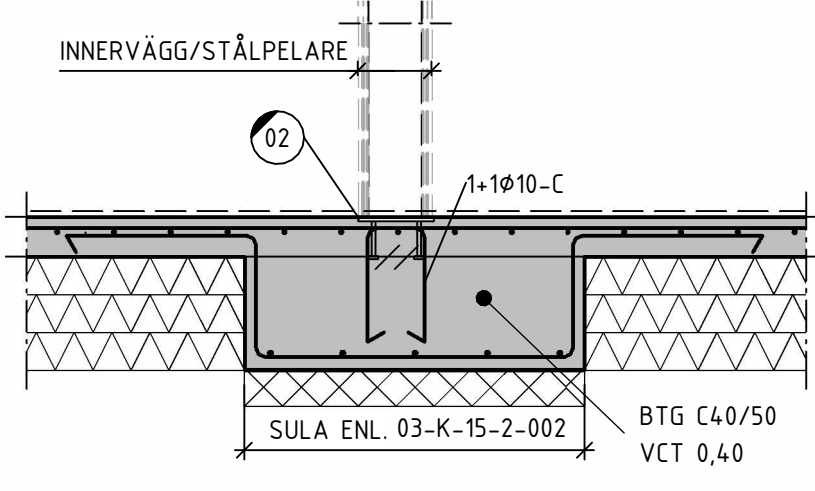


10
1 : 20
INGJUTNINGSGODS FÖR STÅLPELARE

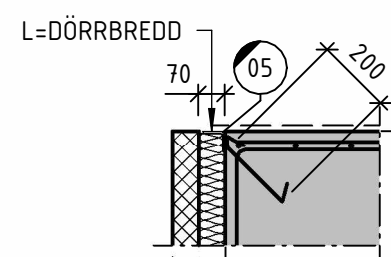


15
1 : 20
PRINCIPDETALJ L-STÅL UNDER YTTERDÖRRAR

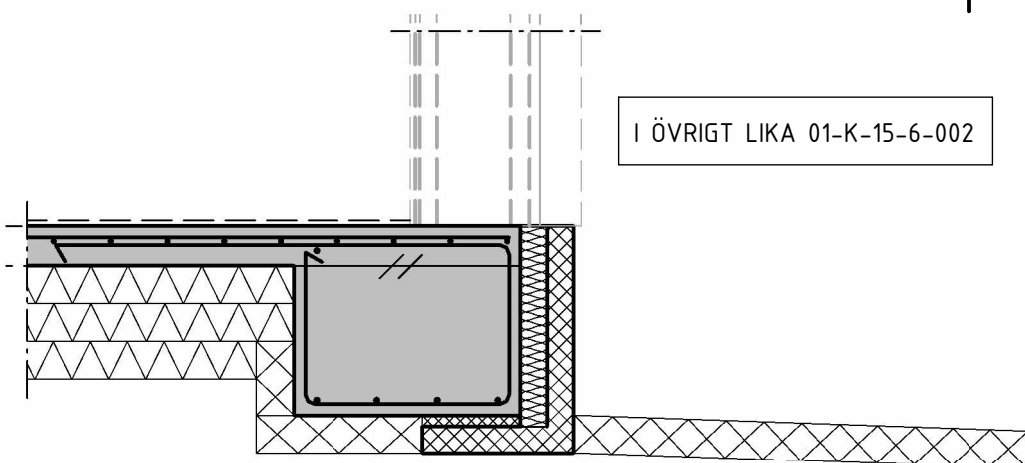


02
1 : 20
KANTBALK UNDER YTTERVÄGG

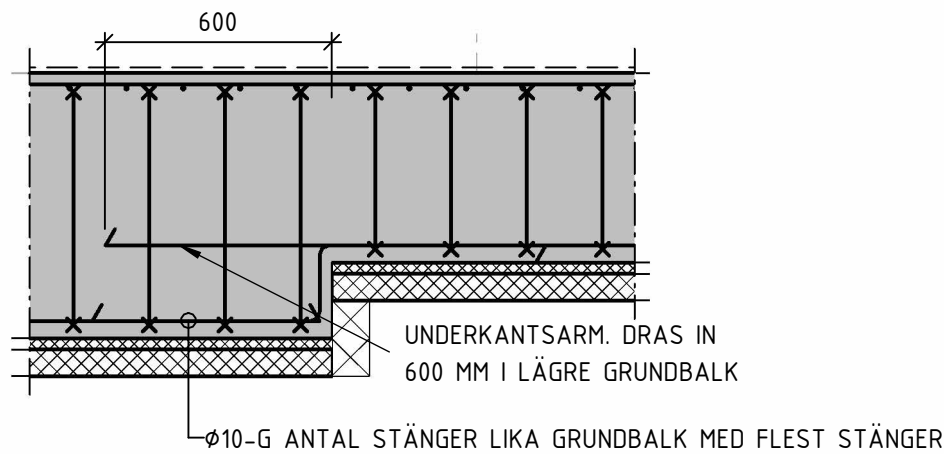


05
1 : 20
PRINCIPDETALJ ÖVERGÅNG KANTBALKSHÖJDER

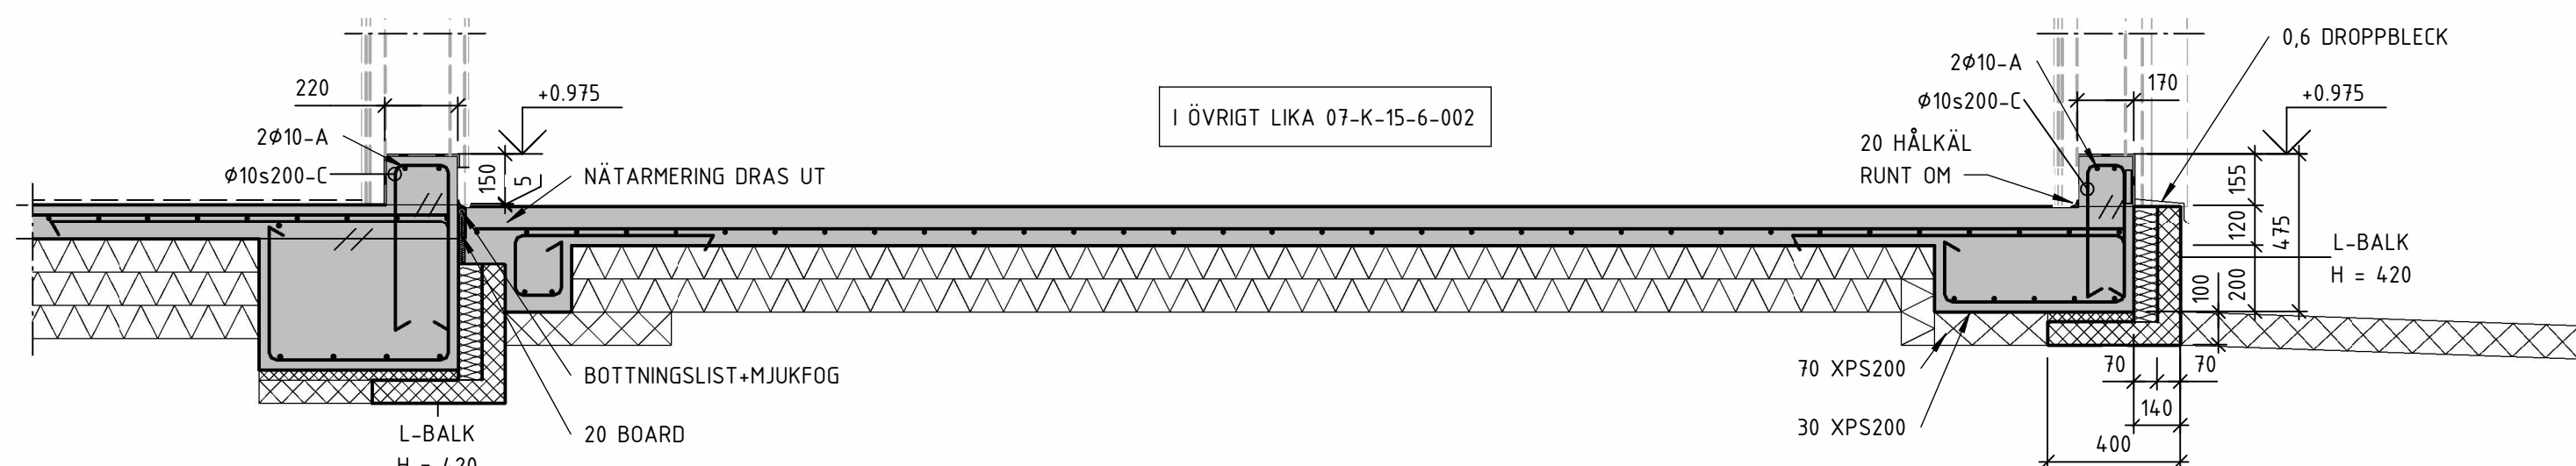


08
1 : 20
TVÄRSEKTION AVFALLSRUM

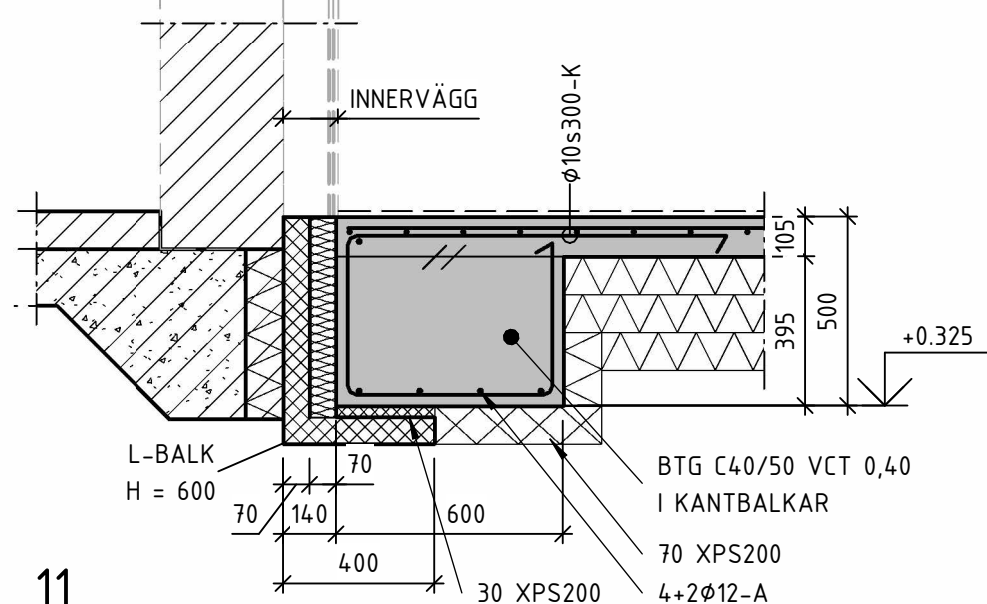


11
1 : 20
ANSLUTNING MOT BEFINTLIGT FRITIDS

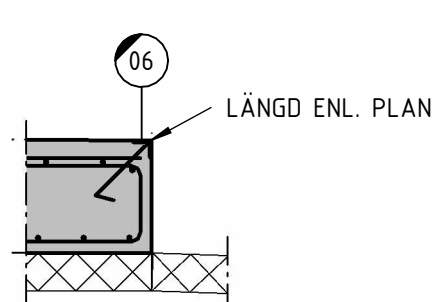


16
1 : 20
PRINCIPDETALJ KANTSKONING LASTKAJ

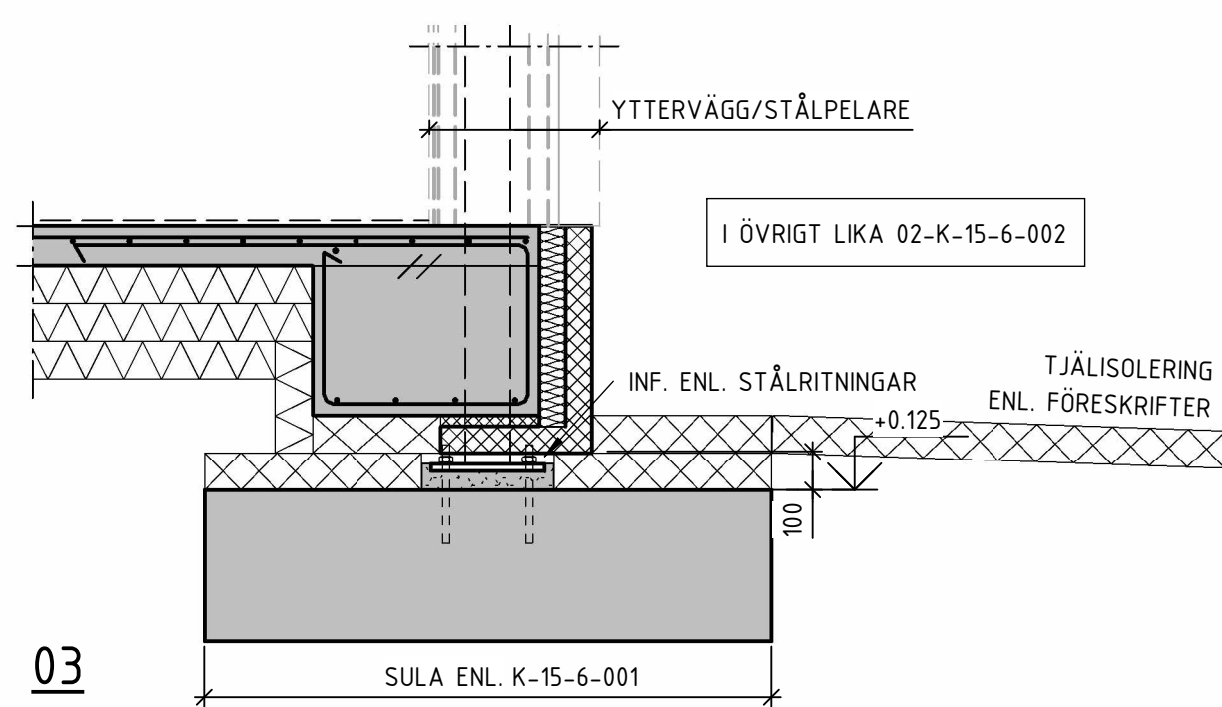


03
1 : 20
SULA UNDER KANTBALK

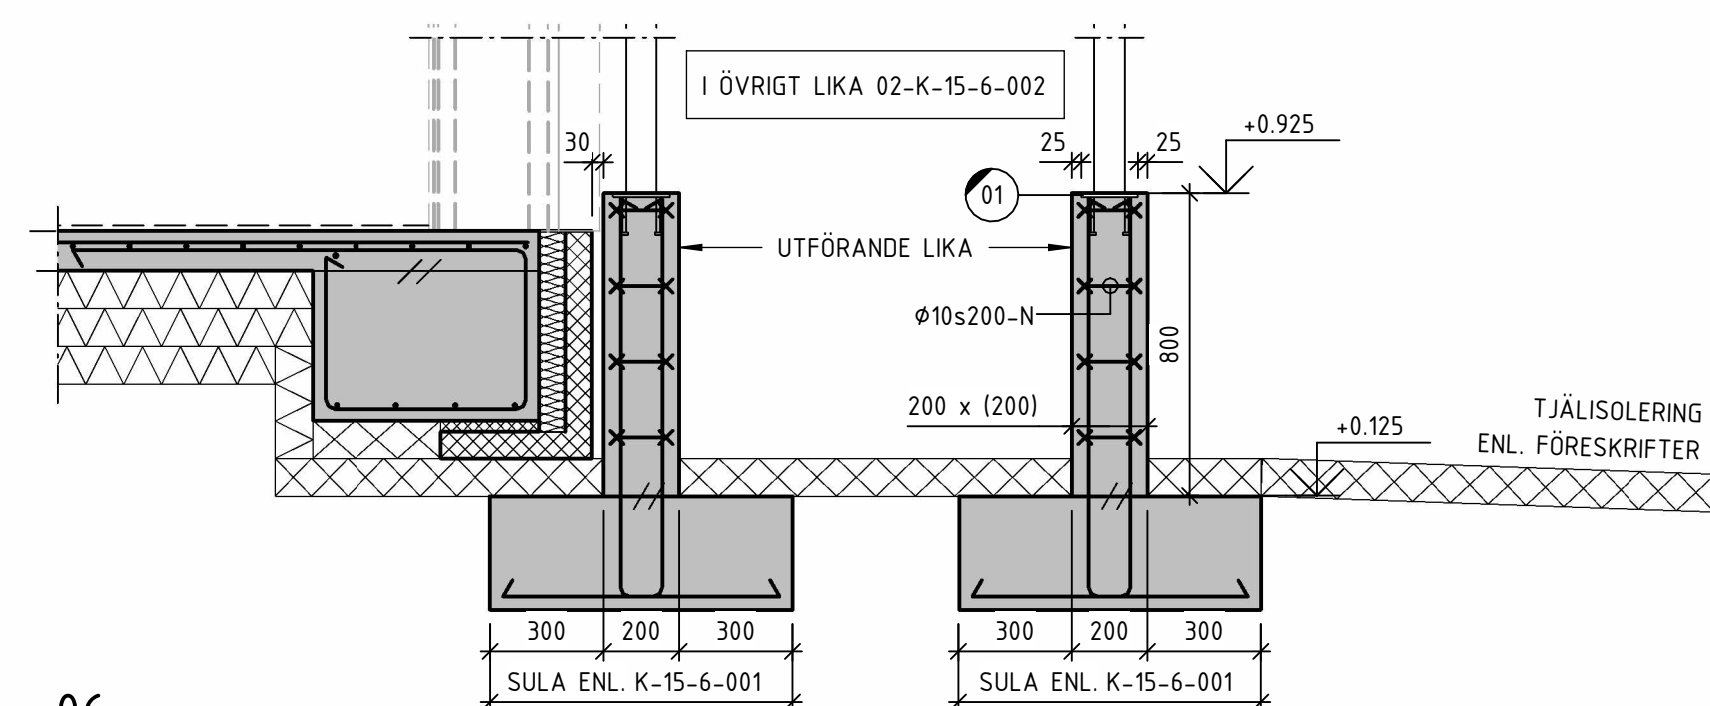

06
1 : 20
FUNDAMENT VID TRAPPA TILL FLÄKTRUM

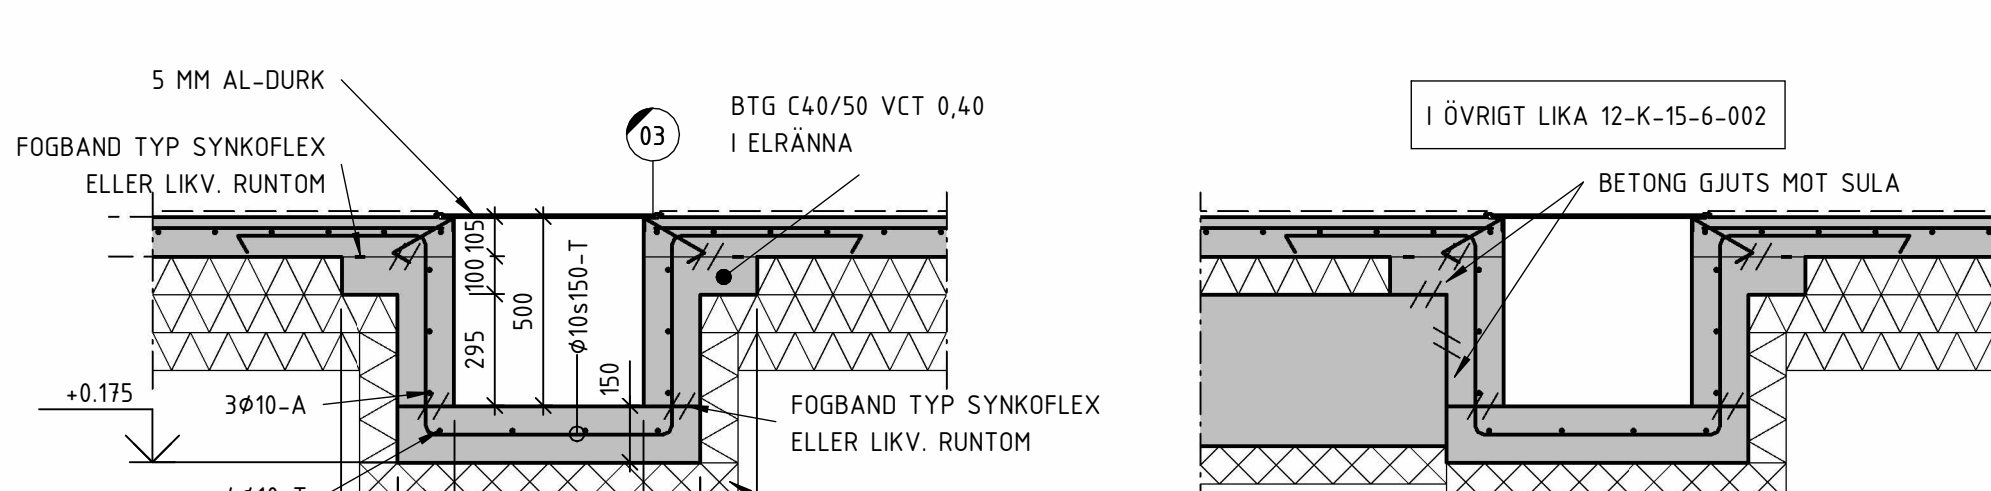

12
1 : 20
ELGROP

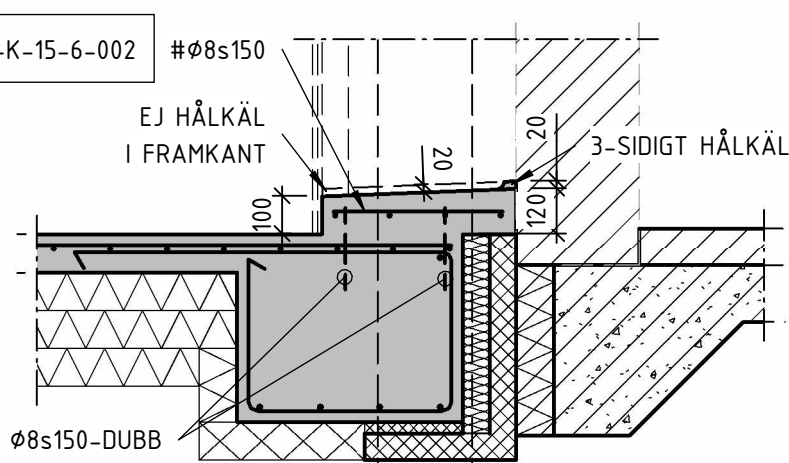

17
1 : 20
ANSLUTNING VID KULVERT MOT BEFINTLIGT FRITIDS

SKALA 1:20 0 1 2 METER

FÖRKLARINGAR

- BEFINTLIG BYGGNAD
- INGJUTNINGSGODS WELDA 150x150-110
- INGJUTNINGSGODS WELDA 200x200-72
- INGJUTNINGSGODS KANTSTÅL NR 2 DURKPLÅT S235JR
- INGJUTNINGSRAM L35x35x5 VFZ TYP WELAND ELLER LIKVÄRDIGT. UTBREDNING ENLIGT GRUNDPLAN
- INGJUTNINGSGODS L60x60x6 S235JR VFZ MED PÅSVETSADE (a5) KRAMLOR Ø8s200. GJUTS IN ENLIGT 15-K-15-6-002, ANTAL ENLIGT ANTAL DÖRRAR I YTTERVÄGG (12 ST), L = DÖRRBREDD
OBS! INGÅR EJ I STÅLLEVERANS
- INGJUTNINGSGODS L50x50x5 MED KRAMLOR Ø12x200/250 GALVANISERAD KANTSKONING TYP BE GROUP. LÄNGDER ENLIGT GRUNDPLAN.
OBS! INGÅR EJ I STÅLLEVERANS
- INGJUTNINGSRAM FÖR SKRAPMATTA ENLIGT BESKRIVNING.

PILMÅTT TAS FRÅN NÄRMAST LIGGANDE STÖMLINJE (MINST 1 METER)

FÖRESKRIFTER

K-01-0-001 -- 003 ALLMÄNNA FÖRESKRIFTER

HÄNVISNINGAR

-

SEKTION		
ORIENTERINGSSKISS		
DEL 7 DEL 2 DEL 3 DEL 1 DEL 4 DEL 5 DEL 6		
STATUS		
FÖRFRÅGNINGSUNDERLAG		
HANDLING		
BYGGHANDLING		
DATUM	FÖRBERED AV	ÄNDRINGS PM
2024-12-20	BJÖRN LIDSTRÖM	
BESTÄLLARE		
ROBERTSFORS KOMMUN		
PROJEKTNAMN		
CENTRALEKÖK		
OMRÅDE		
ROBERTSFORS KOMMUN		
PROJEKTNUMMER	FÄRRESE	
108 83 71	YTTERE RINGVÄGEN 4	
DOKUMENTNR	FASTIGHET	
	FORDONET 1	
DISCIPLIN	FÖRETAG	
K	NORCONSULT SVERIGE AB	
UPPDRAGSNUMMER	SKAPAD AV	
108 83 71	AWG/ATN	
TELEFON	KONTAKTPERSON	
010-141 80 00	BJÖRN LIDSTRÖM	
BYGGGÅRSTID	PRIS (KONTAKT)	
	+45,540 (FG)	
VÄNINGSPLAN	DELOMRÅDE	
	DEL 4, 5	
SYSTEM		
15 GRUNDKONSTRUKTIONER		
SPECIFIKATION		
GRUNDDETALJER		
DETALJ	SKALA	FORMAT
	1:20	A1
DOKUMENTNUMMER	ÄNDRING	
K-15-6-002		