




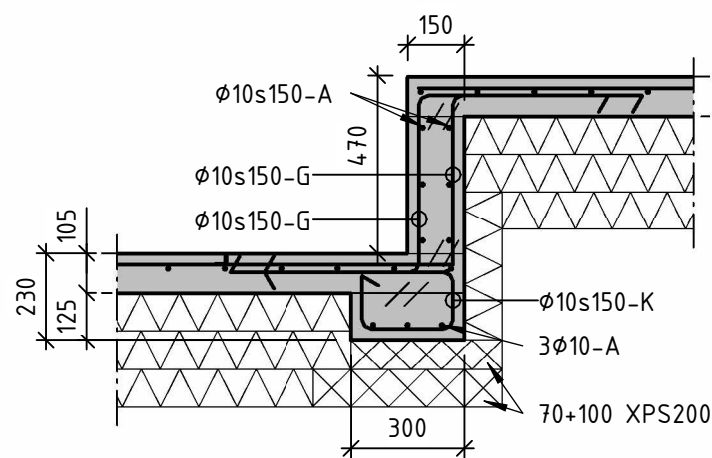


20
1 : 20
NIVÅSKILLNAD KAPPRUM

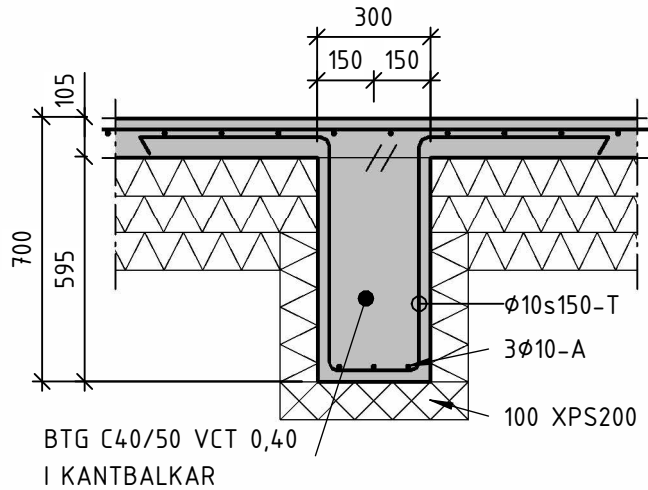


21
1 : 20
ANSLUTNING MOT SULA

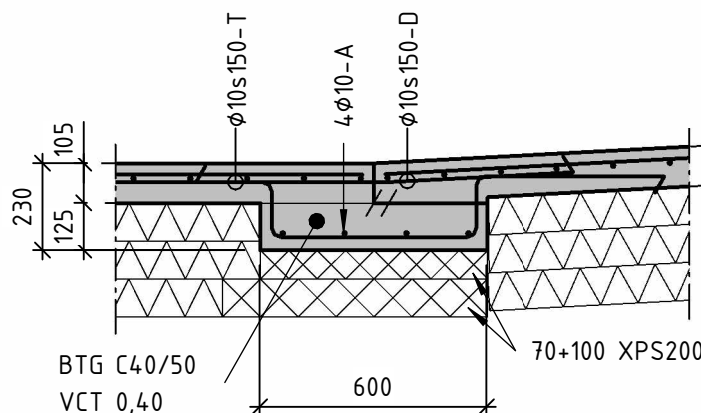


22
1 : 20
ANSLUTNING AV RAMP I BOTTEN

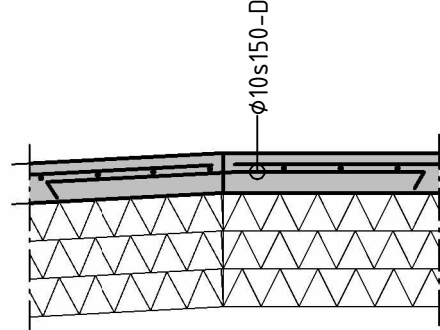

23
1 : 20
ANSLUTNING AV RAMP I TOPPEN

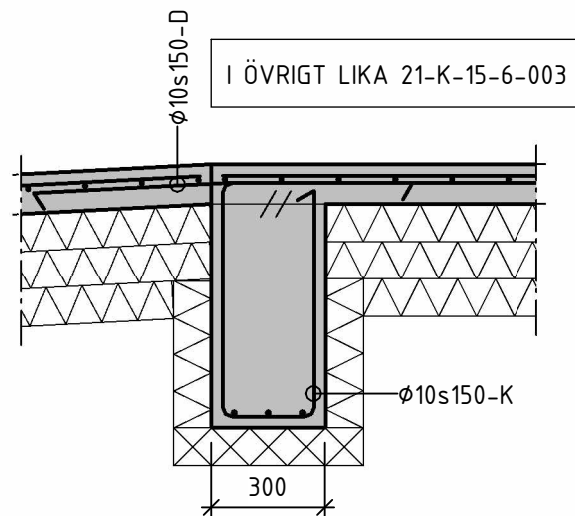

24
1 : 20
ANSLUTNING AV RAMP MOT SULA

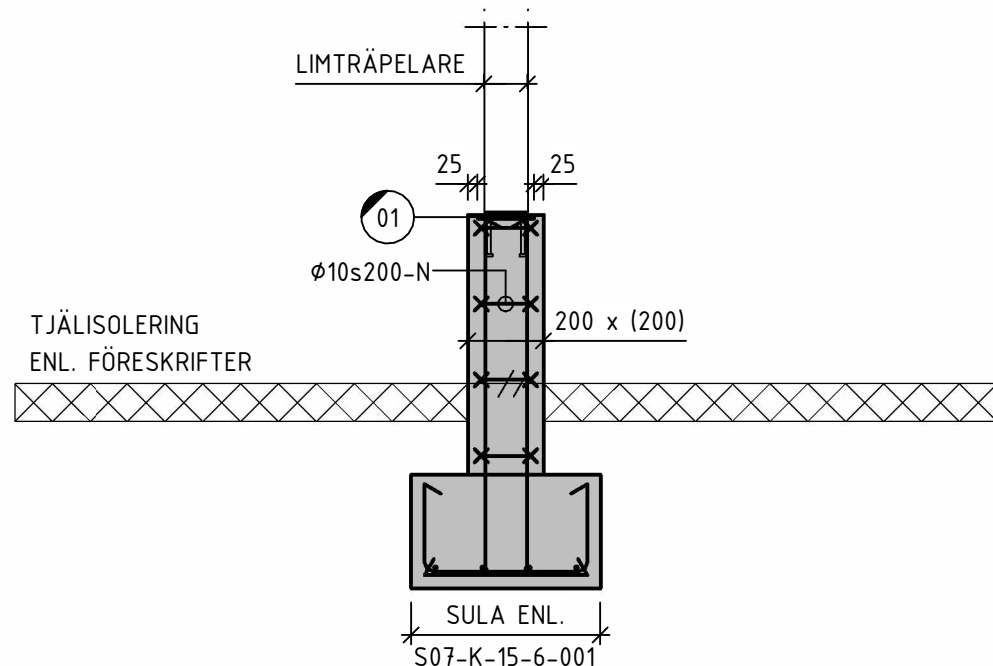

25
1 : 20
FUNDAMENT VID SKÄRMTAK VID ENTRÉ

FÖRKLARINGAR

- BEFINTLIG BYGGNAD
- 01 INGJUTNINGSGODS WELDA 150x150-110
 - 02 INGJUTNINGSGODS WELDA 200x200-72
 - 03 INGJUTNINGSGODS KANTSTÅL NR 2 DURKPLÅT S235JR
 - 04 INGJUTNINGSRAM L35x35x5 VFZ TYP WELAND ELLER LIKVÄRDIGT. UTREDNING ENLIGT GRUNDPLAN
 - 05 INGJUTNINGSGODS L60x60x6 S235JR VFZ MED PÅSVETSAD (a5) KRAMLOR Ø8s200. GJUTS IN ENLIGT 15-K-15-6-002, ANTAL ENLIGT ANTAL DÖRRAR I YTTERVÄGG (12 ST), L = DÖRRBREDD
OBS! INGÅR EJ I STÅLLEVERANS
 - 06 INGJUTNINGSGODS L50x50x5 MED KRAMLOR Ø12x200/250 GALVANISERAD KANTSKONING TYP BE GROUP. LÄNGDER ENLIGT GRUNDPLAN
OBS! INGÅR EJ I STÅLLEVERANS
 - 07 INGJUTNINGSRAM FÖR SKRAMPATTA ENLIGT BESKRIVNING.

PILMÅTT TAS FRÅN NÄRMAST LIGGANDE STÖMLINJE (MINST 1 METER)

FÖRESKRIFTER

K-01-0-001 -- 003 ALLMÄNNA FÖRESKRIFTER

HÄNVISNINGAR

-

SEKTION		
ORIENTERINGSSKISS		
STATUS		
FÖRFRÅGNINGSUNDERLAG		
HANDLING		
BYGGHANDLING		
DATUM	2024-12-20	ANSÖKAN AV
ADRESS	BJÖRN LIDSTRÖM	ÄNDRINGS FM
BESTÄLLARE		
PROJEKTNAMN		
CENTRALEKÖK		
OBJEKT		
ROBERTSFORS KOMMUN		
PROJEKTNUMMER	108 83 71	ADRESS
FASTIGHET	YTTRE RINGVÄGEN 4	
DIREKTOR	FORDONET 1	
DISCIPLIN	K	FÖRETAG
UPPDRAGSRUMMER	108 83 71	NORCONSULT SVERIGE AB
TELEFON	010-141 80 00	KONTAKTPERSON
BYGGNADSTYP		BJÖRN LIDSTRÖM
YTTREBYGGNAD		+45,540 (FG)
VÄNINGSPLAN		DEL 4, 5
SYSTEM	15 GRUNDKONSTRUKTIONER	
SPESIFIKATION	GRUNDDETALJER	
DETALJ	SKALA	FORMAT
K-15-6-003	1:20	A1
ÄNDRING		

SKALA 1:20 0 1 2 METER