

FÖRKLARINGAR

BEFINTLIG BYGGNAD

PILMÅTT TAS FRÅN NÄRMAST LIGGANDE STOMLINJE (MINST 1 METER)

INNERDÖRRAR OCH FÖNSTER VISAS ENDAST SCHEMATISKT I SAMTLIGA K-HANDLINGAR. FÖR EXAKT PLACERING OCH MÄTTSÄTTNING, SE A-HANDLINGAR.

DUBBLA VÄGGREGLAR PLACERAS PÅ RESPEKTIVE SIDA OM SAMTLIGA DÖRRAR OCH FÖNSTER I BÄRANDE VÄGGAR OM EJ ANNAT ANGES.

FÖRESKRIFTER

K-01-0-001 -- 003 ALLMÄNNA FÖRESKRIFTER


HÄNVISNINGAR

K-20-2-001 -- 011 BYGGSEKTIONER
K-20-6-001 BYGGDETALJER
K-20-6-002 BRANDINKLÄDNAD STÅL

K-23-0-100 HÅLDÄCKSPÄN

K-24-1-100 GRUNDBULTAR OCH PELARPLACERING
K-24-1-110 STÅLPLAN
K-24-1-210 STÅLPLAN ÖVRE DEL SAMT TAK
K-24-4-001 -- 004 STÅLELEVATIONER

K-25-1-100 TAKPLAN
K-25-4-001 TAKSTOLSELEVATIONER
K-25-4-002 HÅLTÄGNING BÄRLINA
K-25-6-001 BYGGDETALJER TAK

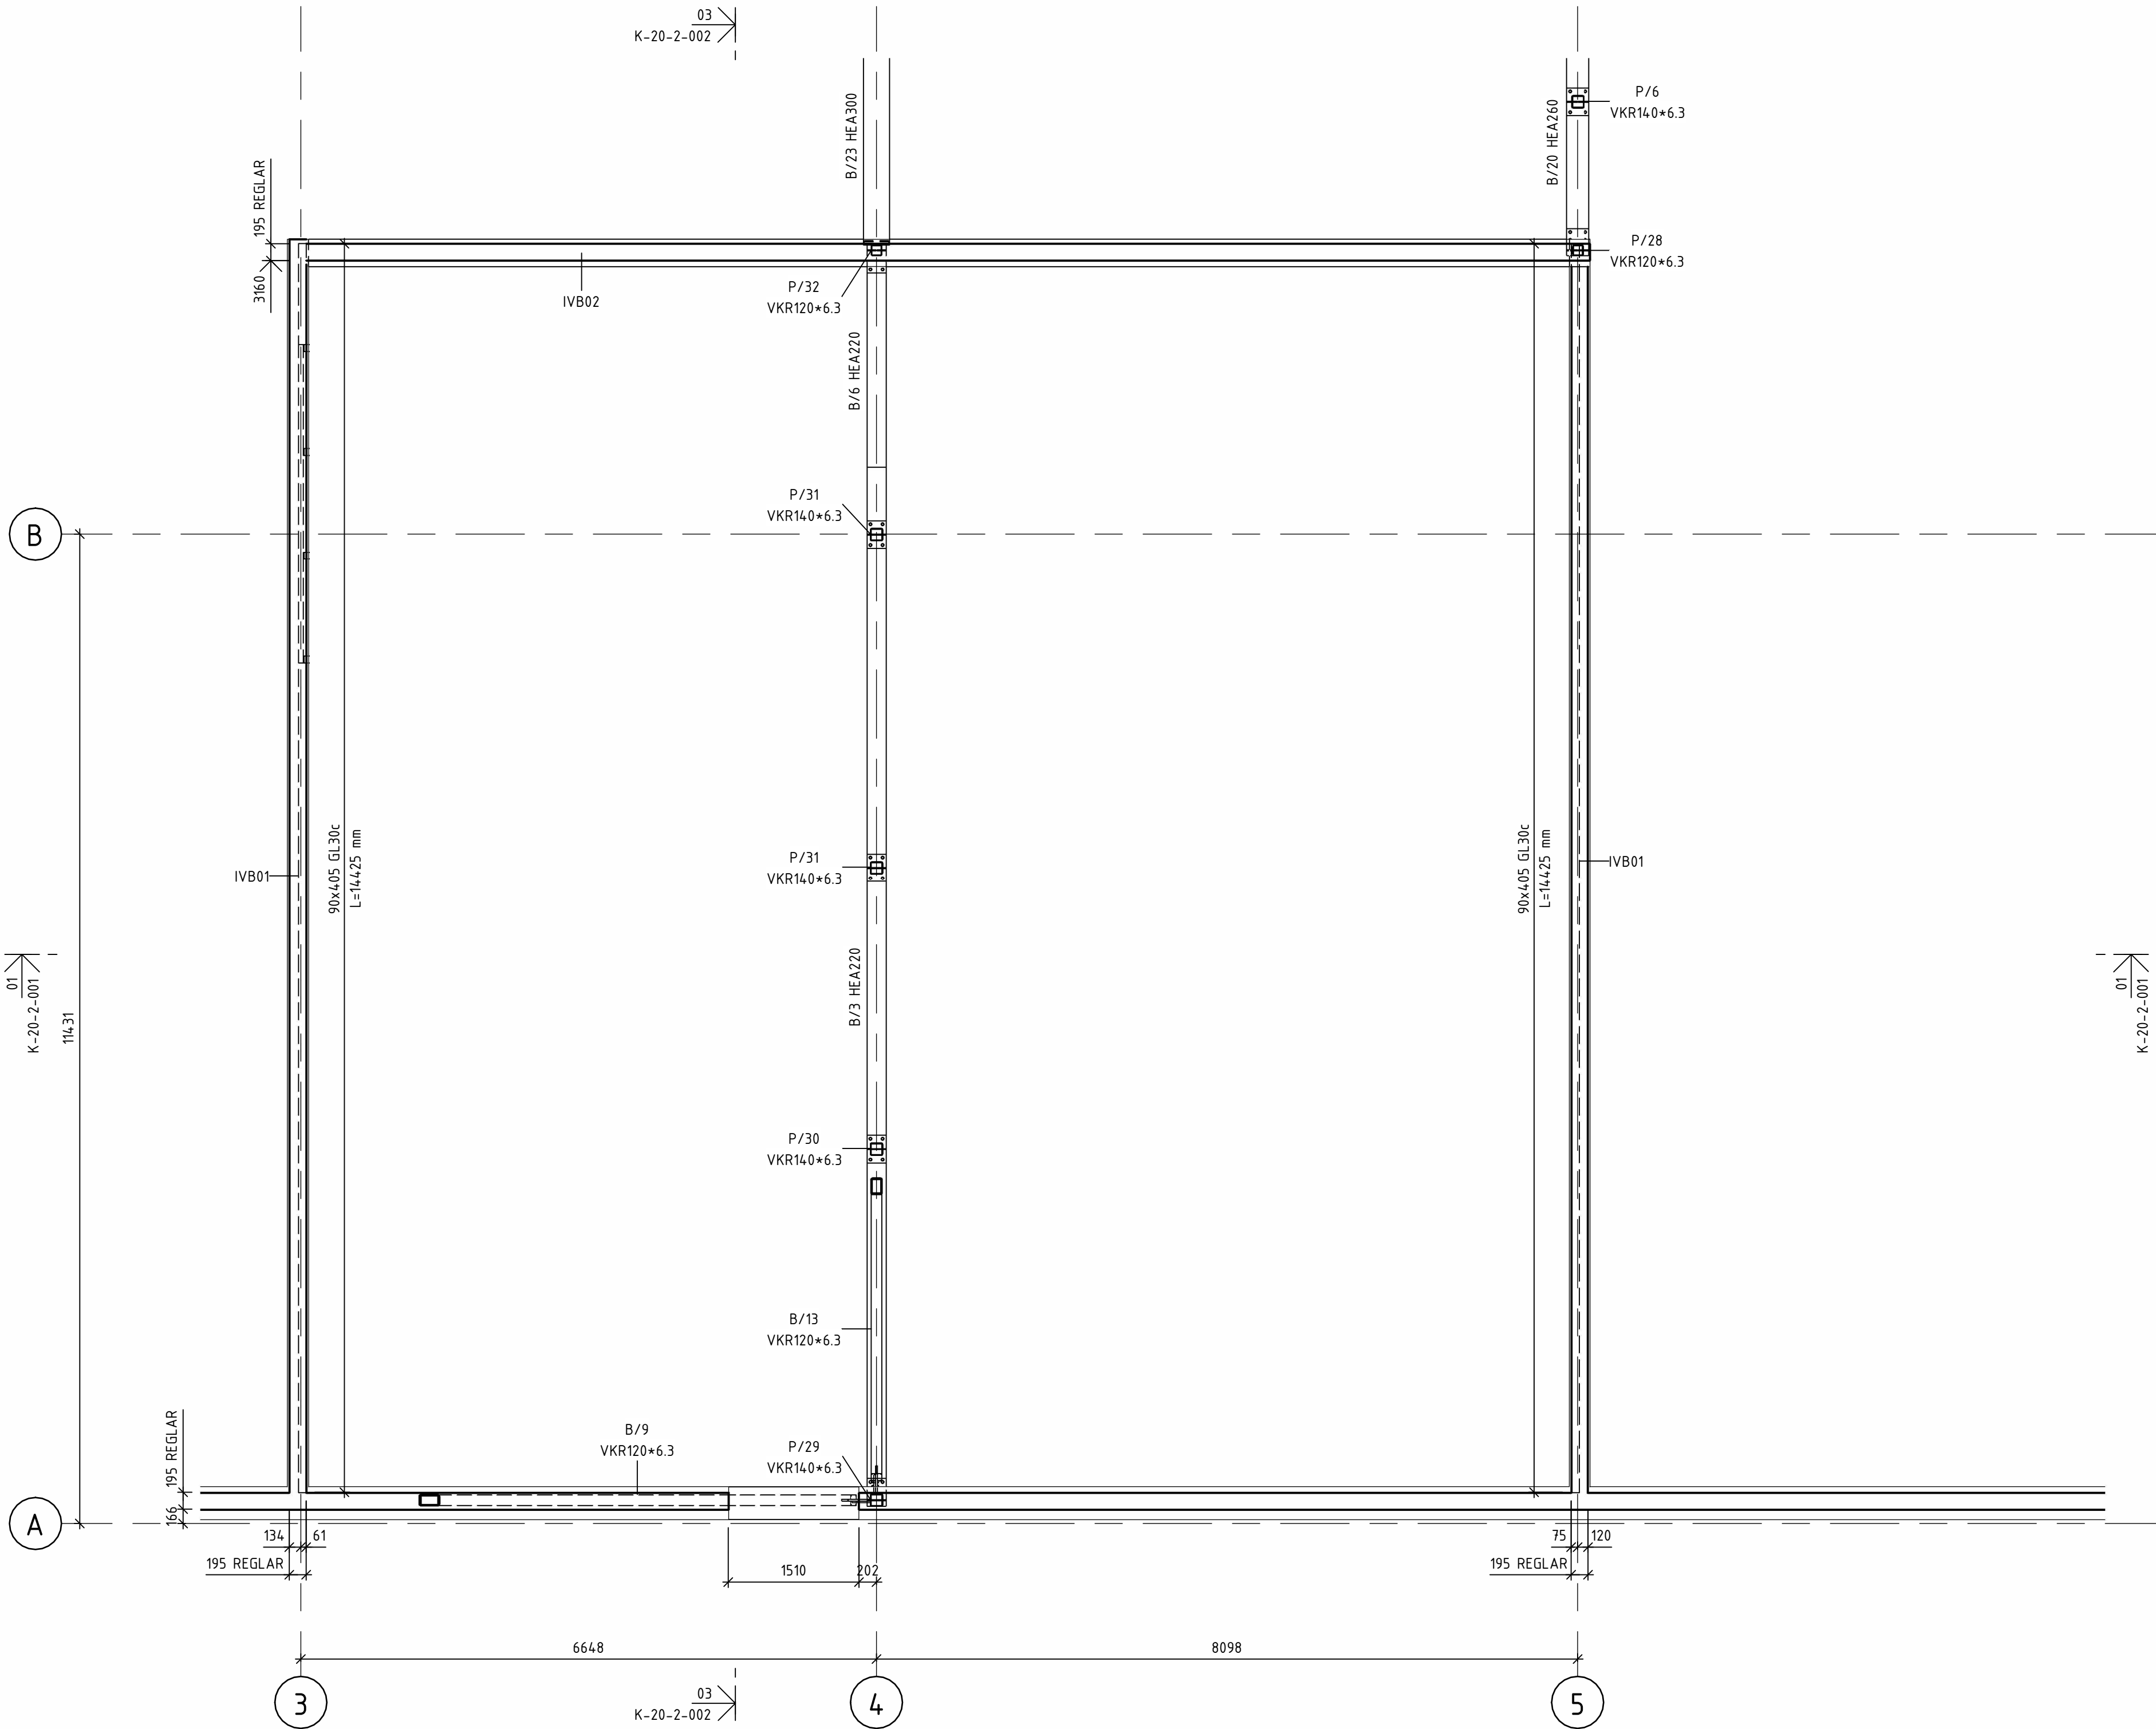

STOMPLAN FLÄKTRUM

1 : 50
VYRIKTNING UPPÅT

SKALA 1:50 0 1 5 METER

SEKTION

ORIENTERINGSSKISS

STATUS

FÖRFRÅGNINGSUNDERLAG

HANDLING

BYGGHANDLING

DATUM

2024-12-20

ANSÖKAN

BJÖRN LIDSTRÖM

ÄNDRINGS PM

BESTÄLLARE

PROJEKTNAMN

CENTRALEKÖ

OMRÅDE

ROBERTSFORS KOMMUN

PROJEKTNUMMER

108 83 71

FASTIGHET

FORDONET 1

DISCIPLIN

K

FÖRETAG

NORCONSULT SVERIGE AB

UPPDRAGSNUMMER

108 83 71

KONTAKTPERSON

AWG/ATN

TELEFON

010-141 80 00

FÖLJESÄNDARE

BJÖRN LIDSTRÖM

BYGGGÄLDSBEVÄR

+45,540 (FG)

VÄNINGSPLAN

VÄNINGSDEL

DEL 4, 5

SYSTEM

20 SAMMANSÄTTA KONSTRUKTIONER

SPECIFIKATION

STOMPLAN FLÄKTRUM

FORMAT

PLAN

SKALA

1:100

ÄNDRING

A1

DOCUMENTNUMMER

K-20-1-210