

FÖRKLARINGAR

BEFINTLIG BYGGNAD

PILMÅTT TAS FRÅN NÄRMAST LIGGANDE STOMLINJE (MINST 1 METER)

INNERDÖRRAR OCH FÖNSTER VISAS ENDAST SCHEMATISKT I SAMTLIGA K-HANDLINGAR. FÖR EXAKT PLACERING OCH MÄTTSÄTTNING, SE A-HANDLINGAR.

DUBBLA VÄGGREGLAR PLACERAS PÅ RESPEKTIVE SIDA OM SAMTLIGA DÖRRAR OCH FÖNSTER OM EJ ANNAT ANGES.

FÖRESKRIFTER

K-01-0-001 -- 003 ALLMÄNNA FÖRESKRIFTER


HÄNVISNINGAR

-

01

1 : 50

HUVUDSEKTION

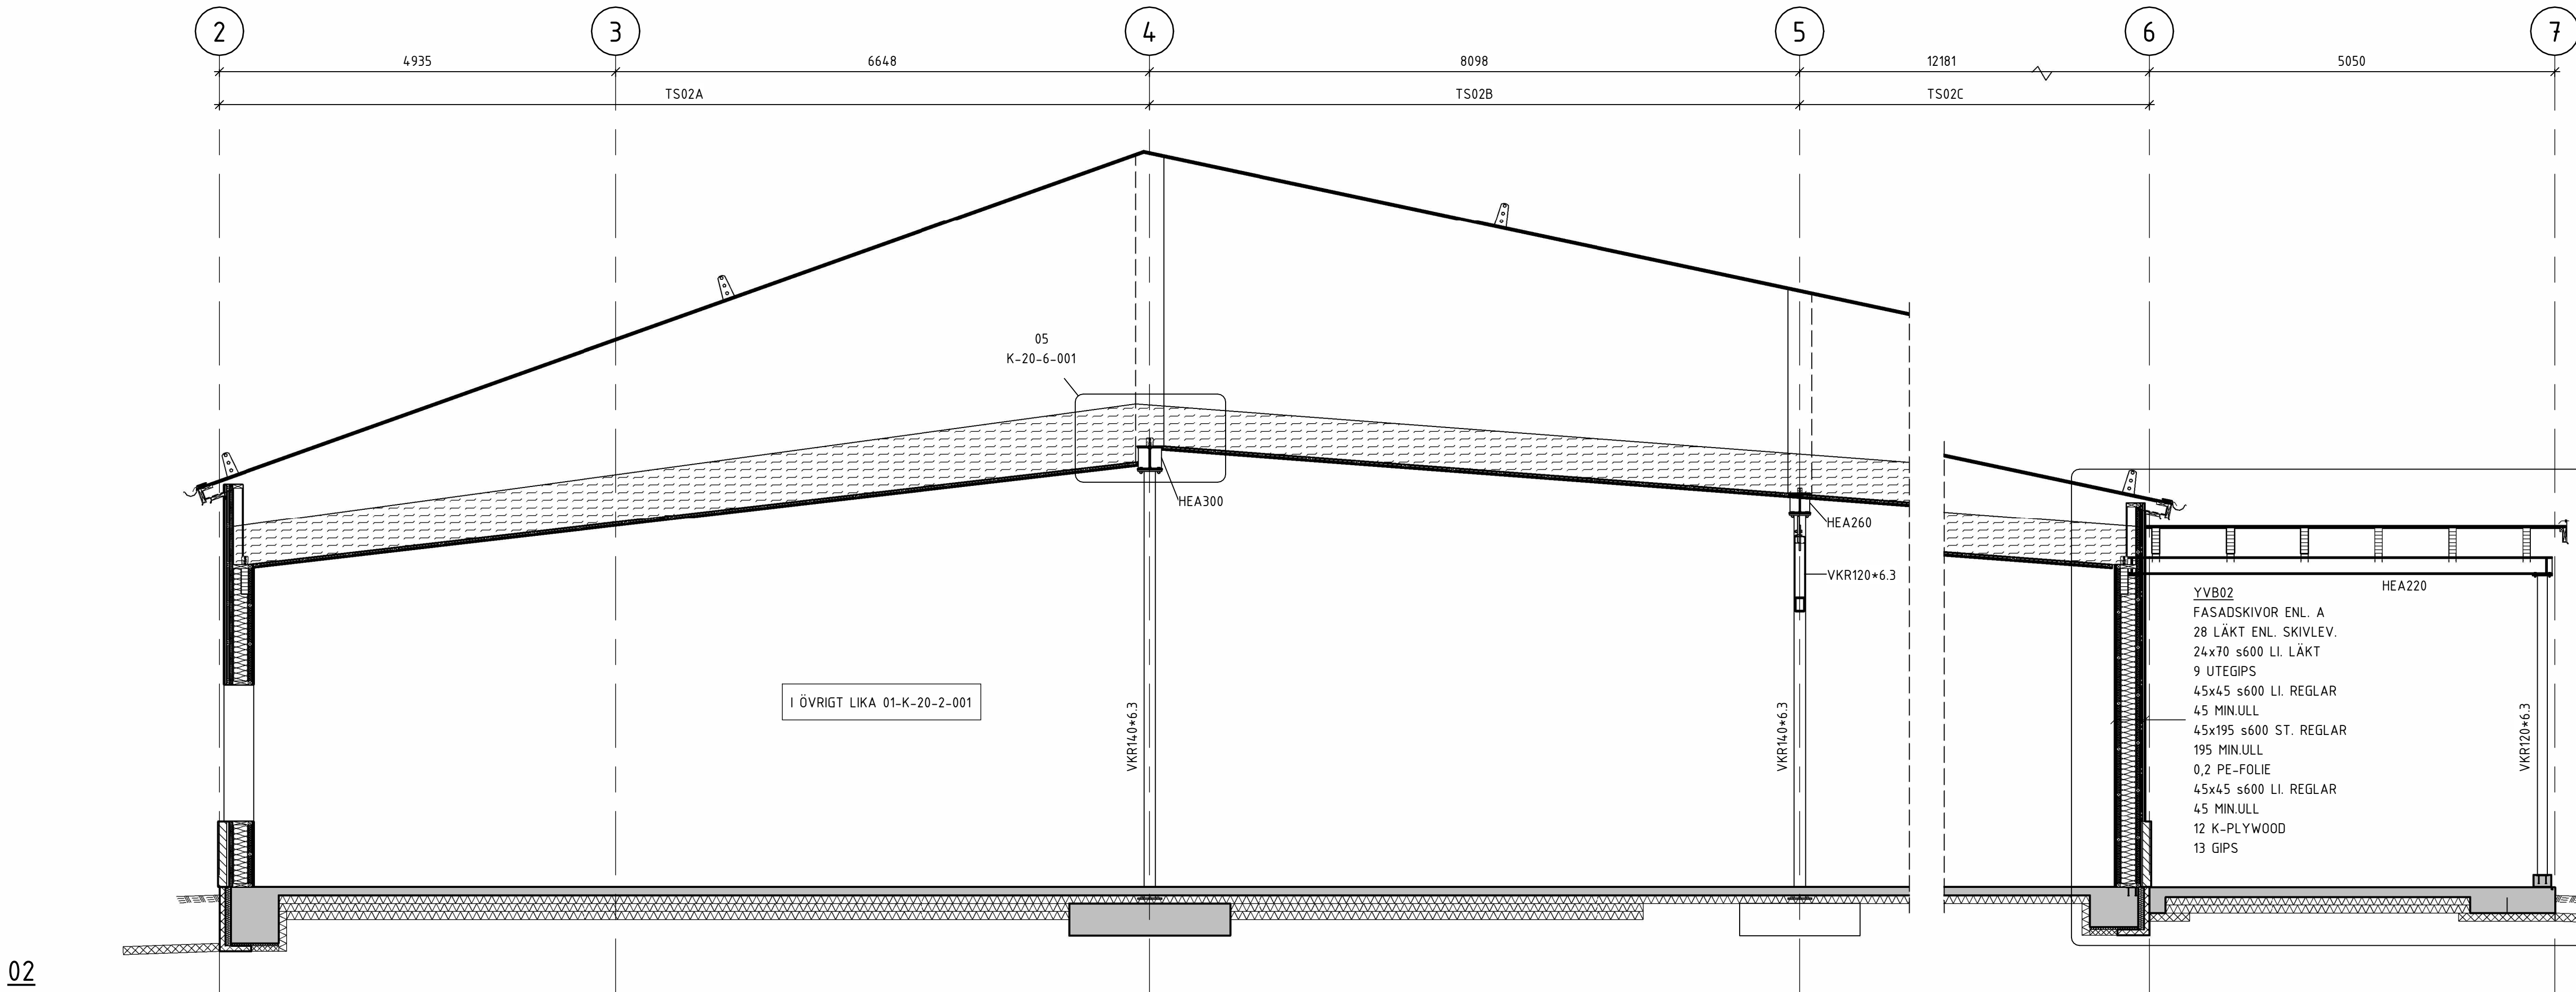

02

1 : 50

HUVUDSEKTION

SEKTION

ORIENTERINGSFIGUR

STATUS

FÖRFRÅGNINGSUNDERLAG

HANDLING

BYGGHANDLING

DATUM

2024-12-20

FÖRFRÅGAV

BJÖRN LIDSTRÖM

ANDRINGS PM

BESTÄLLARE

ROBERTSFORS KOMMUN

PROJEKTNAMN

CENTRALEKÖK

OMRÅDE

ROBERTSFORS KOMMUN

PROJEKTNUMMER

108 83 71

YTTRE RINGVÄGEN 4

DÅRERNUMMER

FASTIGHET

FORDONET 1

DISCIPLIN

K

FÖRETAG

NORCONSULT SVERIGE AB

UPPDRAGSNUMMER

108 83 71

SKAPAD AV

AWG/ATN

TELEFON

010-141 80 00

KONTAKTPERSON

BJÖRN LIDSTRÖM

BYGGGÅRSTYRELSE

FÖLJESÄNDARE

+45,540 (FG)

YANINGSPLAN

YANINGSDEL

DEL 4, 5

SYSTEM

20 SAMMANSATTA KONSTRUKTIONER

SPECIFIKATION

HUVUDSEKTIONER

SEKTION

SKALA

1:50

FORMAT

A1

ANDRINGS

K-20-2-001