

FÖRKLARINGAR

BEFINTLIG BYGGNAD

PILMÅTT TAS FRÅN NÄRMAST LIGGANDE STOMLINJE (MINST 1 METER)

INNERDÖRRAR OCH FÖNSTER VISAS ENDAST SCHEMATISKT I SAMTLIGA K-HANDLINGAR. FÖR EXAKT PLACERING OCH MÄTTSÄTTNING, SE A-HANDLINGAR.


DUBBLA VÄGGREGLAR PLACERAS PÅ RESPEKTIVE SIDA OM SAMTLIGA DÖRRAR OCH FÖNSTER OM EJ ANNAT ANGES.

FÖRESKRIFTER


K-01-0-001 -- 003 ALLMÄNNA FÖRESKRIFTER

HÄNVISNINGAR

-

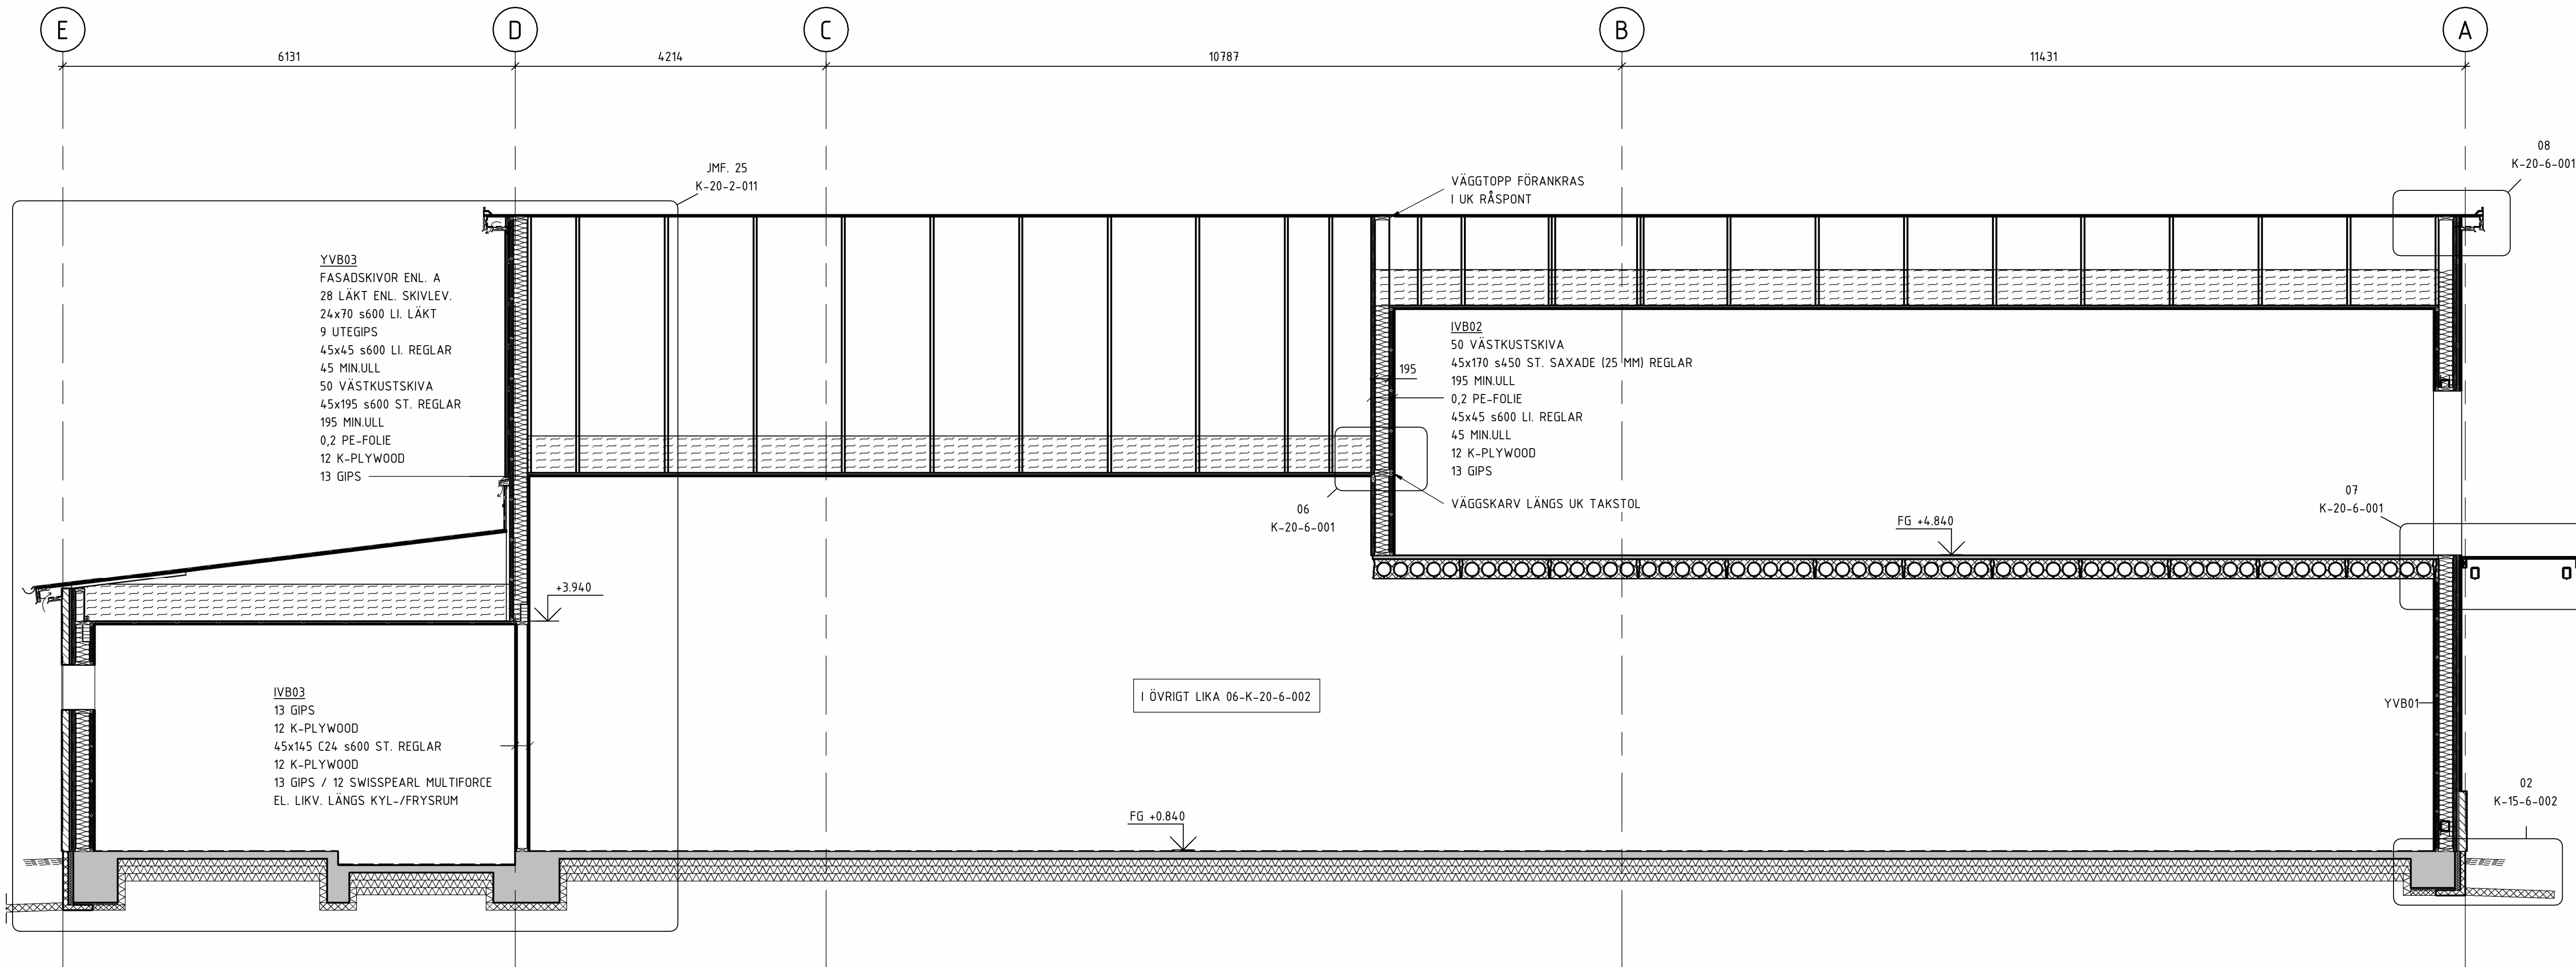

03
1 : 50
HUVUDSEKTION

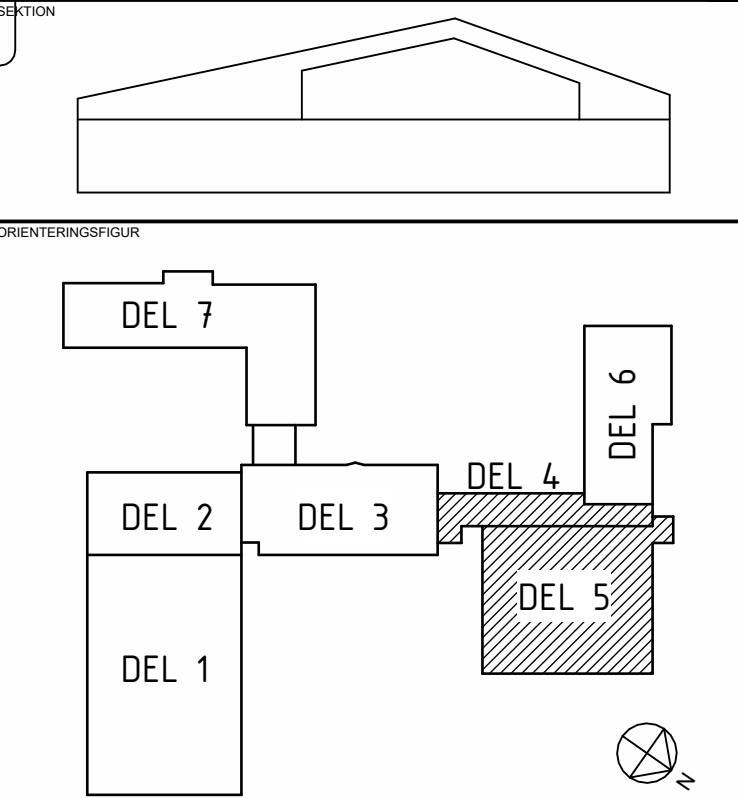

STATUS		
FÖRFRÅGNINGSUNDERLAG		
HANDLING		
BYGGHANDLING		
DATUM	2024-12-20	TEGNADE AV
		BJÖRN LIDSTRÖM
ANDRINGS PM		
BESTÄLLARE		
 ROBERTSFORS KOMMUN		
PROJEKTNAMN		
CENTRALEKÖ		
OBJEKT		
ROBERTSFORS KOMMUN		
PROJEKTNUMMER	108 83 71	ADRESS
		YTTRE RINGVÄGEN 4
DOKUMENT		FASTIGHET
		FORDONET 1
DISCIPLIN	K	FÖRETAG
		NORCONSULT SVERIGE AB
UPPDRAGSNUMMER	108 83 71	SKAPAD AV
		AWG/ATN
TELEFON	010-141 80 00	KONTAKTPERSON
		BJÖRN LIDSTRÖM
BYGGKOSTNAD		FÖLJANDE PRIS
		+45,540 (FG)
VÄNINGSPLAN		DELNING
		DEL 4, 5
SYSTEM		
20 SAMMANSATTA KONSTRUKTIONER		
SPECIFIKATION		
HUVUDSEKTIONER		
SEKTION		SKALA
		1:50
FORMAT		A1
DOKUMENTNUMMER		ANDRING
K-20-2-002		

SKALA 1:50 0 1 5 METER