

FÖRKLARINGAR

BEFINTLIG BYGGNAD

PILMÅTT TAS FRÅN NÄRMAST LIGGANDE STOMLINJE (MINST 1 METER)

INNERDÖRRAR OCH FÖNSTER VISAS ENDAST SCHEMATISKT I SAMTLIGA K-HANDLINGAR. FÖR EXAKT PLACERING OCH MÄTTSÄTTNING, SE A-HANDLINGAR.


DUBBLA VÄGGREGLAR PLACERAS PÅ RESPEKTIVE SIDA OM SAMTLIGA DÖRRAR OCH FÖNSTER OM EJ ANNAT ANGES.

FÖRESKRIFTER


K-01-0-001 -- 003 ALLMÄNNA FÖRESKRIFTER

HÄNVISNINGAR

-

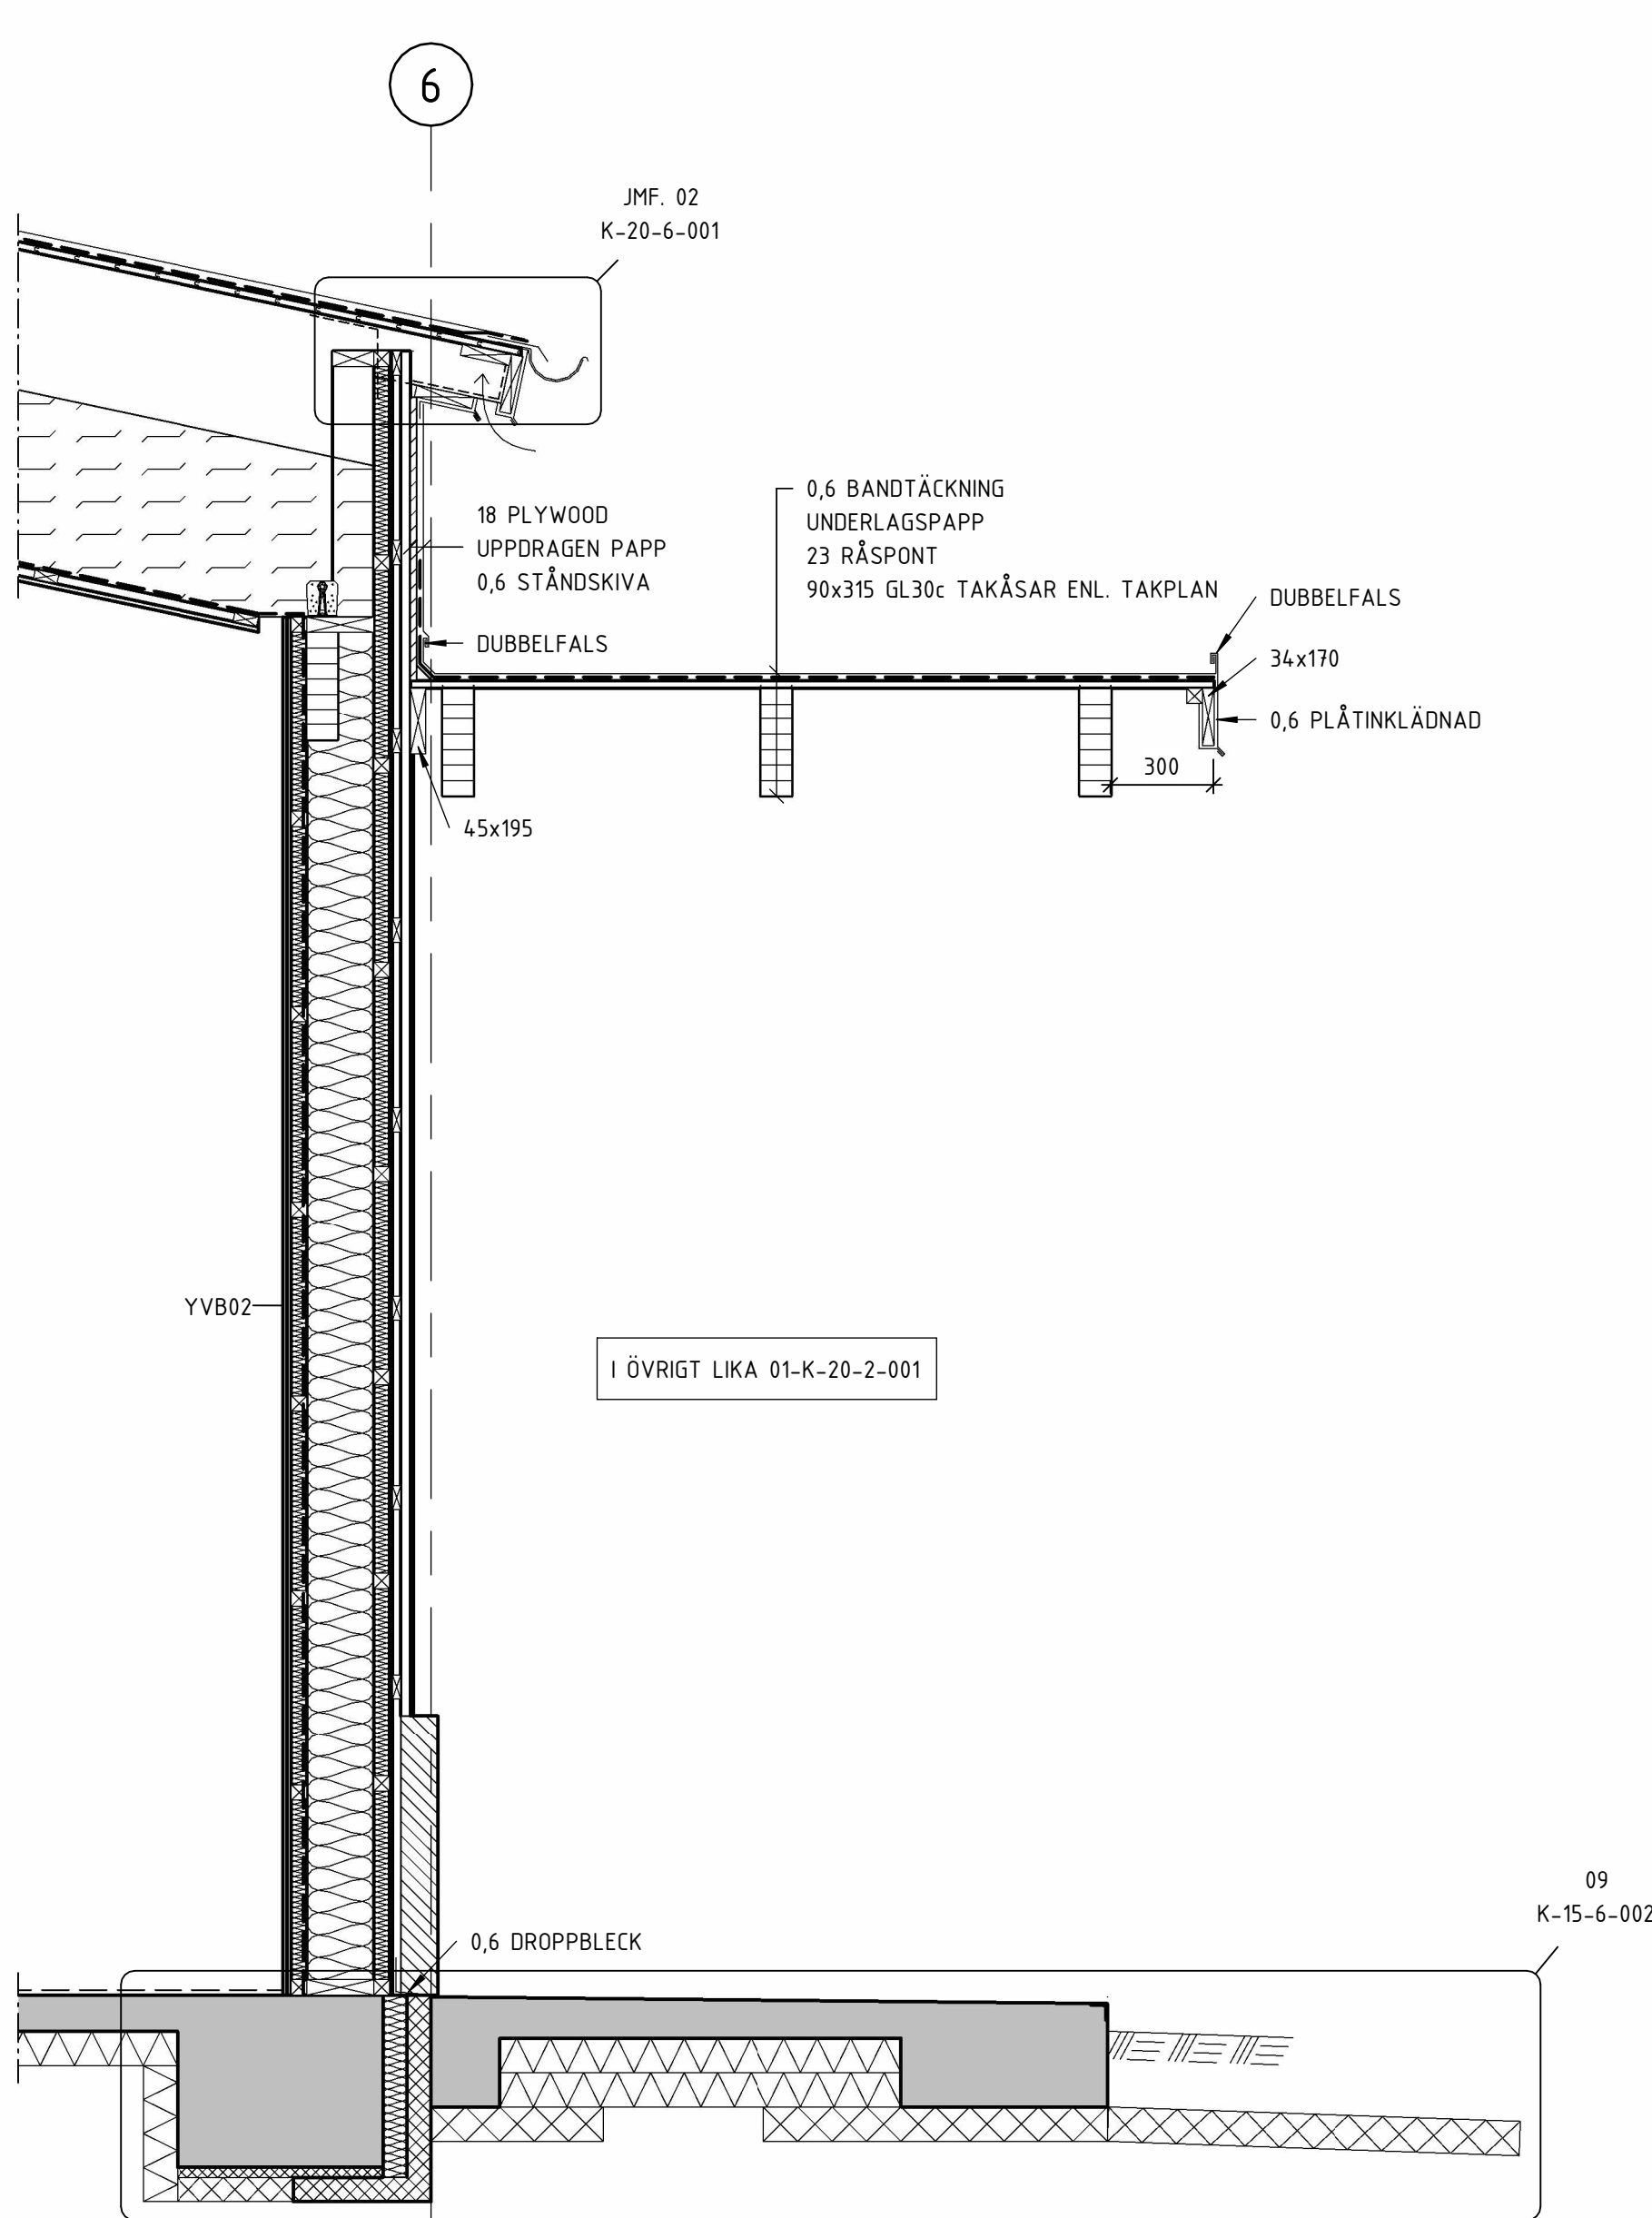

04
1 : 20
LASTKAJ

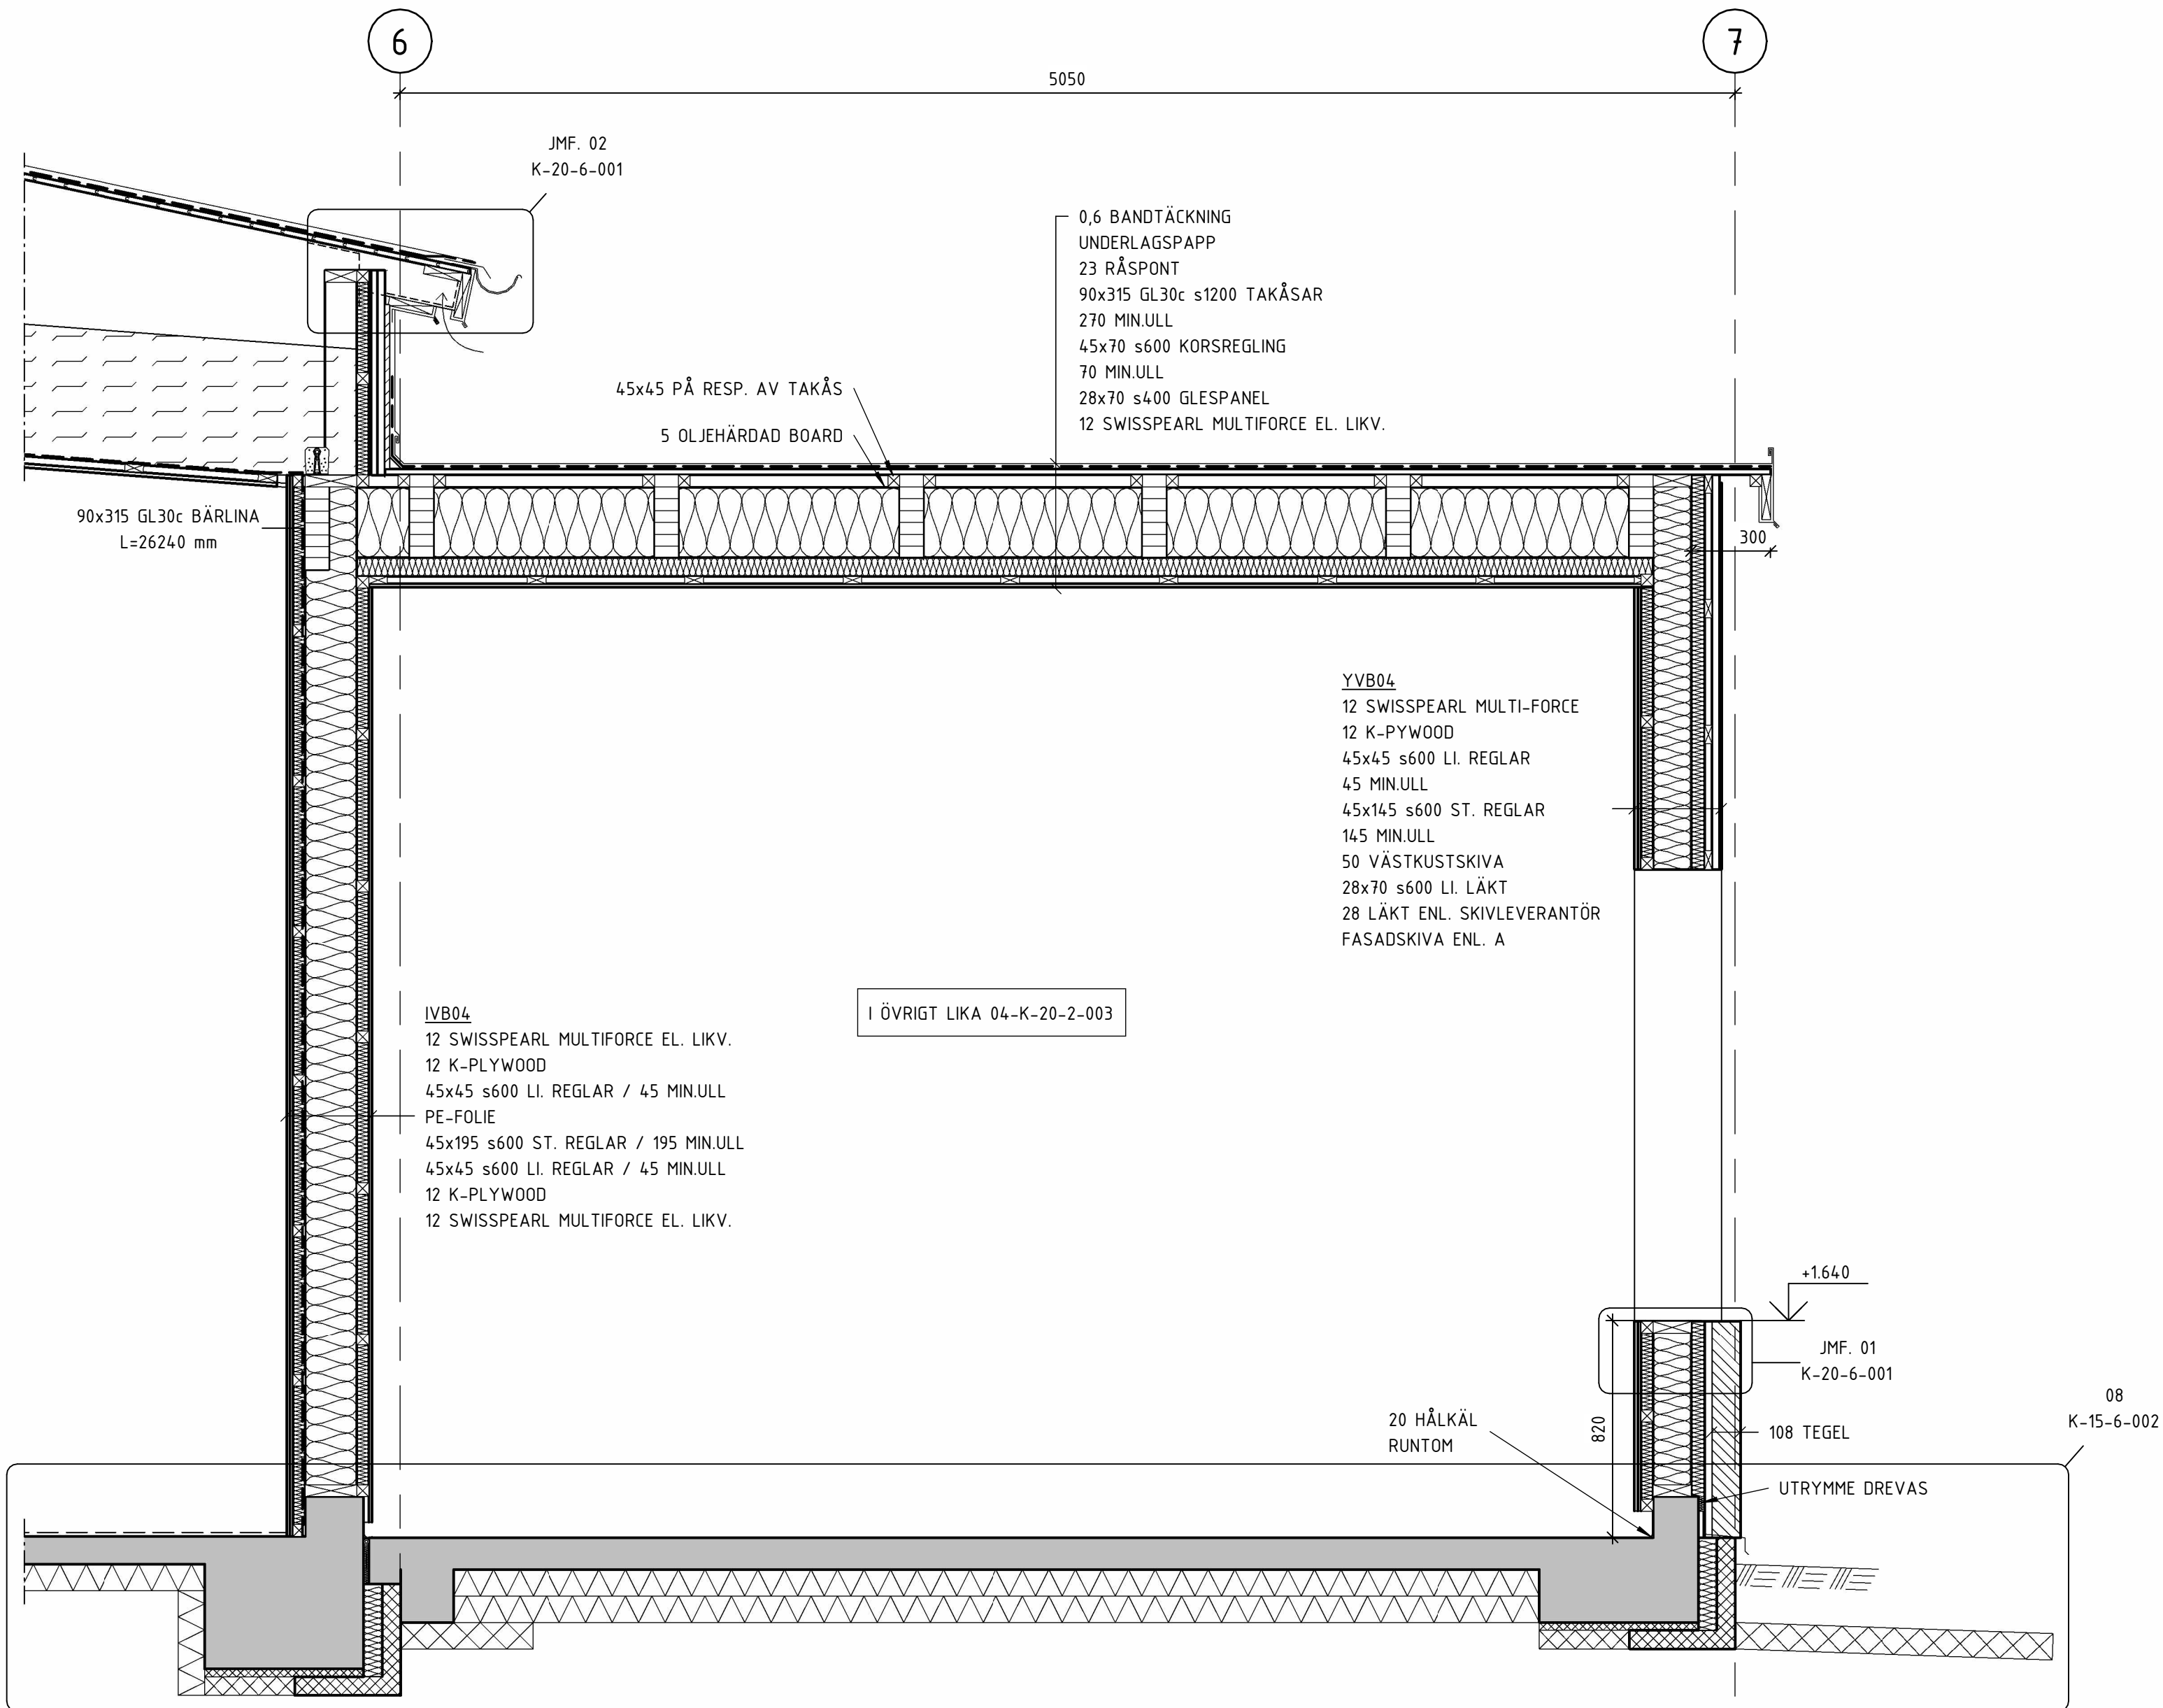

05
1 : 20
AVFALLSRUM

SKALA 1:20 0 1 2 METER

SEKTION

ORIENTERINGSFIGUR

DEL 7
DEL 2
DEL 1
DEL 3
DEL 4
DEL 5
DEL 6

STATUS
FÖRFRÅGNINGSUNDERLAG

HANDLING
BYGGHANDLING

DATUM
2024-12-20

ANSÖKAN AV
BJÖRN LIDSTRÖM

ANDRINGS PM

BESTÄLLARE

ROBERTSFORS
KOMMUN

PROJEKTNAMN
CENTRALEKÖK

OMRÅDE
ROBERTSFORS KOMMUN

PROJEKTNUMMER
108 83 71

FASTIGHET
YTTRE RINGVÄGEN 4

DISCIPLIN
K

FÖRETAG
NORCONSULT SVERIGE AB

UPPDRAGSRUMMER
108 83 71

SKAPAD AV
AWG/ATN

TELEFON
010-141 80 00

KONTAKTPERSON
BJÖRN LIDSTRÖM

BYGGGÅRSTYCKE
+45,540 (FG)

VÄNINGSPLAN
VÄNINGSDEL
DEL 4, 5

SYSTEM
20 SAMMANSATTA KONSTRUKTIONER

SEKTIONER

SEKTION

SKALA
1:20

FORMAT
A1

ANDRINGS

K-20-2-003