



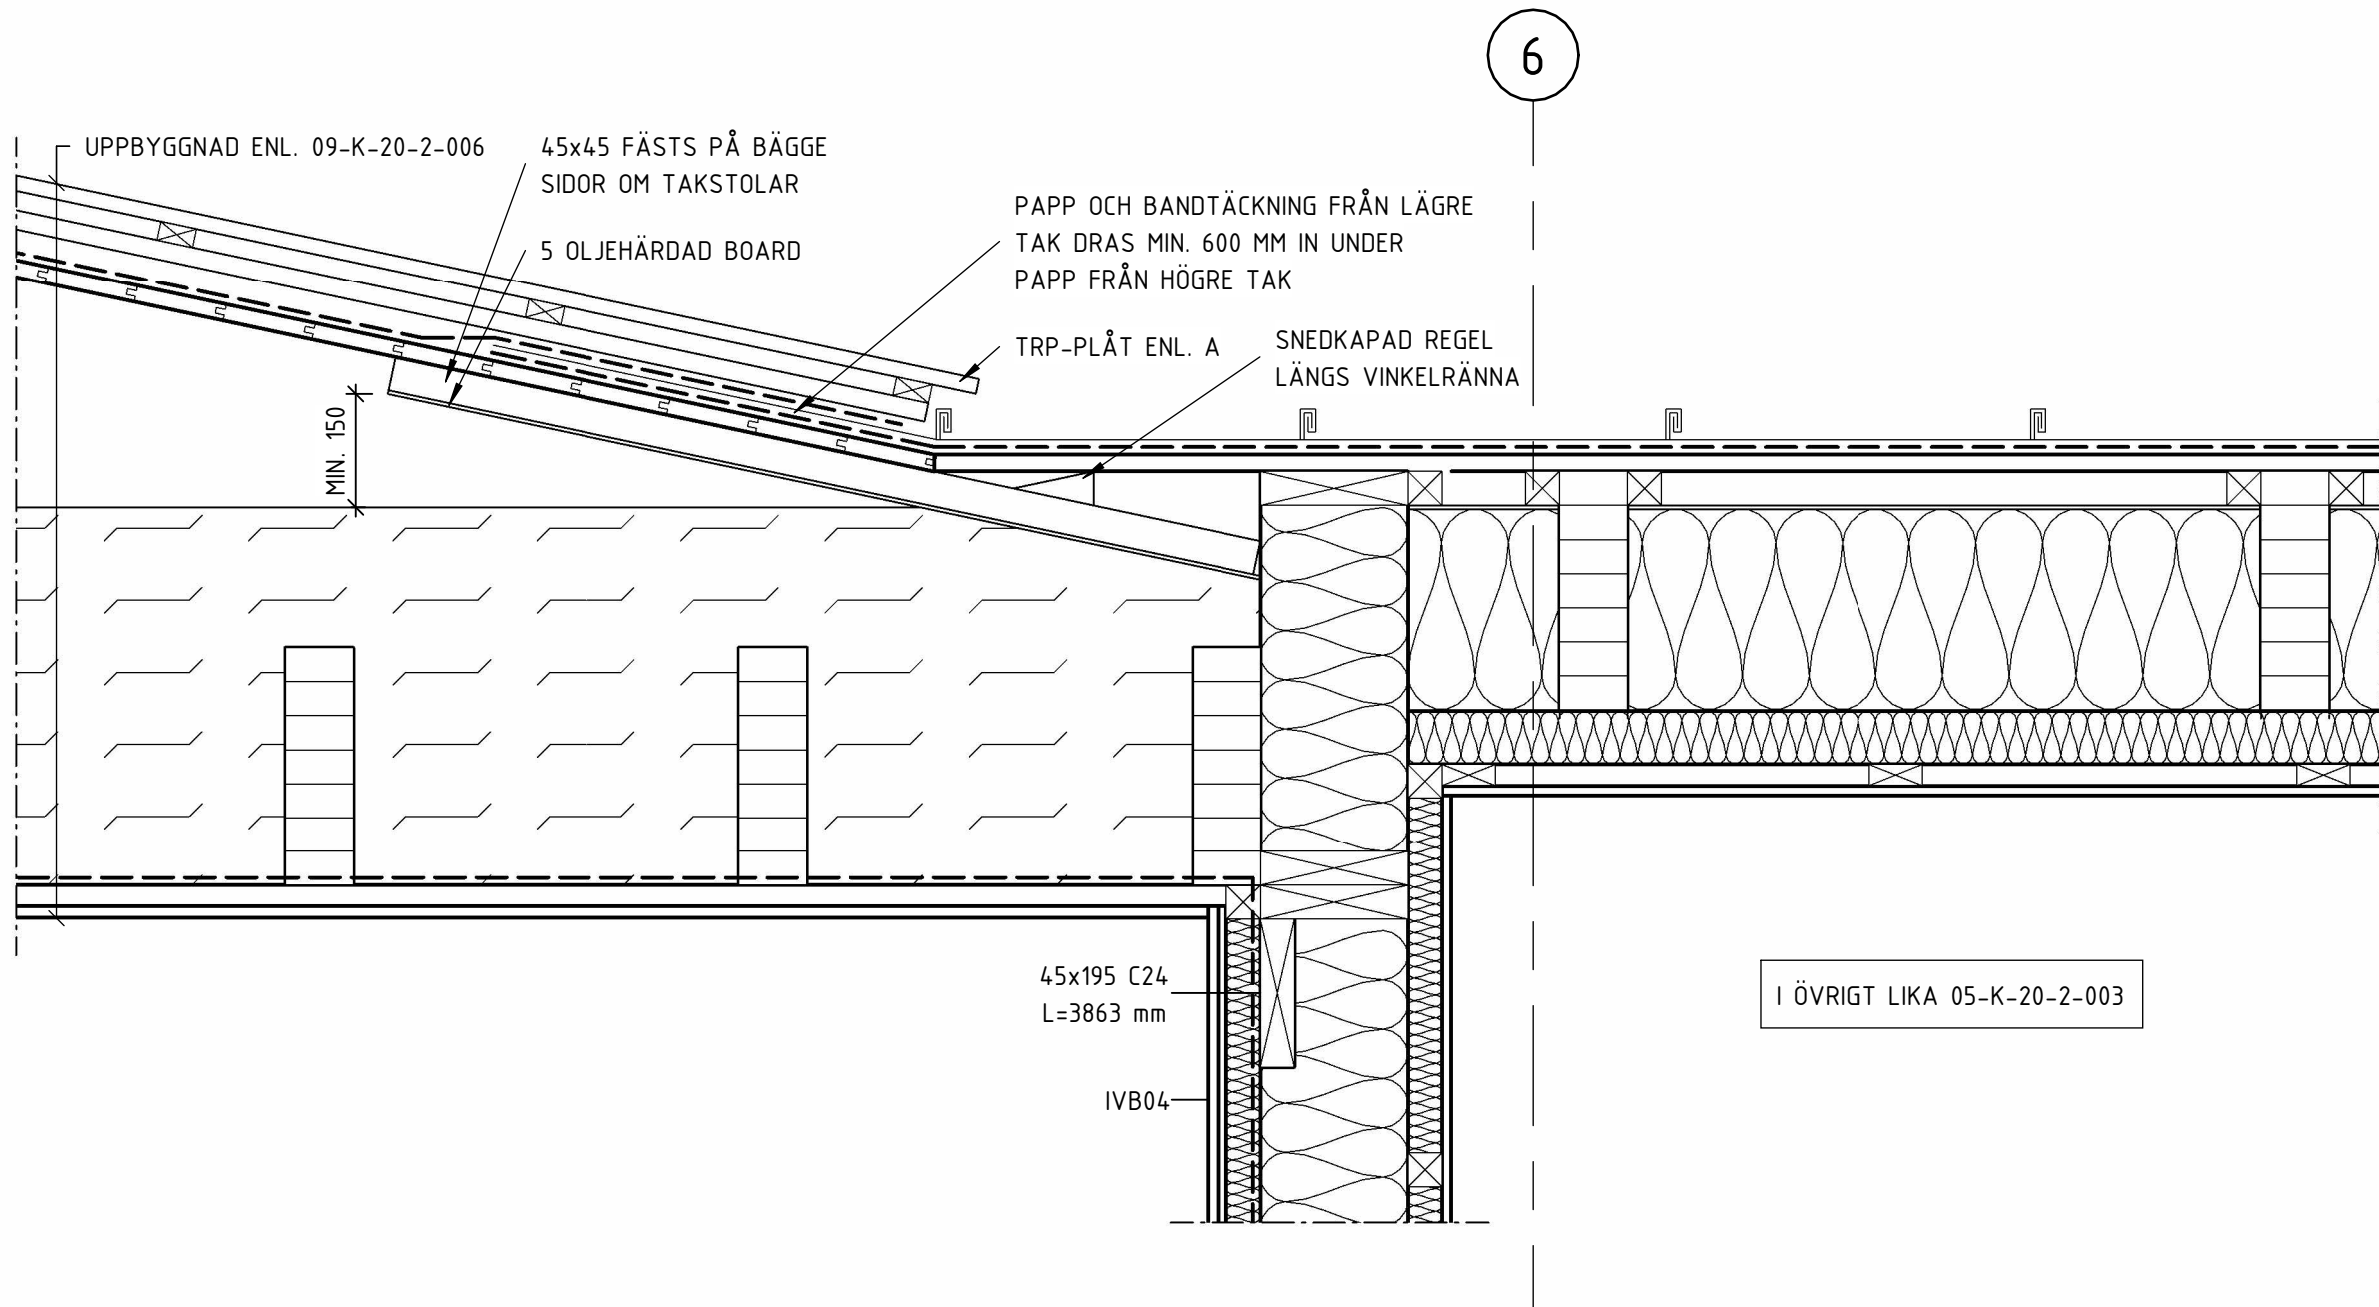


06
1 : 10
AVFALLSRUM

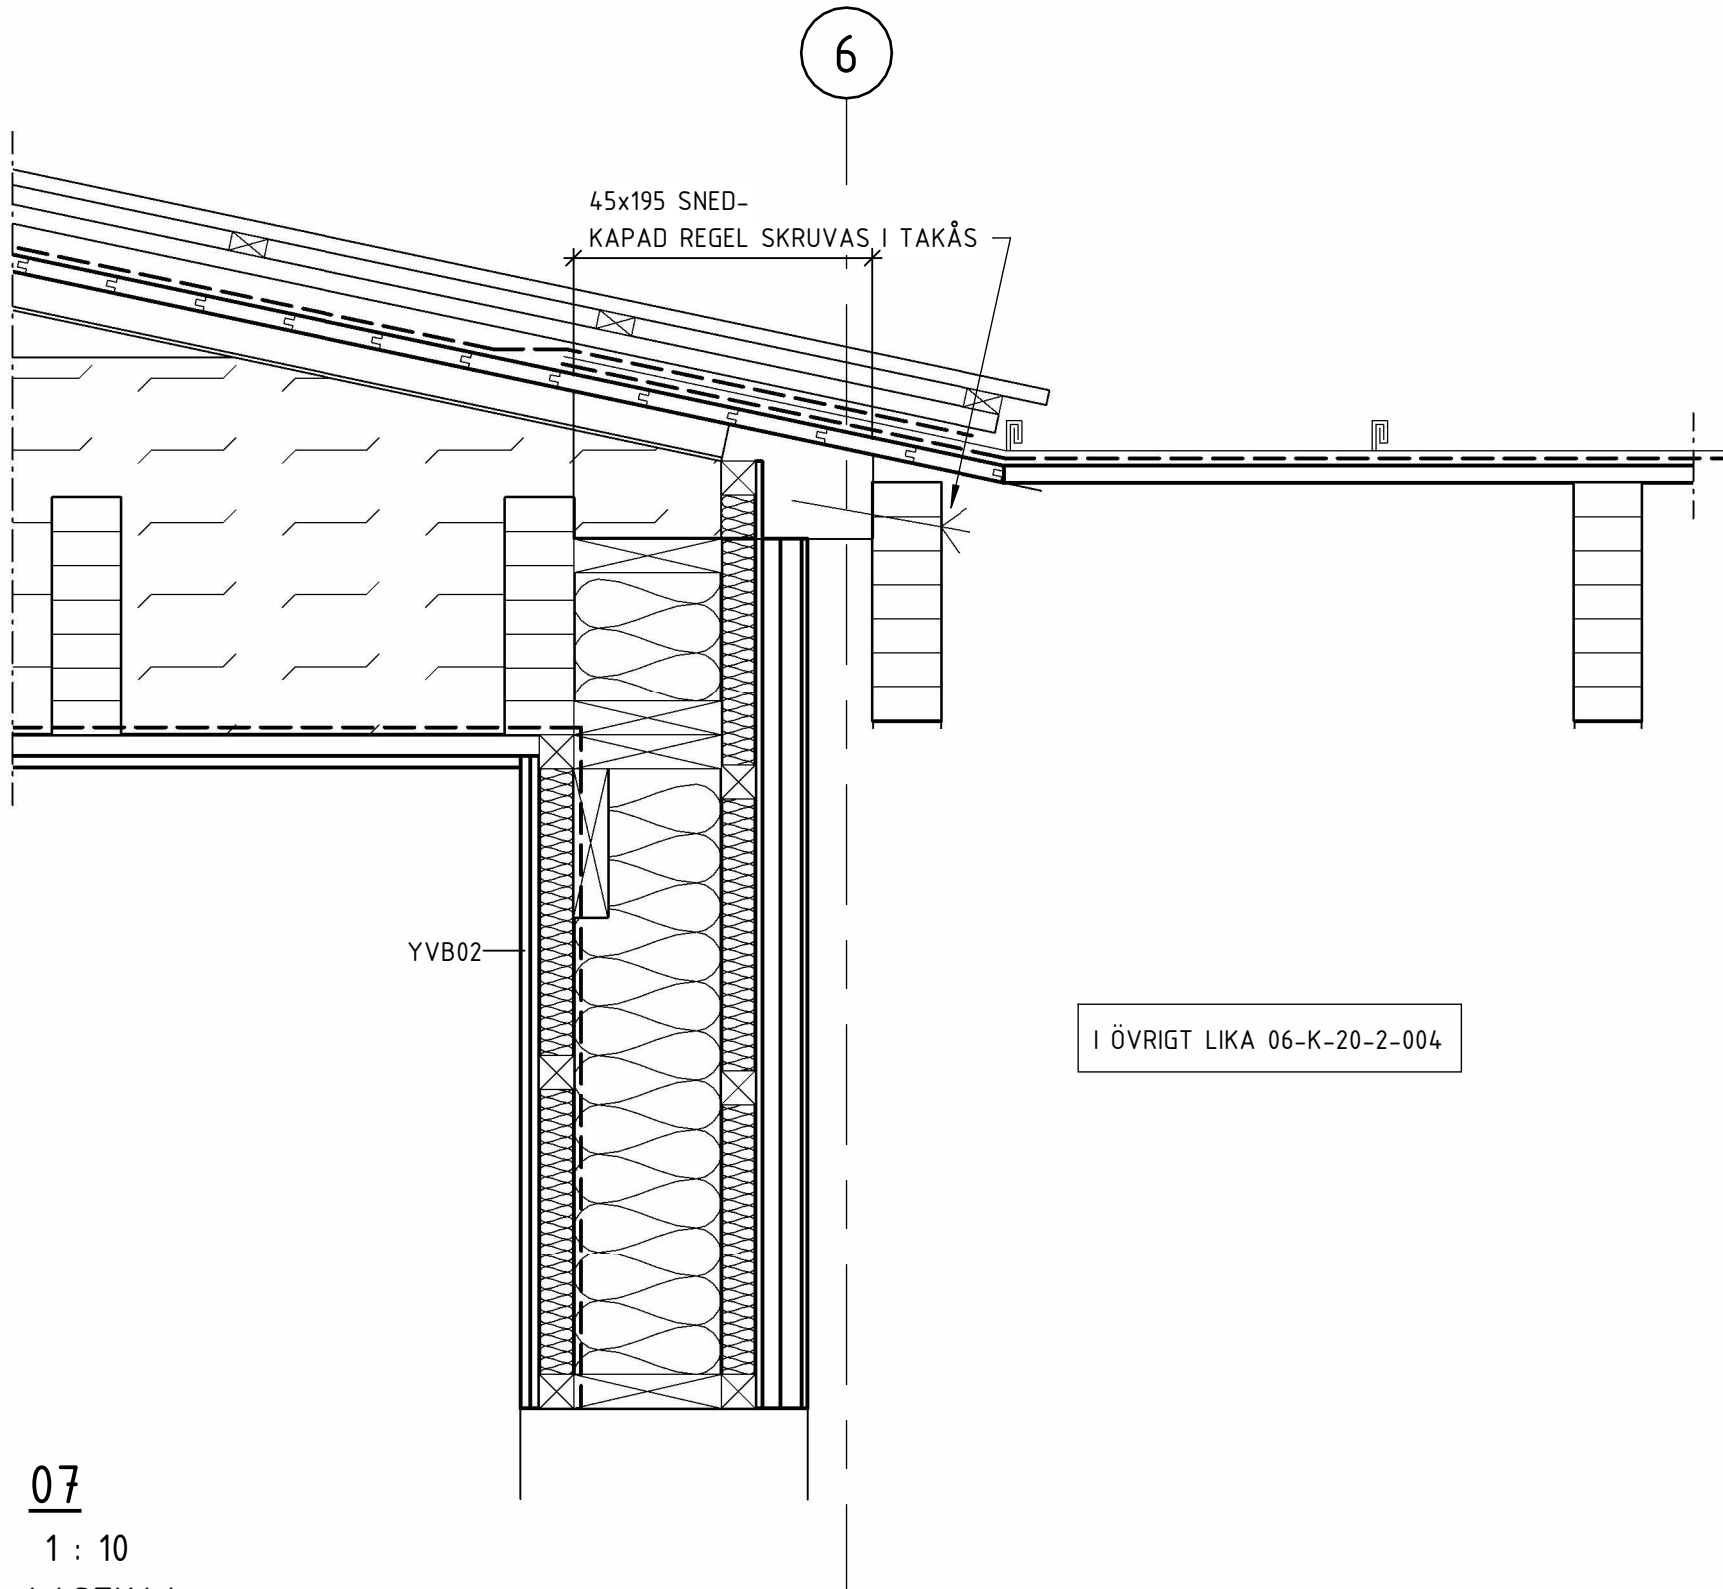

07
1 : 10
LASTKAJ



FÖRKLARINGAR

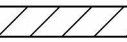 BEFINTLIG BYGGNAD

PILMÅTT TAS FRÅN NÄRMAST LIGGANDE STOMLINJE (MINST 1 METER)

INNERDÖRRAR OCH FÖNSTER VISAS ENDAST SCHEMATISKT I SAMTLIGA K-HANDLINGAR. FÖR EXAKT PLACERING OCH MÄTTSÄTTNING, SE A-HANDLINGAR.

DUBBLA VÄGGREGLAR PLACERAS PÅ RESPEKTIVE SIDA OM SAMTLIGA DÖRRAR OCH FÖNSTER OM EJ ANNAT ANGES.

FÖRESKRIFTER

K-01-0-001 -- 003 ALLMÄNNA FÖRESKRIFTER

HÄNVISNINGAR

-

SEKTION

ORIENTERINGSGRUPP

STATUS

HANDLING

DATUM

ADRESS

ÄNDRINGS FM

BESTÄLLARE

PROJEKTNAMN

OMRÅDE

PROJEKTNUMMER

FASTIGHET

DISCIPLIN

UPPDRAGSRUMMER

TELEFON

BYGGGASTVÄRDE

VÄNINGSPLAN

VÄNINGSDEL

SYSTEM

SPECIFIKATION

SEKTION

SKALA

FORMAT

DOCUMENTNUMMER



ROBERTSFORS
KOMMUN

CENTRALEKÖ

ROBERTSFORS KOMMUN

108 83 71

YTTRE RINGVÄGEN 4

K

NORCONSULT SVERIGE AB

108 83 71

AWG/ATN

010-141 80 00

BJÖRN LIDSTRÖM

+45,540 (FG)

DEL 4, 5

20 SAMMANSATTA KONSTRUKTIONER

SEKTIONER

SEKTION

1:10

A1

K-20-2-004