

FÖRKLARINGAR

BEFINTLIG BYGGNAD

PILMÅTT TAS FRÅN NÄRMAST LIGGANDE STOMLINJE (MINST 1 METER)

INNERDÖRRAR OCH FÖNSTER VISAS ENDAST SCHEMATISKT I SAMTLIGA K-HANDLINGAR. FÖR EXAKT PLACERING OCH MÄTTSÄTTNING, SE A-HANDLINGAR.


DUBBLA VÄGGREGLAR PLACERAS PÅ RESPEKTIVE SIDA OM SAMTLIGA DÖRRAR OCH FÖNSTER OM EJ ANNAT ANGES.

FÖRESKRIFTER

K-01-0-001 -- 003 ALLMÄNNA FÖRESKRIFTER

HÄNVISNINGAR

-

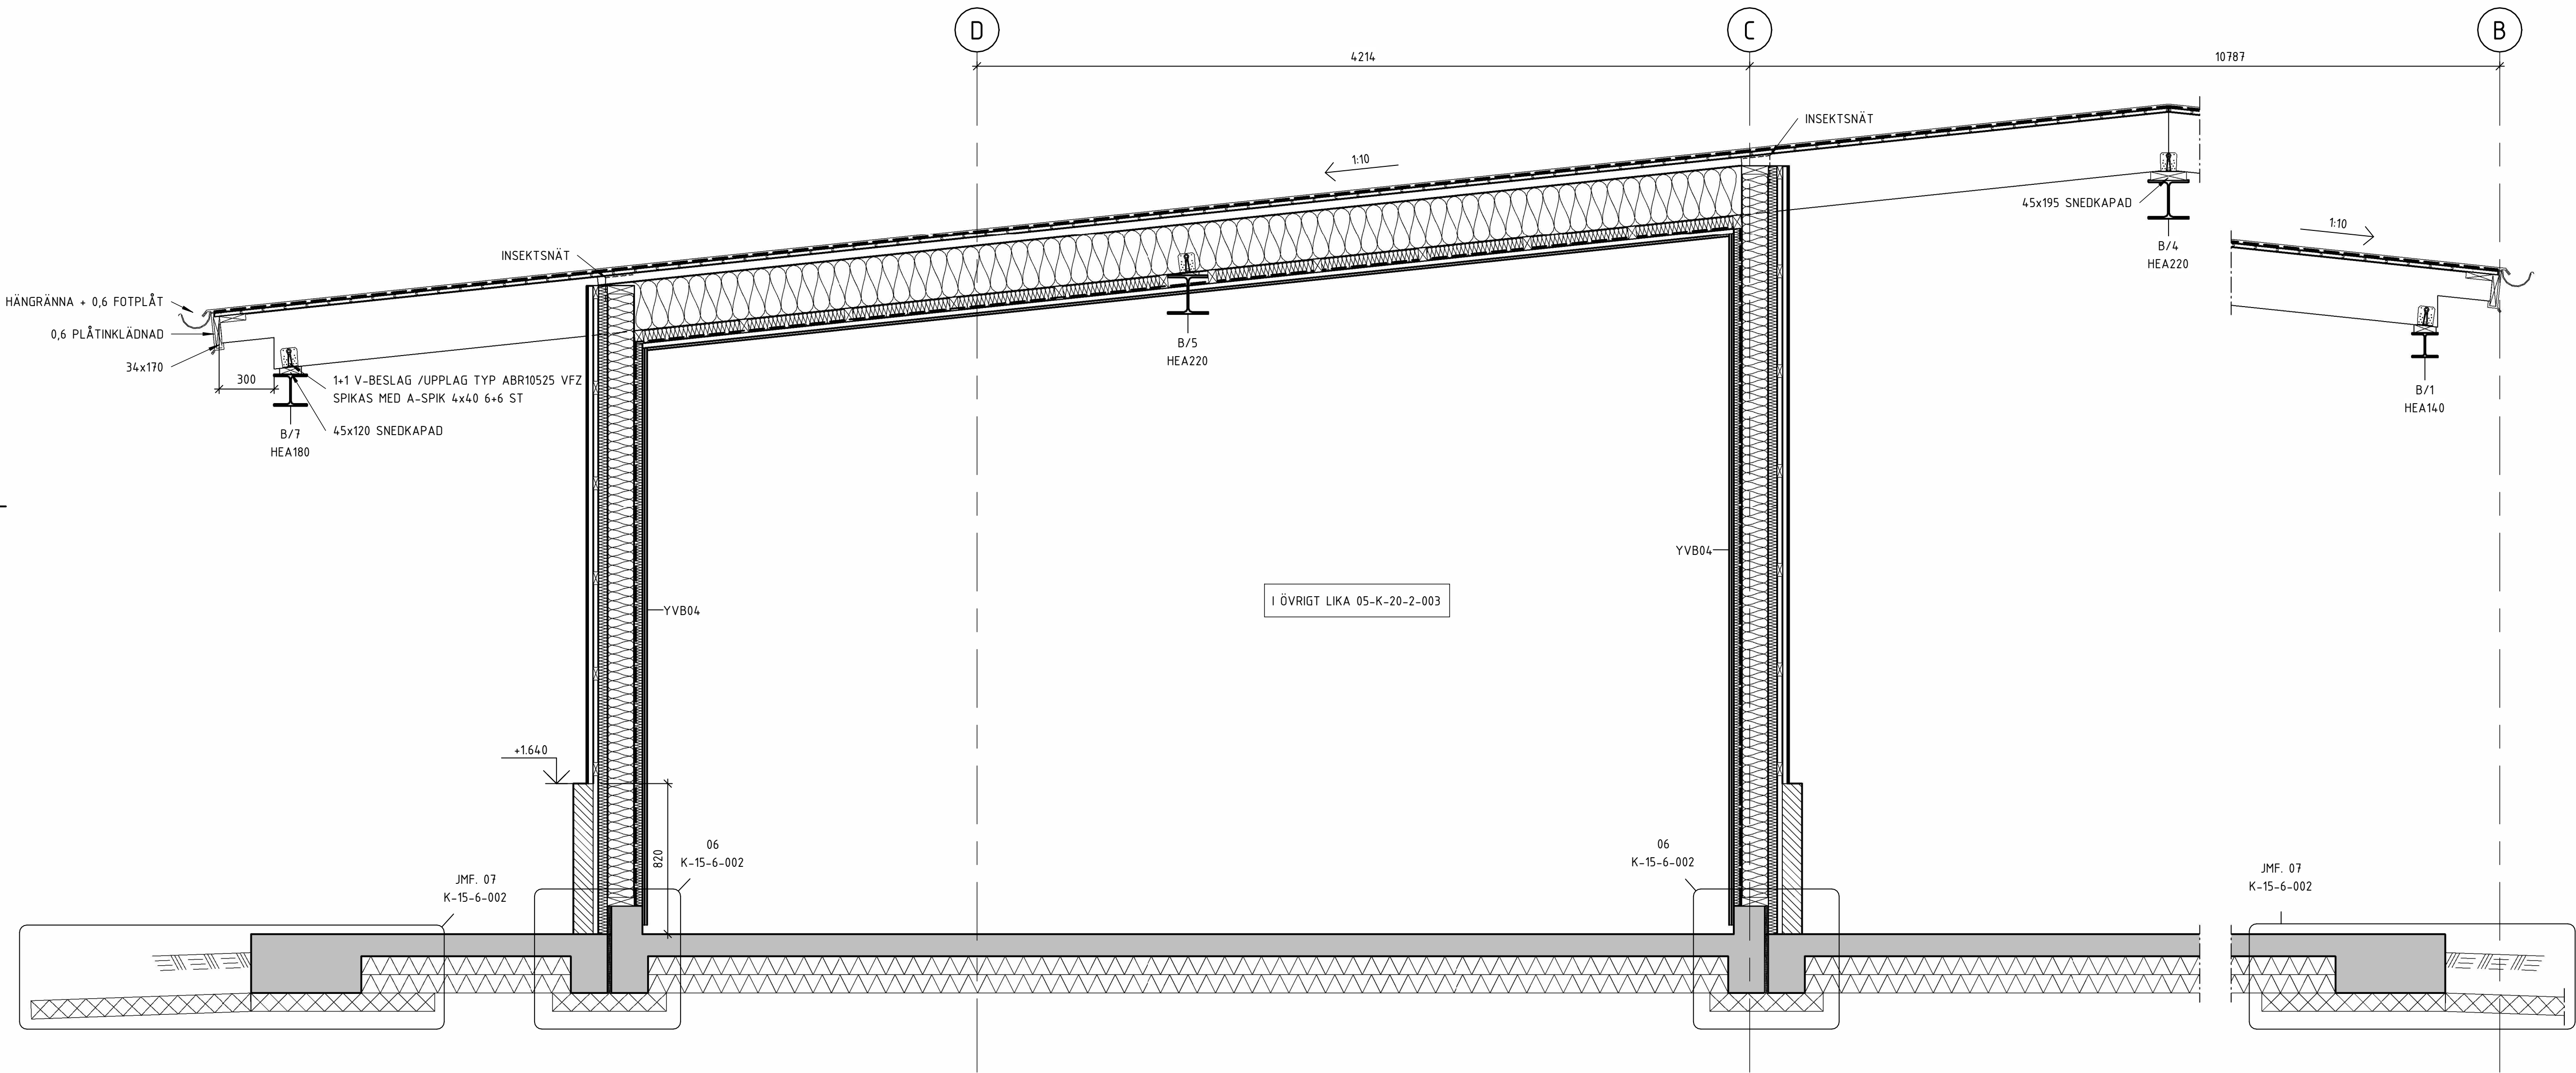

08
1 : 20
LASTKAJ

SEKTION

ORIENTERINGSSKISS

STATUS

HANDLING

ANTAG

BEFÄLL

PROJEKTNAMN

OMRÅDE

PROJEKTNUMMER

DISCIPLIN

UPPDRAGSRUMMER

TELEFON

BYGGNADSTYP

YV

SYSTEM

SPECIFIKATION

SEKTION

SEKTION

SEKTION

DEL 7

DEL 2

DEL 1

DEL 3

DEL 4

DEL 5

DEL 6

FÖRFRÅGNINGSUNDERLAG

BYGGHANDLING

2024-12-20

BJÖRN LIDSTRÖM

ANDRINGS PM

ROBERTSFORS

KOMMUN

CENTRALEKÖ

ROBERTSFORS KOMMUN

108 83 71

YTTRE RINGVÄGEN 4

FORDONET 1

NORCONSULT SVERIGE AB

AWG/ATN

010-141 80 00

BJÖRN LIDSTRÖM

+45,540 (FG)

DEL 4, 5

20 SAMMANSATTA KONSTRUKTIONER

SEKTIONER

SEKTION

SEKTION

SEKTION