

FÖRKLARINGAR

BEFINTLIG BYGGNAD

PILMÅTT TAS FRÅN NÄRMAST LIGGANDE STOMLINJE (MINST 1 METER)

INNERDÖRRAR OCH FÖNSTER VISAS ENDAST SCHEMATISKT I SAMTLIGA K-HANDLINGAR. FÖR EXAKT PLACERING OCH MÄTTSÄTTNING, SE A-HANDLINGAR.


DUBBLA VÄGGREGLAR PLACERAS PÅ RESPEKTIVE SIDA OM SAMTLIGA DÖRRAR OCH FÖNSTER OM EJ ANNAT ANGES.

FÖRESKRIFTER

K-01-0-001 -- 003 ALLMÄNNA FÖRESKRIFTER

HÄNVISNINGAR

-

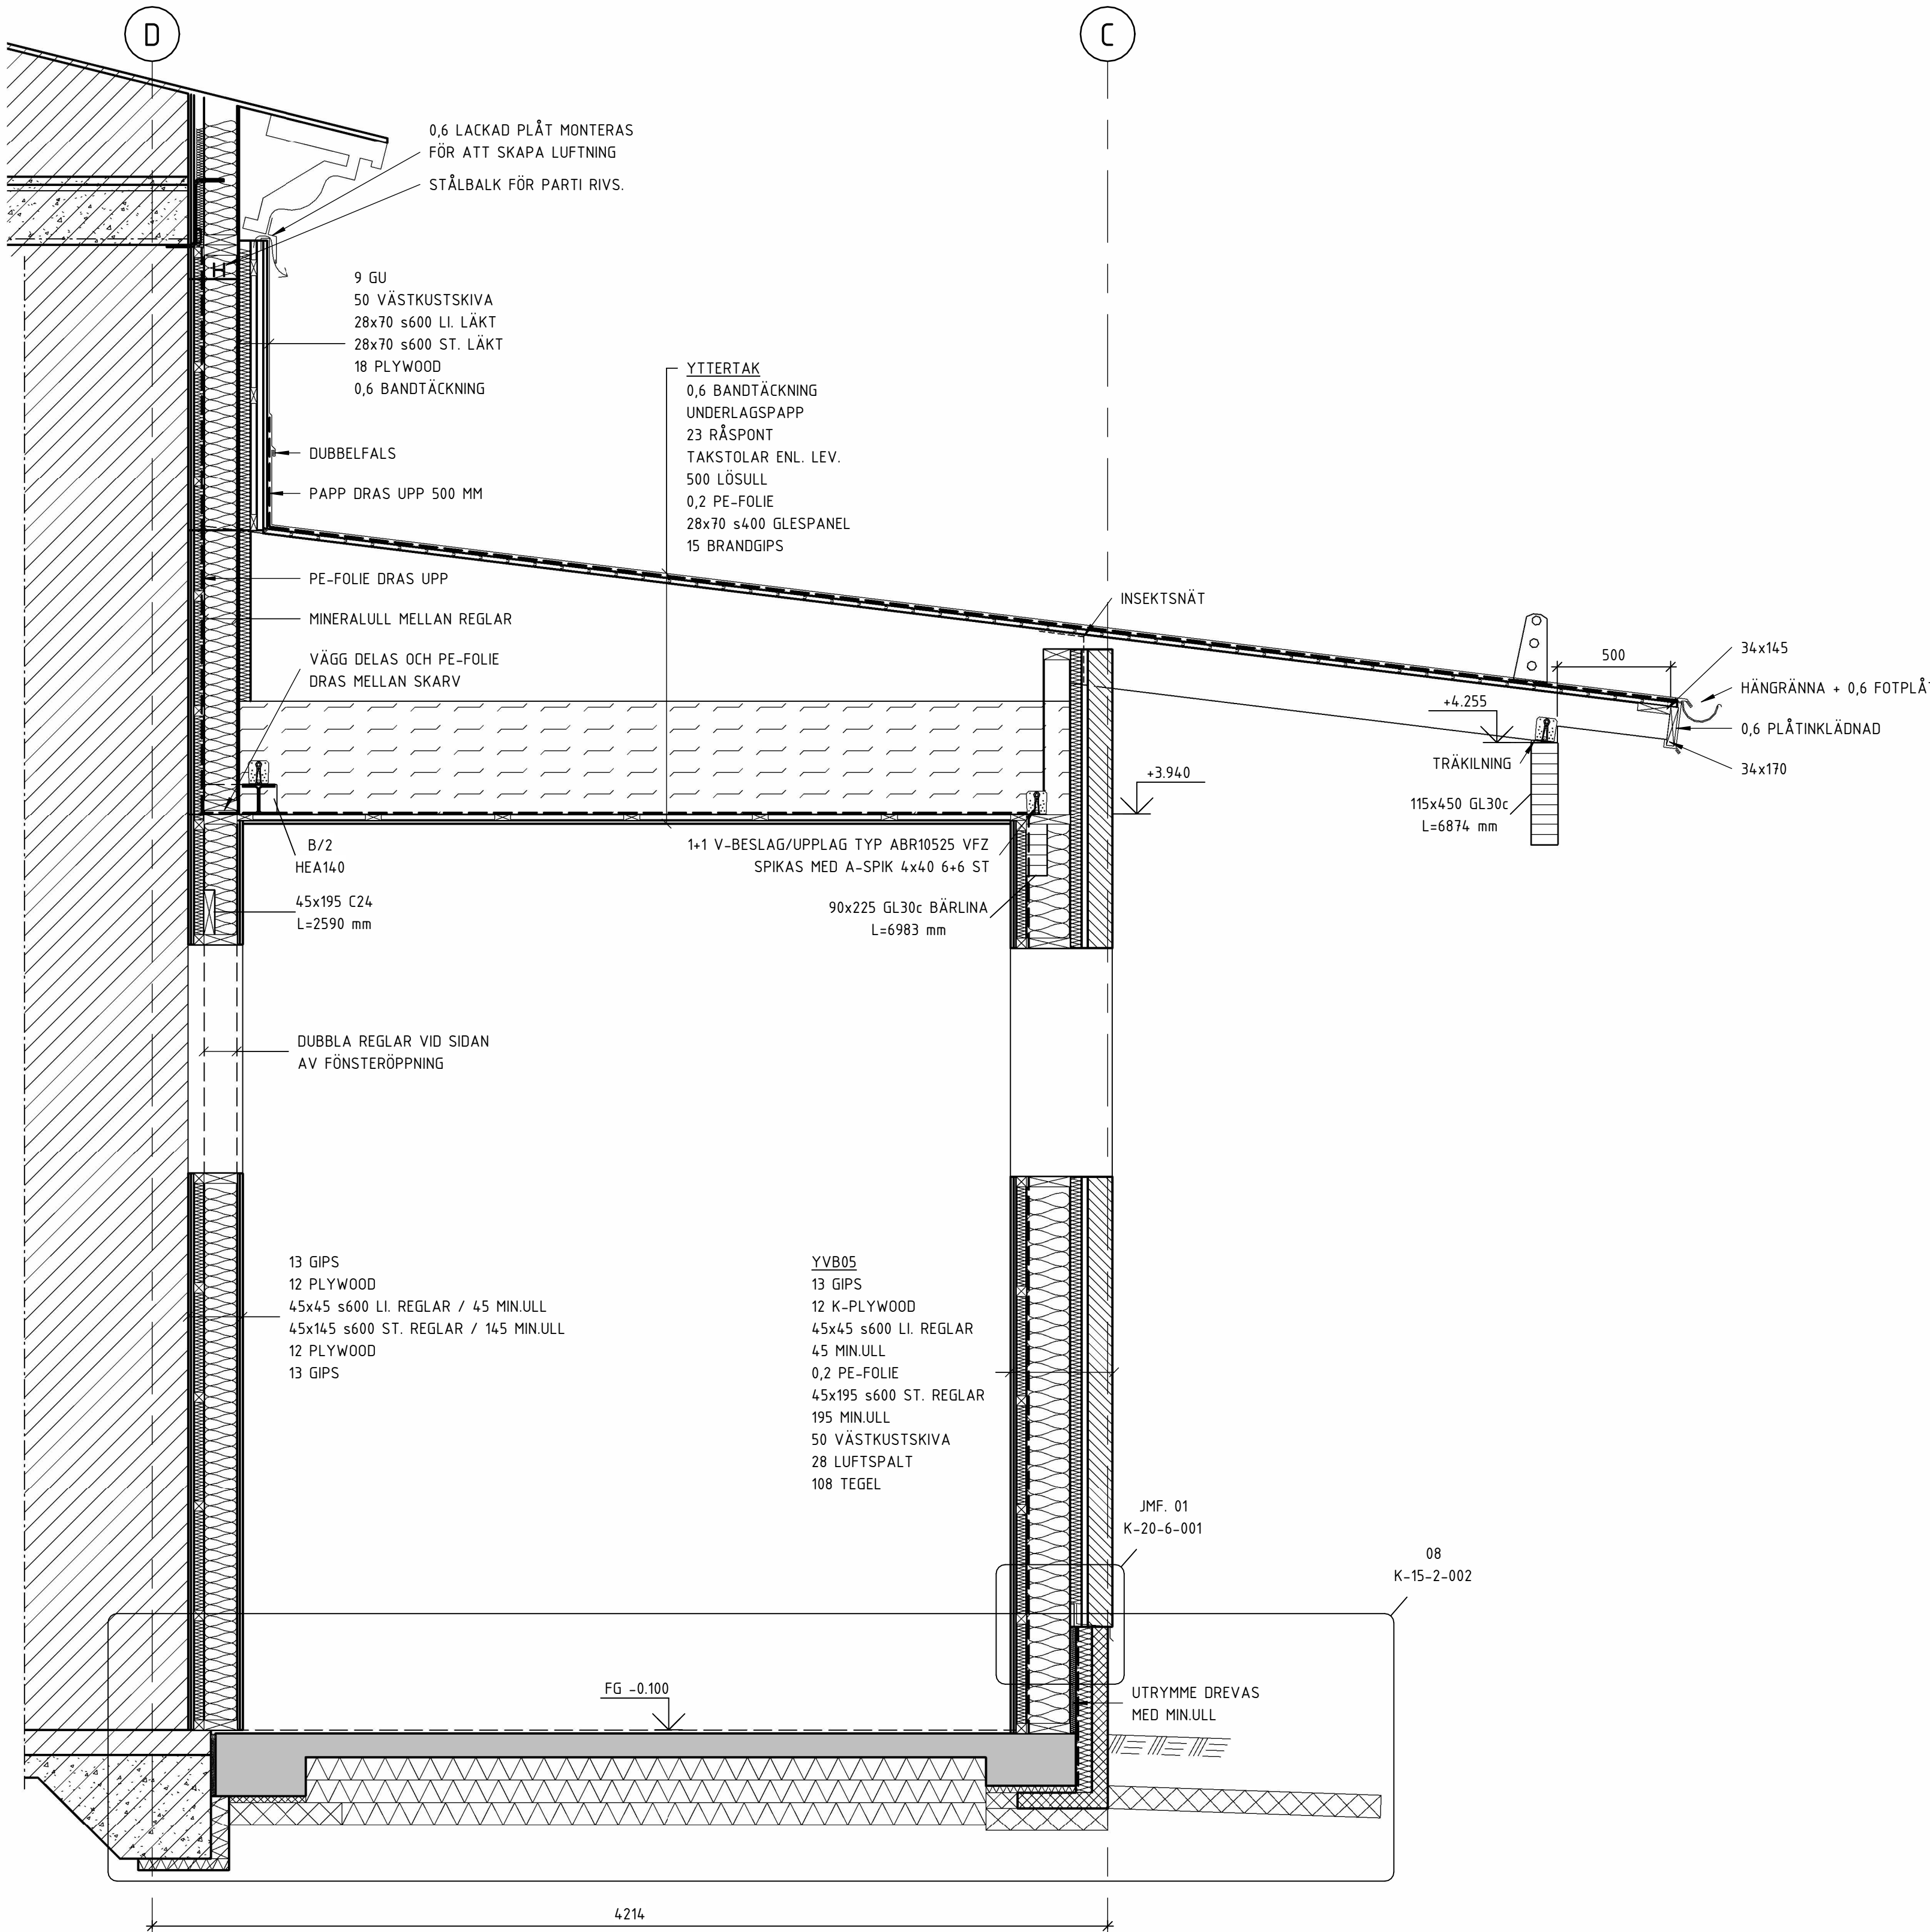

20
1 : 20
ENTRÉ

SKALA 1:20 0 1 2 METER

SEKTION		
ORIENTERINGSFIGUR		
STATUS		
FÖRFRÅGNINGSUNDERLAG		
HANDLING		
BYGGHANDLING		
DATUM	2024-12-20	ANSÖKAN
ANSÖKAN	BJÖRN LIDSTRÖM	ANSÖKAN
BESTÄLLARE		
 ROBERTSFORS KOMMUN		
PROJEKTNAMN		
CENTRALEKÖ		
OBJEKT		
ROBERTSFORS KOMMUN		
PROJEKTNUMMER	108 83 71	YTTRE RINGVÄGEN 4
DIREKTÖR	FASTIGHET	FORDONET 1
DIREKTÖR	FÖRETAG	NORCONSULT SVERIGE AB
UPPDRAGSNUMMER	108 83 71	AWG/ATN
TELEFON	010-141 80 00	BJÖRN LIDSTRÖM
BYGGNADSTYRELSE	FÖLJESAMTÄLLNING	+45,540 (FG)
VÄNNSBIL	DELNING	DEL 4, 5
SYSTEM		
20 SAMMANSÄTTA KONSTRUKTIONER		
SEKTIONER		
SEKTION	SKALA 1:20	FORMAT A1
SEKTION	SKALA 1:20	ANSÖKAN
K-20-2-007		