

FÖRKLARINGAR

BEFINTLIG BYGGNAD

PILMÅTT TAS FRÅN NÄRMAST LIGGANDE STOMLINJE (MINST 1 METER)

INNERDÖRRAR OCH FÖNSTER VISAS ENDAST SCHEMATISKT I SAMTLIGA K-HANDLINGAR. FÖR EXAKT PLACERING OCH MÄTTSÄTTNING, SE A-HANDLINGAR.


DUBBLA VÄGGREGLAR PLACERAS PÅ RESPEKTIVE SIDA OM SAMTLIGA DÖRRAR OCH FÖNSTER OM EJ ANNAT ANGES.

FÖRESKRIFTER


K-01-0-001 -- 003 ALLMÄNNA FÖRESKRIFTER

HÄNVISNINGAR

-


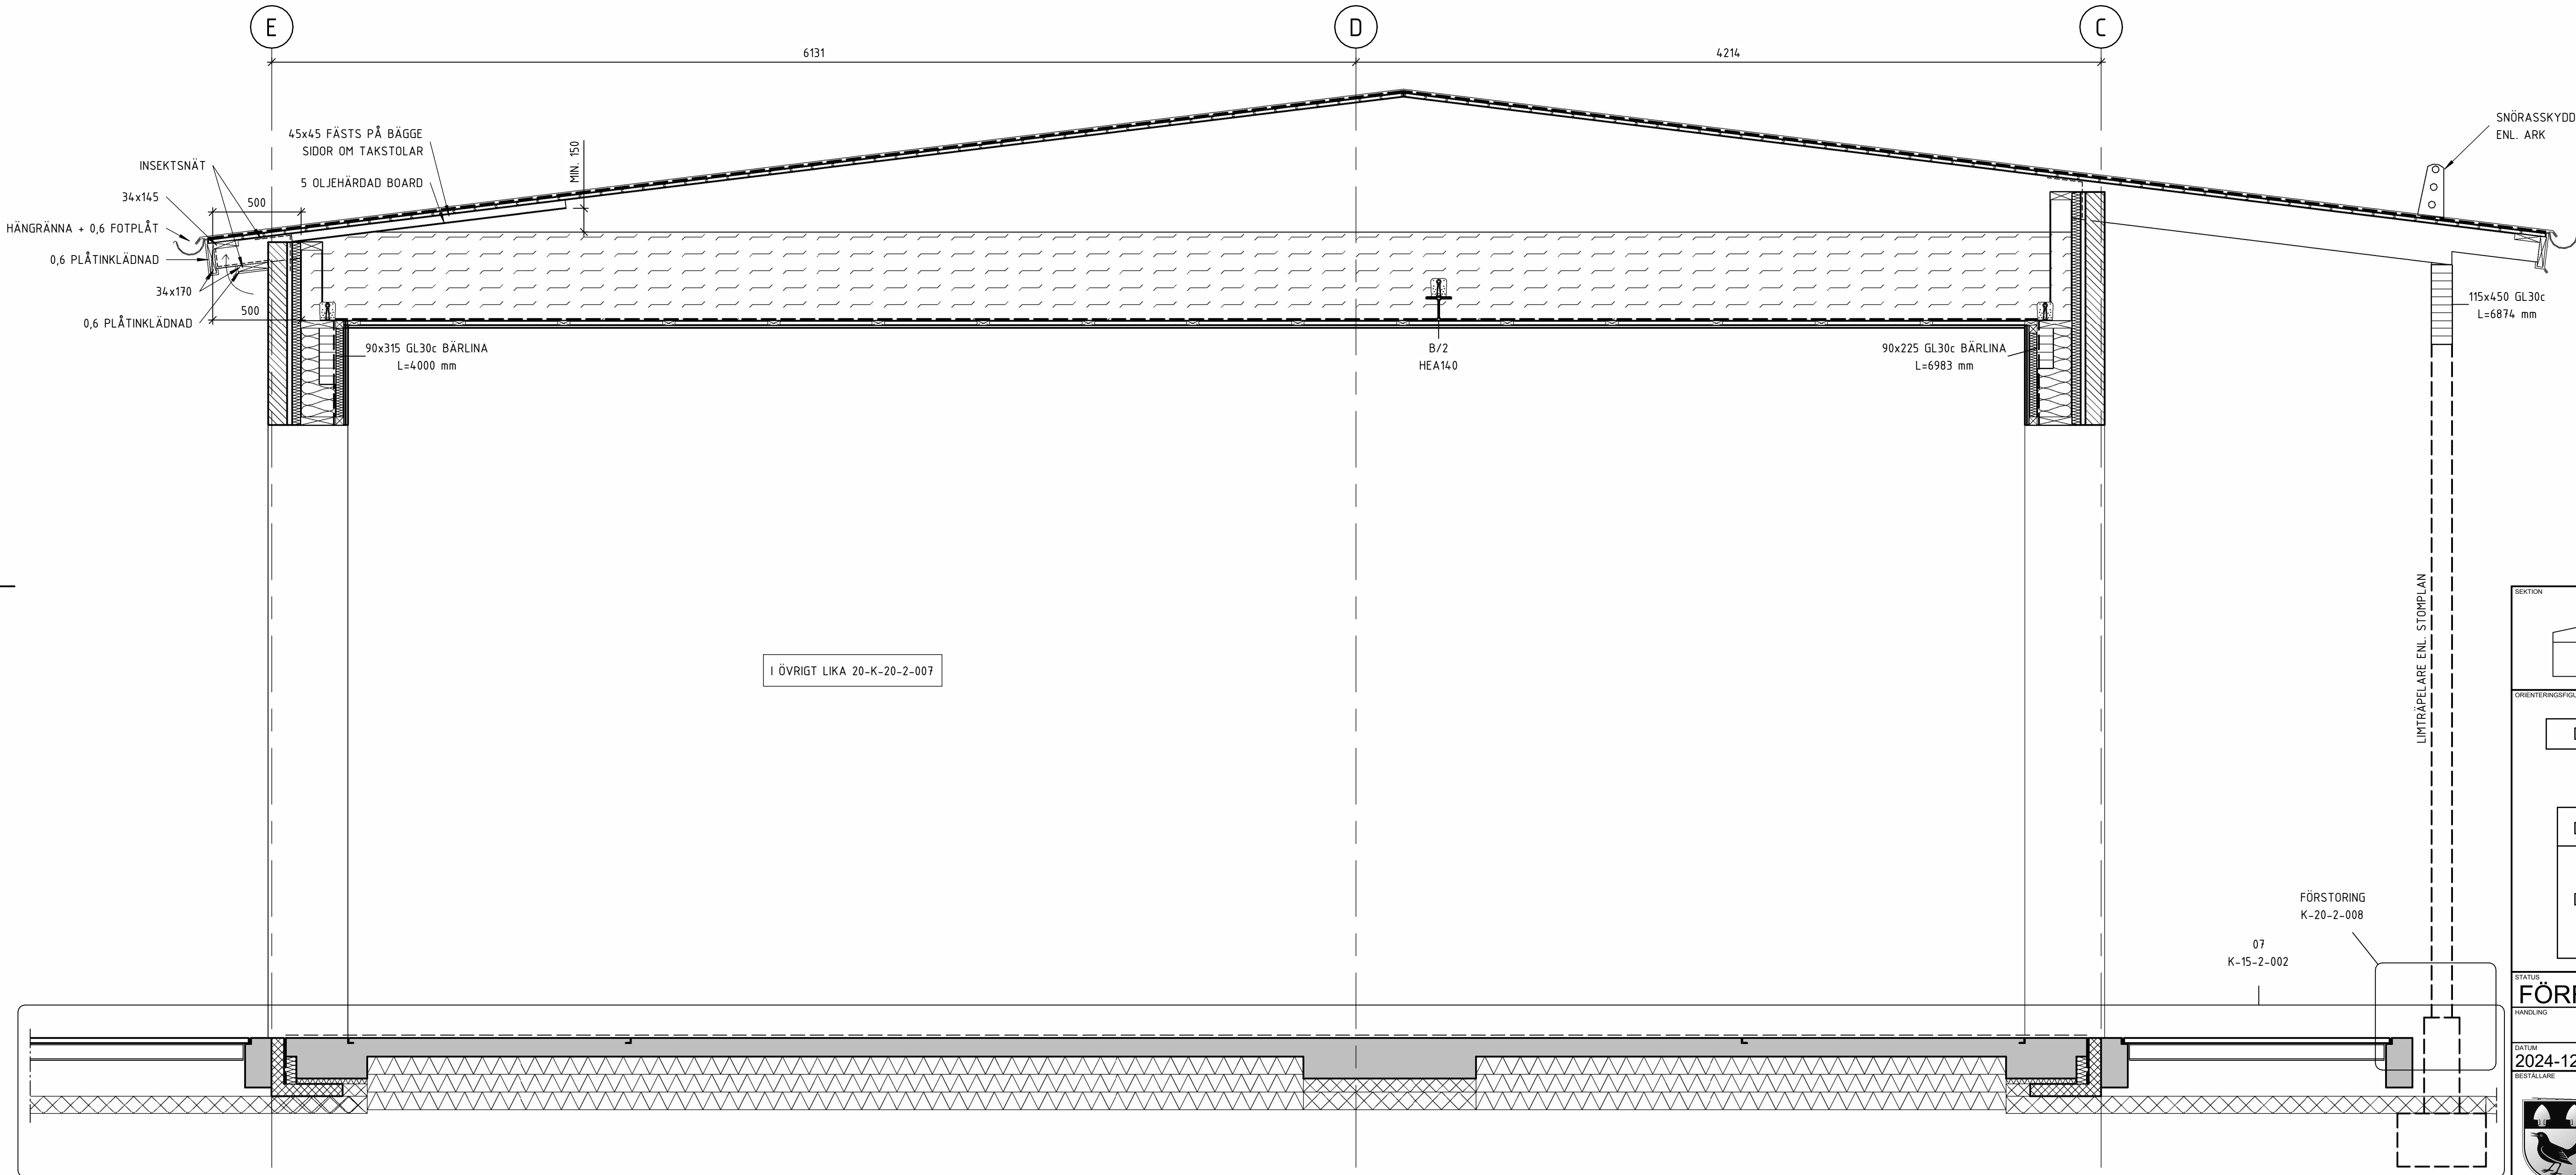


21
1 : 20
ENTRÉ

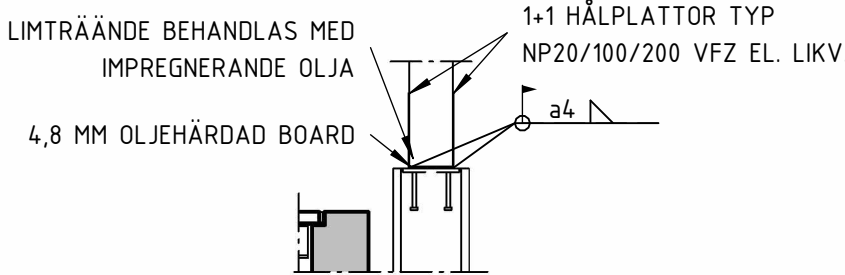

FÖRSTÖRING
1 : 20
INFÄSTNING LIMTRÄPELARE

SKALA 1:20 0 1 2 METER

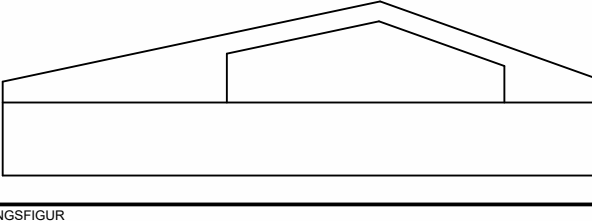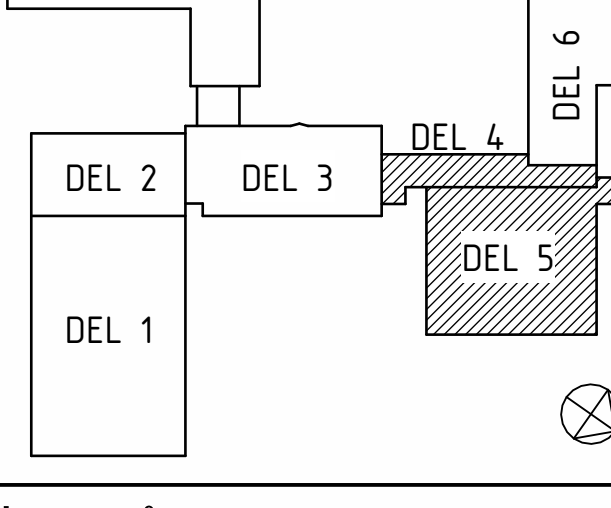		
ORIENTERINGSSKISSUR		
		
STATUS		
FÖRFRÅGNINGSUNDERLAG		
HANDLING		
BYGGHANDLING		
DATUM	2024-12-20	ÖVERSKICK AV
ANSÖKAN AV	BJÖRN LIDSTRÖM	ÄNDRINGS PM
BESTÄLLARE		
		
ROBERTSFORS KOMMUN		
PROJEKTNAMN		
CENTRALEKÖK		
OMRÅDE		
ROBERTSFORS KOMMUN		
PROJEKTNUMMER	108 83 71	YTTRE RINGVÄGEN 4
DIREKTOR	FORDONET 1	
DIREKTOR	FORDONET 1	
UPPDRAGSNUMMER	108 83 71	NORCONSULT SVERIGE AB
UPPDRAGSNUMMER	108 83 71	AWG/ATN
TELEFON	010-141 80 00	BJÖRN LIDSTRÖM
BYGGGÅRSTID	+45,540 (FG)	
VÄNINGSPLAN	VÄNINGSDEL	DEL 4, 5
SYSTEM		
20 SAMMANSATTA KONSTRUKTIONER		
SEKTIONER		
SEKTION	SKALA	FORMAT
SEKTION	1:20	A1
SEKTION	1:20	ÄNDRING
K-20-2-008		