

FÖRKLARINGAR

BEFINTLIG BYGGNAD

PILMÅTT TAS FRÅN NÄRMAST LIGGANDE STOMLINJE (MINST 1 METER)

INNERDÖRRAR OCH FÖNSTER VISAS ENDAST SCHEMATISKT I SAMTLIGA K-HANDLINGAR. FÖR EXAKT PLACERING OCH MÄTTSÄTTNING, SE A-HANDLINGAR.


DUBBLA VÄGGREGLAR PLACERAS PÅ RESPEKTIVE SIDA OM SAMTLIGA DÖRRAR OCH FÖNSTER OM EJ ANNAT ANGES.

FÖRESKRIFTER


K-01-0-001 -- 003 ALLMÄNNA FÖRESKRIFTER

HÄNVISNINGAR


-

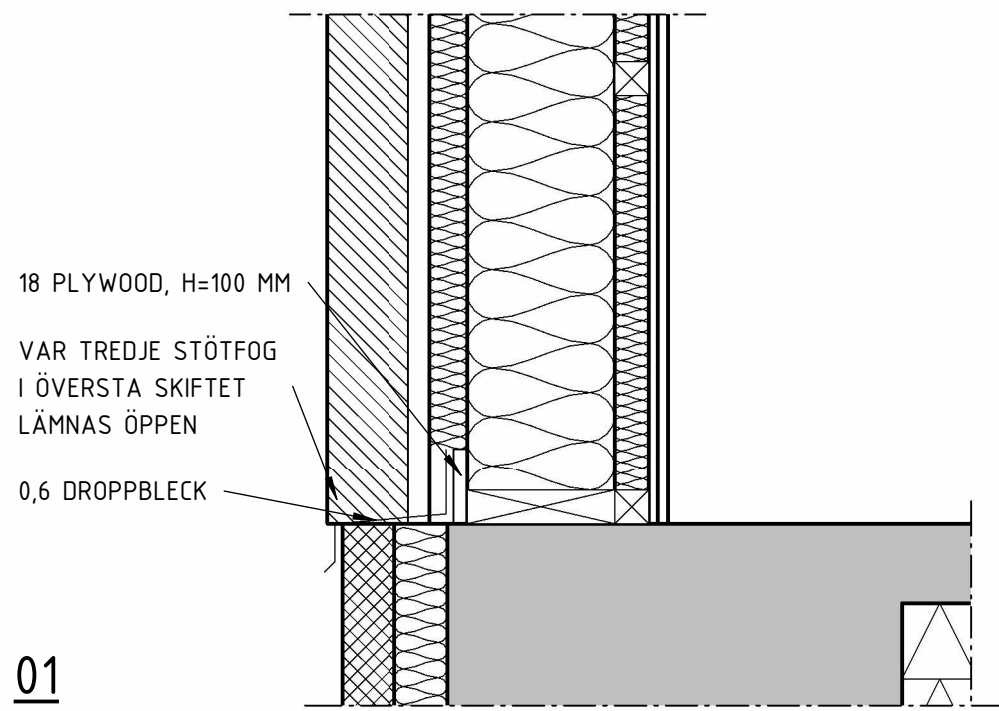


01
1 : 10
HUVUDSEKTION

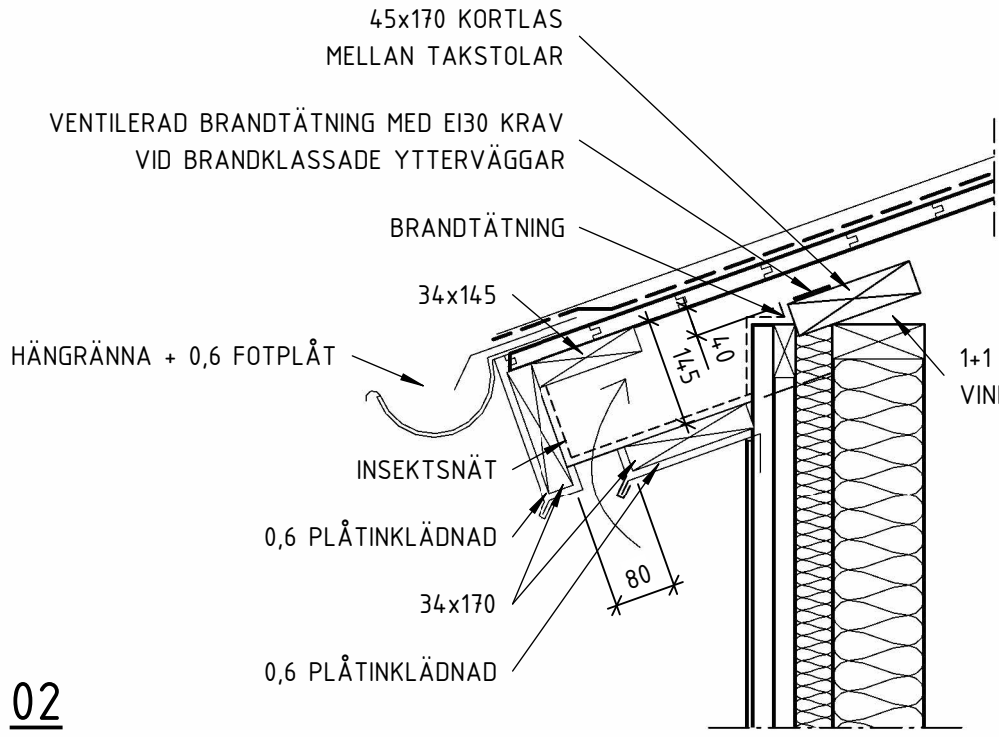


02
1 : 10
TAKFOT

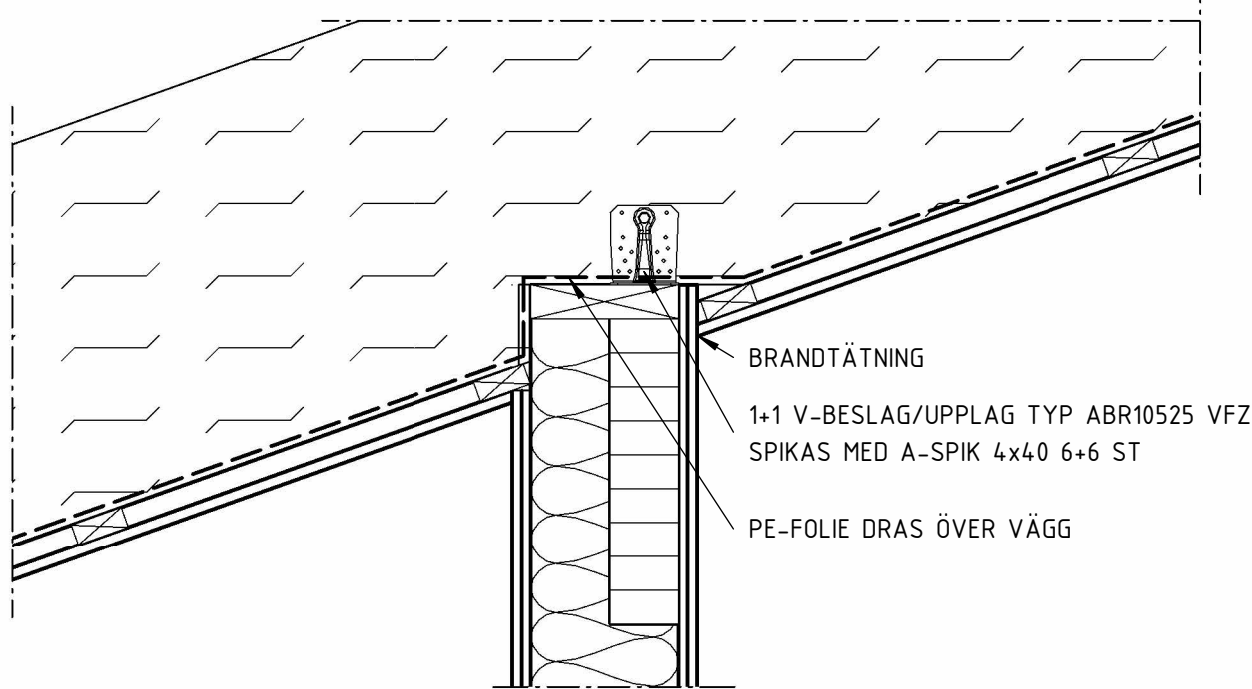


03
1 : 10
TAKSTOL PÅ FLÄKTRUMSVÄGG

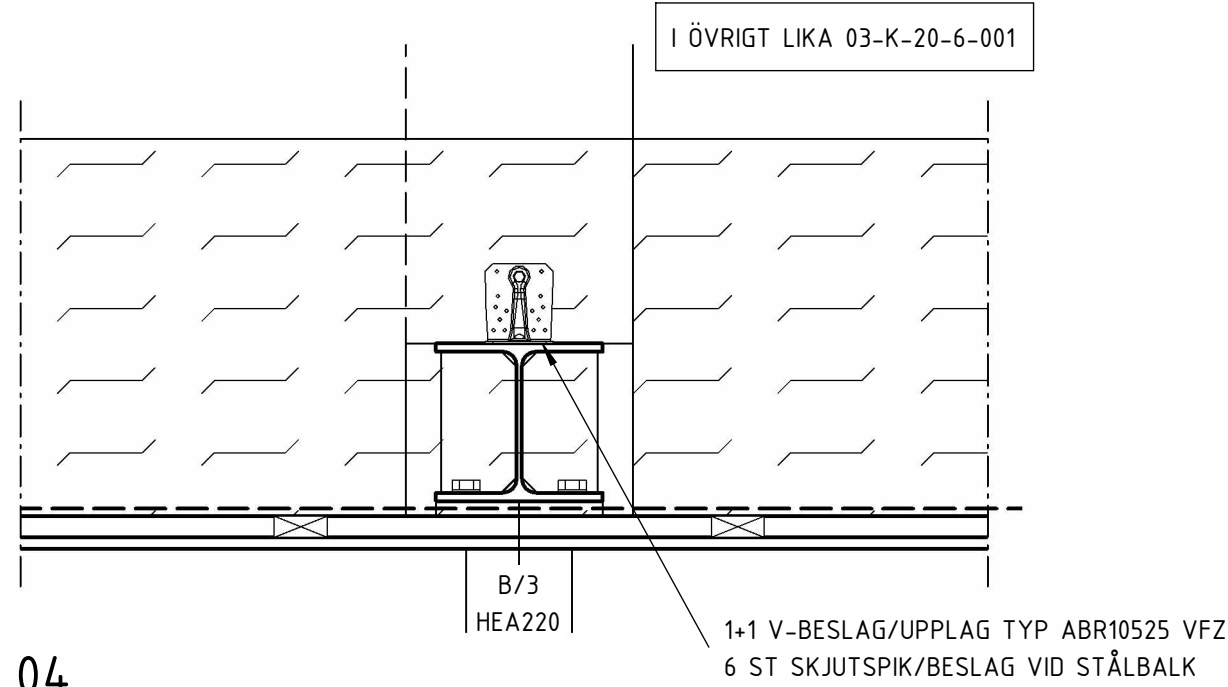


04
1 : 10
TAKSTOL PÅ STÅLBALK

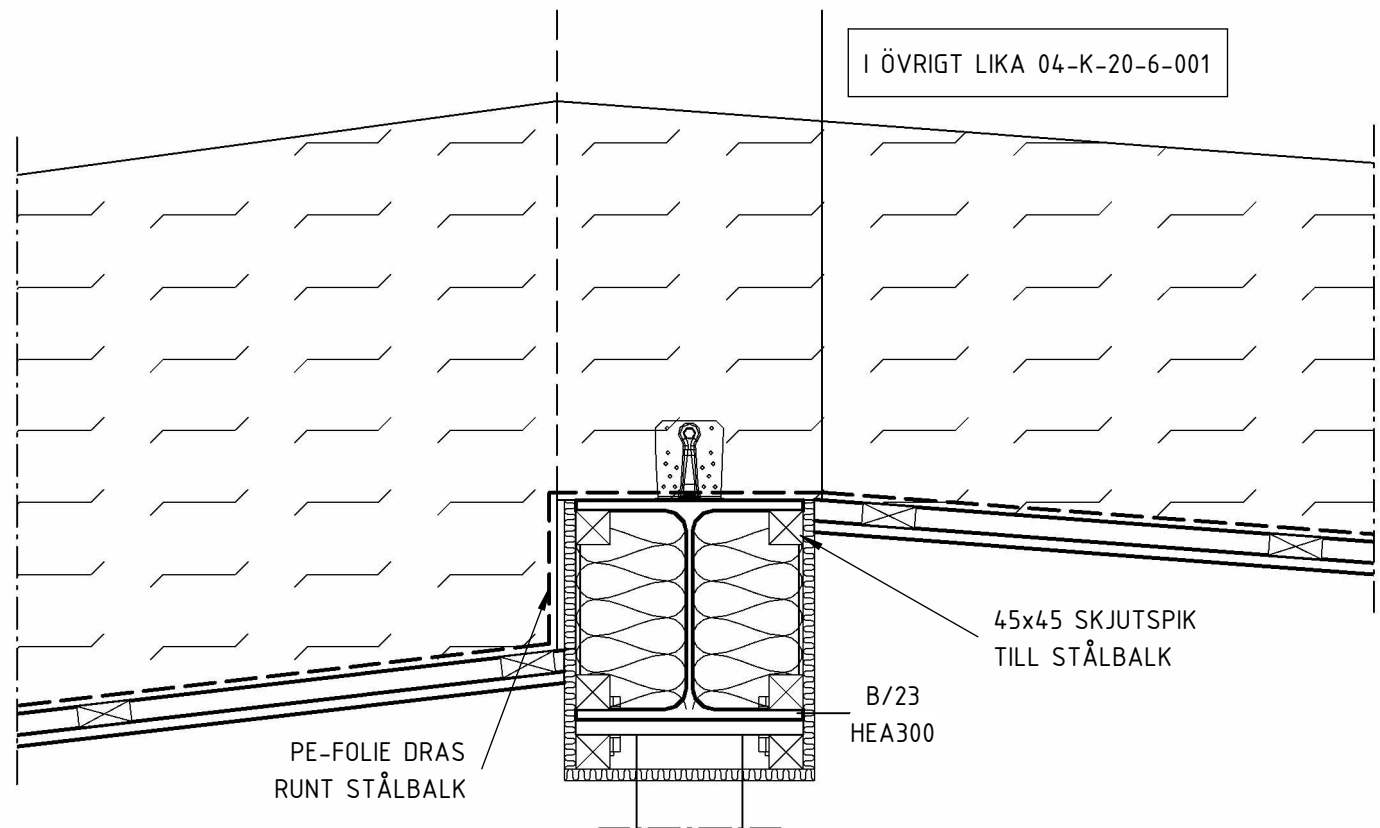


05
1 : 10
TAKSTOL PÅ STÅLBALK

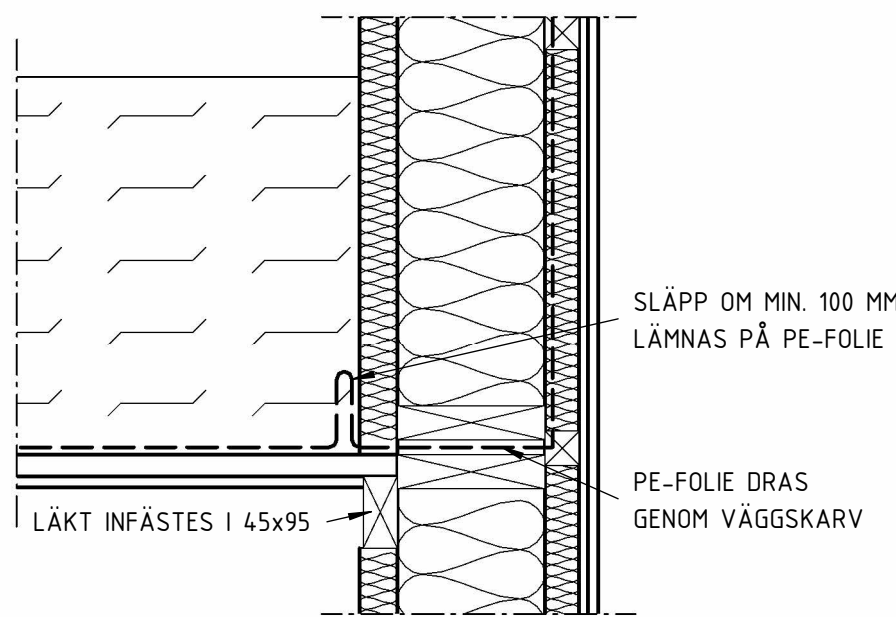


06
1 : 10
ÖVERGÅNG TAKSTOLSTYPER

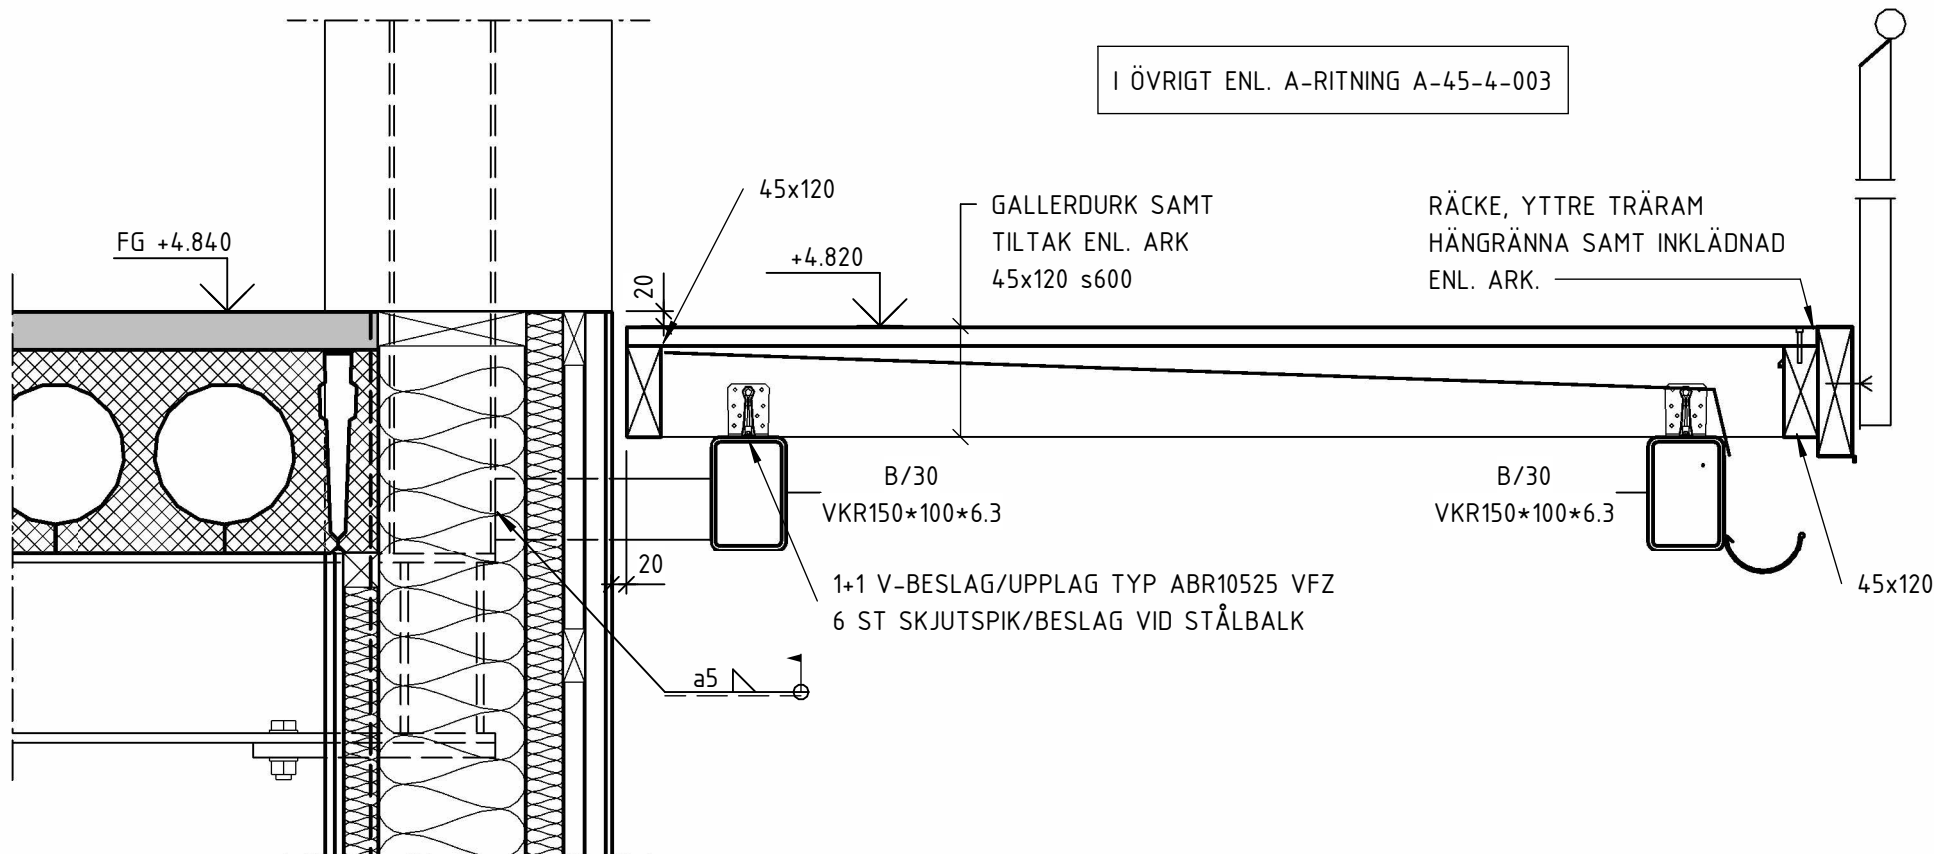


07
1 : 10
FLÄKTRUMSBALKONG TVÄR

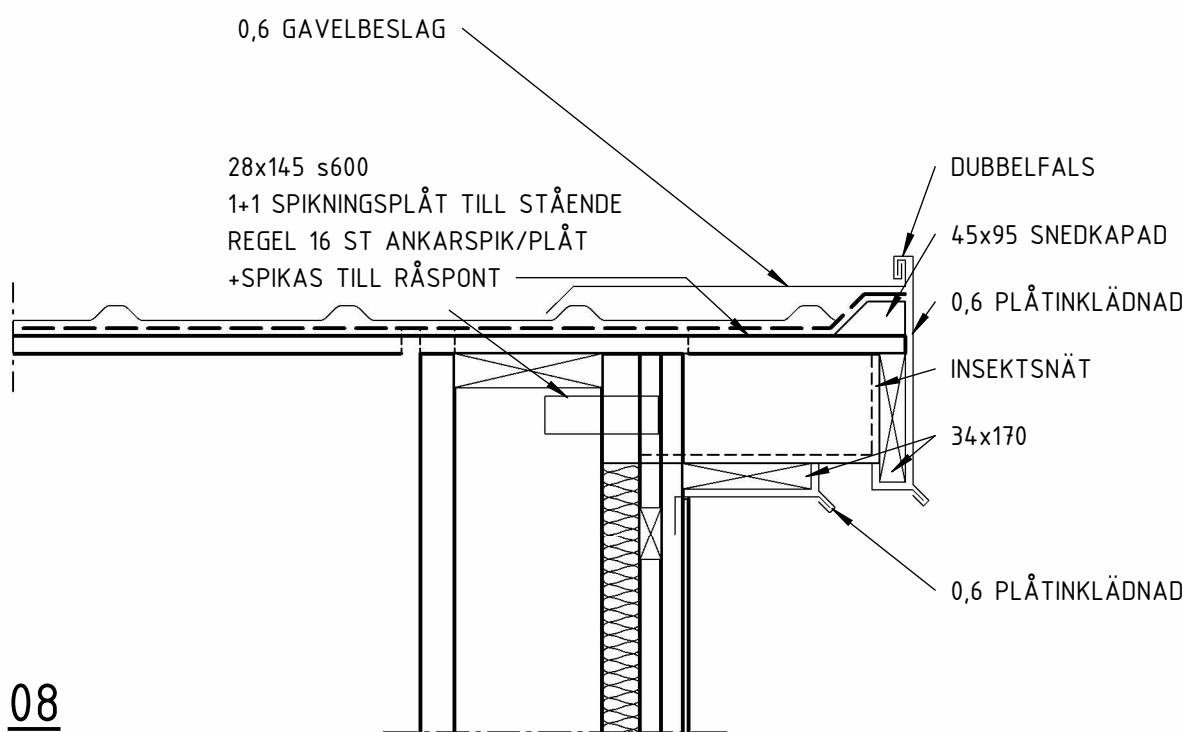


08
1 : 10
GAVEL

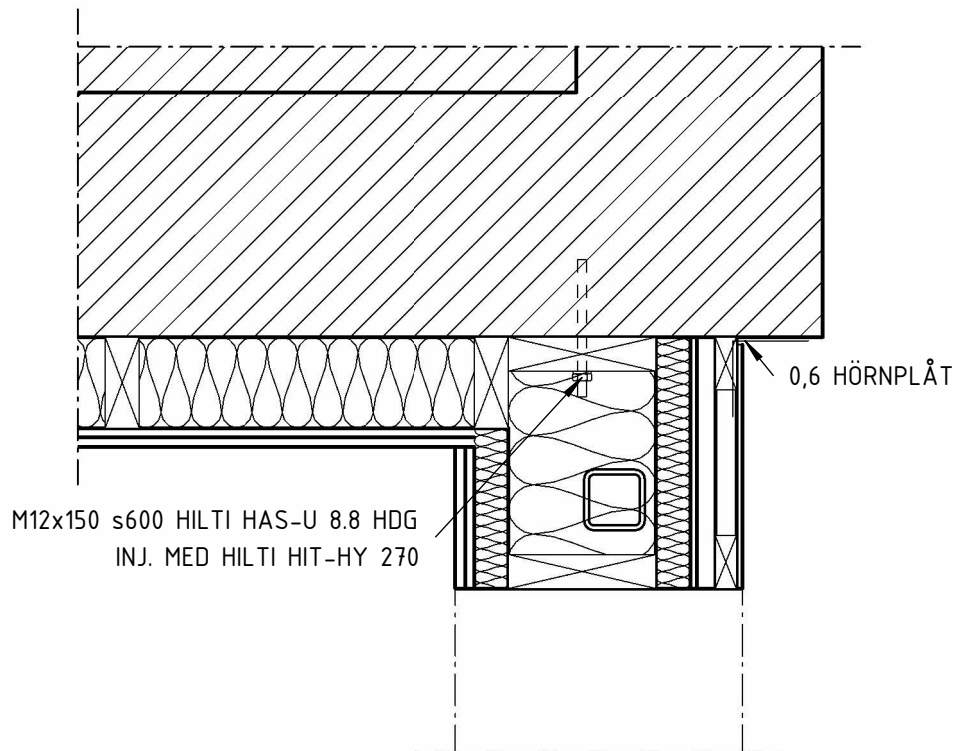


09
1 : 10
ANSLUTNING MOT BEFINTLIGT

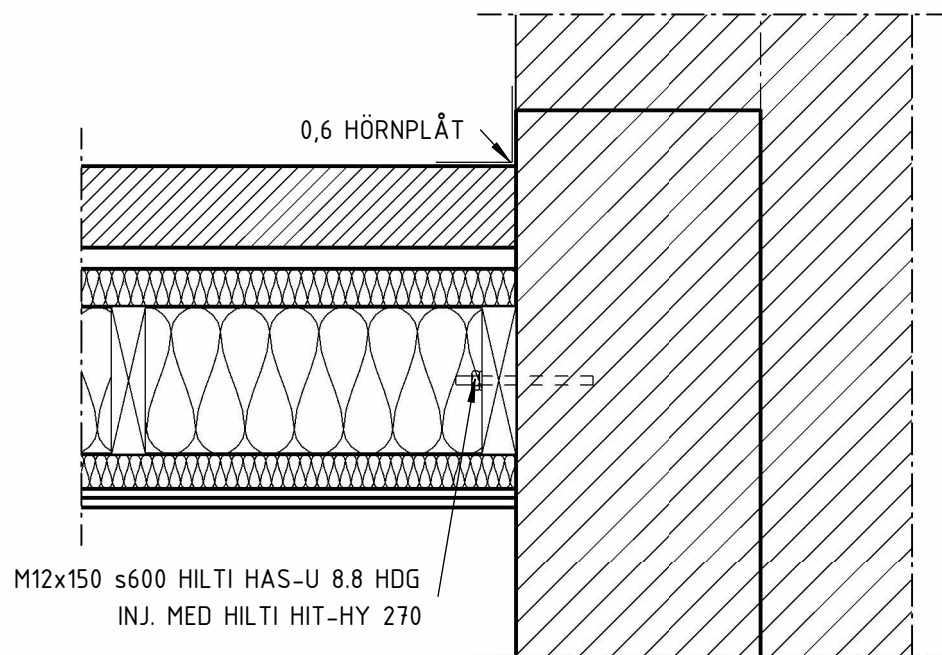

10
1 : 10
ANSLUTNING MOT BEFINTLIGT

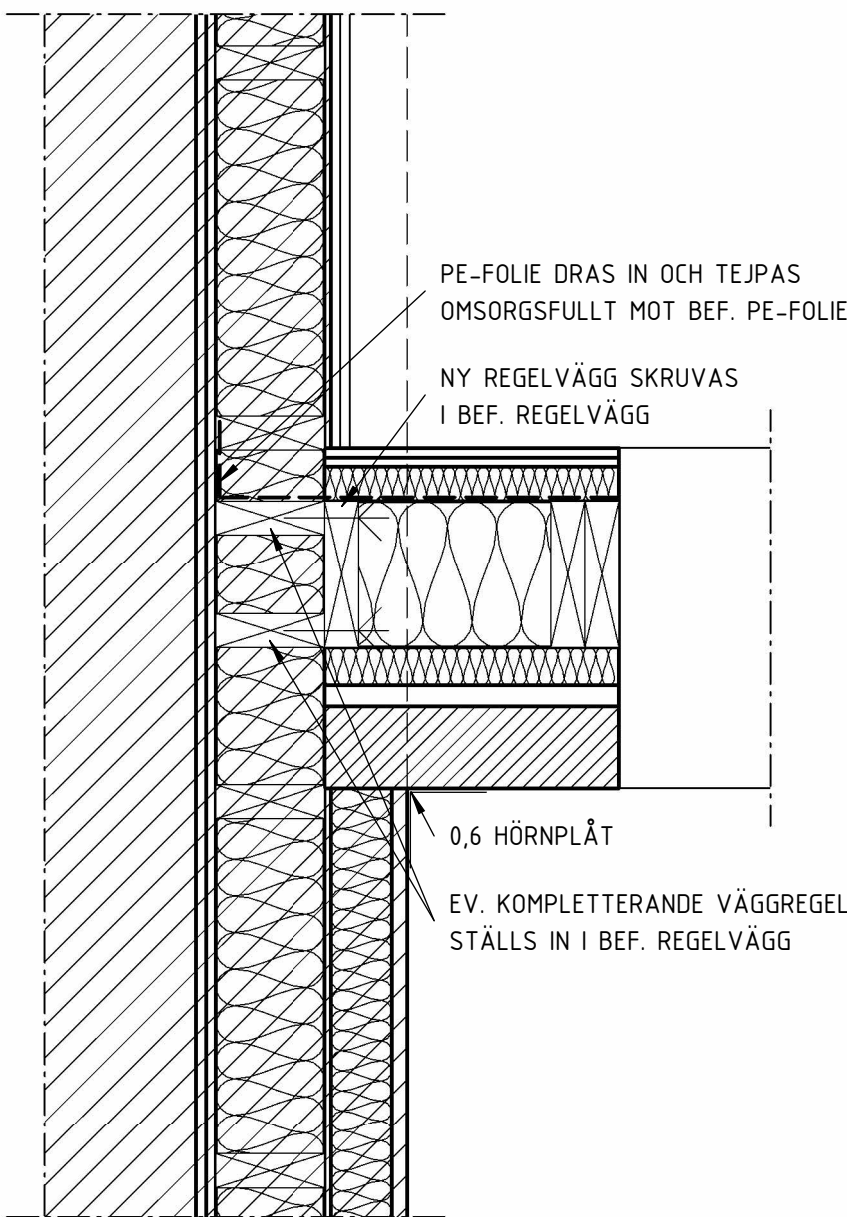

11
1 : 10
ANSLUTNING MOT BEFINTLIGT

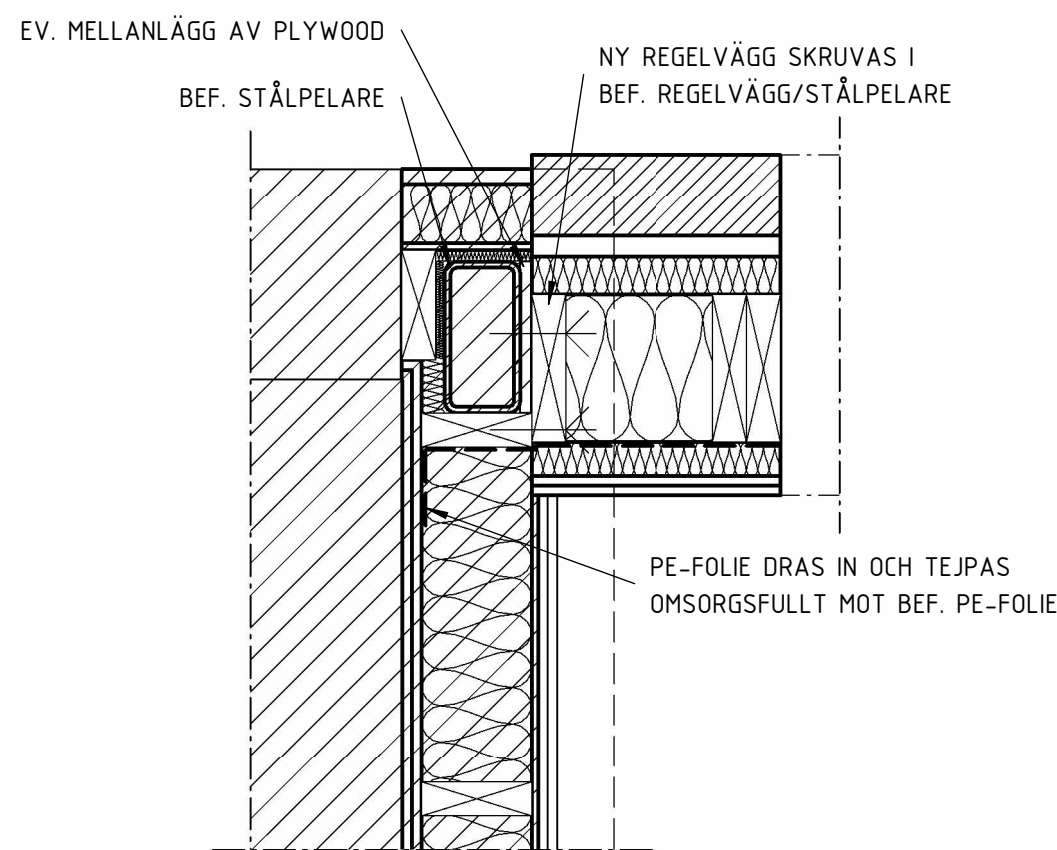

12
1 : 10
ANSLUTNING MOT BEFINTLIGT

SKALA 1:10 0 100 1000 MILLIMETER

SEKTION		
ORIENTERINGSSKISS		
STATUS		
FÖRFRÅGNINGSUNDERLAG		
HANDLING		
BYGGHANDLING		
DATUM	FÖRFRÅGAD AV	ÄNDRINGS PM
2024-12-20	BJÖRN LIDSTRÖM	
BESTÄLLARE		
ROBERTSFORS KOMMUN		
PROJEKTNAMN		
CENTRALKÖK		
OMRÅDE		
ROBERTSFORS KOMMUN		
PROJEKTNUMMER	FASTIGHET	
108 83 71	YTTRE RINGVÄGEN 4	
DOKUMENTNUMMER	FÖRETAG	
	FORDONET 1	
DIREKTÖR	FÖRETAG	
K	NORCONSULT SVERIGE AB	
UPPDRAGSNUMMER	SKAPAD AV	
108 83 71	AWG/ATN	
TELEFON	KONTAKTPERSON	
010-141 80 00	BJÖRN LIDSTRÖM	
BYGGGÅRSTID	PRIS/STYCKE	
	+45,540 (FG)	
VÄNINGSPLAN	VÄNINGSDEL	DELOMRÅDE
		DEL 4, 5
SYSTEM		
20 SAMMANSATTA KONSTRUKTIONER		
SPECIFIKATION		
BYGGDETALJER		
DETALJ	SKALA	FORMAT
	1:10	A1
DOKUMENTNUMMER		
K-20-6-001		