

FÖRKLARINGAR

BEFINTLIG BYGGNAD

PILMÅTT TAS FRÅN NÄRMAST LIGGANDE STOMLINJE (MINST 1 METER)

INNERDÖRRAR OCH FÖNSTER VISAS ENDAST SCHEMATISKT I SAMTLIGA K-HANDLINGAR. FÖR EXAKT PLACERING OCH MÄTTSÄTTNING, SE A-HANDLINGAR.


DUBBLA VÄGGREGLAR PLACERAS PÅ RESPEKTIVE SIDA OM SAMTLIGA DÖRRAR OCH FÖNSTER OM EJ ANNAT ANGES.

FÖRESKRIFTER


K-01-0-001 -- 003 ALLMÄNNA FÖRESKRIFTER

HÄNVISNINGAR


-

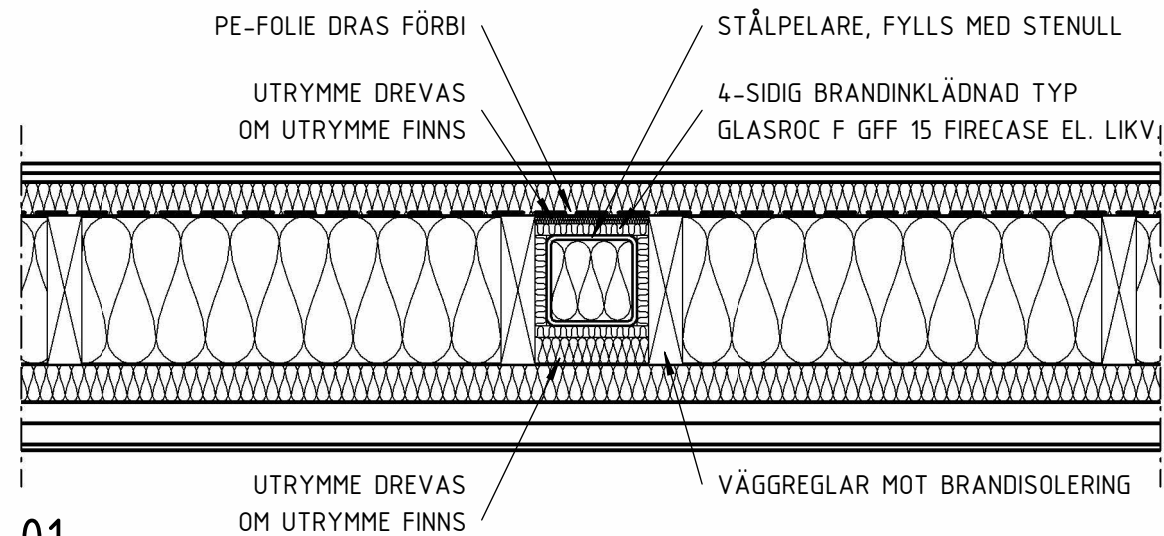


01
1 : 10
STÅLPELARE I YTTERVÄGG

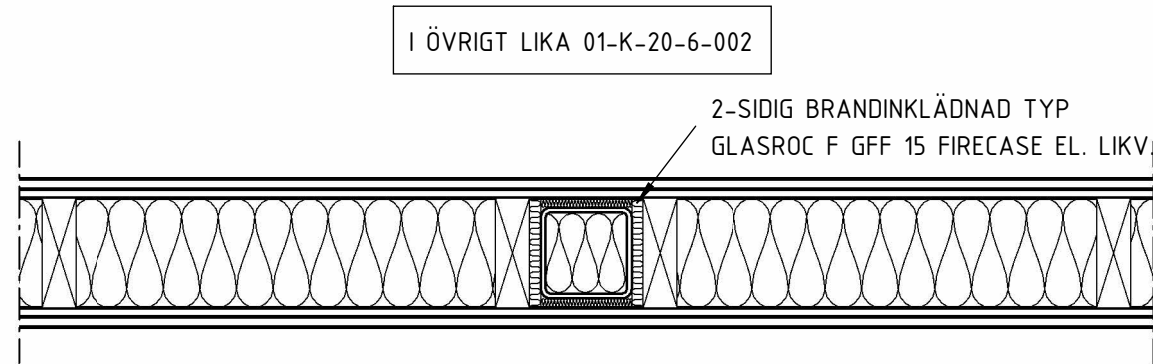


02
1 : 10
STÅLPELARE I BÄRANDE INNERVÄGG

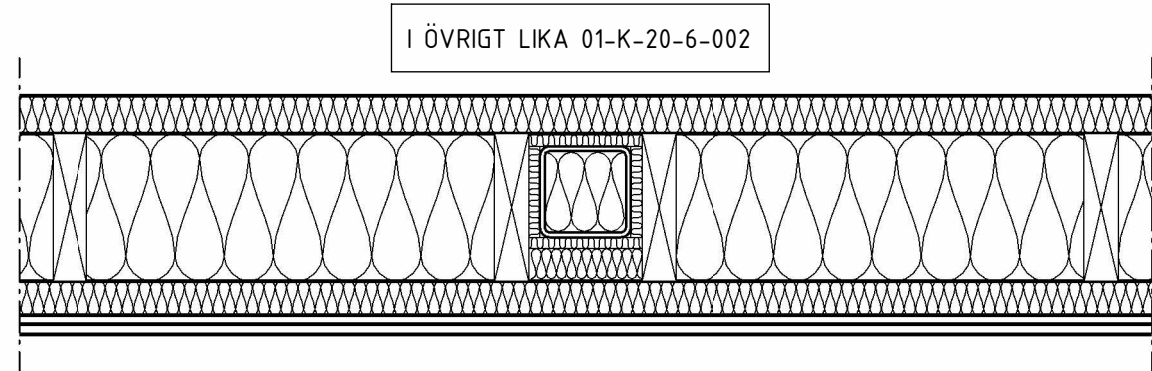


03
1 : 10
STÅLPELARE I FLÄKTRUMSVÄGG

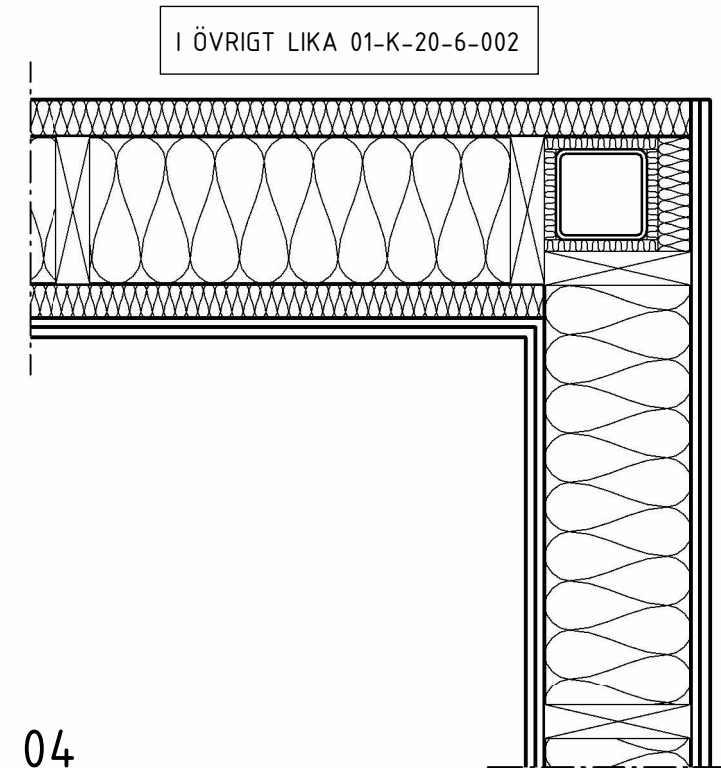


04
1 : 10
STÅLPELARE I FLÄKTRUMSVÄGG HÖRN

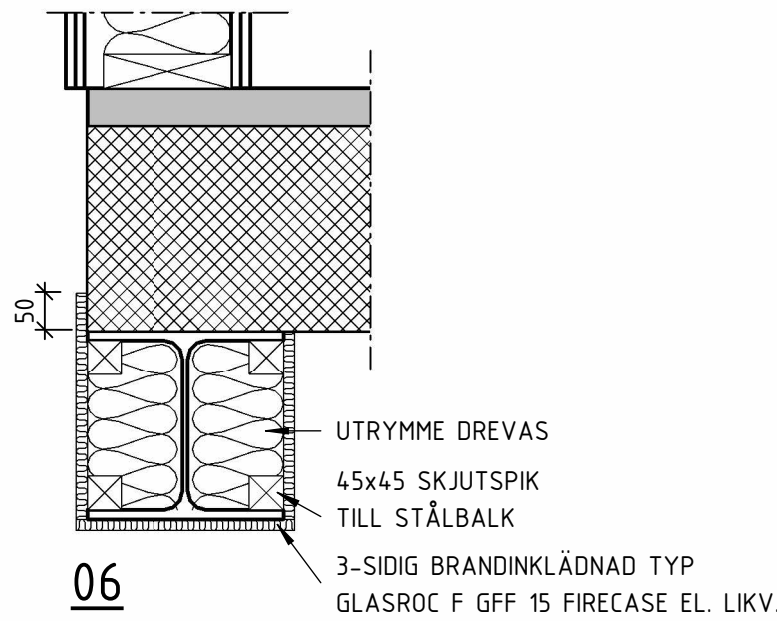


06
1 : 10
STÅLBALK UNDER HÅLDÄCK KANT

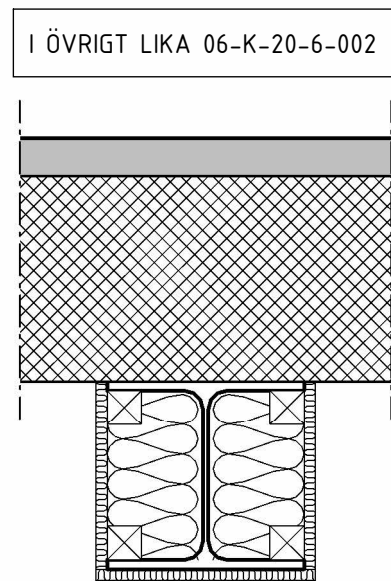


07
1 : 10
STÅLBALK UNDER HÅLDÄCK MITTEN

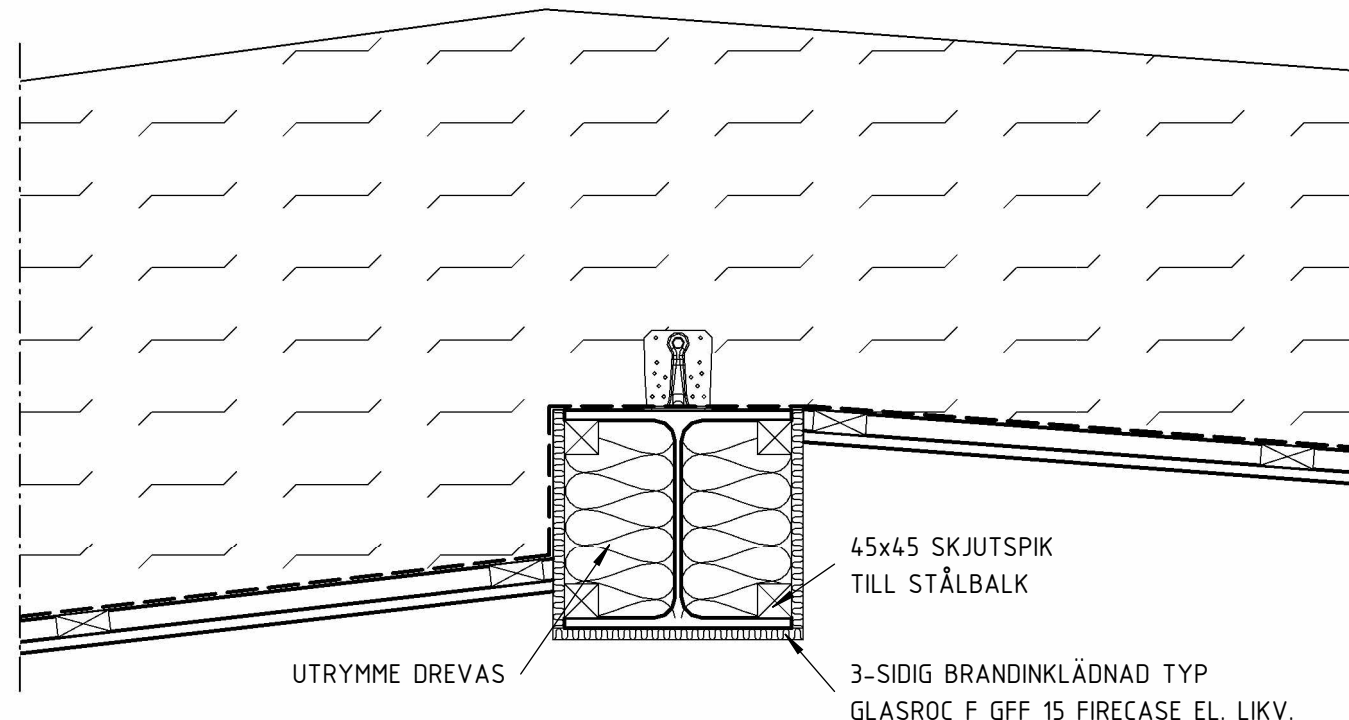

08
1 : 10
STÅLBALK UNDER TAKSTOLAR

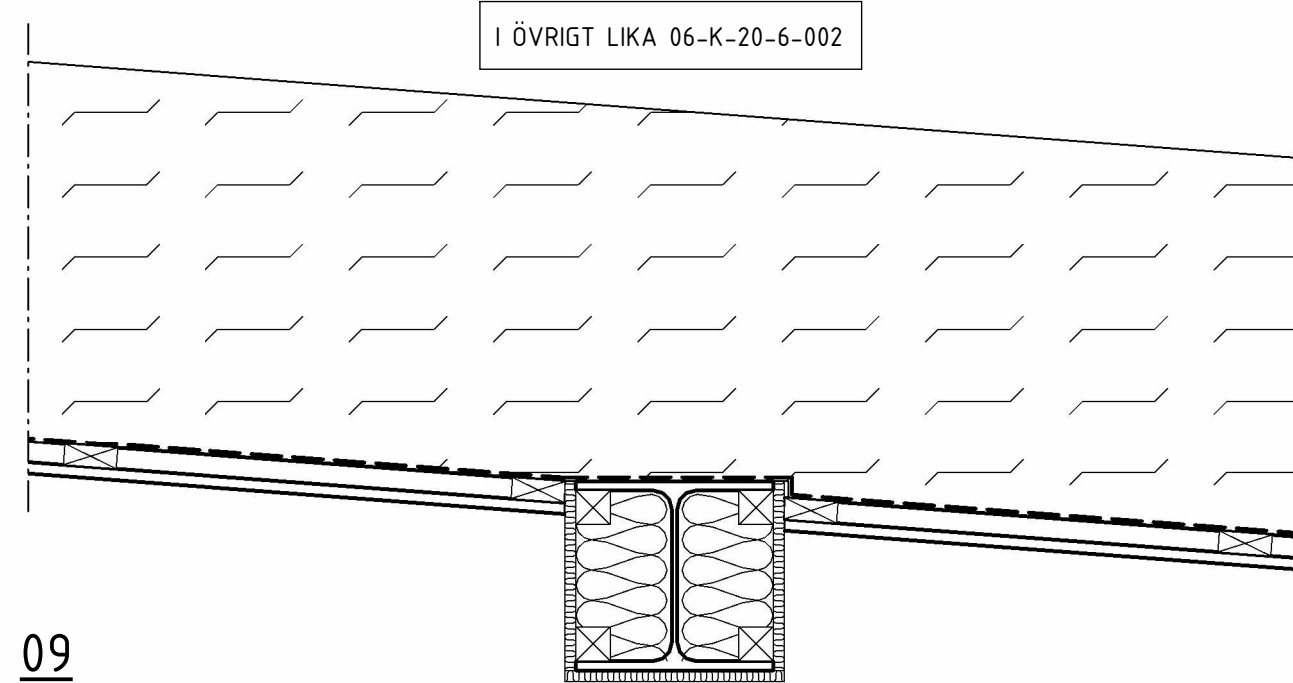

09
1 : 10
STÅLBALK UNDER TAKSTOLAR

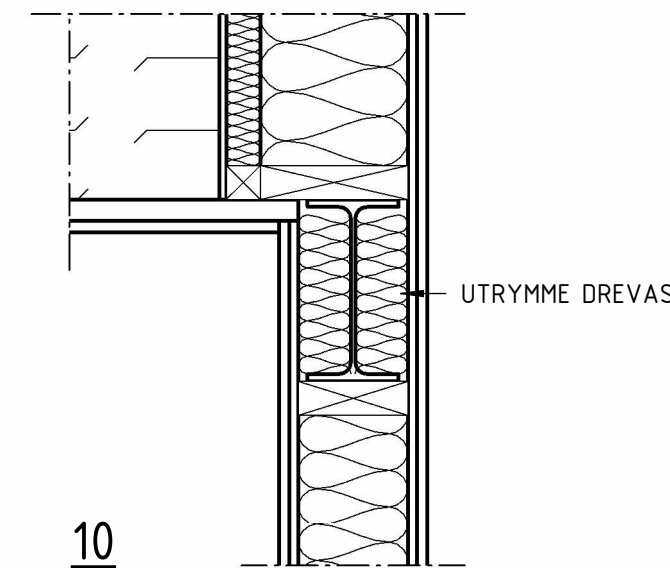

10
1 : 10
STÅLBALK I BÄRANDE INNERVÄGG

SKALA 1:10 0 100 1000 MILLIMETER

SEKTION		
ORIENTERINGSFIGUR		
STATUS		
FÖRFRÅGNINGSUNDERLAG		
HANDLING		
BYGGHANDLING		
DATUM	GÖRANDE AV	ÄNDRINGS PM
2024-12-20	BJÖRN LIDSTRÖM	
BESTÄLLARE		
 ROBERTSFORS KOMMUN		
PROJEKTNAMN		
CENTRALEKÖK		
OBJEKT		
ROBERTSFORS KOMMUN		
PROJEKTNUMMER	FASTIGHET	
108 83 71	YTTRE RINGVÄGEN 4	
DOKUMENTNUMMER	FÖRETAG	
	FORDONET 1	
DISCIPLIN	FÖRETAG	
K	NORCONSULT SVERIGE AB	
UPPRORGSNUMMER	SKAPAD AV	
108 83 71	AWG/ATN	
TELEFON	KONTAKTPERSON	
010-141 80 00	BJÖRN LIDSTRÖM	
BYGGKOSTNAD	FÖLJANDE PRIS	
	+45,540 (FG)	
VÄRNINGSPÅN	VÄRNINGSD	DELNING
		DEL 4, 5
SYSTEM		
20 SAMMANSATTA KONSTRUKTIONER		
SPECIFIKATION		
BRANDINKLÄDNAD AV STÅL		
TEKNIK	SKALA	FORMAT
DETALJ	1:10	A1
DOKUMENTNUMMER	ÄNDRING	
K-20-6-002		