



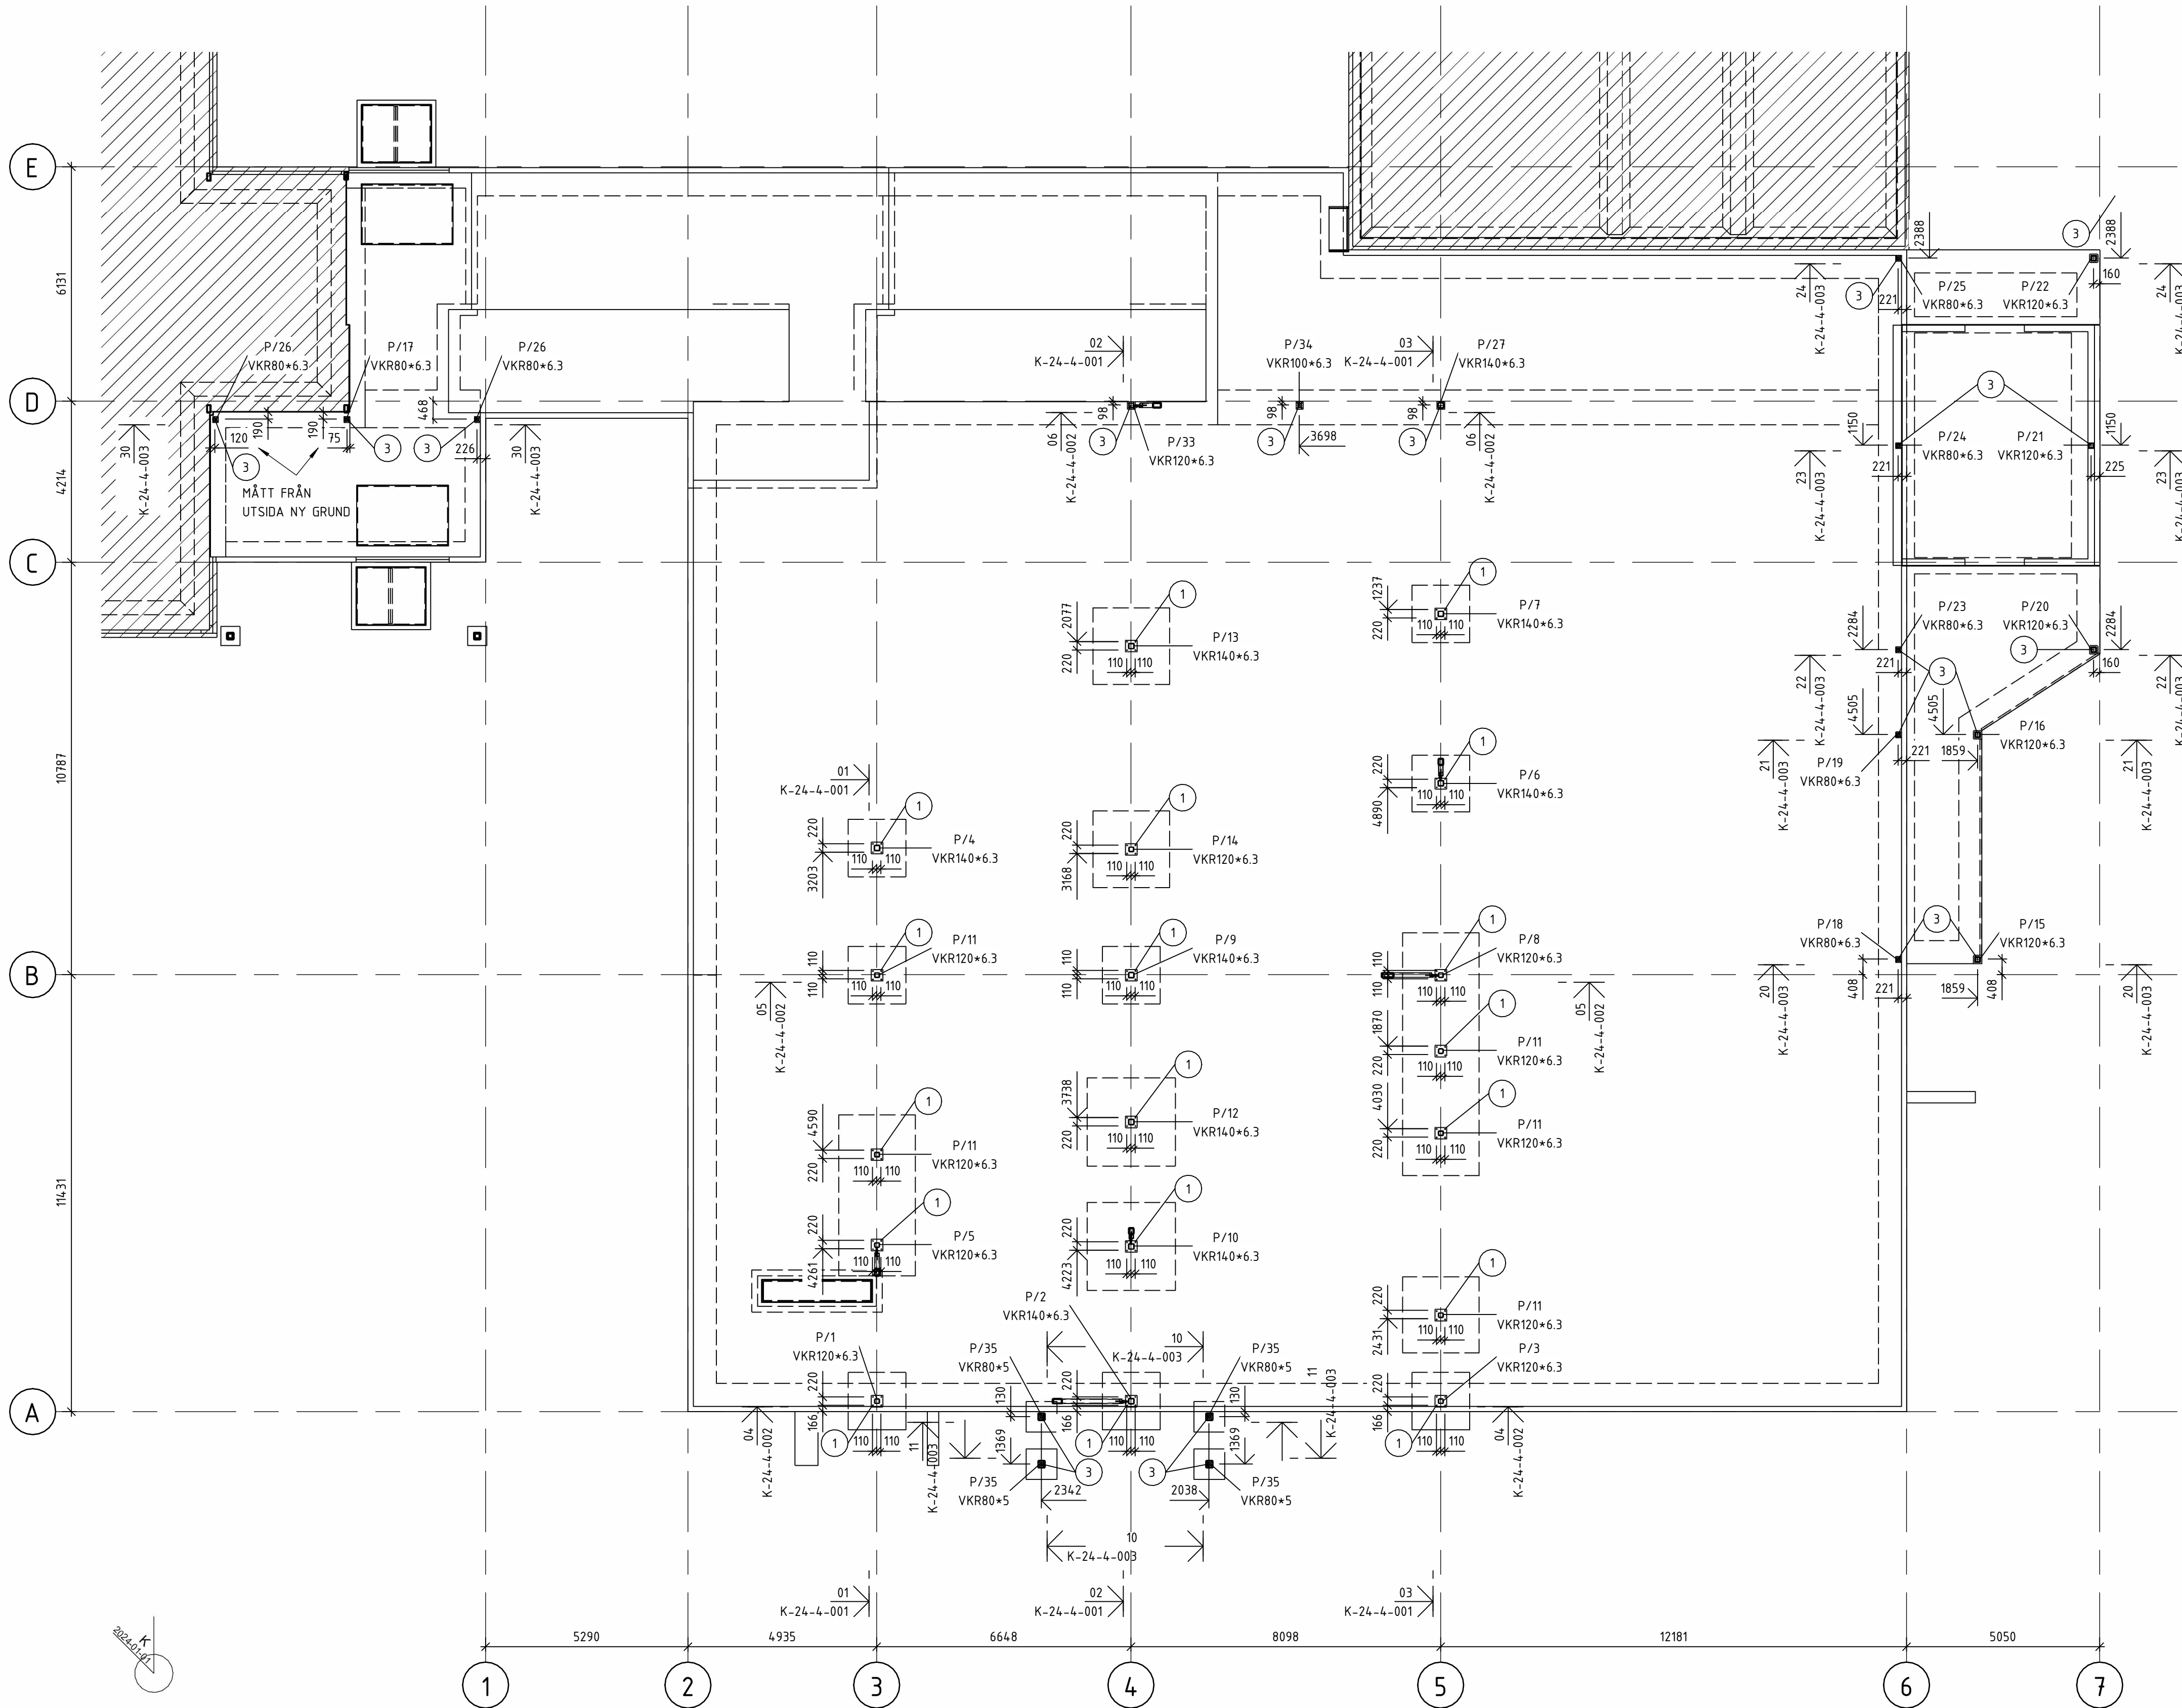

GRUNDBULTAR OCH PELARPLACERING

1 : 100
VYRIKTNING NEDÅT

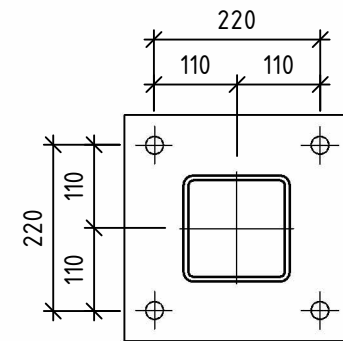

FÖRSTÖRING
1 : 10
GRUNDBULTAR

SKALA 1:100 0 1 10 METER

FÖRKLARINGAR

- BEFINTLIG BYGGNAD
- 01 4 ST M20x260 HILTI HAS 8.8 HDG INJEKTAS MED HILTI HIT-CT 100. BORRDJUP ENLIGT LEVERANTÖRS ANVISNINGAR. 50 UNDERGJUTNING UNDER FOTPLÅT.
- 02 M12 8.8 GÄNSTÅNG BOCKAS RUNT ÖVERRAM PÅ TRÄAKSTOL
- 03 PELARE PÅ SVETSPLÅT. SVETSDIMENSION ENLIGT STÅLELEVATIONER

PILMÅTT TAS FRÅN NÄRMAST LIGGANDE STOLINJE (MINST 1 METER)

FÖRESKRIFTER

K-01-0-001 -- 003 ALLMÄNNA FÖRESKRIFTER

HÄNVISNINGAR

K-24-4-001 -- 004 STÅLELEVATIONER

SEKTION

ORIENTERINGSFIGUR

STATUS

FÖRFRÅGNINGSUNDERLAG

HANDLING

BYGGHANDLING

DATUM 2024-12-20

ANSÖKAN BJÖRN LIDSTRÖM

ÄNDRINGS PM

BESTÄLLARE

ROBERTSFORS KOMMUN

PROJEKTNAMN

CENTRALEKÖK

KOMMUNE

ROBERTSFORS KOMMUN

PROJEKTNUMMER 108 83 71

YTTRE RINGVÄGEN 4

DIREKTÖRSNUMMER

FÖRSTÖRING

FORDONET 1

DIREKTÖRS

NORCONSULT SVERIGE AB

UPPDRAGSNUMMER 108 83 71

AWG/ATN

TELEFON 010-141 80 00

BJÖRN LIDSTRÖM

BYGGNADSTYRELSE

+45 540 (FG)

VÄNINGSPLAN

DEL 4, 5

SYSTEM

24 STÅLKONSTRUKTIONER

SPESIFIKATION

GRUNDBULTAR OCH PELARPLACERING

BYGGNADSTYRELSE

PLAN

1:100

A1

ÄNDRING

K-24-1-100