


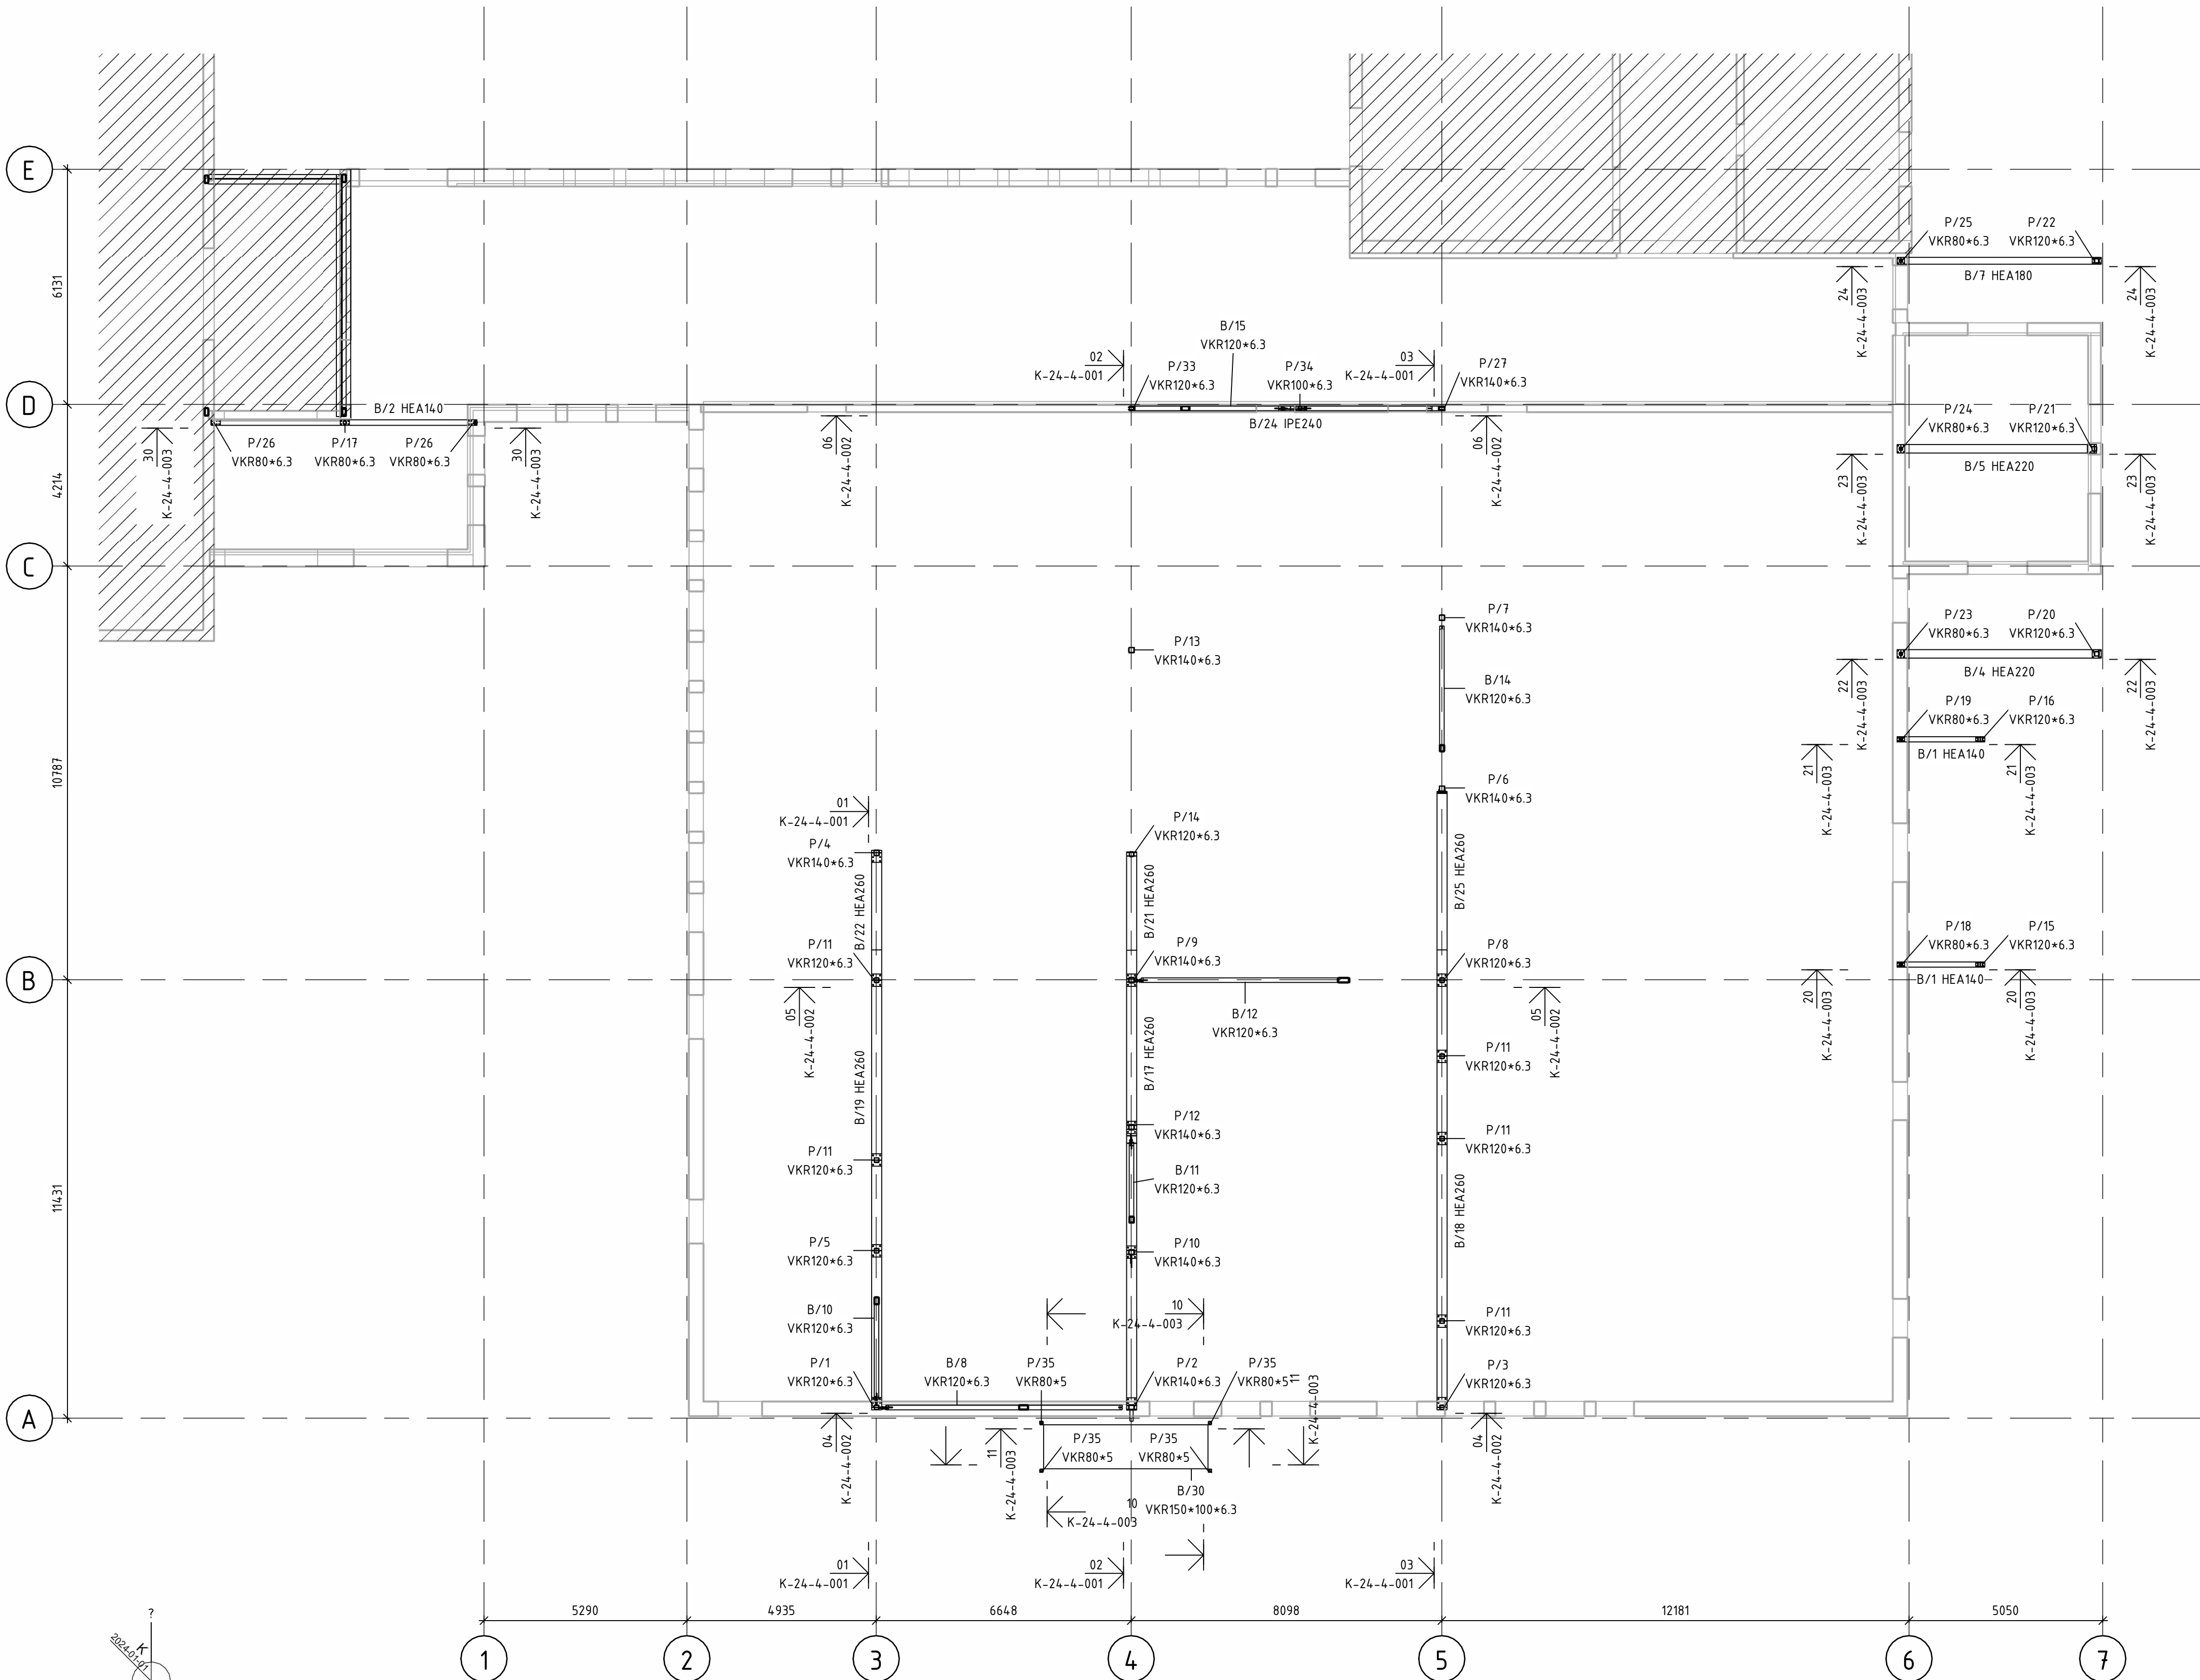

STÅLPLAN
1 : 100
VYRIKTNING UPPÅT

SKALA 1:100 0 1 10 METER

FÖRKLARINGAR

- BEFINTLIG BYGGNAD
- 01 4 ST M20x260 HILTI HAS 8.8 HDG INJEKTAS MED HILTI HIT-CT 100. BORRDJUP ENLIGT LEVERANTÖRS ANVISNINGAR. 50 UNDERGJUTNING UNDER FOTPLÅT.
- 02 M12 8.8 GÄNSTÅNG BOCKAS RUNT ÖVERRAM PÅ TRÄTAKSTOL
- 03 PELARE PÅ SVETSPLÅT. SVETSDIMENSION ENLIGT STÅLELEVATIONER


PILMÅTT TAS FRÅN NÄRMAST LIGGANDE STOMLINJE (MINST 1 METER)

FÖRESKRIFTER

K-01-0-001 -- 003 ALLMÄNNA FÖRESKRIFTER

HÄNVISNINGAR

K-24-4-001 -- 004 STÅLELEVATIONER

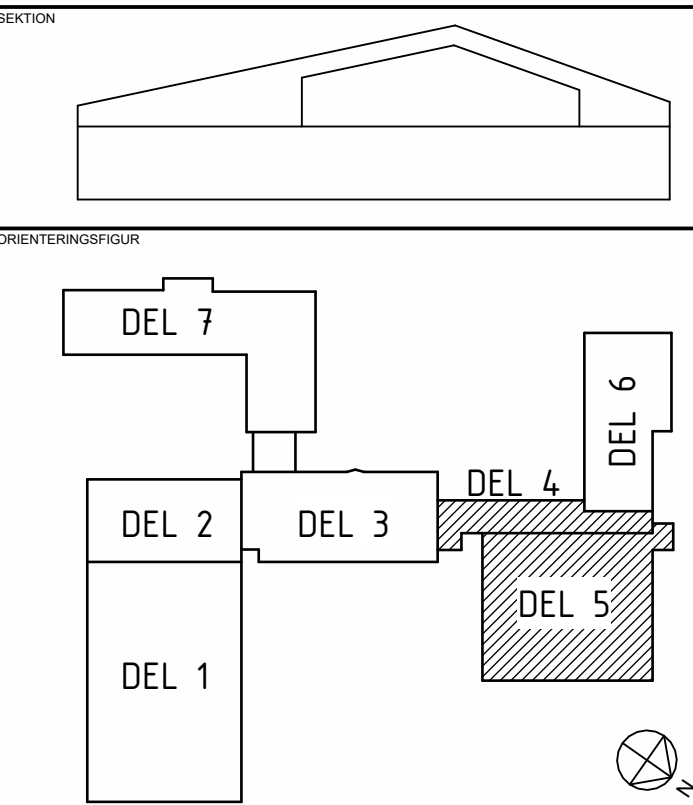

STATUS
FÖRFRÅGNINGSUNDERLAG

HANDLING
BYGGHANDLING

DATUM
2024-12-20

ANSÖKAN AV
BJÖRN LIDSTRÖM

ÄNDRINGS FM

BESTÄLLARE
 ROBERTSFORS KOMMUN

PROJEKTNAMN
CENTRALEKÖK

OMRÅDE
ROBERTSFORS KOMMUN

PROJEKTNUMMER
108 83 71

ADRESS
YTTRE RINGVÄGEN 4

DOKUMENTNUMMER
FORDONET 1

DISCIPLIN
K

FÖRETAG
NORCONSULT SVERIGE AB

UPPDRAGSNUMMER
108 83 71

SKAPAD AV
AWG/ATN

TELEFON
010-141 80 00

KONTAKTPERSON
BJÖRN LIDSTRÖM

BYGGKOSTNAD
+45,540 (FG)

VÄNINGSPLAN
DEL 4, 5

SYSTEM
24 STÅLKONSTRUKTIONER

SPECIFIKATION
STÅLPLAN

UTDRAGSNUMMER
PLAN

SKALA
1:100

FORMAT
A1

DOKUMENTNUMMER
K-24-1-110

ÄNDRING