




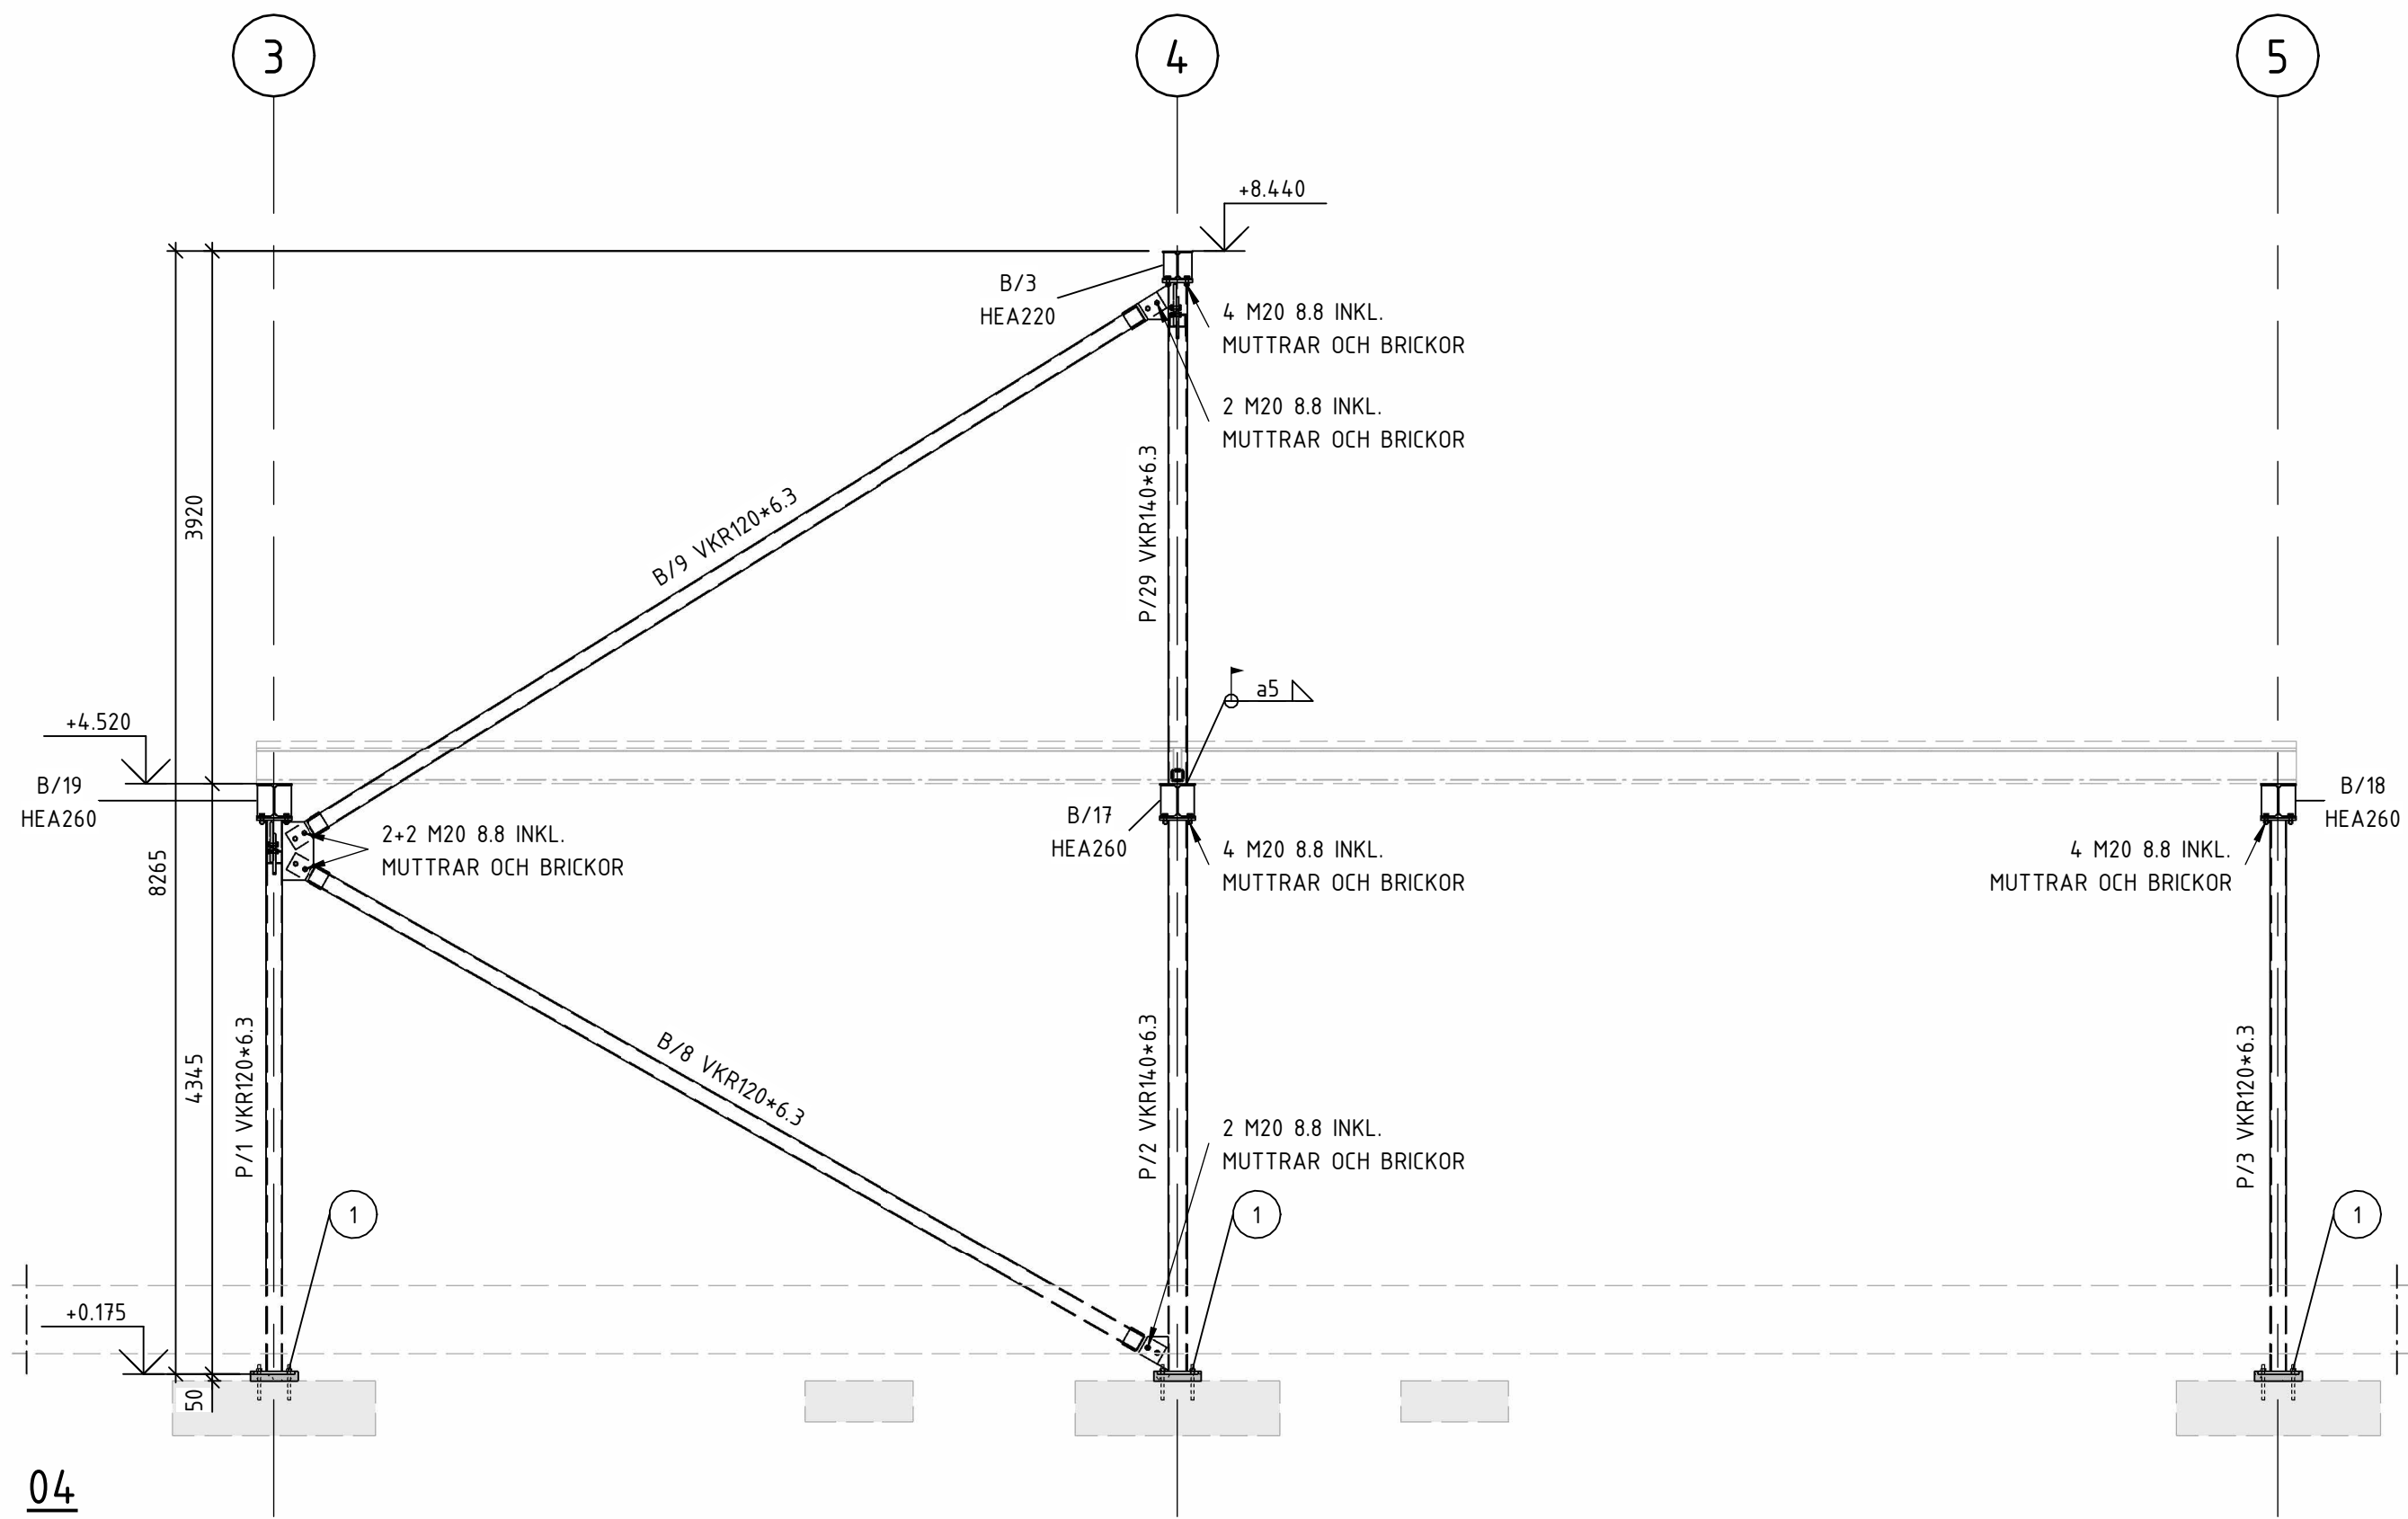

04
1 : 50

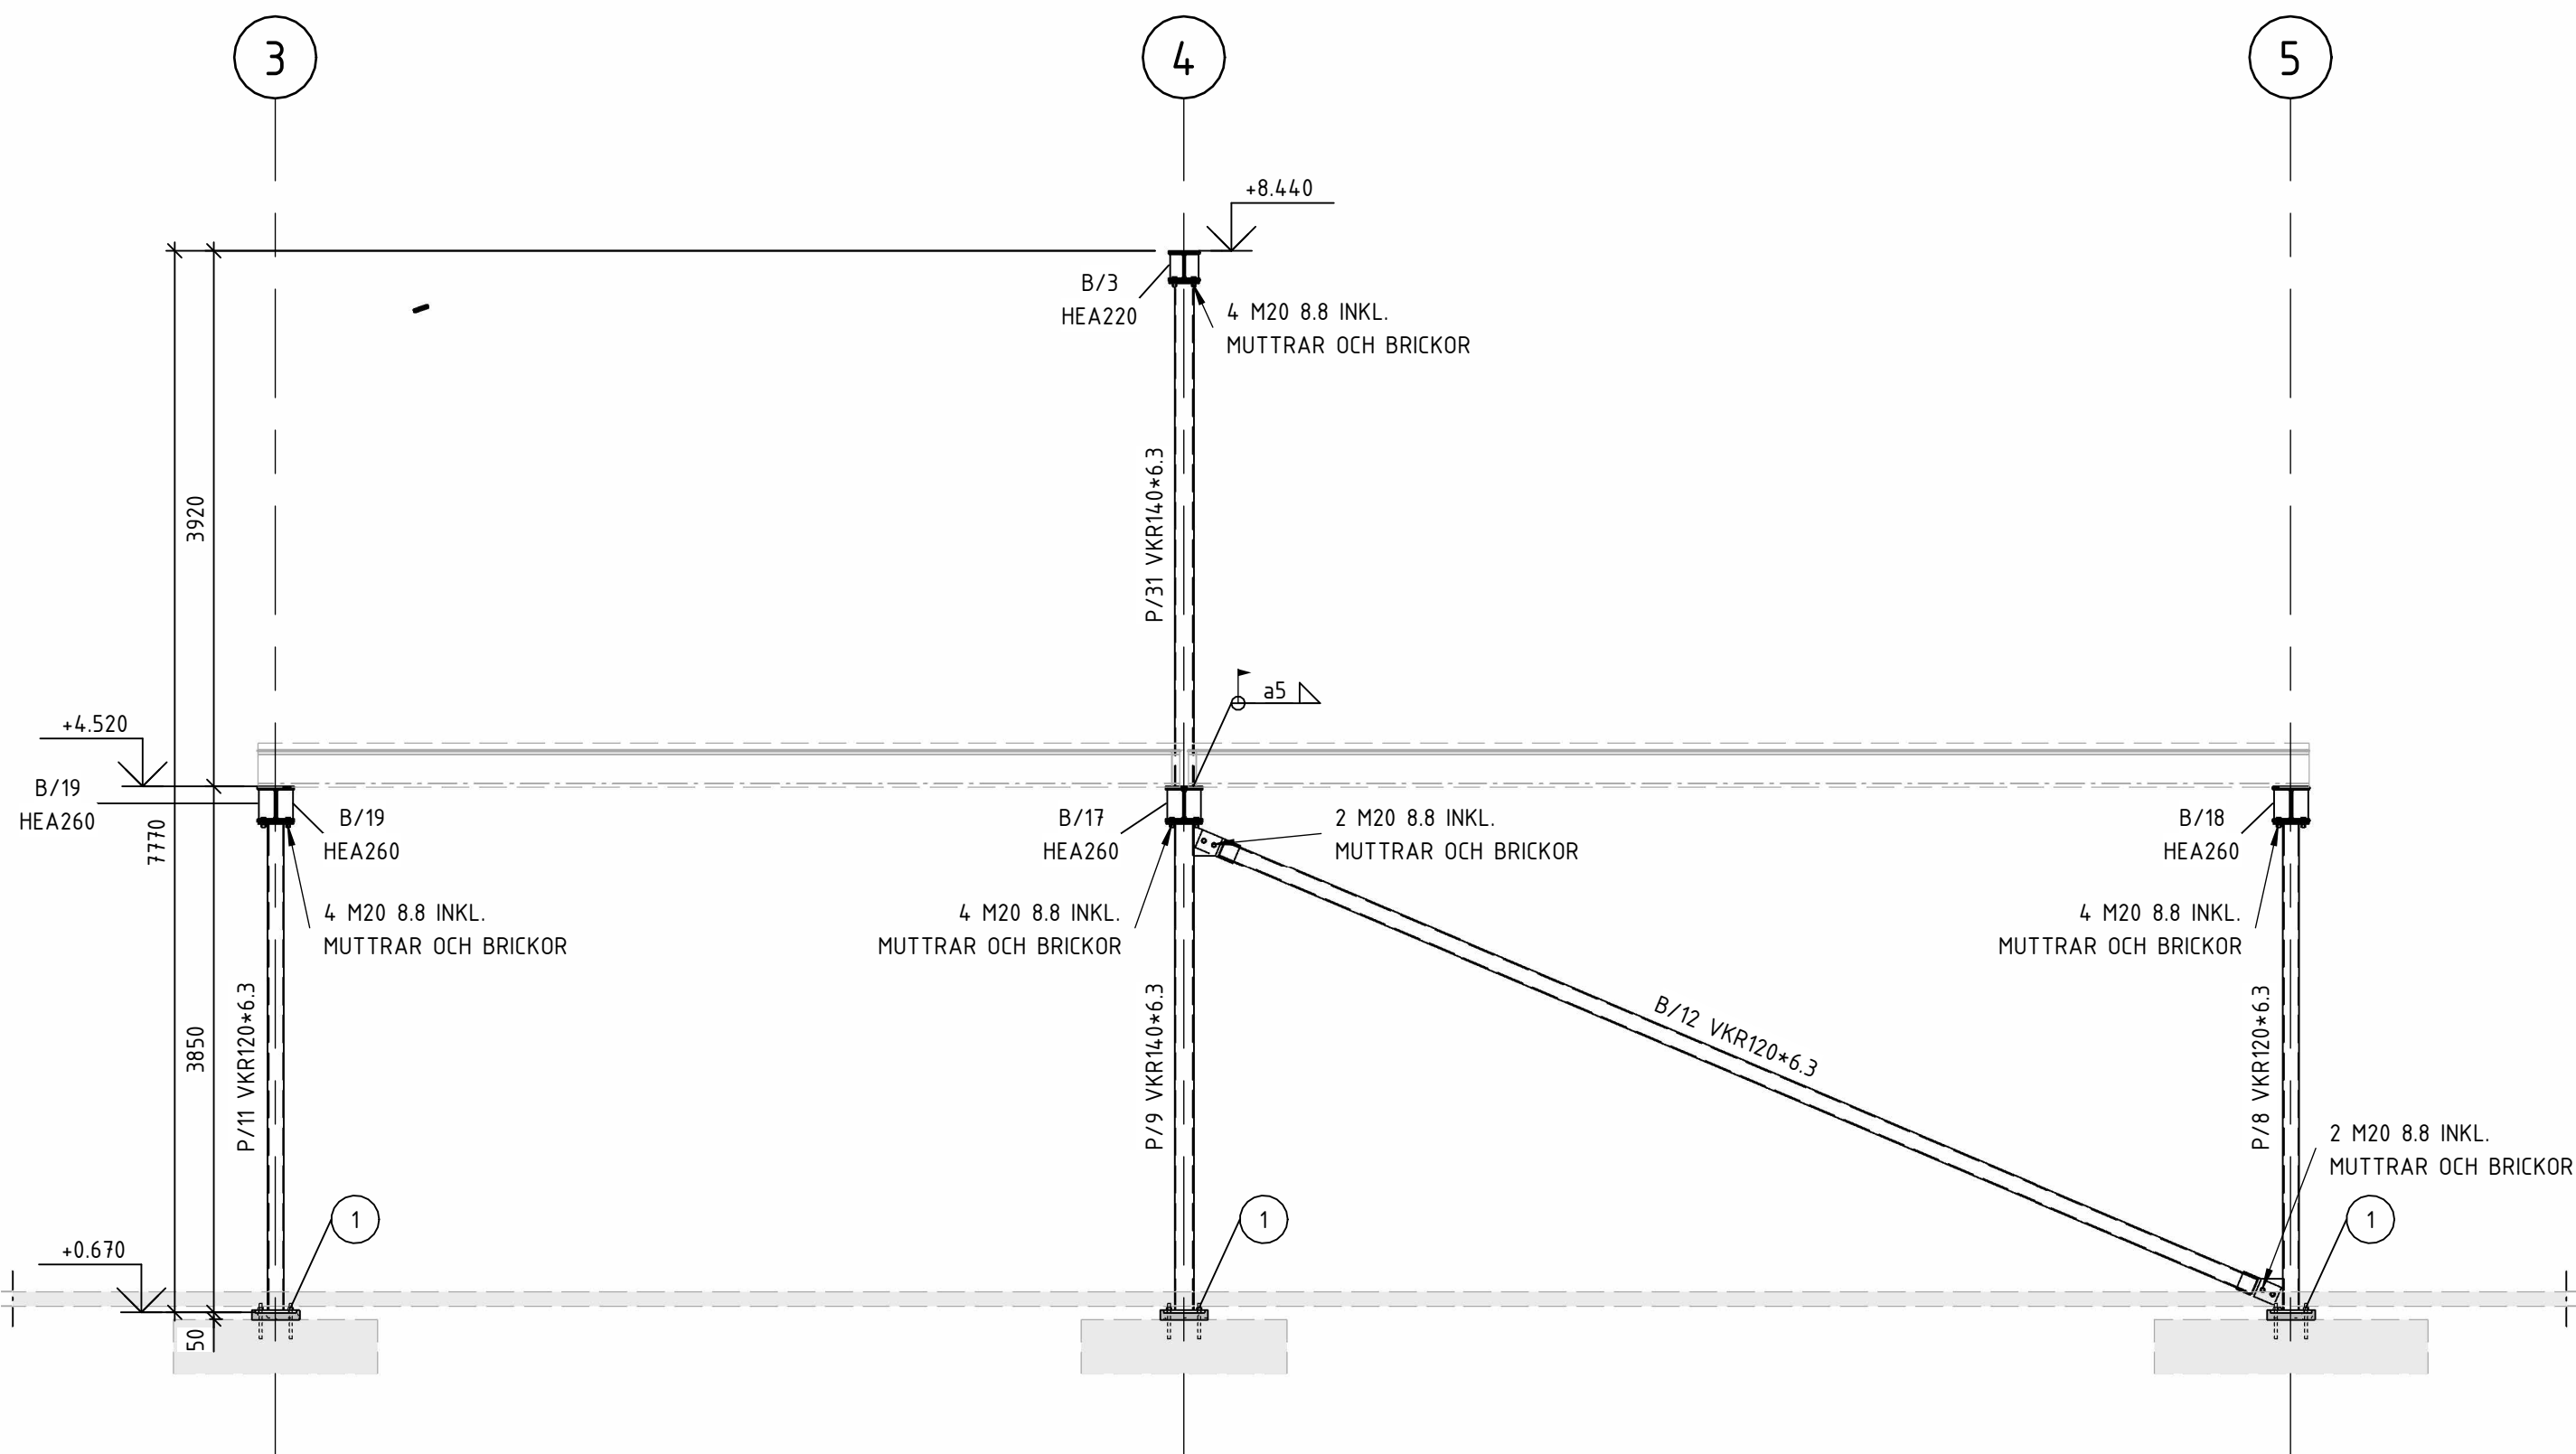

05
1 : 50

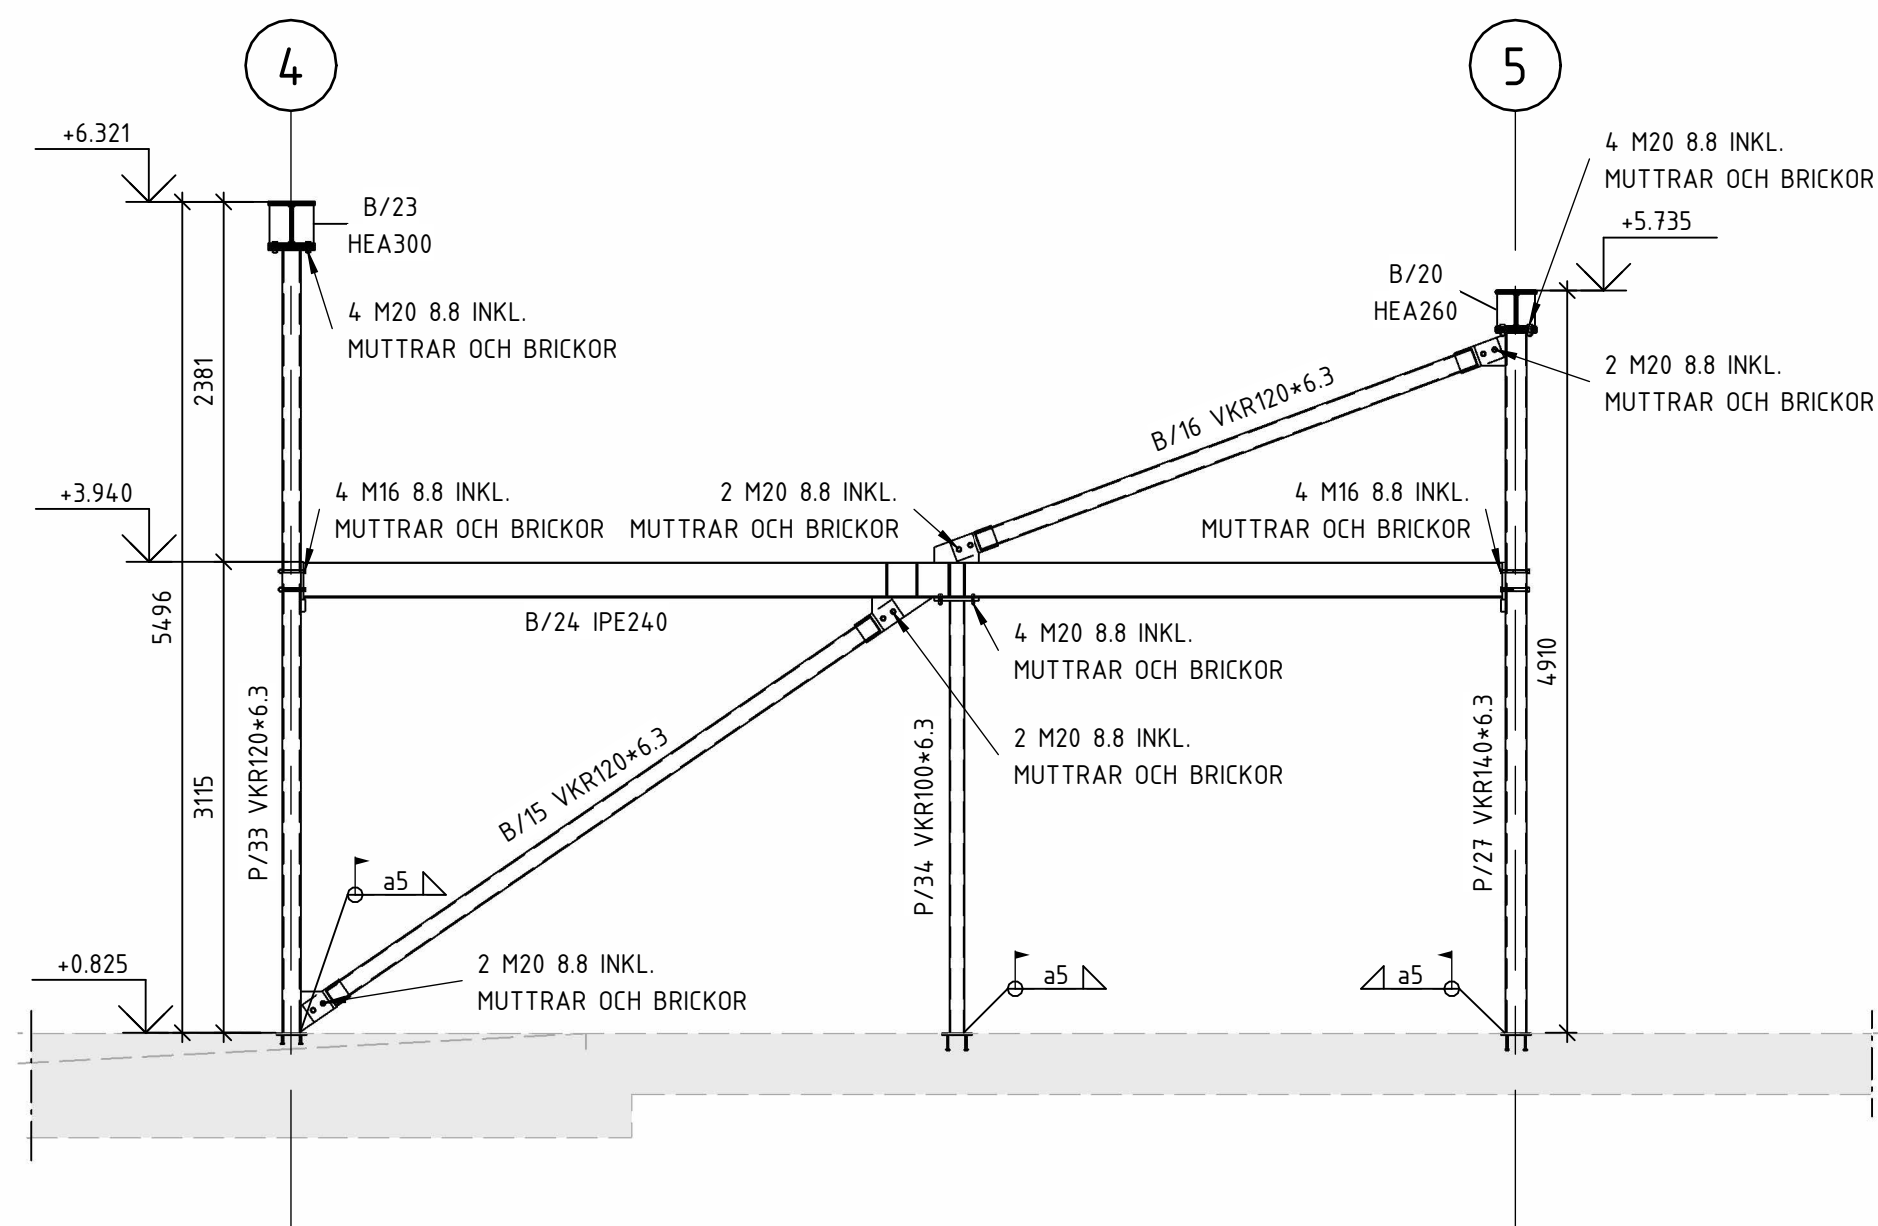

06
1 : 50

SKALA 1:50 0 1 5 METER

FÖRKLARINGAR

BEFINTLIG BYGGNAD

- 4 ST M20x260 HILTI HAS 8.8 HDG INJEKTAS MED HILTI HIT-CT 100. BORRDJUP ENLIGT LEVERANTÖRS ANVISNINGAR. 50 UNDERGJUTNING UNDER FOTPLÅT.
- M12 8.8 GÄNSTÅNG BOCKAS RUNT ÖVERRAM PÅ TRÅTAKSTOL
- PELARE PÅ SVETSPLÅT. SVETSDIMENSION ENLIGT STÅLELEVATIONER

a5 SVETS GÄLLER OM EJ ANNAT ANGES

FÖRESKRIFTER

K-01-0-001 -- 003 ALLMÄNNA FÖRESKRIFTER

HÄNVISNINGAR

-

SEKTION		
ORIENTERINGSFIGUR		
STATUS		
FÖRFRÅGNINGSUNDERLAG		
HANDLING		
BYGGHANDLING		
DATUM	FÖRORDAD AV	ÄNDRINGS FM
2024-12-20	BJÖRN LIDSTRÖM	
BESTÄLLARE		
 ROBERTSFORS KOMMUN		
PROJEKTNAMN		
CENTRALEKÖK		
OMRÅDE		
ROBERTSFORS KOMMUN		
PROJEKTNUMMER	FASTIGHET	
108 83 71	YTTRE RINGVÄGEN 4	
DÅRSENAMNET	FASTIGHET	
	FORDONET 1	
DISCIPLIN	FÖRETAG	
K	NORCONSULT SVERIGE AB	
UPPDRAGSNUMMER	SKAPAD AV	
108 83 71	AWG/ATN	
TELEFON	KONTAKTPERSON	
010-141 80 00	BJÖRN LIDSTRÖM	
BYGGNADSTYRE	TELEFON	
	+45,540 (FG)	
VÄNINGSPLAN	DELOMRÅDE	
	DEL 4, 5	
SYSTEM		
24 STÅLKONSTRUKTIONER		
SPECIFIKATION		
STÅLELEVATIONER		
BYGGNADSTYRE	SKALA	FORMAT
ELEVATION	1:50	A1
BYGGNADSTYRE	BYGGNADSTYRE	BYGGNADSTYRE
K-24-0-002		