




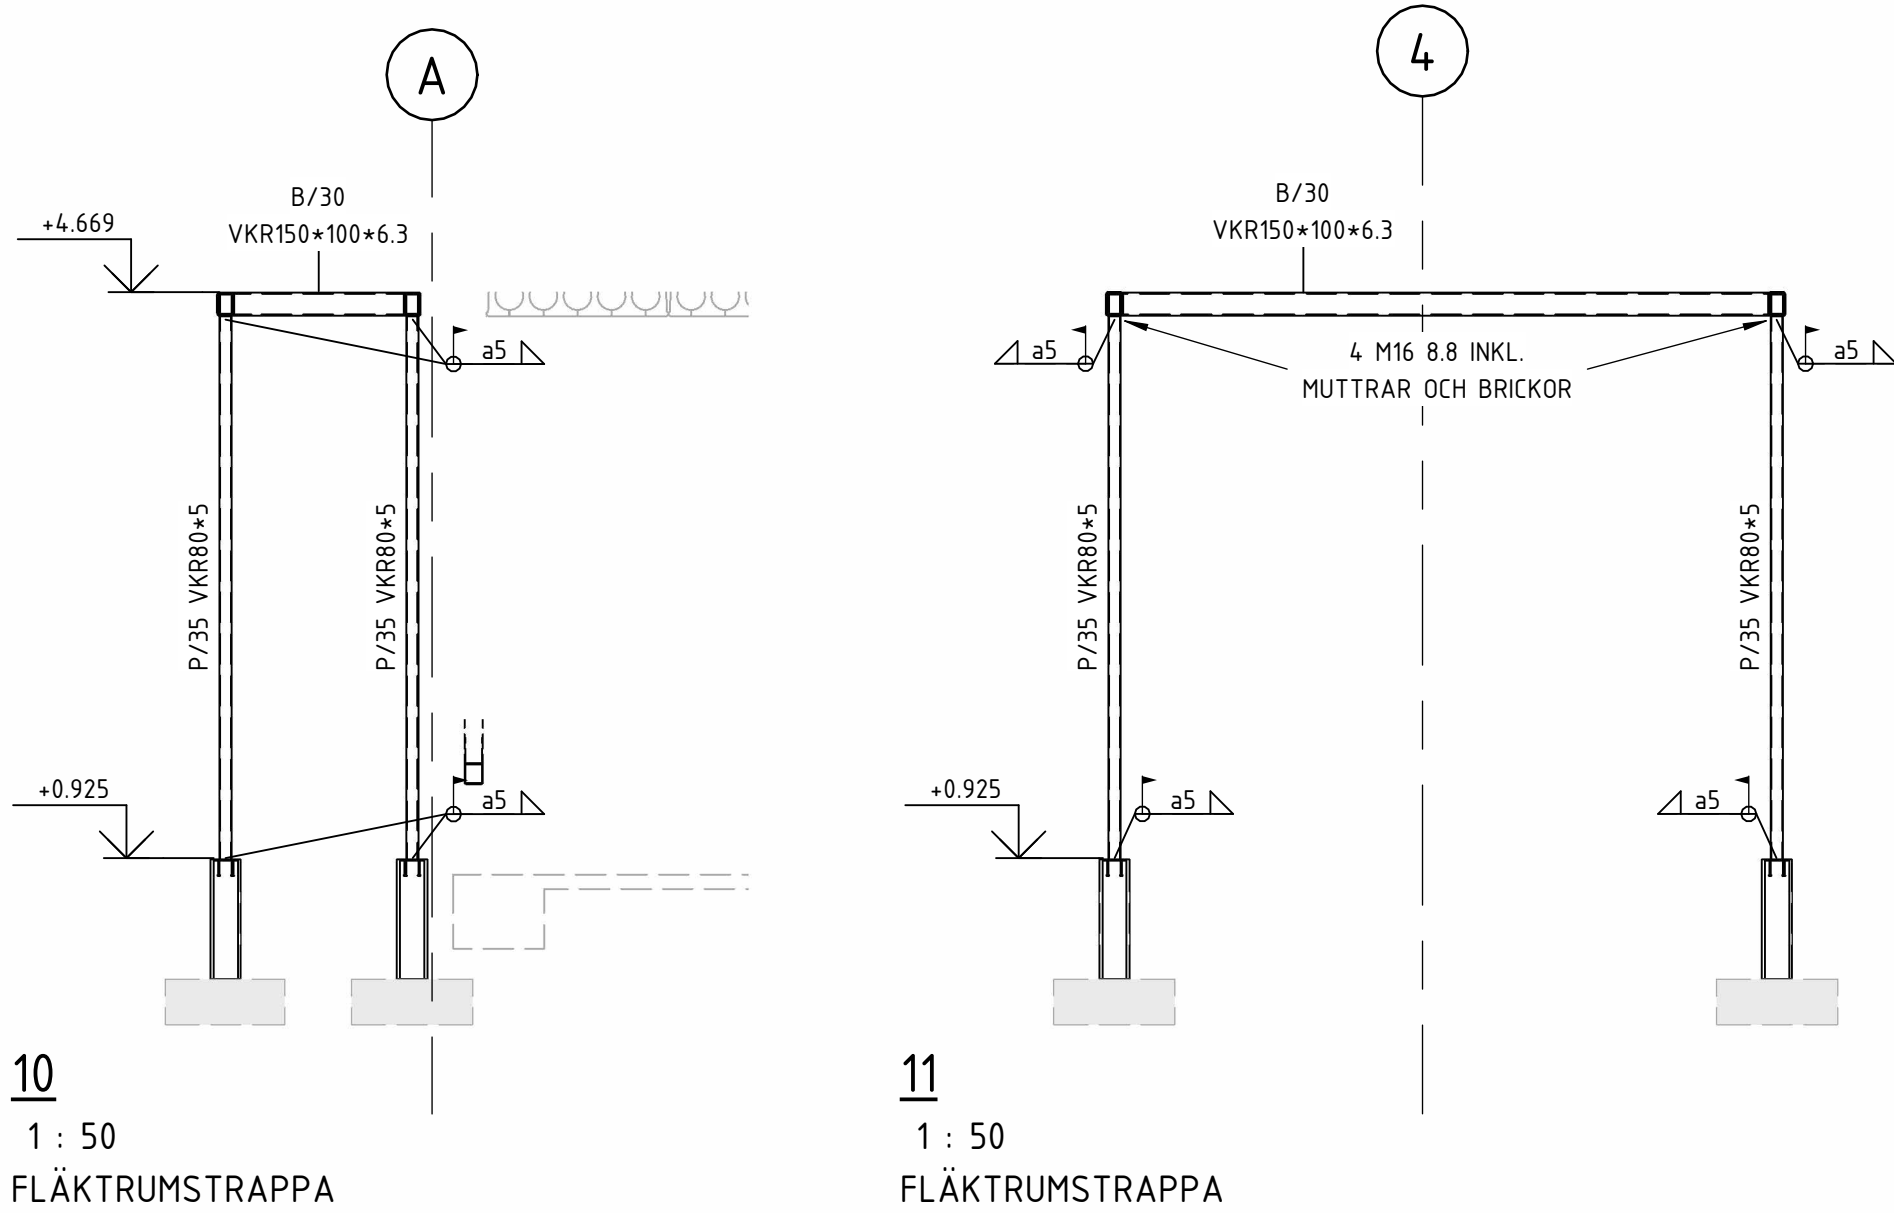


10
1 : 50
FLÄKTRUMSTRAPPA

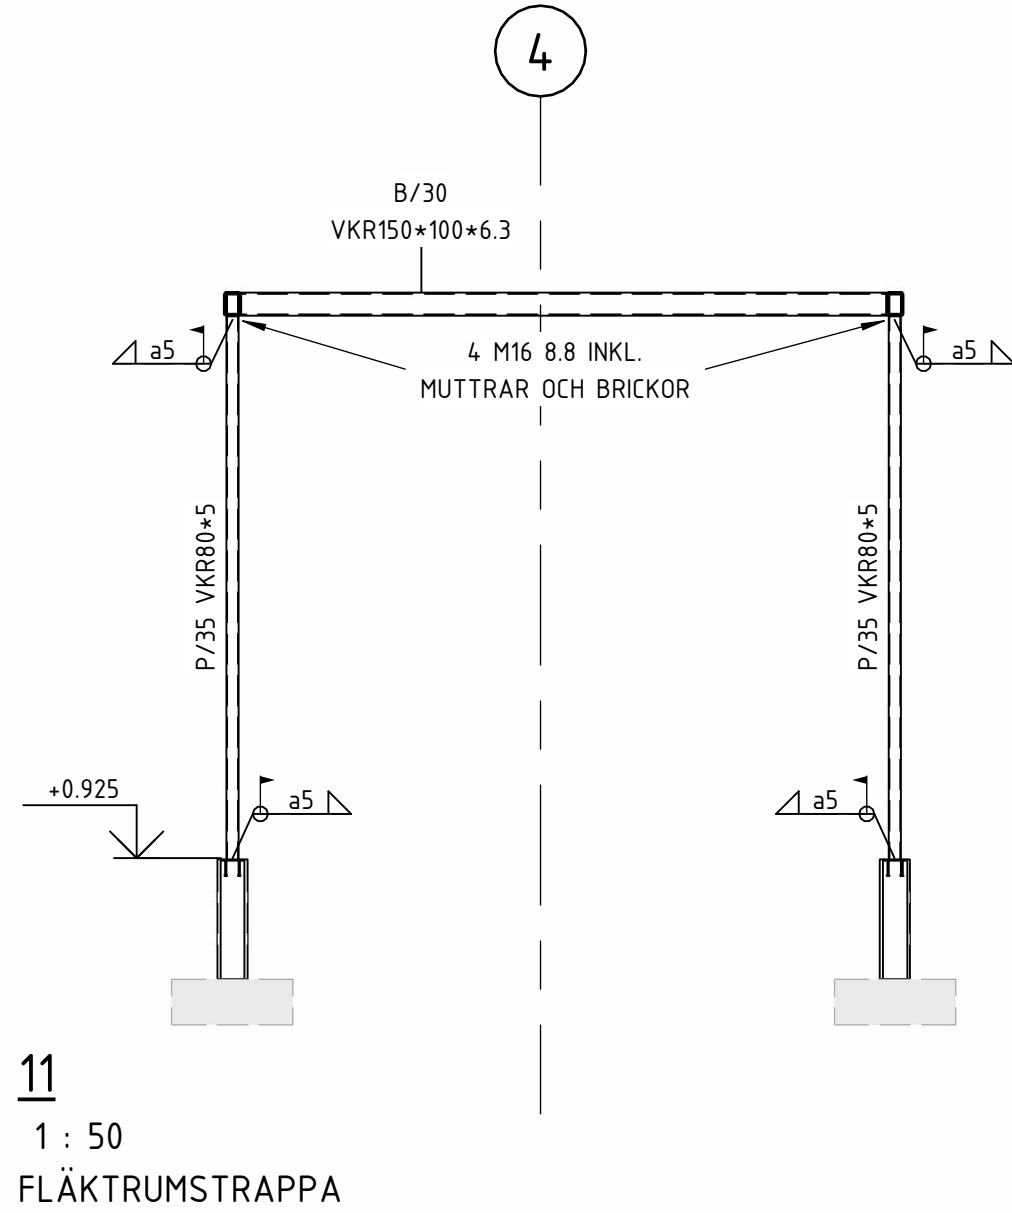


11
1 : 50
FLÄKTRUMSTRAPPA

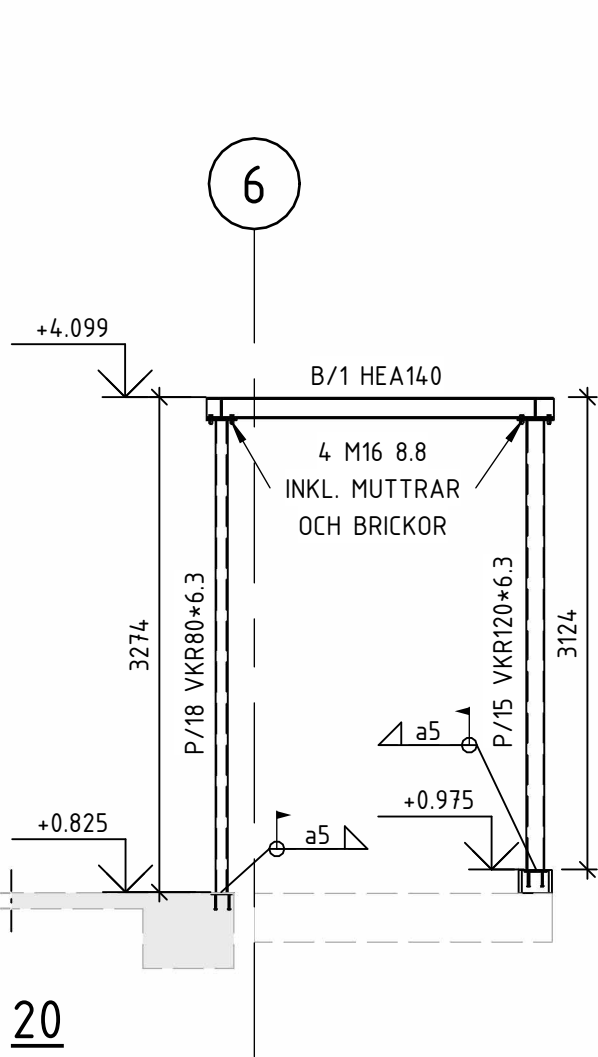


20
1 : 50
LASTKAJ

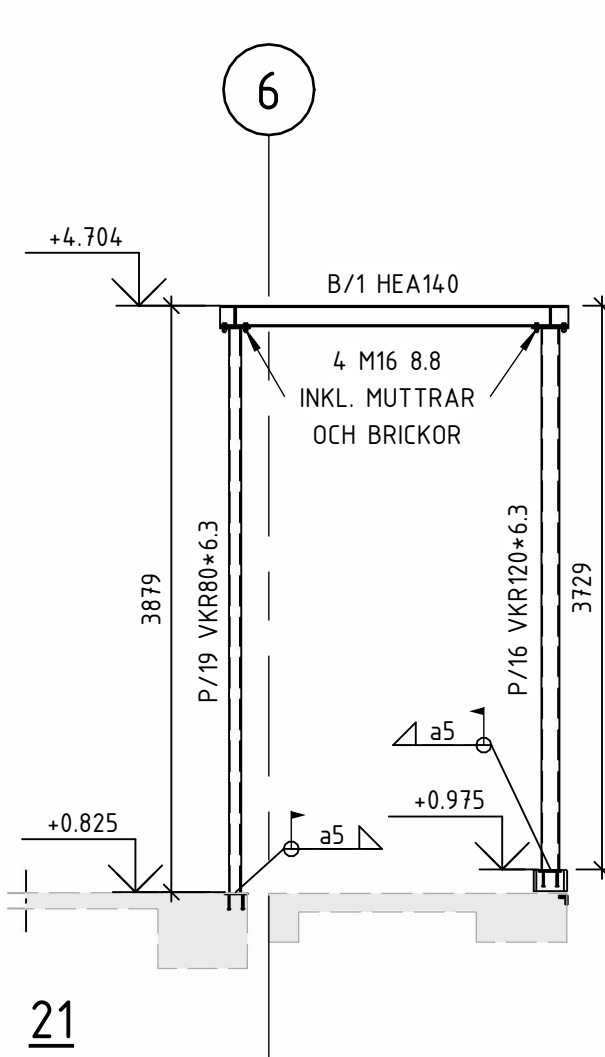


21
1 : 50
LASTKAJ

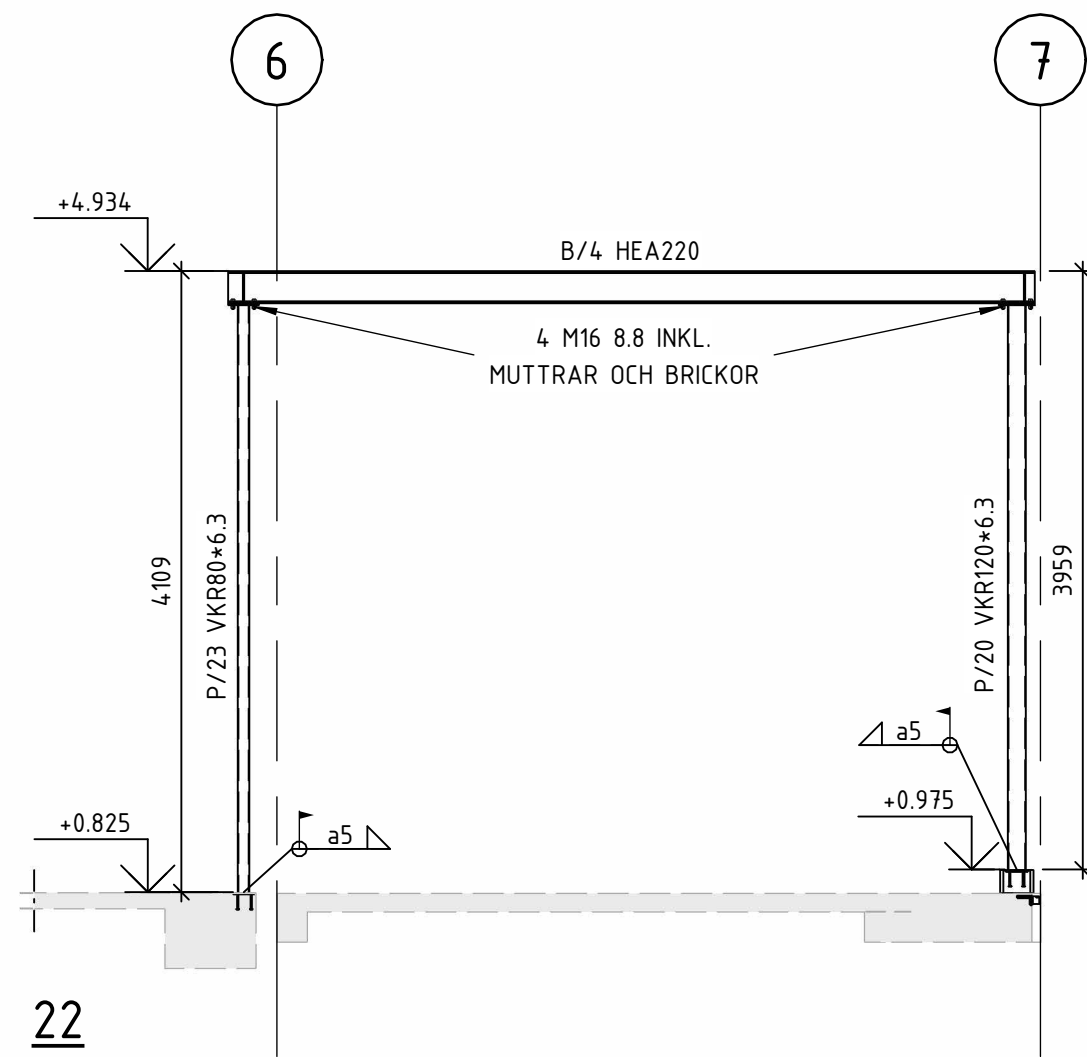


22
1 : 50
LASTKAJ

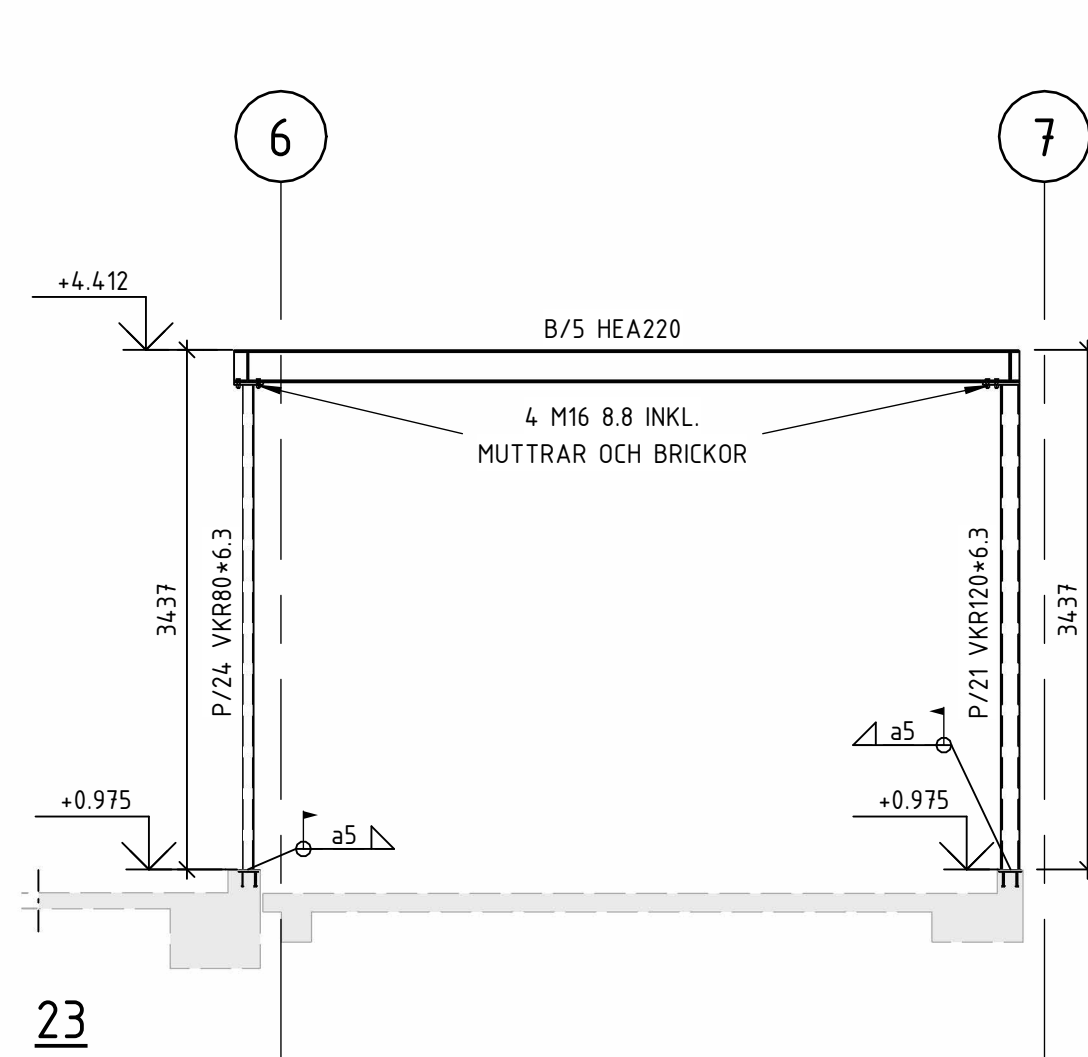

23
1 : 50
LASTKAJ

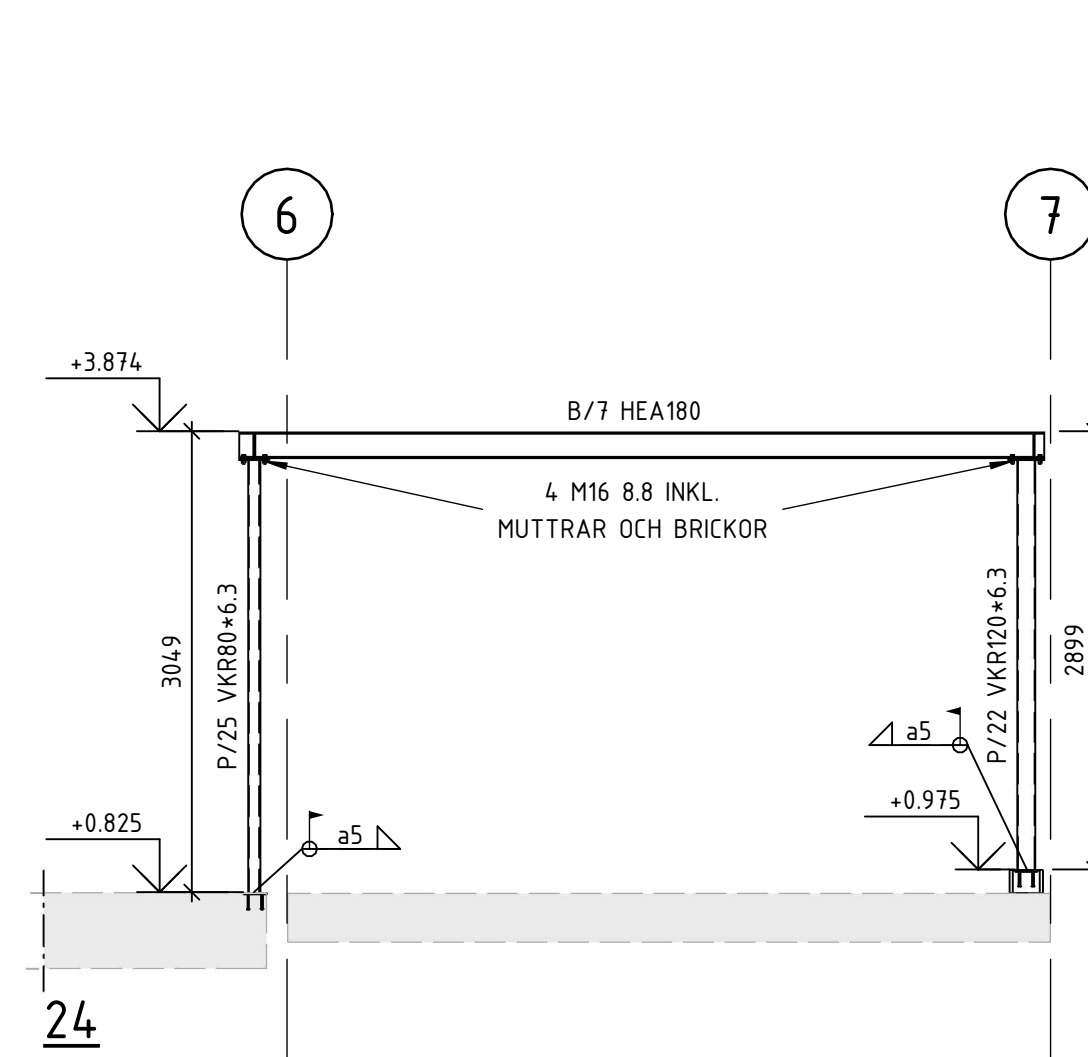

24
1 : 50
LASTKAJ

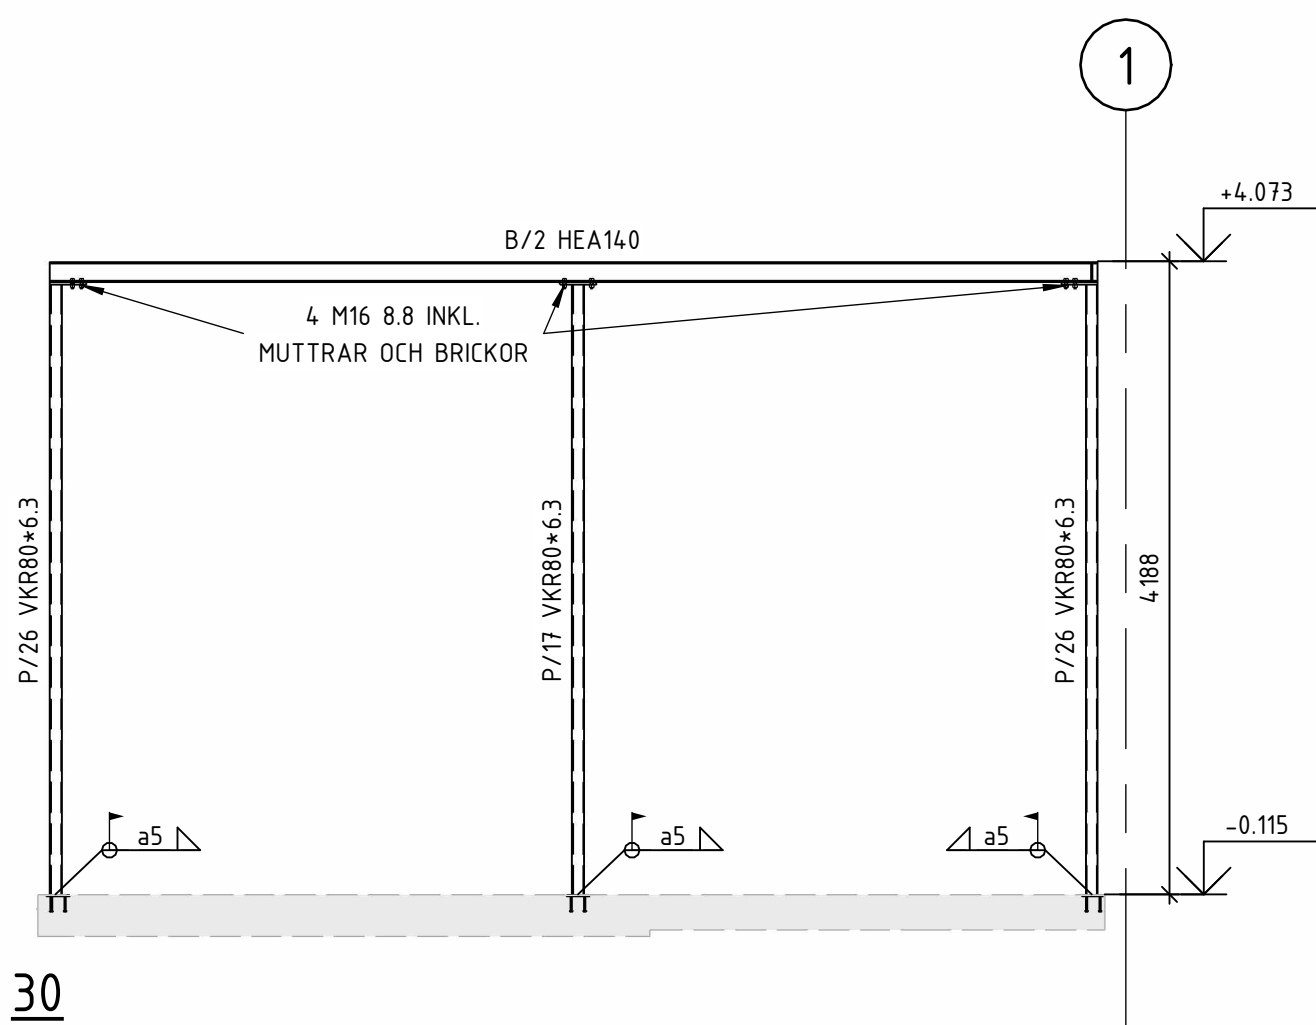

30
1 : 50
ENTRÉPASSAGE

FÖRKLARINGAR

BEFINTLIG BYGGNAD

- 4 ST M20x260 HILTI HAS 8.8 HDG INJEKTERAS MED HILTI HIT-CT 100. BORRDJUP ENLIGT LEVERANTÖRS ANVISNINGAR. 50 UNDERGJUTNING UNDER FOTPLÅT.
- M12 8.8 GÄNSTÅNG BOCKAS RUNT ÖVERRAM PÅ TRÄTAKSTOL
- PELARE PÅ SVETSPLÅT. SVETSDIMENSION ENLIGT STÅLELEVATIONER

a5 SVETS GÄLLER OM EJ ANNAT ANGES

FÖRESKRIFTER

K-01-0-001 -- 003 ALLMÄNNA FÖRESKRIFTER

HÄNVISNINGAR

-

SEKTION		
ORIENTERINGSFIGUR		
STATUS		
FÖRFRÅGNINGSUNDERLAG		
HANDLING		
BYGGHANDLING		
DATUM	2024-12-20	ADRESS
BESTÄLLARE	BJÖRN LIDSTRÖM	ANDRINGS FM
PROJEKTNAMN		
CENTRALEKÖK		
OMRÅDE		
ROBERTSFORS KOMMUN		
PROJEKTNUMMER	108 83 71	FASTIGHET
DIREKTOR	YTTRE RINGVÄGEN 4	FÖRETAG
DIREKTOR	FORDONET 1	NORCONSULT SVERIGE AB
UPPDRAGSNUMMER	108 83 71	SKAPAD AV
TELEFON	010-141 80 00	AWG/ATN
BYGGKOSTNAD	+45,540 (FG)	KONTAKTPERSON
VÄRNINGSPÅN	DEL 4, 5	BJÖRN LIDSTRÖM
SYSTEM		
24 STÅLKONSTRUKTIONER		
SPECIFIKATION		
STÅLELEVATIONER		
SKALA	1:50	FORMAT
DOCUMENTNUMMER	K-24-4-003	ANDRINGS

SKALA 1:50 0 1 5 METER