

FÖRKLARINGAR

- BEFINTLIG BYGGNAD
- 01

4 ST M20x260 HILTI HAS 8.8 HDG INJEKTERAS MED HILTI HIT-CT 100. BORRDJUP ENLIGT LEVERANTÖRS ANVISNINGAR. 50 UNDERGJUTNING UNDER FOTPLÅT.
- 02

M12 8.8 GÄNSTÅNG BOCKAS RUNT ÖVERRAM PÅ TRÅTAKSTOL
- 03


PELARE PÅ SVETSPLÅT. SVETSDIMENSION ENLIGT STÅLELEVATIONER
- a5 SVETS GÄLLER OM EJ ANNAT ANGES

FÖRESKRIFTER


K-01-0-001 -- 003 ALLMÄNNA FÖRESKRIFTER

HÄNVISNINGAR


-

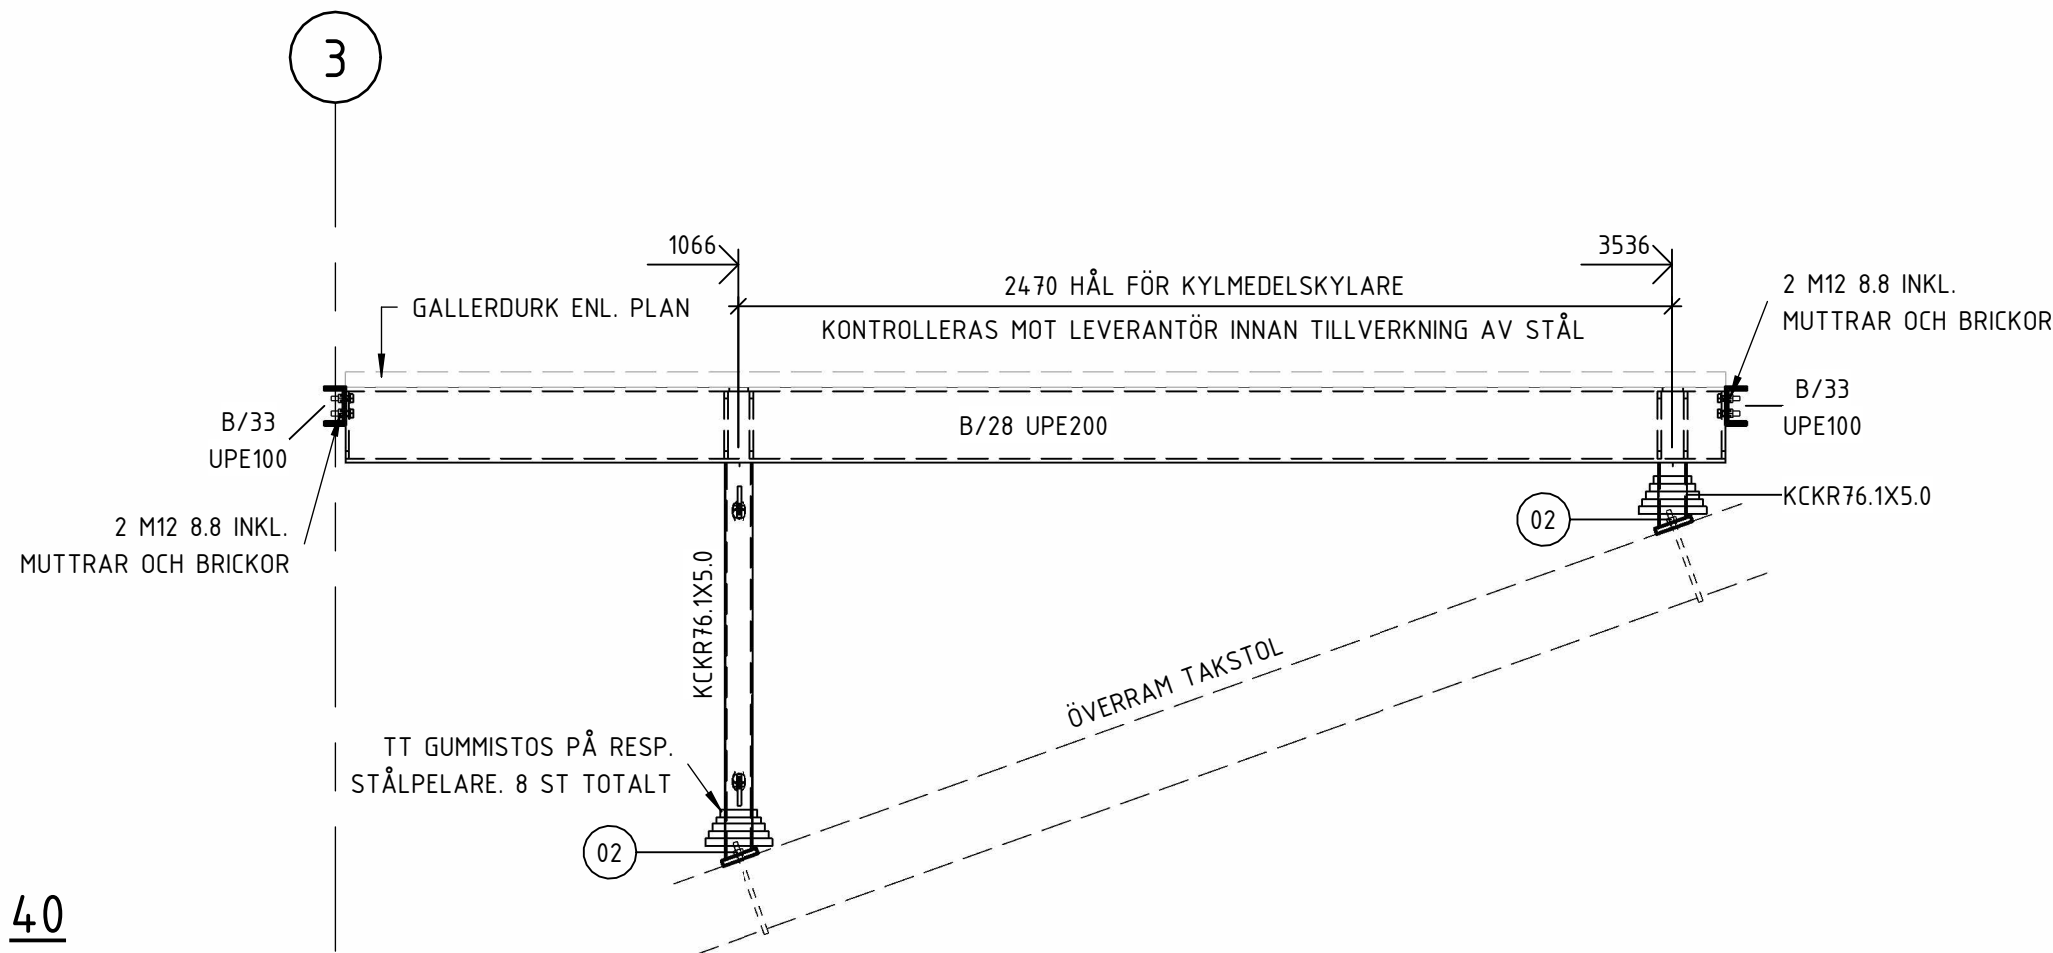

40
1 : 20
KYLMEDELSKYLARE

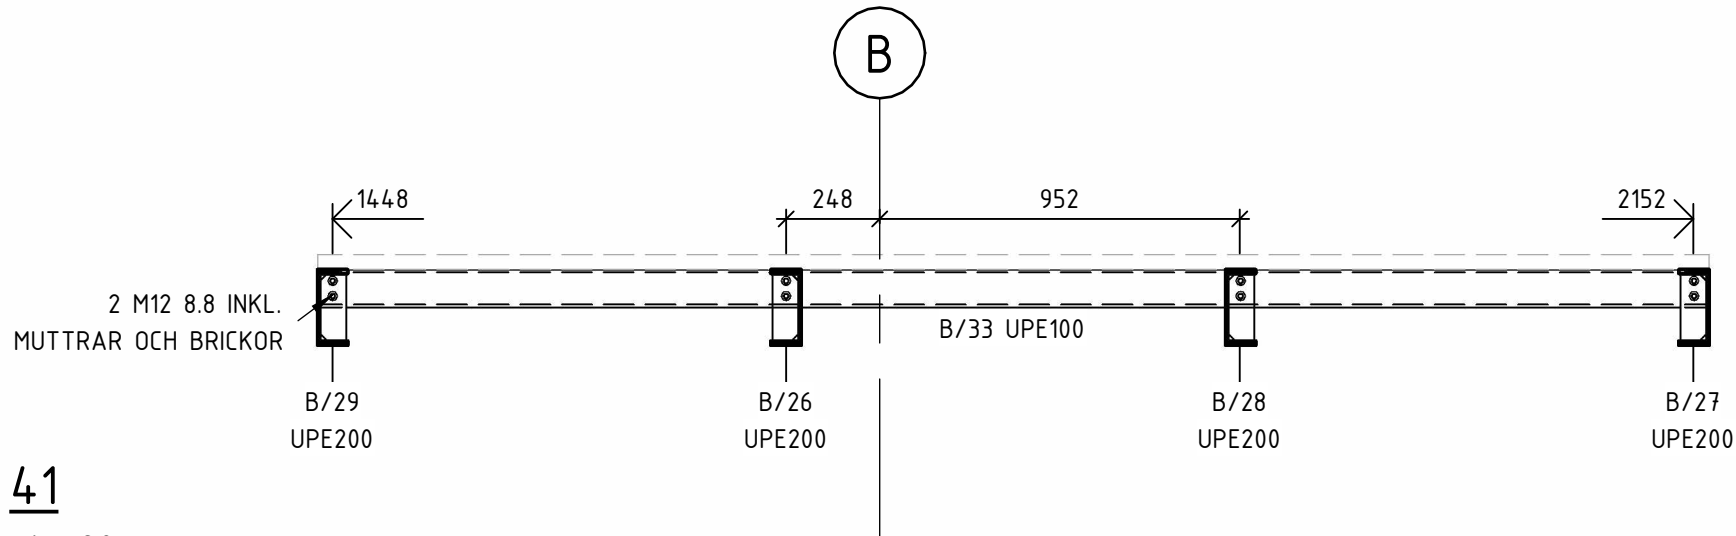

41
1 : 20
KYLMEDELSKYLARE

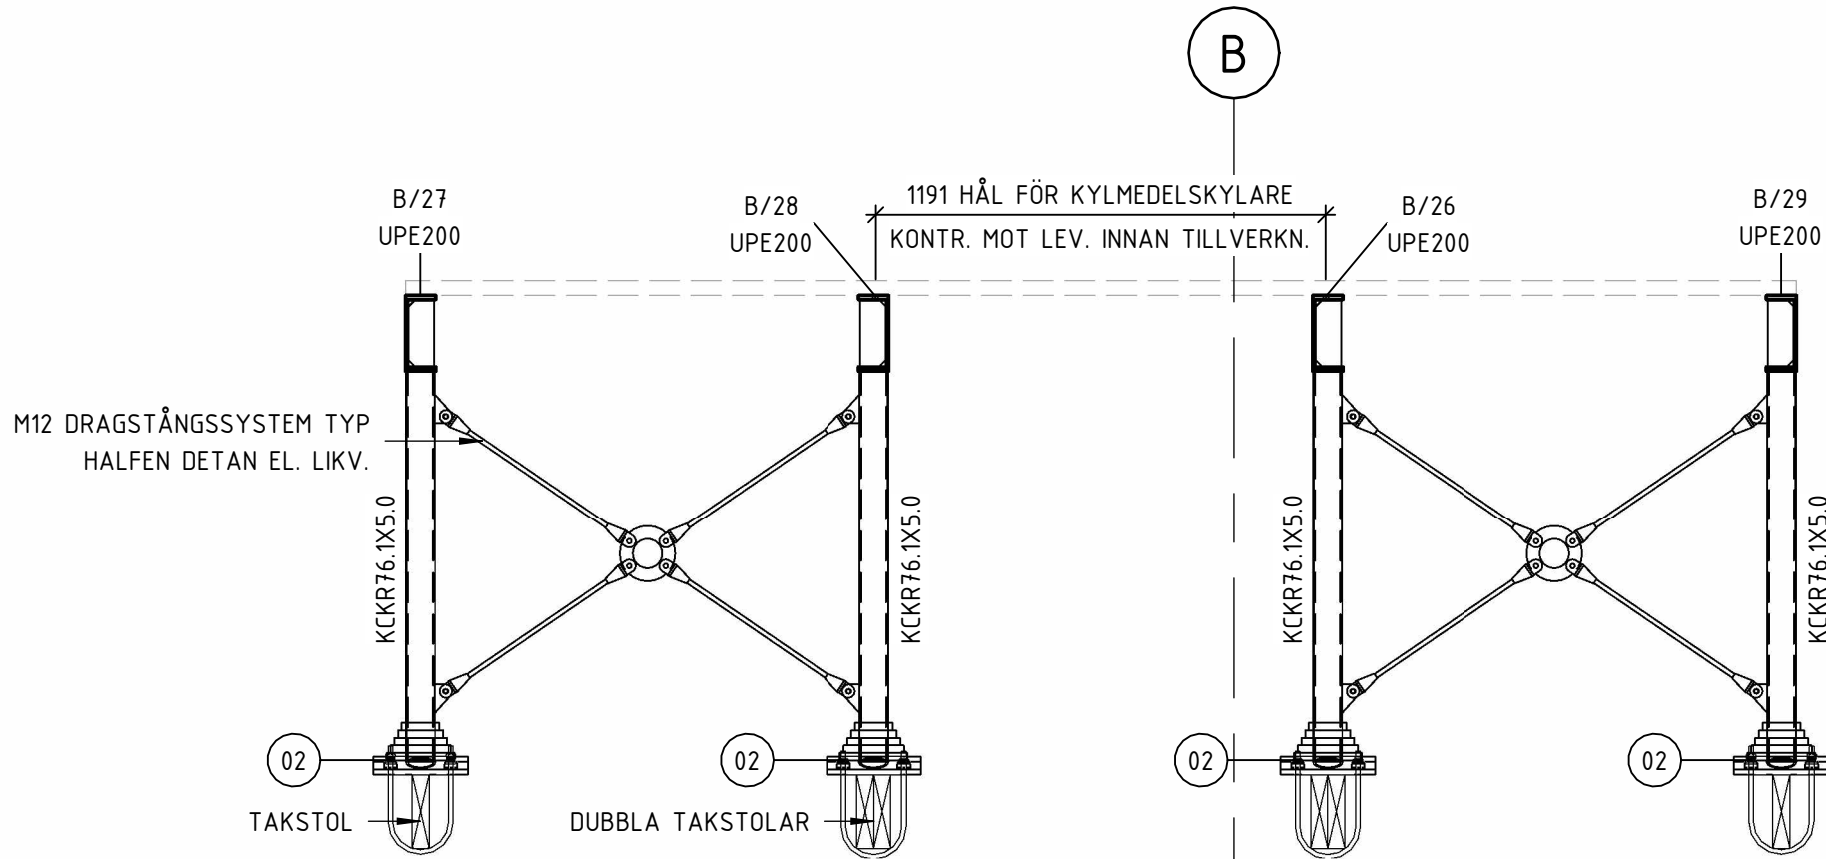

43
1 : 20
KYLMEDELSKYLARE

SKALA 1:20 0 1 2 METER

SEKTION

ORIENTERINGSGUR

STATUS

FÖRFRÅGNINGSUNDERLAG

HANDLING

BYGGHANDLING

DATUM

2024-12-20

ADRESS

BJÖRN LIDSTRÖM

ÄNDRINGS FM

BESTÄLLARE

PROJEKTNAMN

CENTRALEKÖK

ORAD

ROBERTSFORS KOMMUN

PROJEKTNUMMER

108 83 71

FASTIGHET

YTTRE RINGVÄGEN 4

DISCIPLIN

K

FÖRETAG

NORCONSULT SVERIGE AB

UPPDRAGSNUMMER

108 83 71

KONTAKTPERSON

AWG/ATN

TELEFON

010-141 80 00

BYGGGÅRSTID

+45,540 (FG)

VÄNINGSPLAN

DEL 4, 5

SYSTEM

24 STÅLKONSTRUKTIONER

SPECIFIKATION

STÅLELEVATIONER

SKALA

1:50

FORMAT

A1

ANORDNING

K-24-4-004