

FÖRKLARINGAR

BEFINTLIG BYGGNAD

PILMÅTT TAS FRÅN NÄRMAST LIGGANDE STOMLINJE (MINST 1 METER)


FÖRESKRIFTER

K-01-0-001 -- 005 ALLMÄNNA FÖRESKRIFTER

HÄNVISNINGAR

K-20-6-002 BYGGDETALJER TAK

K-25-4-001 -- 002 TAKSTOLSELEVATIONER

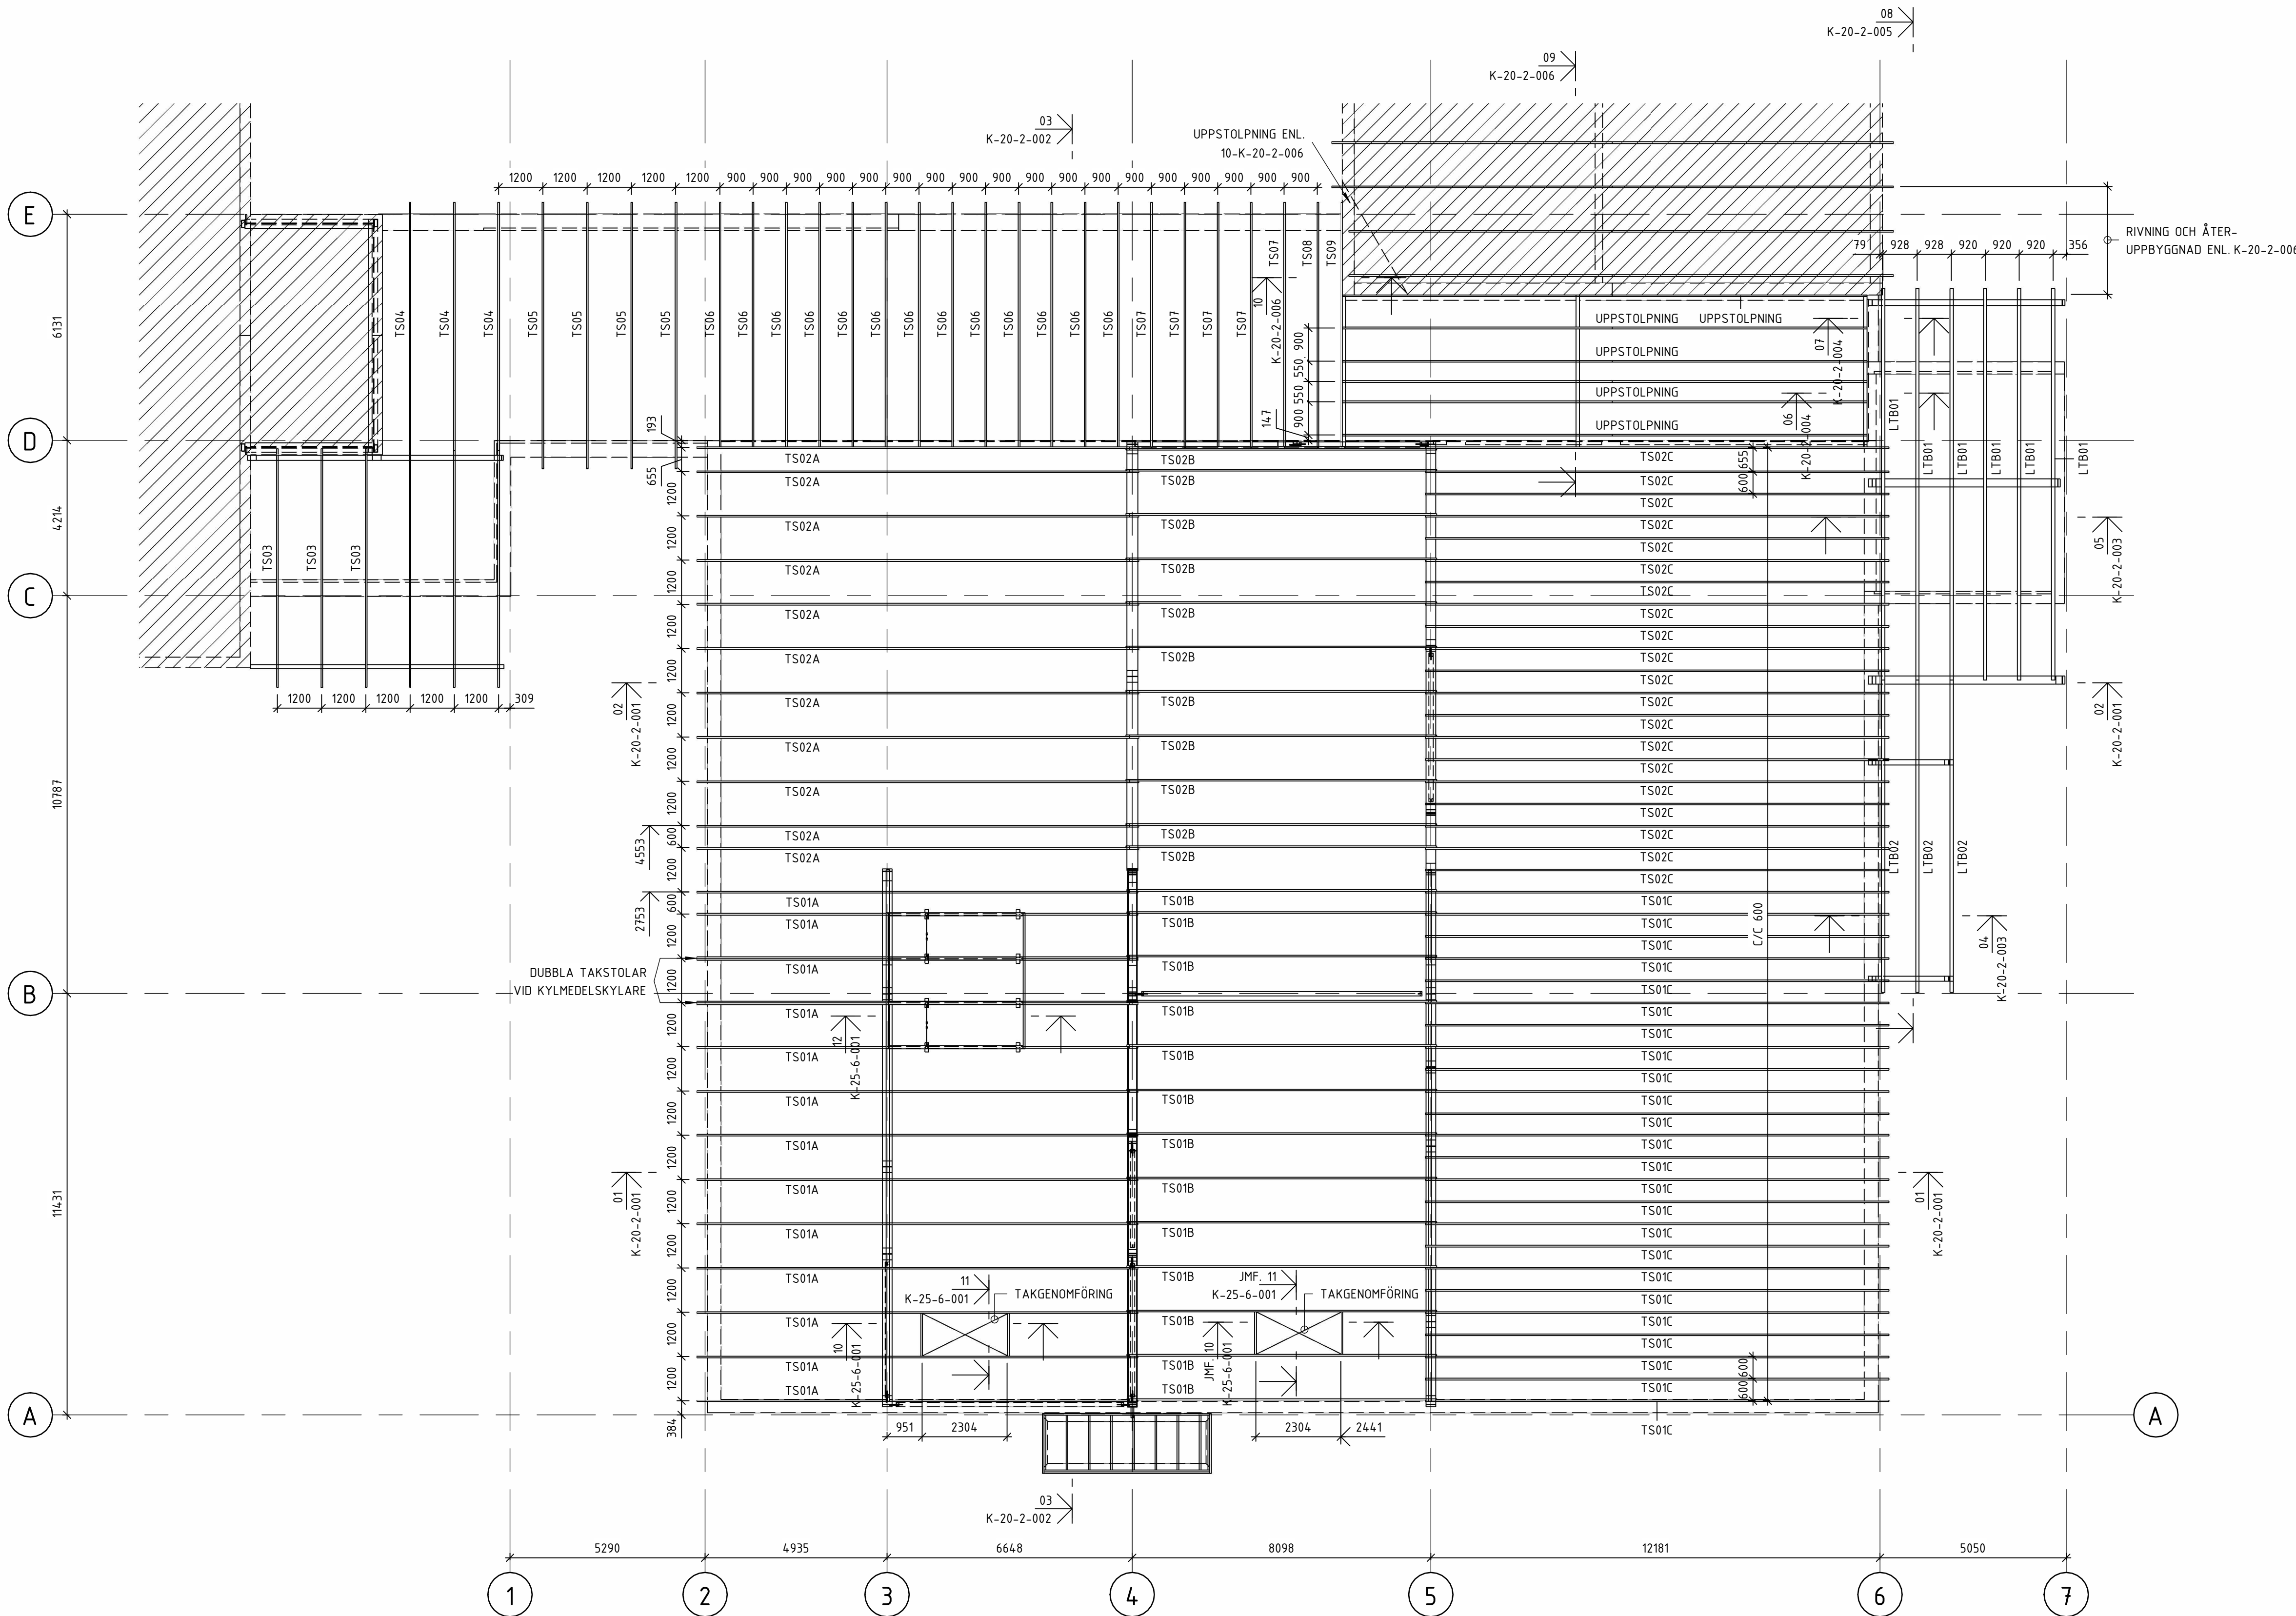

TAKPLAN ÖVERSIKT

1 : 100
VYRIKTNING NEDÅT

SKALA 1:100 0 1 10 METER

SEKTION

ORIENTERINGSFIGUR

STATUS

FÖRFRÅGNINGSUNDERLAG

HANDLING

BYGGHANDLING

DATUM: 2024-12-20

ANSÖKAN AV: BJÖRN LIDSTRÖM

ANDRINGS PM

BESTÄLLARE

PROJEKTNAMN

CENTRALEKÖ

OMRÅDE

ROBERTSFORS KOMMUN

PROJEKTNUMMER: 108 83 71

FASTIGHET: YTTRE RINGVÄGEN 4

DIREKTÖR: FORDONET 1

DISCIPLIN: K

FÖRETAG: NORCONSULT SVERIGE AB

UPPDRAGSNUMMER: 108 83 71

SKAPAD AV: AWG/ATN

TELEFON: 010-141 80 00

KONTAKTPERSON: BJÖRN LIDSTRÖM

BYGGGÅRSTID: +45,540 (FG)

VÄNINGSPLAN: DEL 4, 5

SYSTEM: 25 TRÄKONSTRUKTIONER

SPECIFIKATION: TAKPLAN

UTRINNINGSDOKUMENT: PLAN

SKALA: 1:100

FORMAT: A1

ANDRINGS: K-25-1-100