
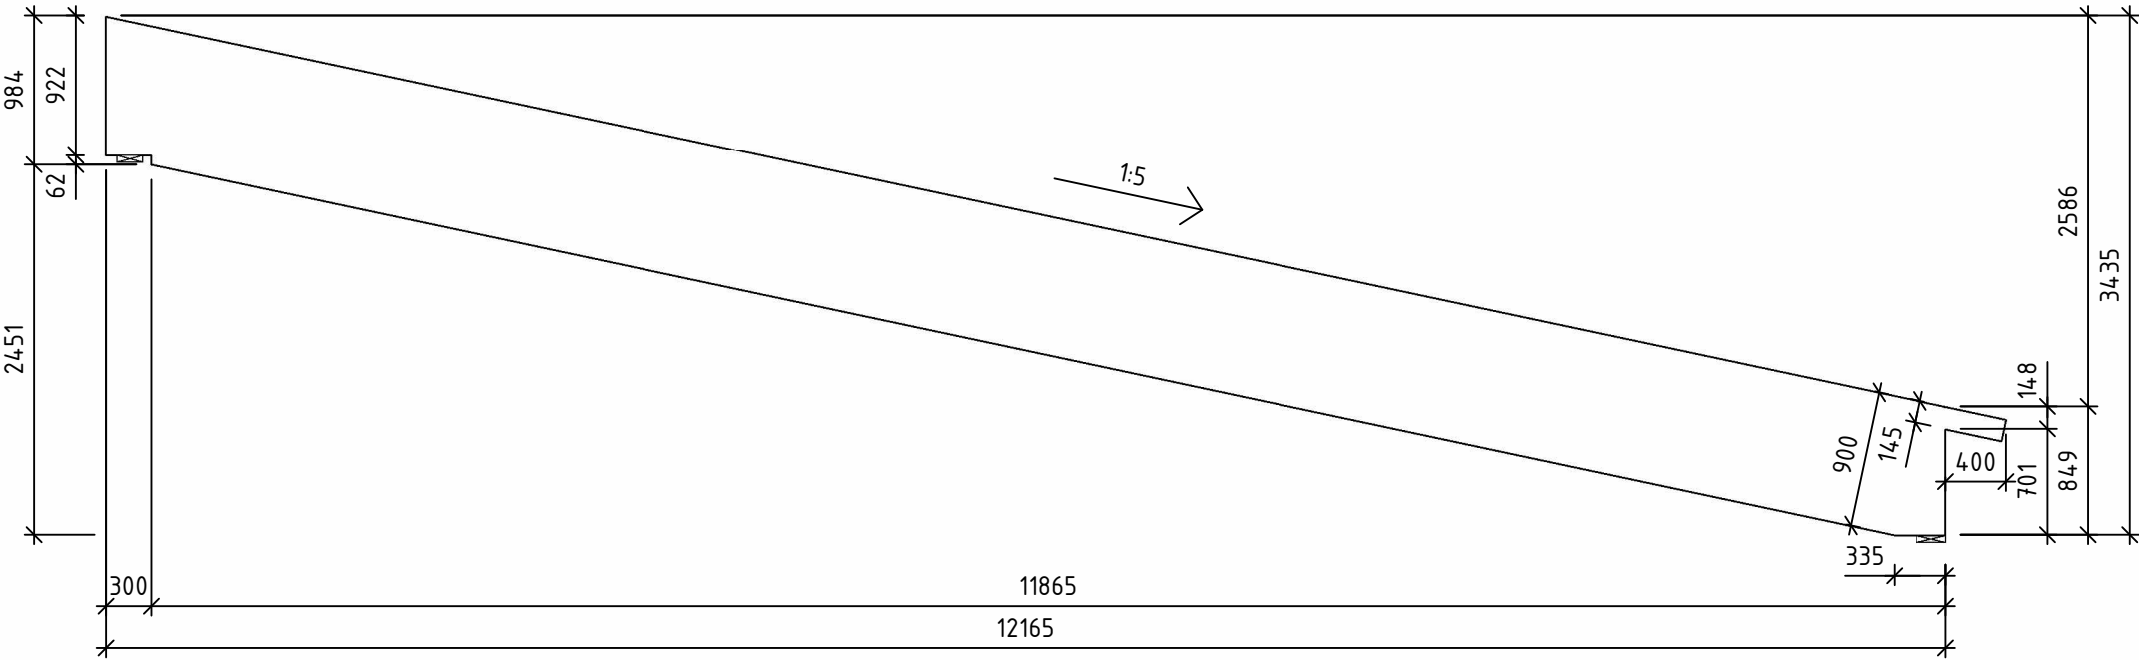
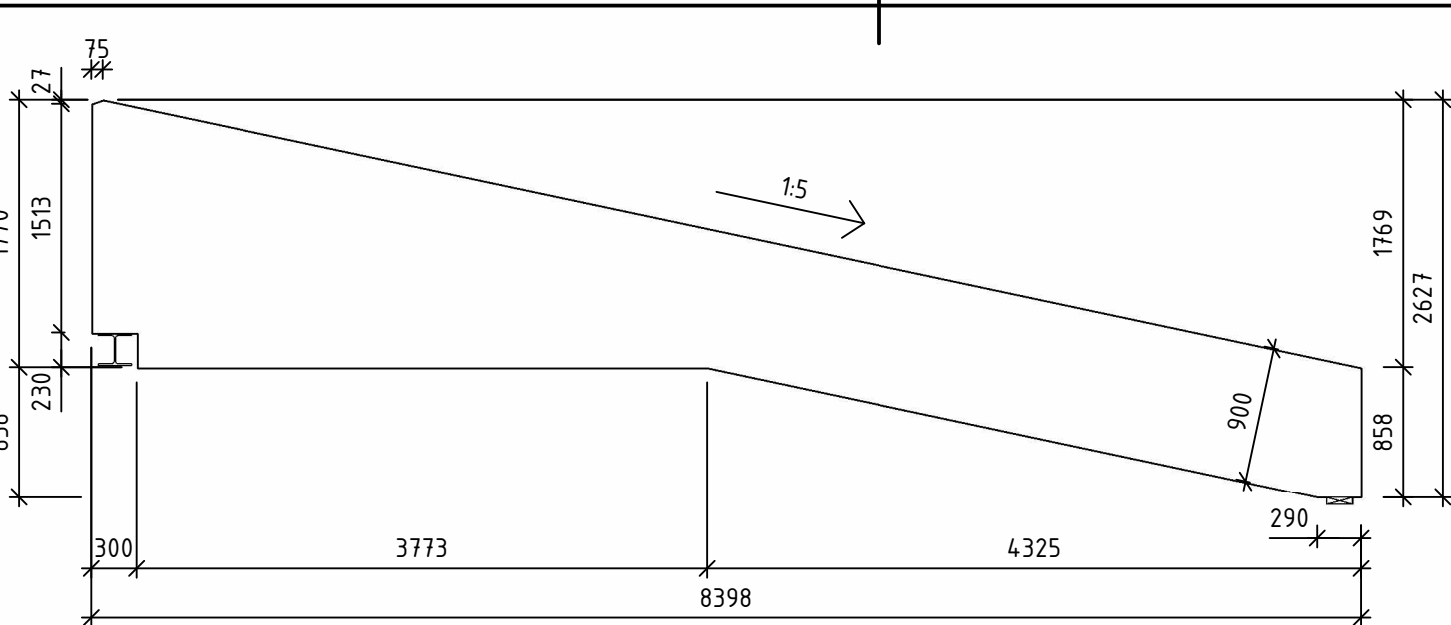


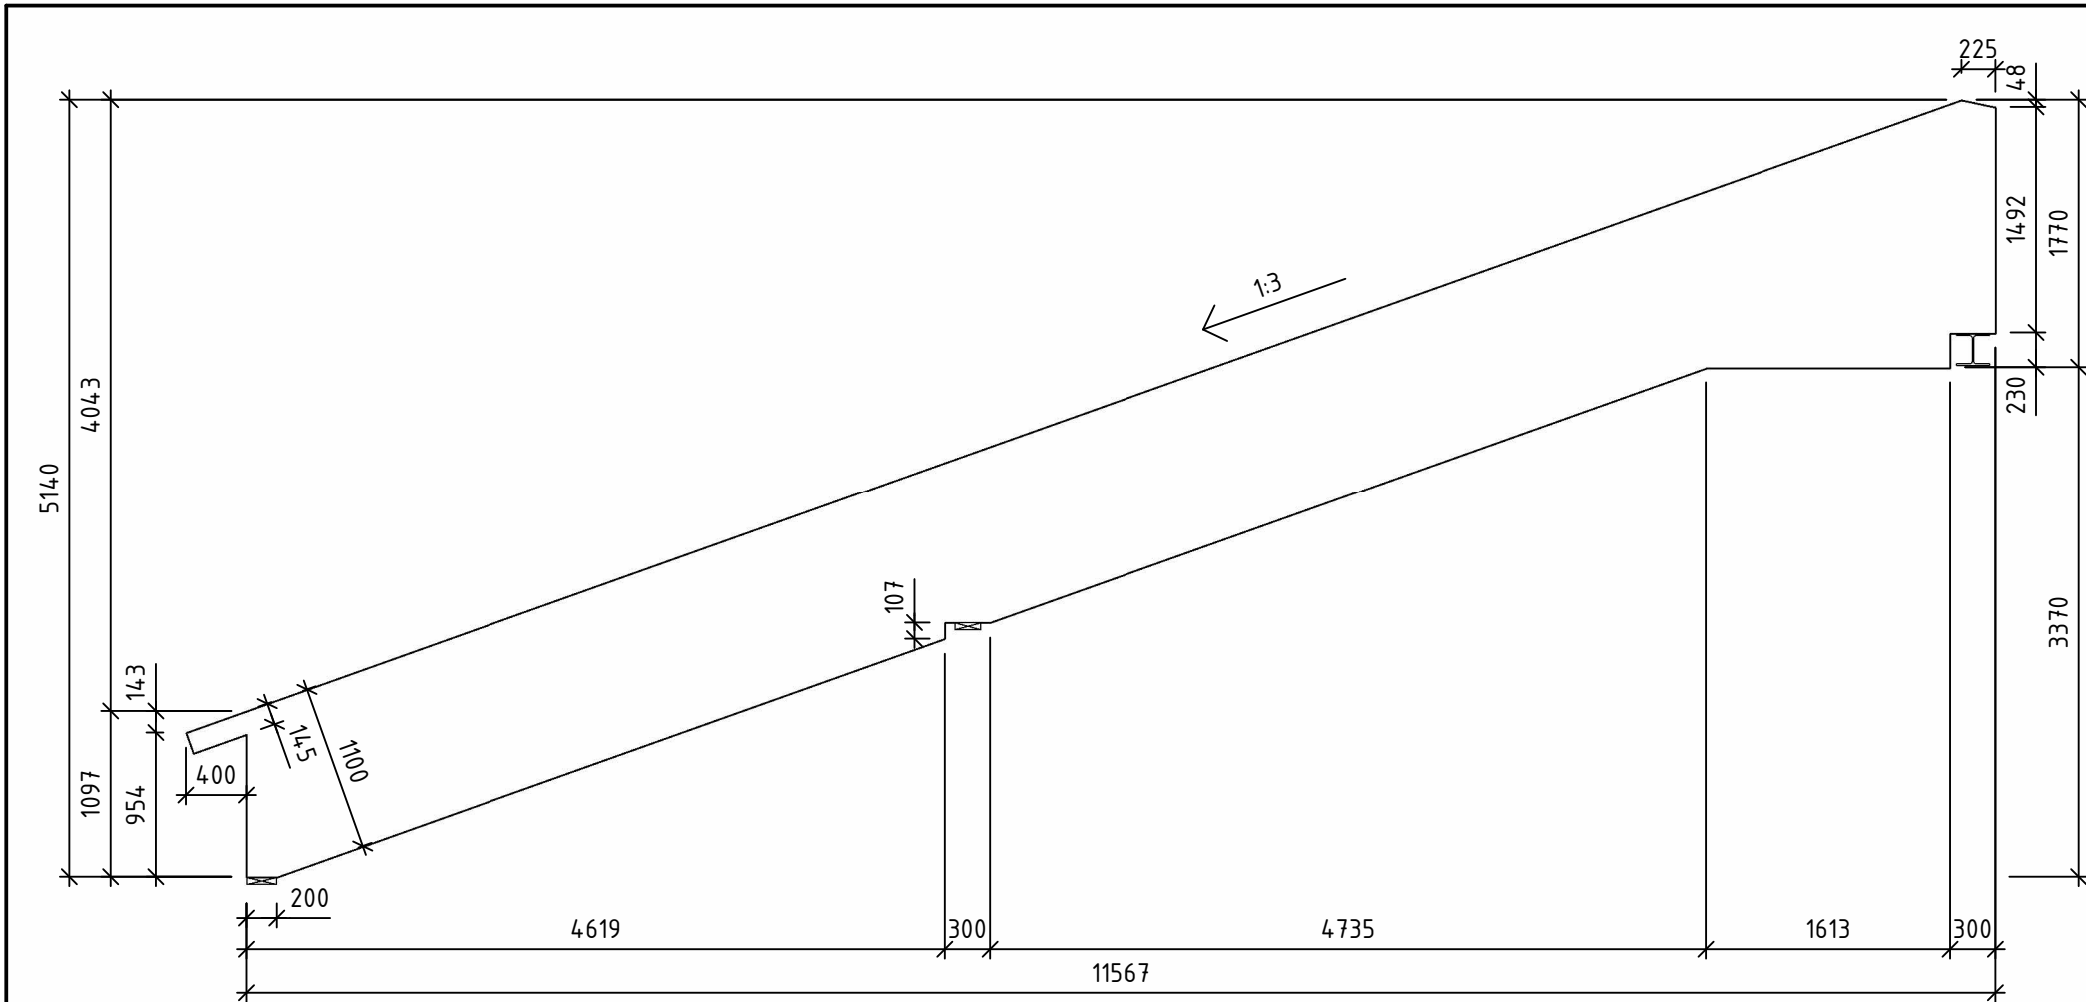

TS01A




1 : 50
15 ST

TS01B

1 : 50
13 ST

TS01C

1 : 50
24 ST

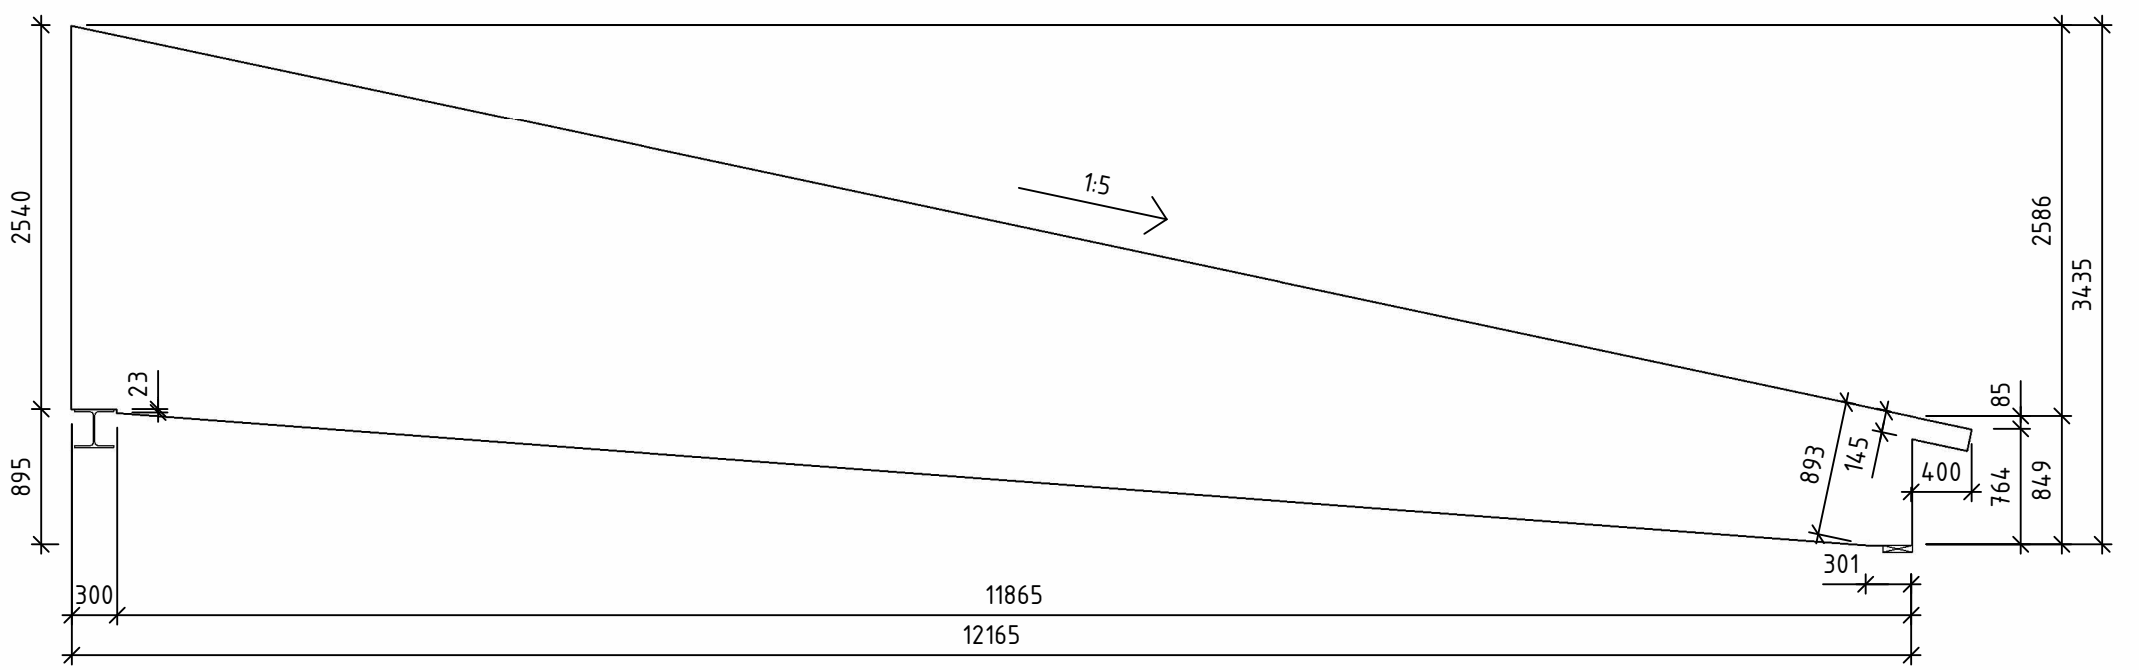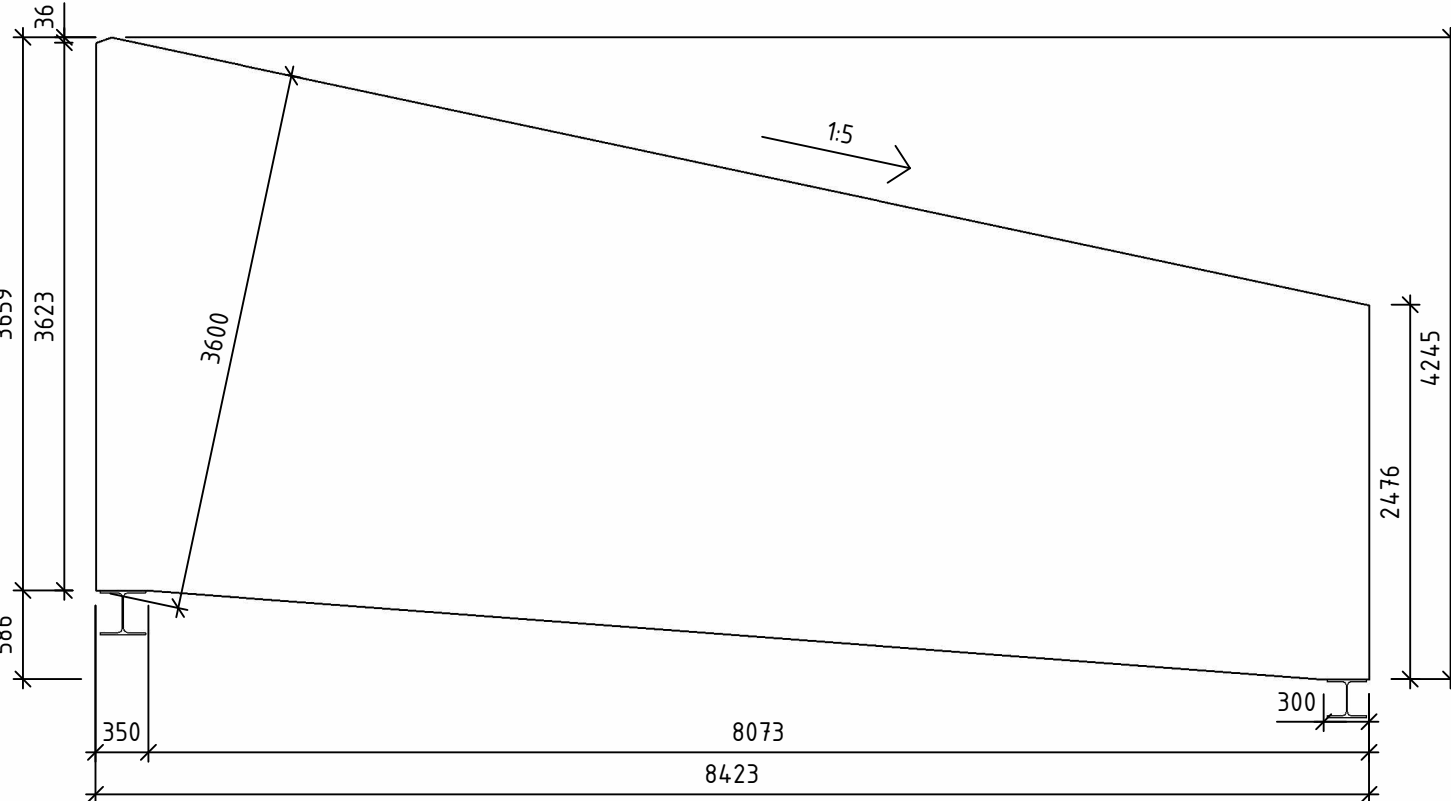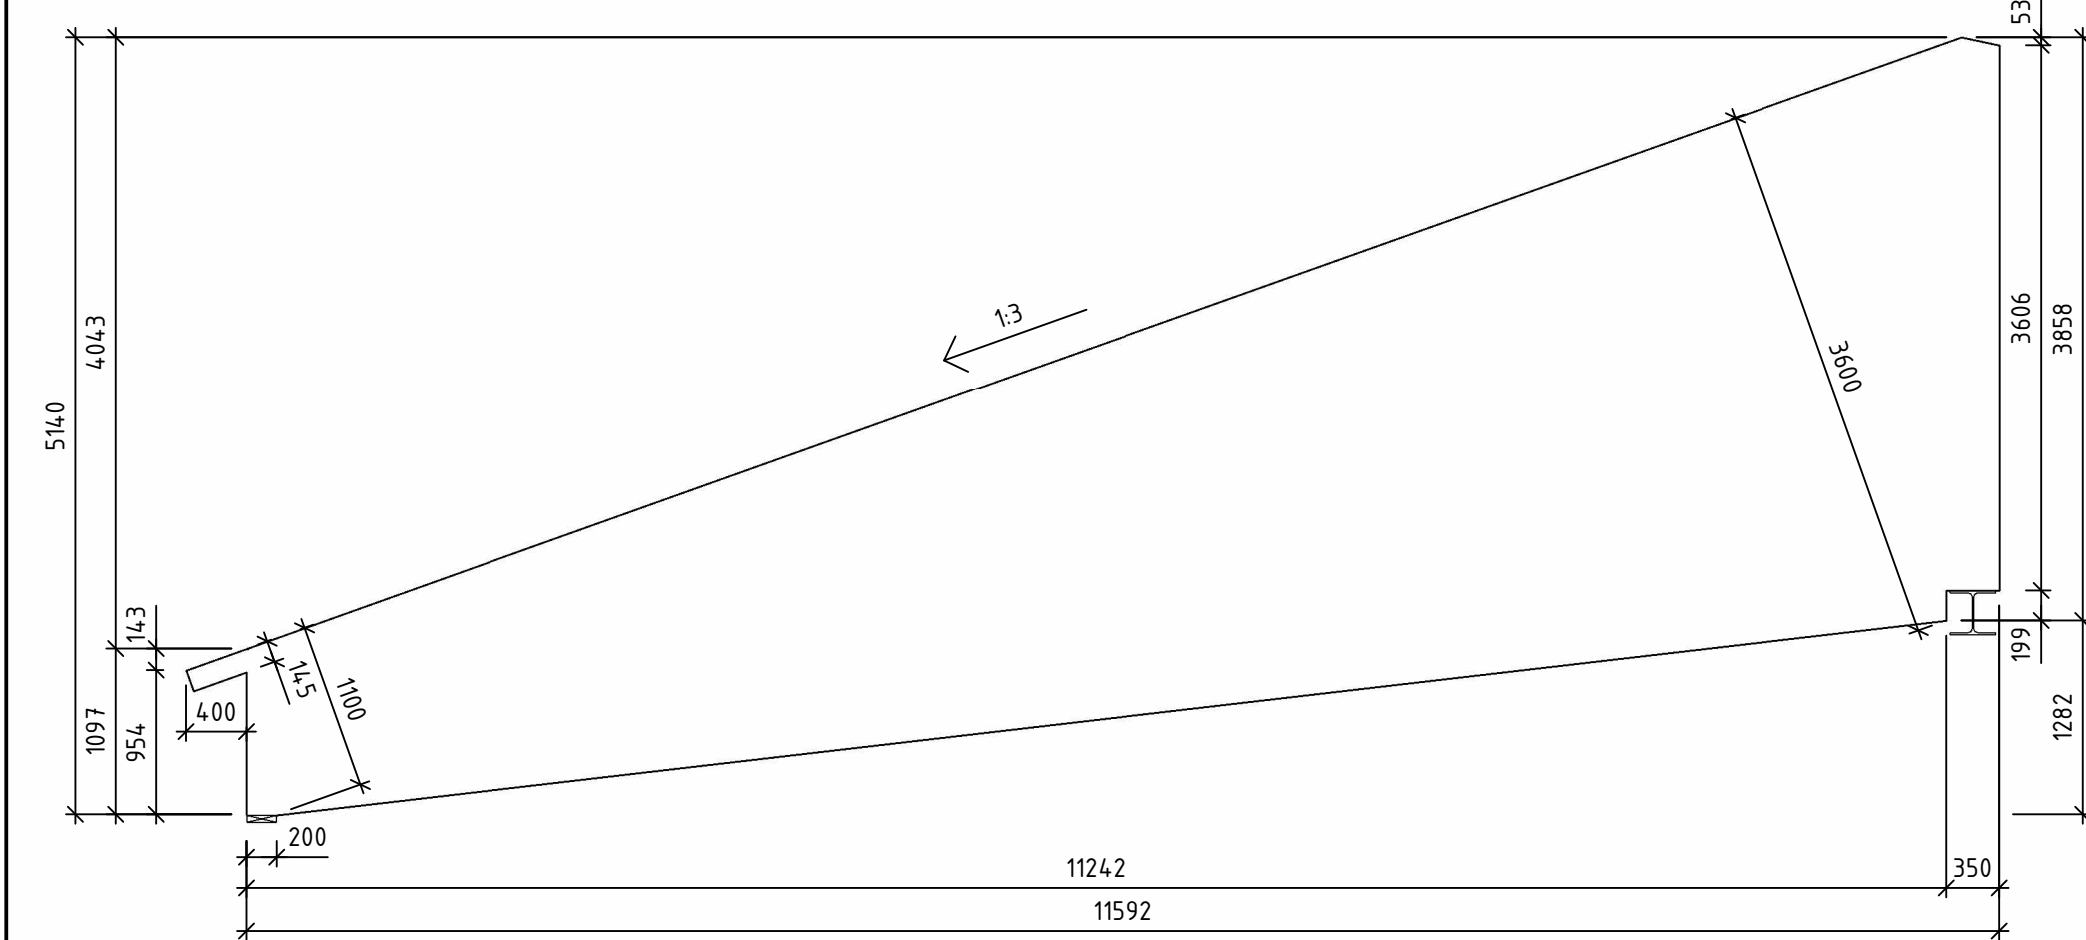

TS02A

1 : 50
11 ST

TS02B

1 : 50
11 ST

TS02C

1 : 50
20 ST

FÖRKLARINGAR

FÖRESKRIFTER

K-01-0-001 -- 003 ALLMÄNNA FÖRESKRIFTER

EGENTYNGDER
TAK 0,5 kN/m²
INSTALLATIONER 0,4 kN/m²


VARIABLA LASTER
SNÖLAST SNÖZON 3,0 kN/m², SNÖFICKOR
BEAKTAS
VINDLAST V_{REF} 22 m/s, TERRÄNGTYP II

LASTBREDDER
LASTBREDDER FÖR TAKSTOLSTYPER ANGES I TAKPLAN
HÄNVISAT NEDAN.

I ÖVRIGT, SE ALLMÄNNA FÖRESKRIFTER.


HÄNVISNINGAR

K-25-1-100 TAKPLAN

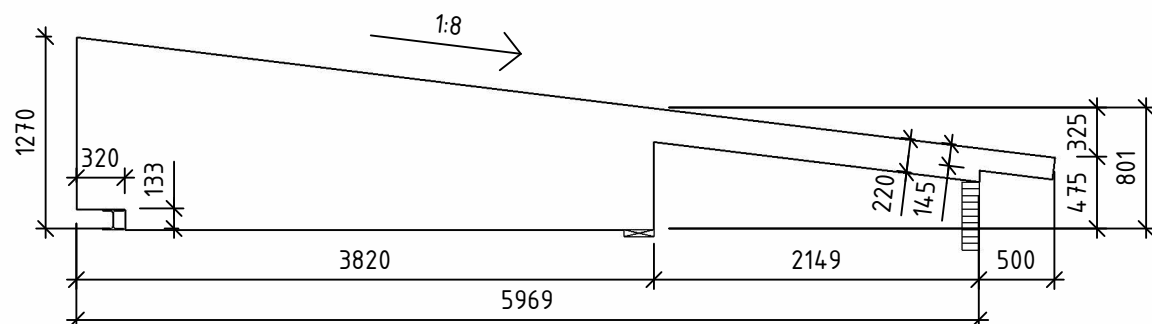


TS03

1 : 50
3 ST

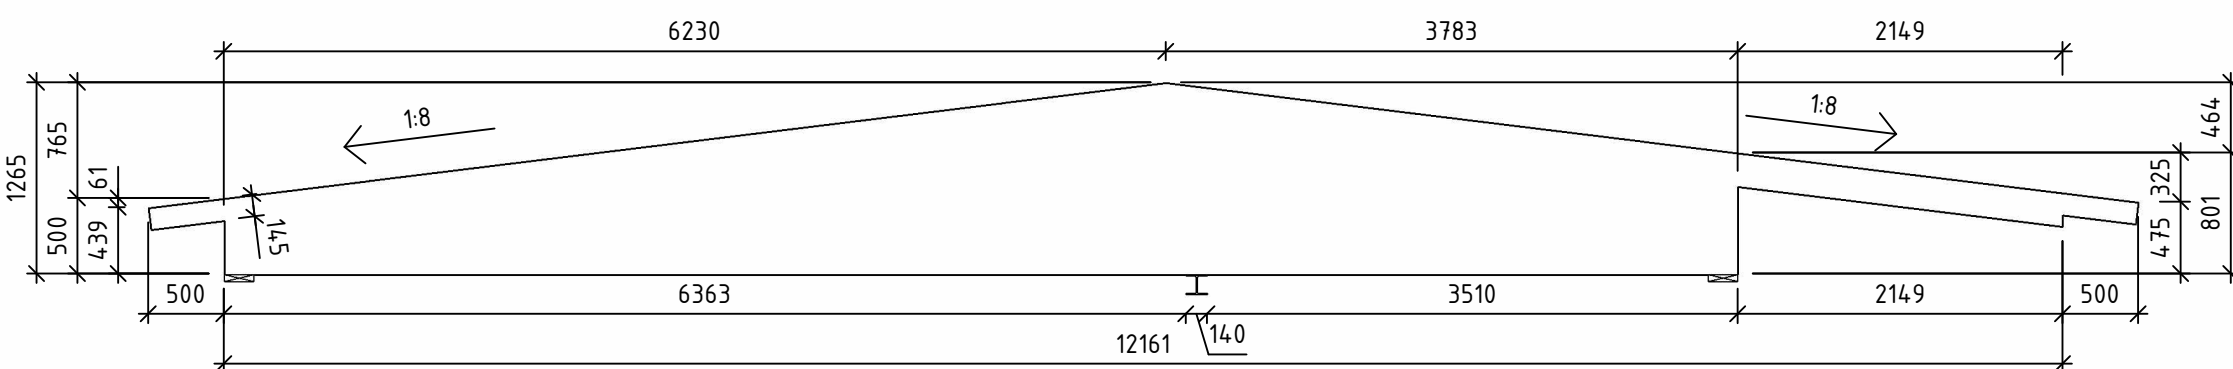


TS04

1 : 50
3 ST

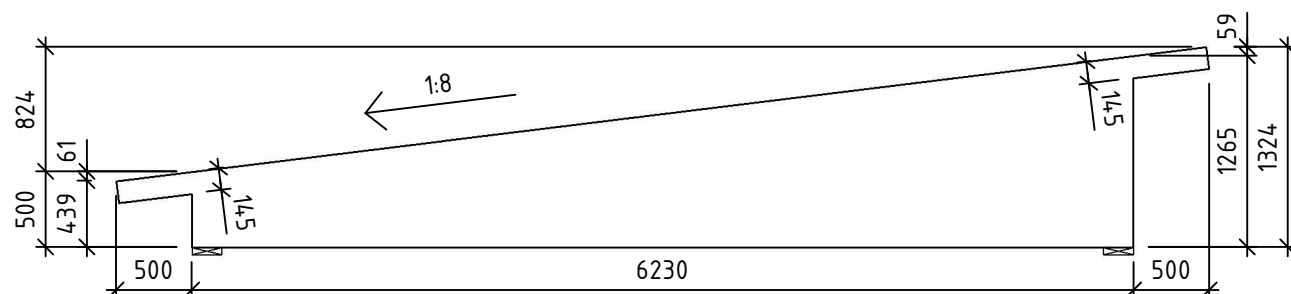


TS05

1 : 50
4 ST

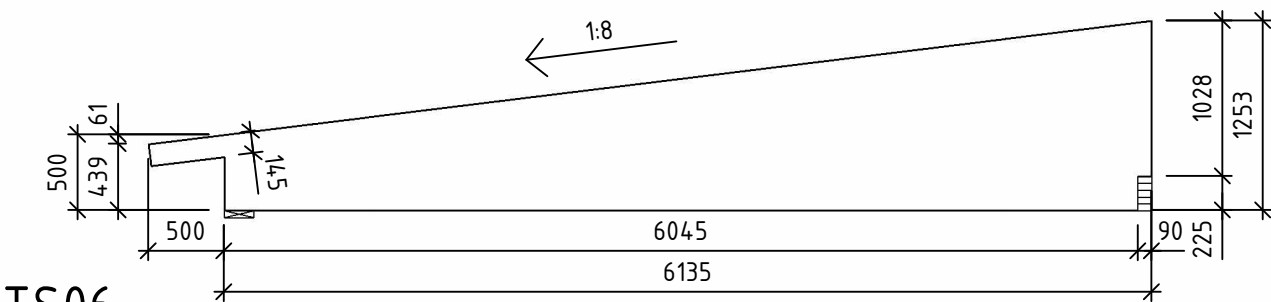


TS06

1 : 50
13 ST

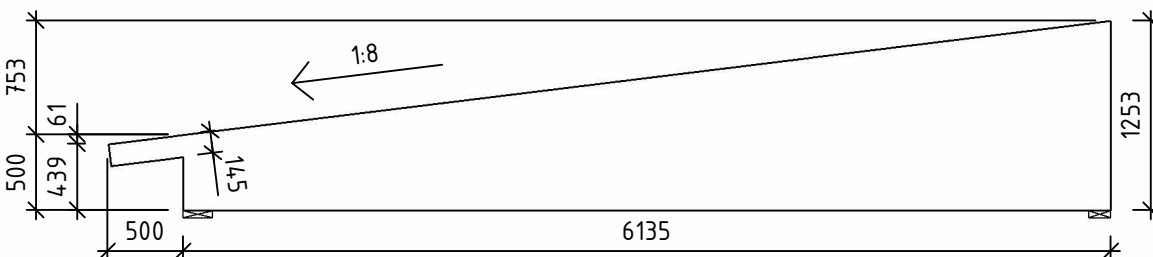


TS07

1 : 50
5 ST

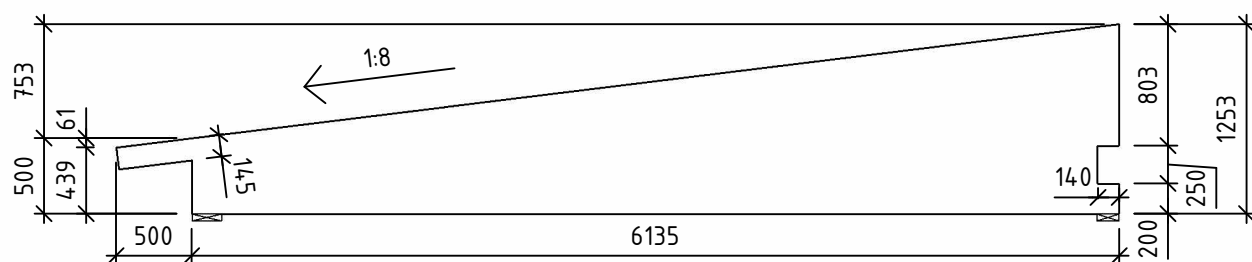


TS08

1 : 50
1 ST

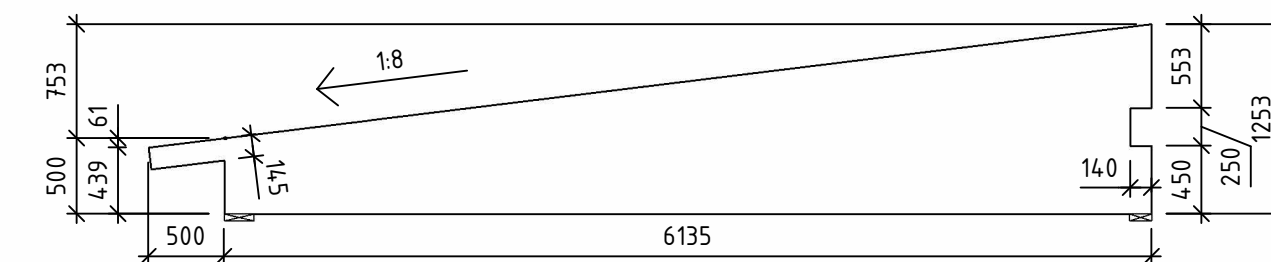


TS09

1 : 50
1 ST

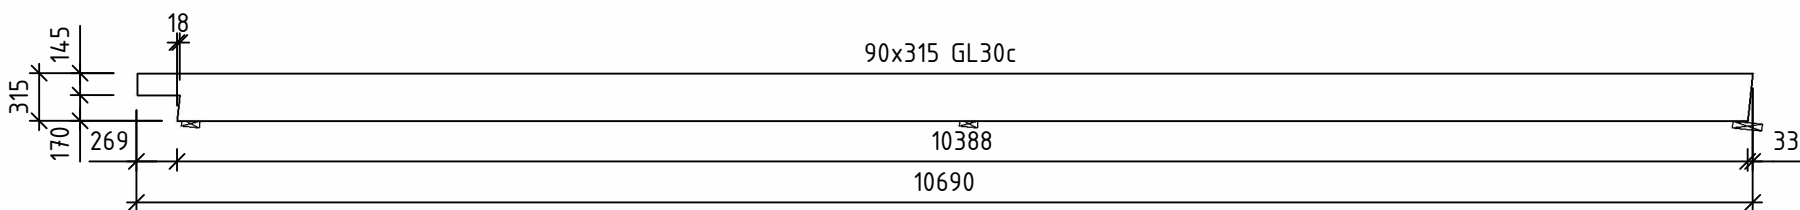


LTB01

1 : 50
6 ST

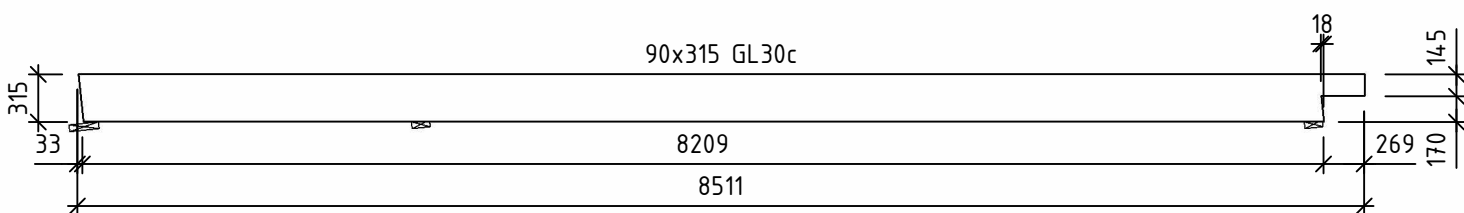

LTB02

1 : 50
3 ST

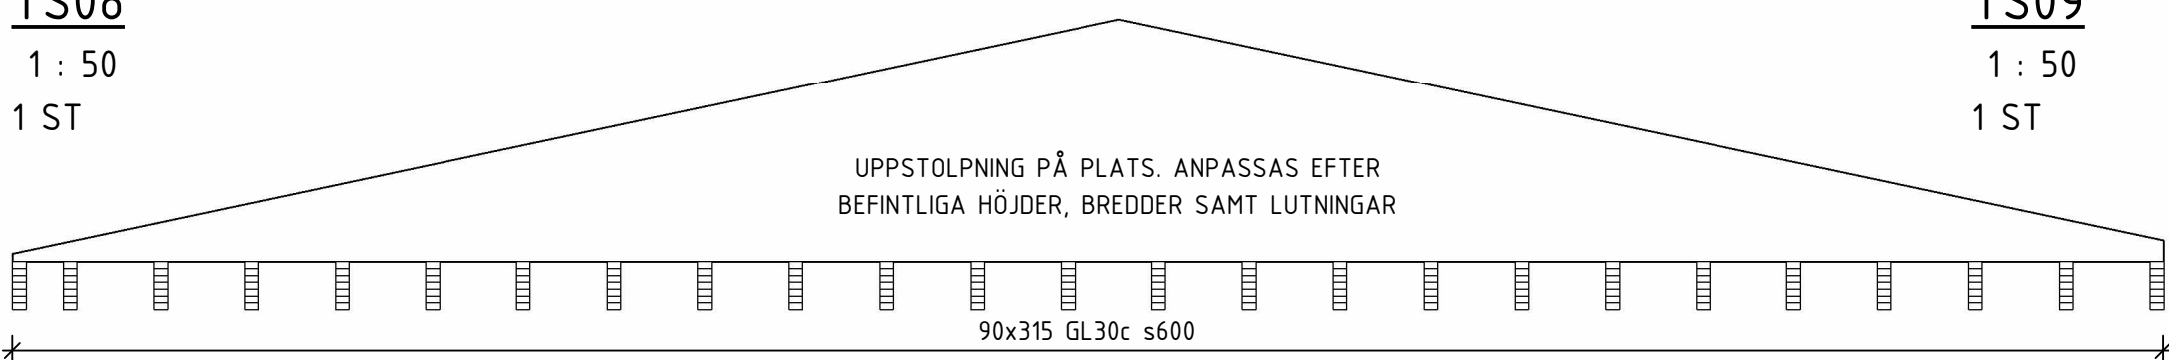

UPPSTOLPNING

1 : 50
6 ST

SKALA 1:50 0 1 5 METER

SEKTION

ORIENTERINGSSKISS

STATUS

FÖRFRÅGNINGSUNDERLAG

HANDLING

BYGGHANDLING

DATUM

2024-12-20

ANSÖKAN AV

BJÖRN LIDSTRÖM

ÄNDRINGS PM

BESTÄLLARE

ROBERTSFORS KOMMUN

PROJEKTNAMN

CENTRALEKÖ

KOMMUNE

ROBERTSFORS KOMMUN

PROJEKTNUMMER

108 83 71

FASTIGHET

YTRE RINGVÄGEN 4

DOKUMENTNUMMER

FORDONET 1

DISCIPLIN

K

FÖRETAG

NORCONSULT SVERIGE AB

UPPDRAGSNUMMER

108 83 71

KONTAKTPERSON

AWG/ATN

TELEFON

010-141 80 00

TELEFON (HJÄLP)

+45 540 (FG)

VÄRNINGSPÅN

DELNING

DEL 4, 5

SYSTEM

25 TRÄKONSTRUKTIONER

SPECIFIKATION

TAKSTOLSELEVATIONER

ELEVATION

SKALA

1:50

FORMAT

A1

DOKUMENTNUMMER

K-25-4-001

ÄNDRING