

FÖRKLARINGAR


-

FÖRESKRIFTER

K-01-0-001 -- 005 ALLMÄNNA FÖRESKRIFTER

HÄNVISNINGAR

-

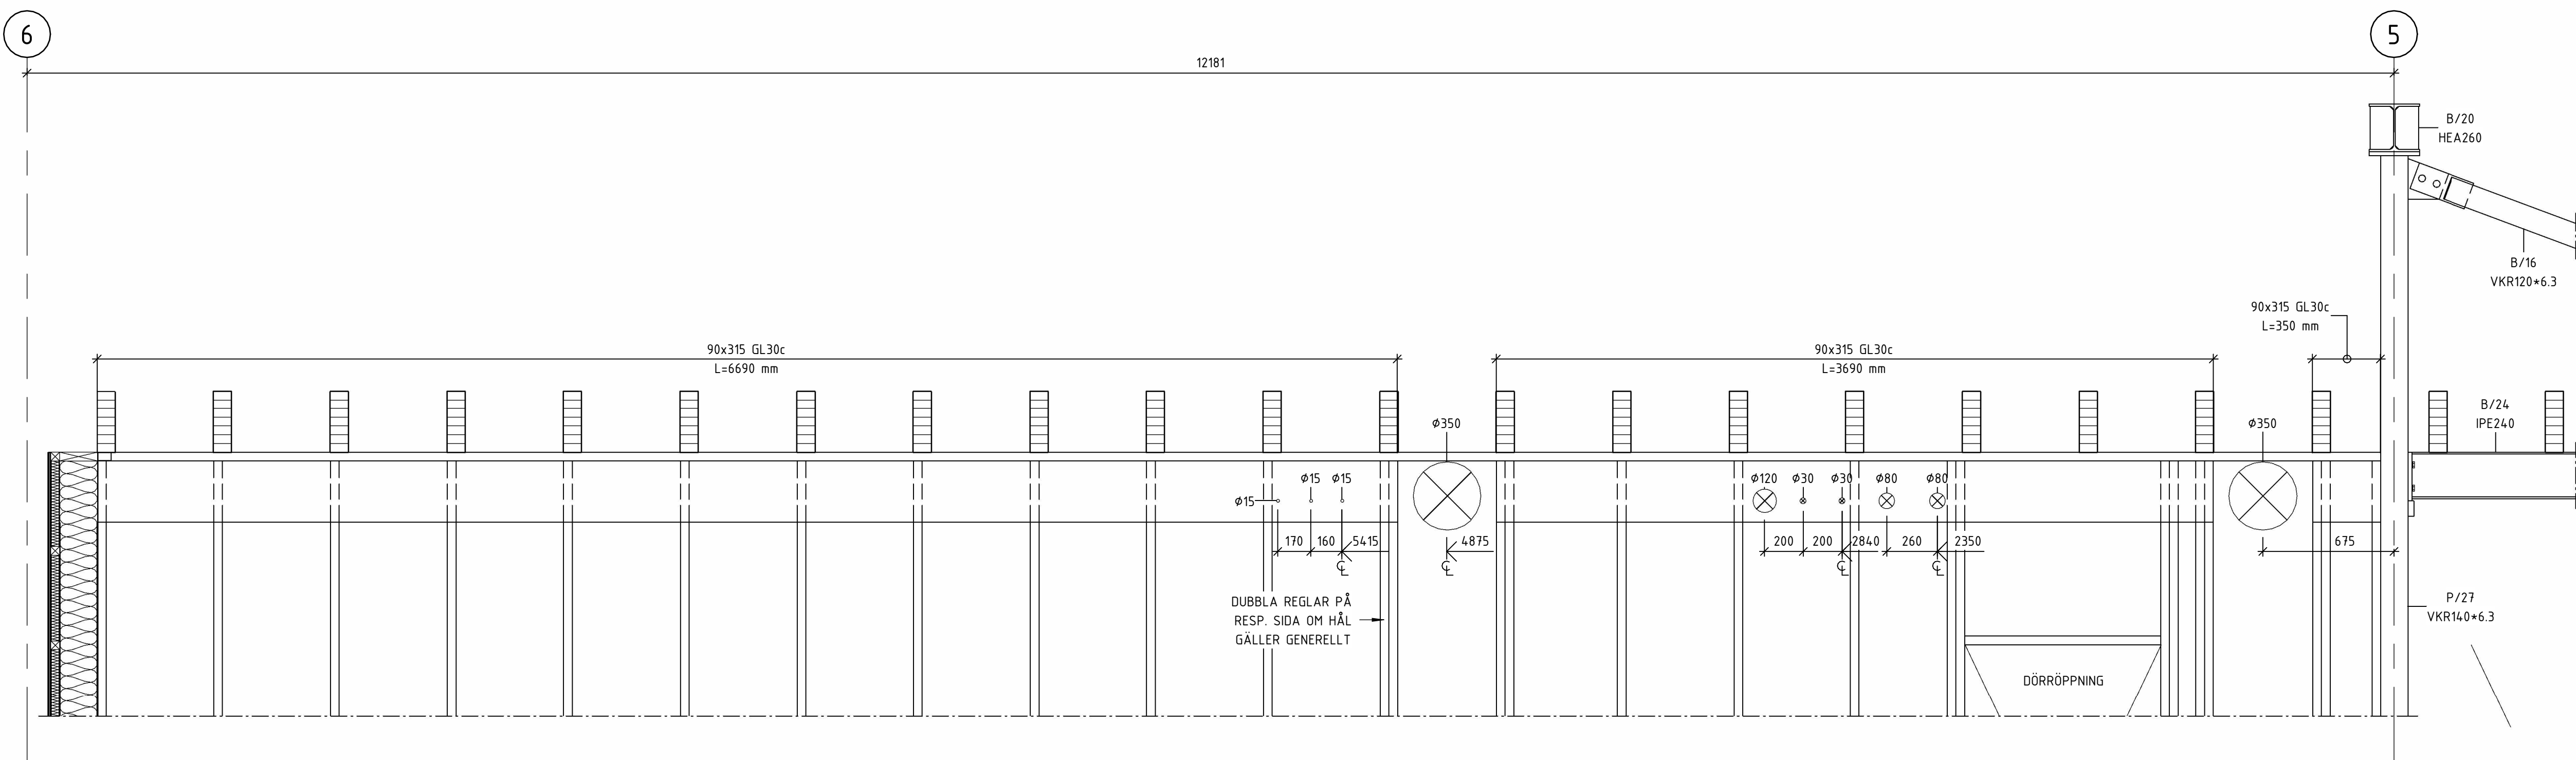


01 HÅLTAGNING BÄRLINA

1 : 20

BÄRLINA LINJE D MELLAN LINJE 5-6

SKALA 1:20 0 1 2 METER

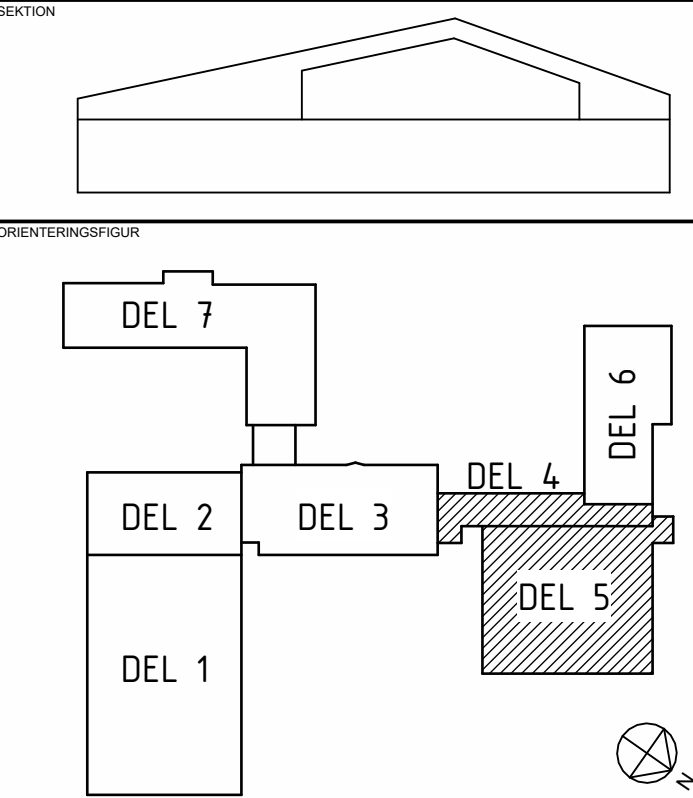

STATUS FÖRFRÅGNINGSUNDERLAG

HANDLING BYGGHANDLING

DATUM: 2024-12-20 ADRESS: BJÖRN LIDSTRÖM



PROJEKTNAMN CENTRALEKÖ

KOMMUNE ROBERTSFORS KOMMUN

PROJEKTNUMMER: 108 83 71 YTTRE RINGVÄGEN 4

DOKUMENTNUMMER: FORDONET 1

DISCIPLIN: K FÖRETAG: NORCONSULT SVERIGE AB

UPPDRAGSNUMMER: 108 83 71 SKAPAD AV: AWG/ATN

TELEFON: 010-141 80 00 BJÖRN LIDSTRÖM

BYGGKOSTNAD: +45,540 (FG)

VÄNINGSPLAN: VÄNINGSDEL: DEL 4, 5

SYSTEM: 25 TRÄKONSTRUKTIONER

SPESIFIKATION: HÅLTAGNING BÄRLINA

ELEVATION: SKALA: 1:50 FORMAT: A1

DOKUMENTNUMMER: K-25-4-002