

FÖRKLARINGAR

BEFINTLIG BYGGNAD

PILMÅTT TAS FRÅN NÄRMAST LIGGANDE STOMLINJE (MINST 1 METER)

INNERDÖRRAR OCH FÖNSTER VISAS ENDAST SCHEMATISKT I SAMTLIGA K-HANDLINGAR. FÖR EXAKT PLACERING OCH MÄTTSÄTTNING, SE A-HANDLINGAR.


DUBBLA VÄGGREGLAR PLACERAS PÅ RESPEKTIVE SIDA OM SAMTLIGA DÖRRAR OCH FÖNSTER OM EJ ANNAT ANGES.

FÖRESKRIFTER


K-01-0-001 -- 003 ALLMÄNNA FÖRESKRIFTER

HÄNVISNINGAR


-

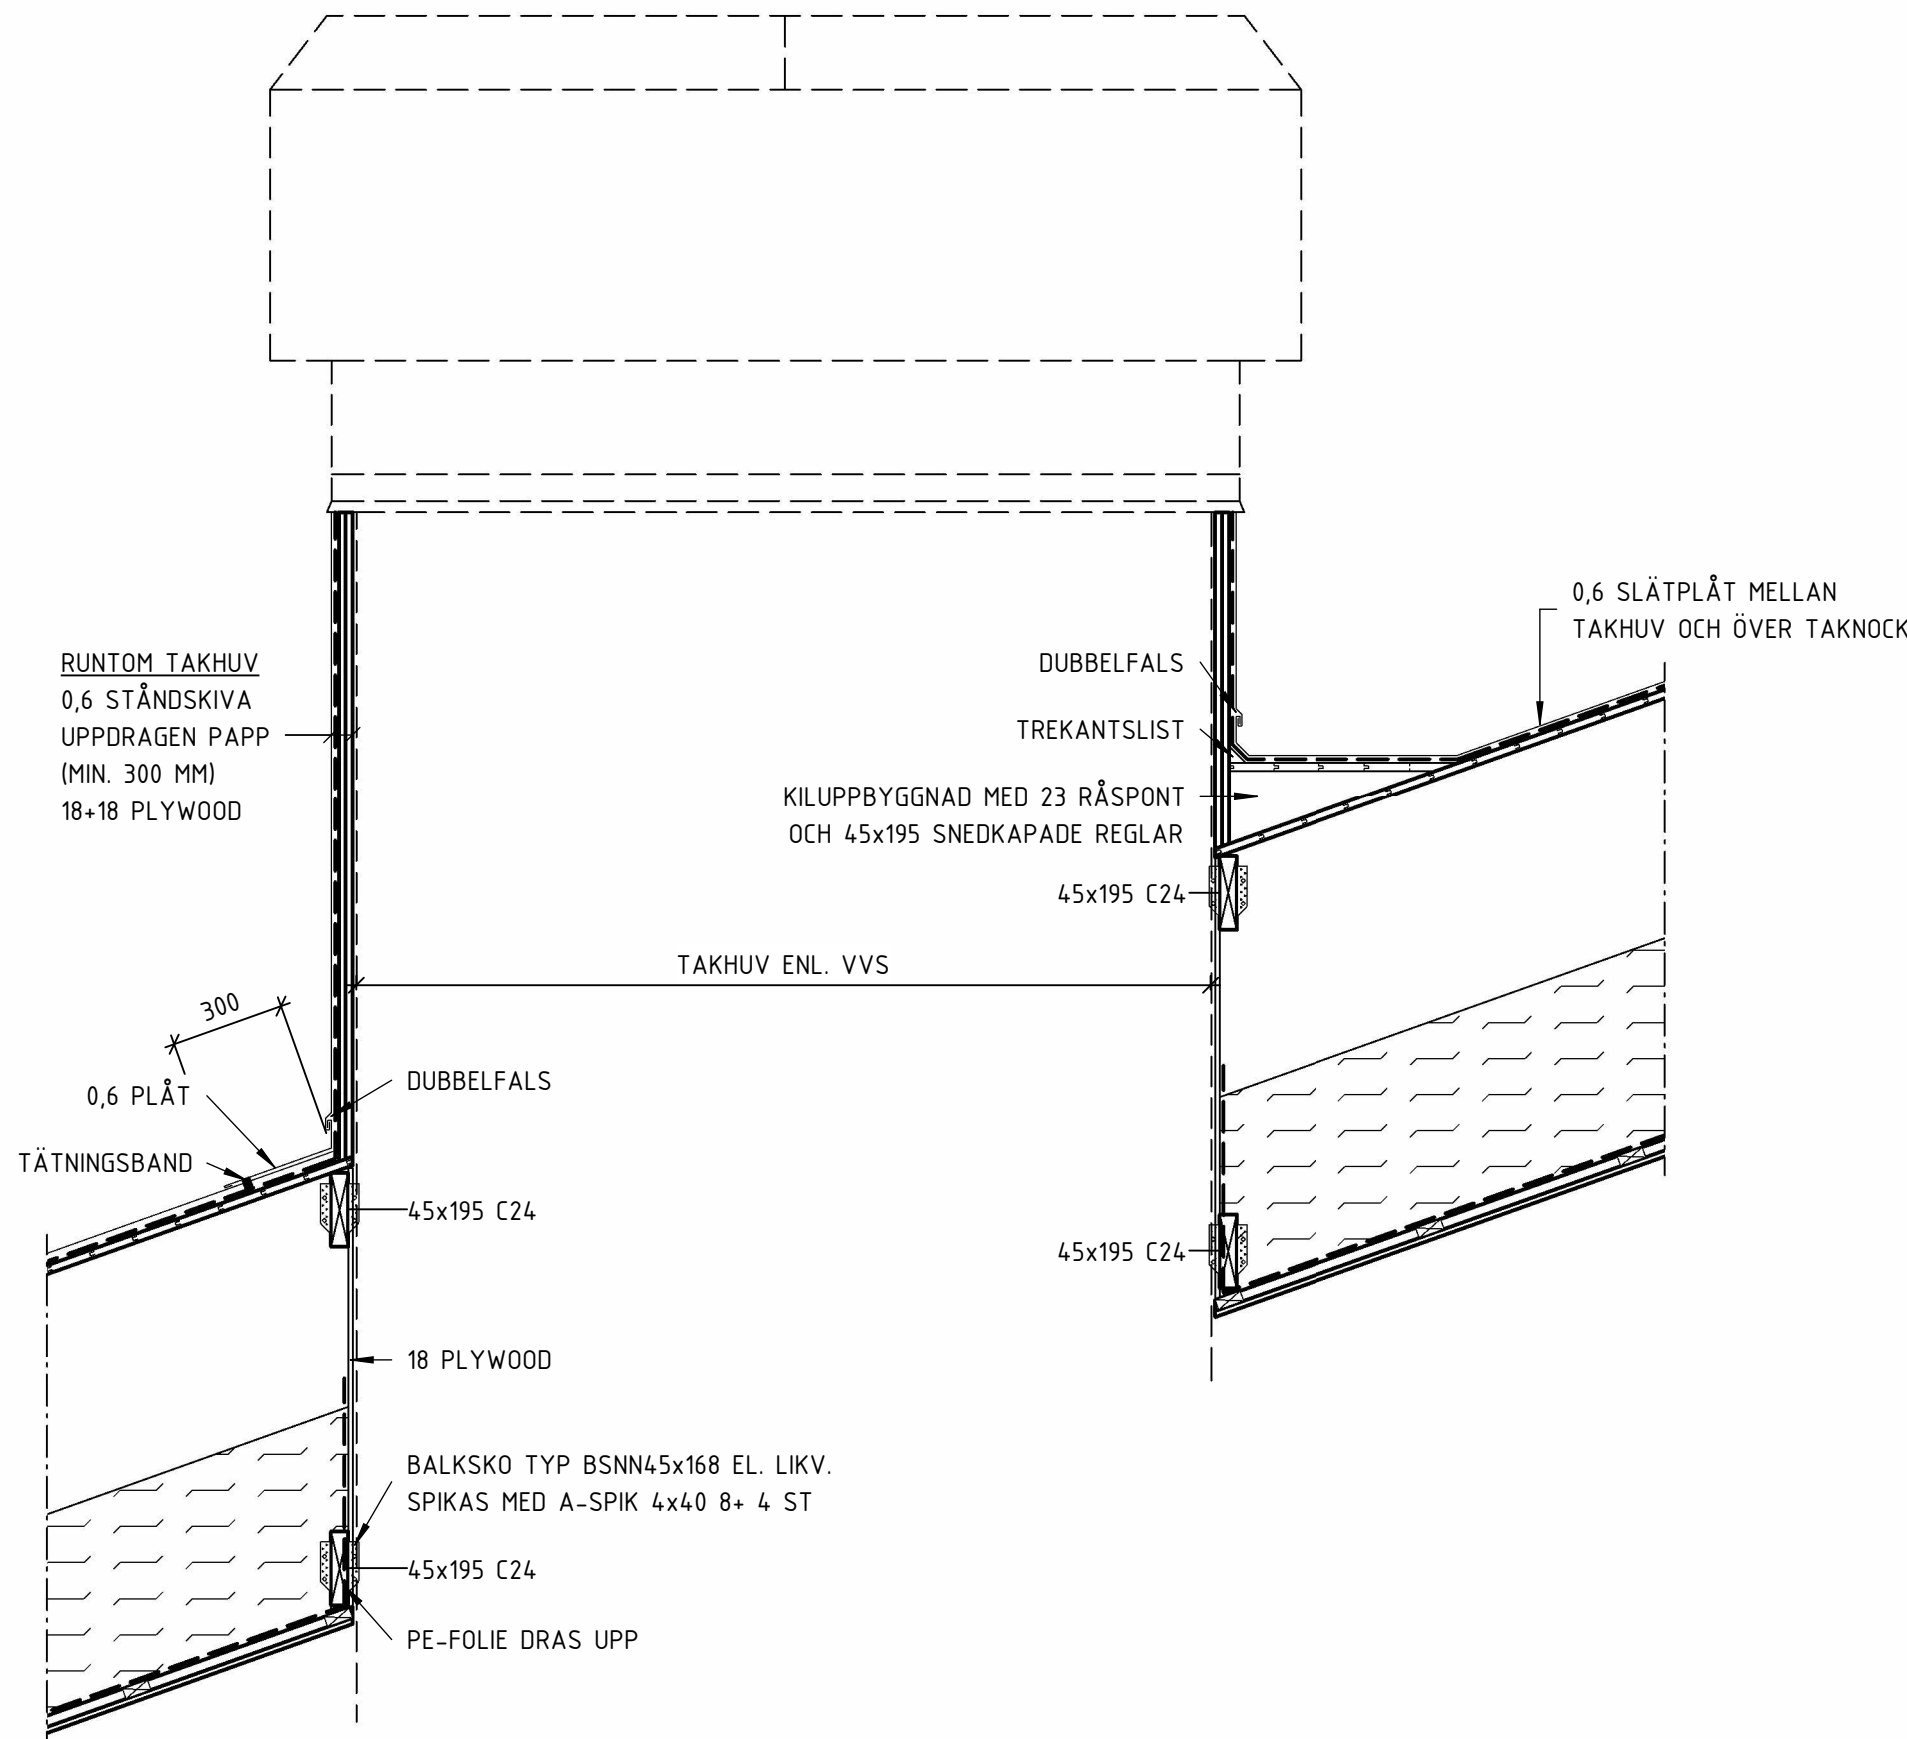

10
1 : 20
PRINCIPDETALJ TAKHUV

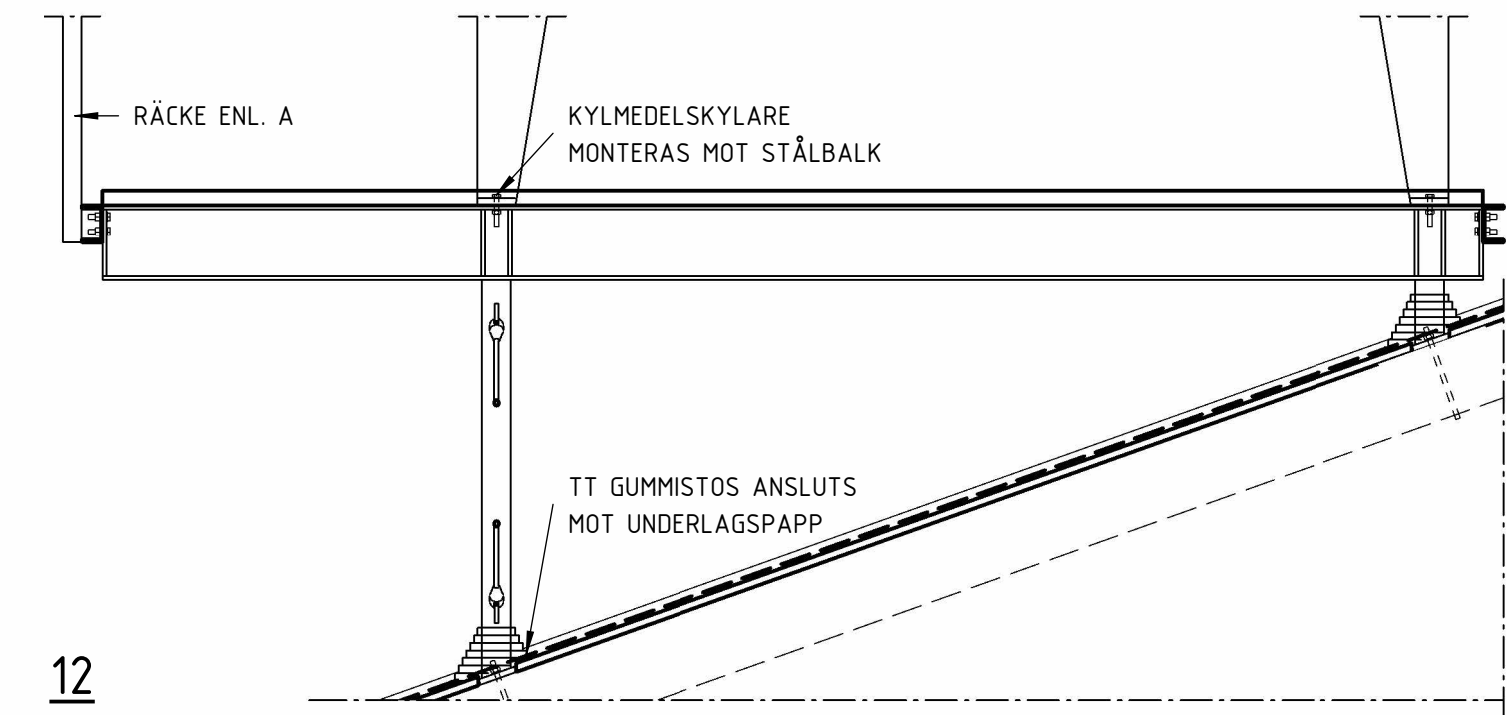

12
1 : 20
KYLMEDELSKYLARE

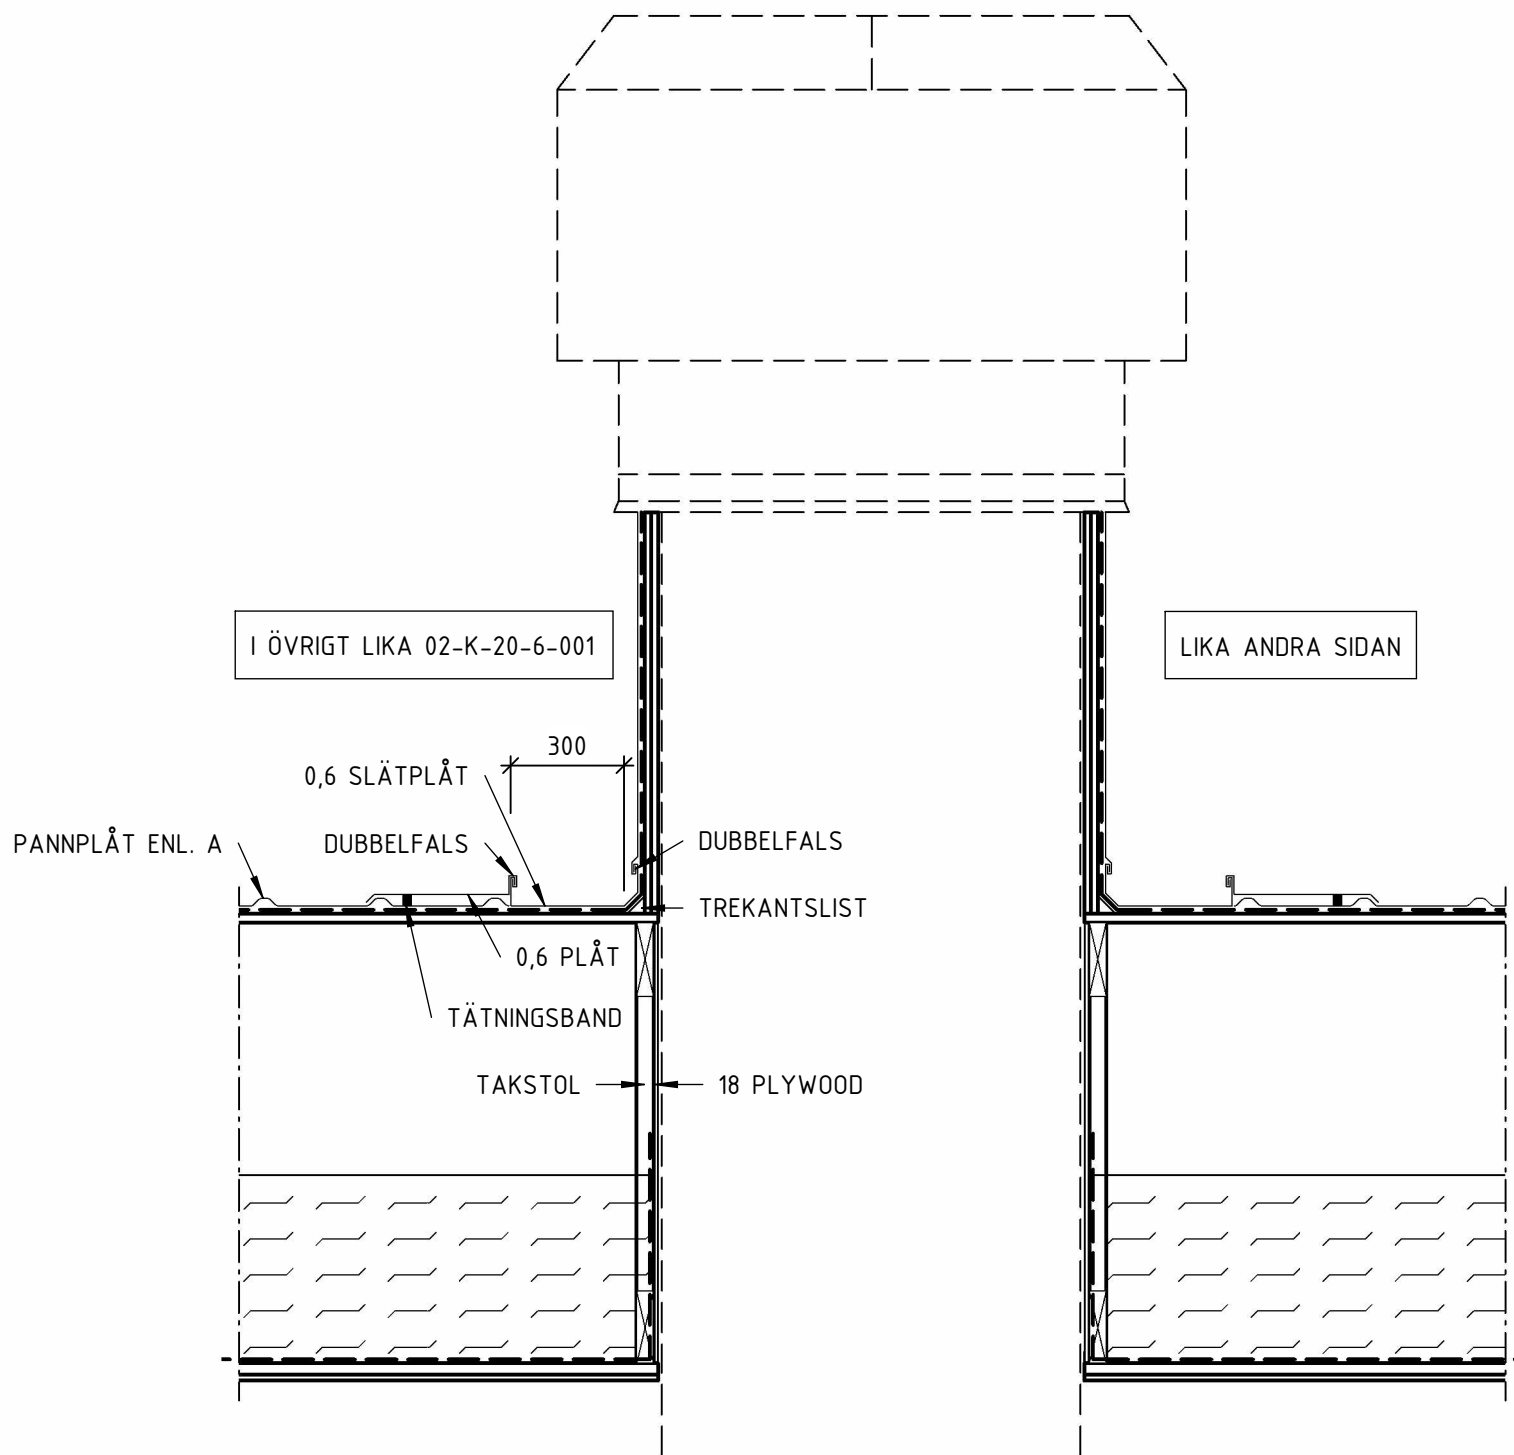

11
1 : 20
PRINCIPDETALJ TAKHUV

SKALA 1:20 0 1 2 METER

SEKTION		
ORIENTERINGSSKISS		
STATUS		
FÖRFRÅGNINGSUNDERLAG		
HANDLING		
BYGGHANDLING		
DATUM	LOSRÄDD AV	ÄNDRINGS PM
2024-12-20	BJÖRN LIDSTRÖM	
BESTÄLLARE		
ROBERTSFORS KOMMUN		
PROJEKTNAMN		
CENTRALEKÖ		
OBJEKT		
ROBERTSFORS KOMMUN		
PROJEKTNUMMER	FASTIGHET	
108 83 71	YTTRE RINGVÄGEN 4	
DIREKTOR	FÖRETAG	
	FORDONET 1	
DISCIPLIN	FÖRETAG	
K	NORCONSULT SVERIGE AB	
UPPDRAGSNUMMER	SKAPAD AV	
108 83 71	AWG/ATN	
TELEFON	KONTAKTPERSON	
010-141 80 00	BJÖRN LIDSTRÖM	
BYGGGÅRSTYR	FÖLJESÄTTNING	
	+45,540 (FG)	
VÄNINGSPLAN	VÄNINGSDEL	DEL 4, 5
SYSTEM		
25 TRÄKONSTRUKTIONER		
SPECIFIKATION		
BYGGDETALJER TAK		
BYGGDETALJ	SKALA	FORMAT
	1:10	A1
DOCUMENTNUMMER		
K-25-6-001		