

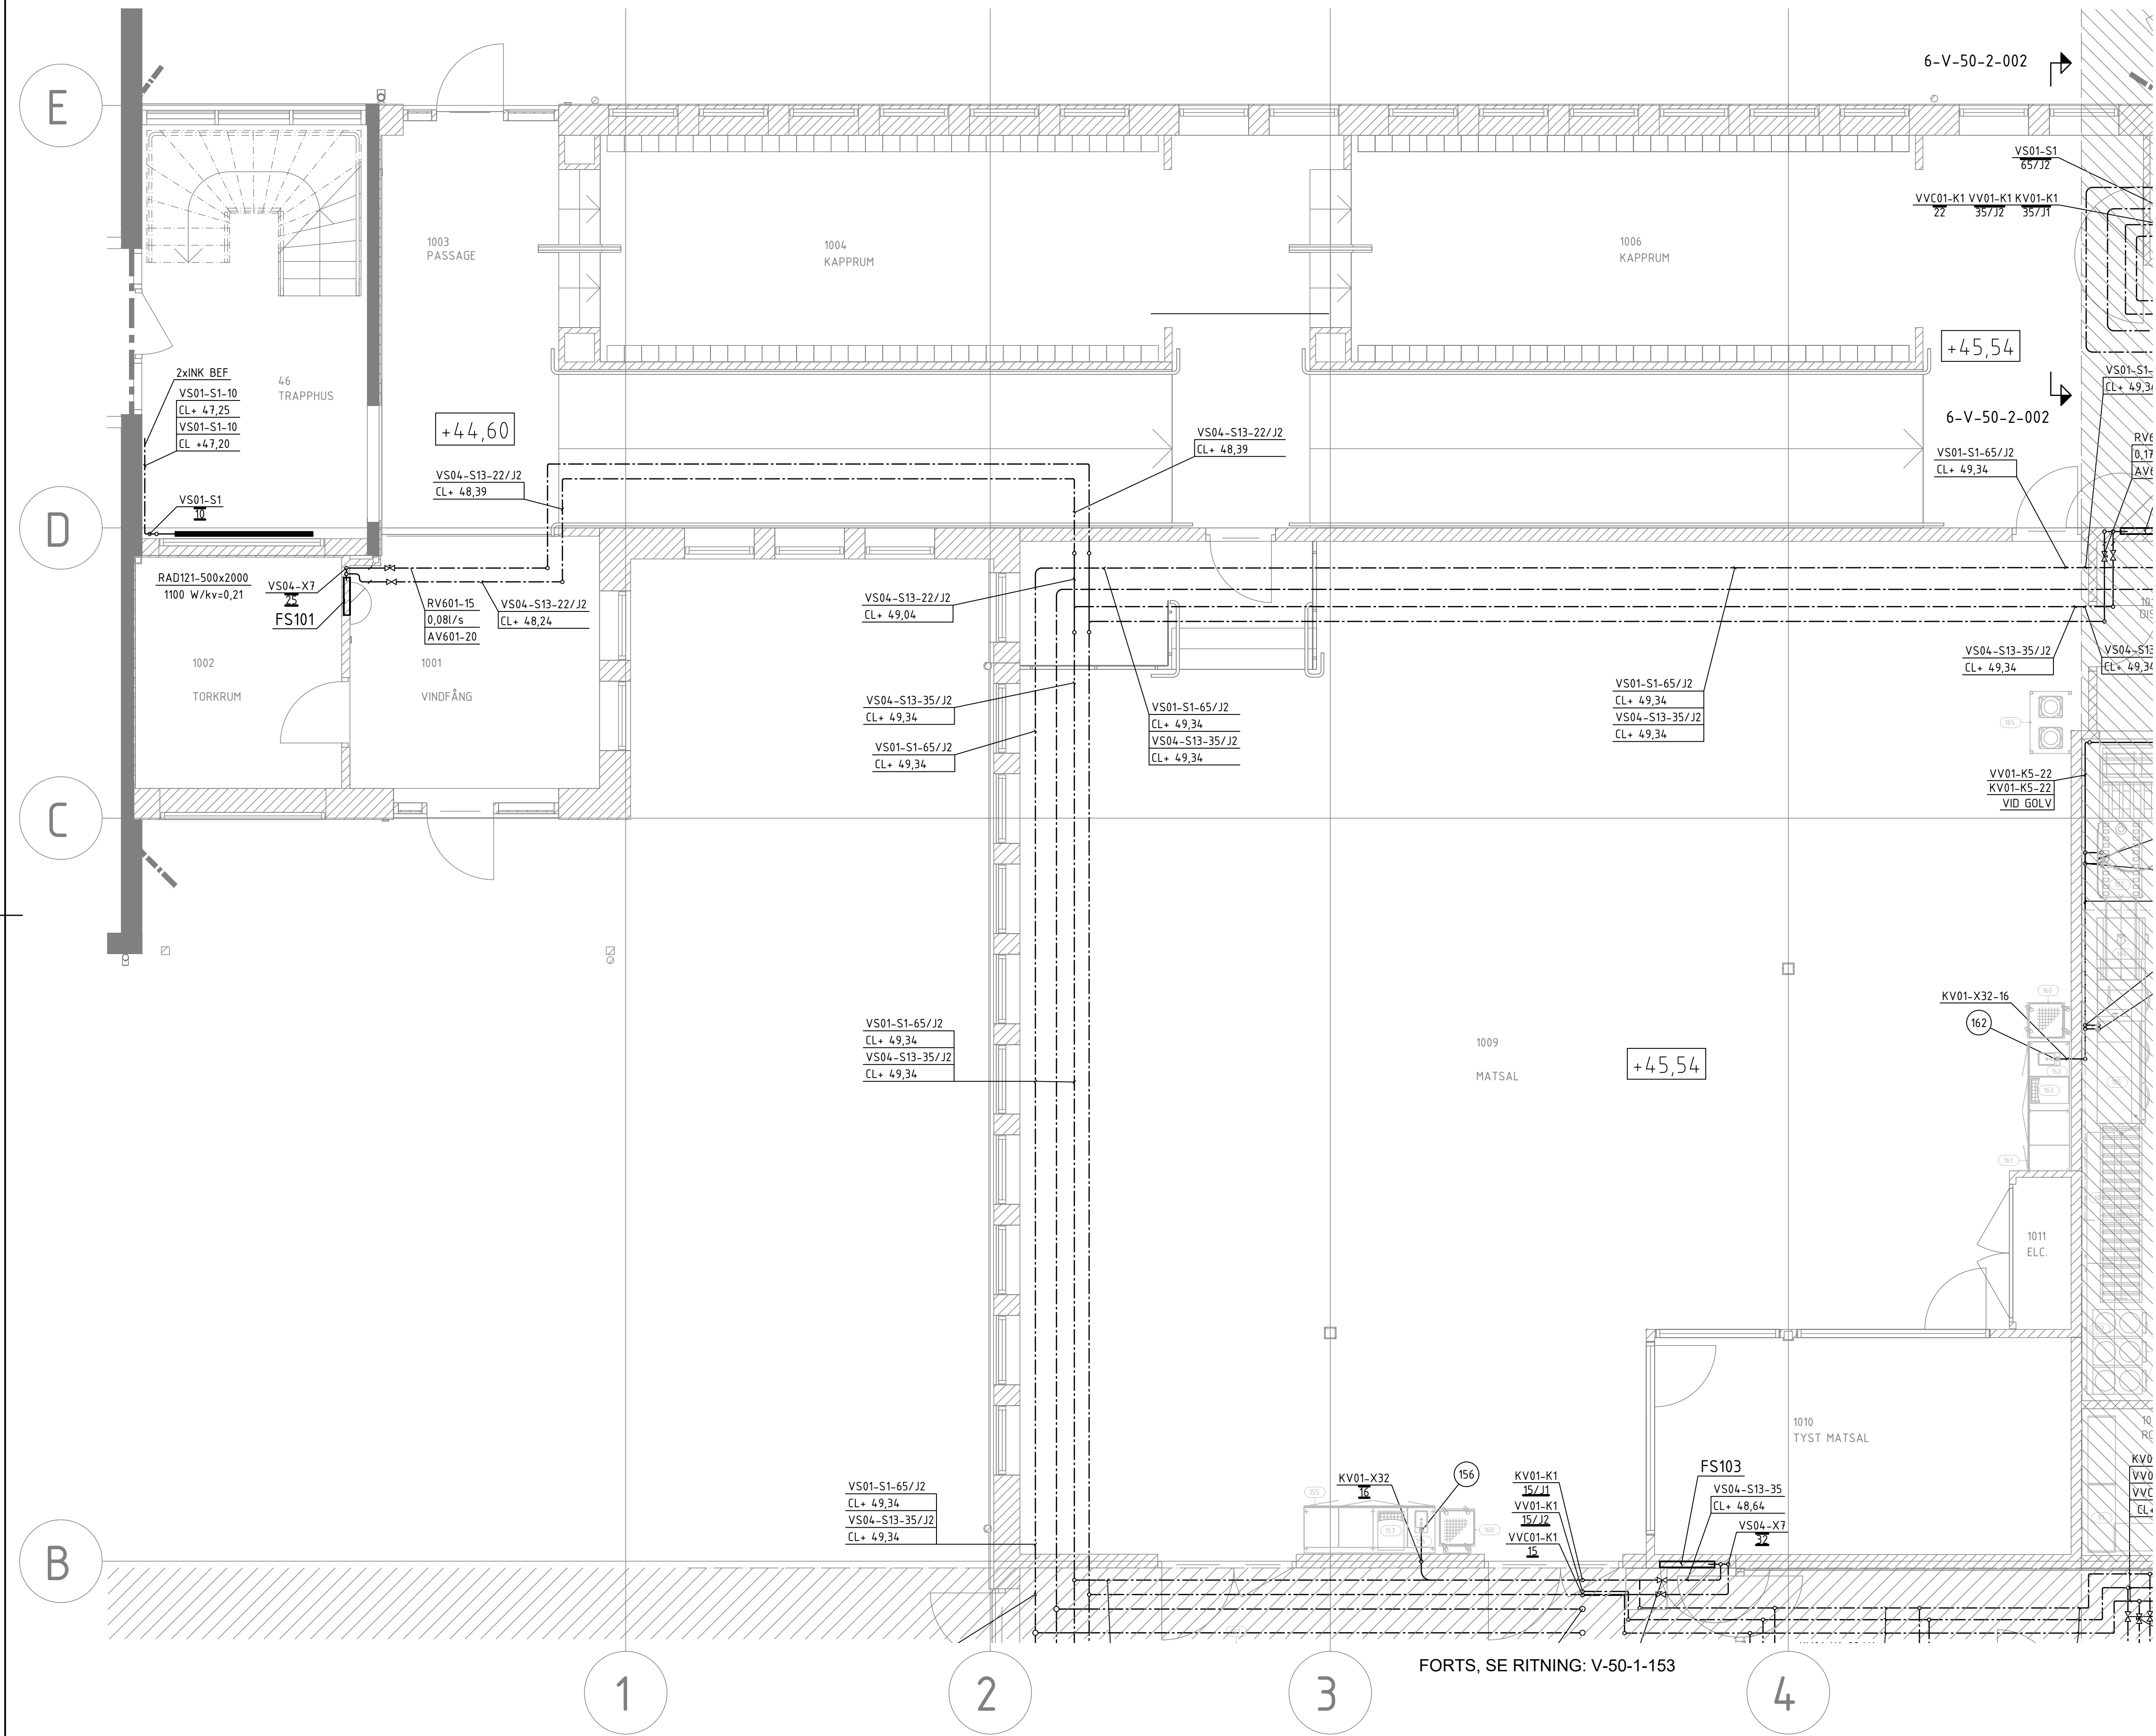


FÖRKLARINGSTEXT
SE RITNING V-50-0-001

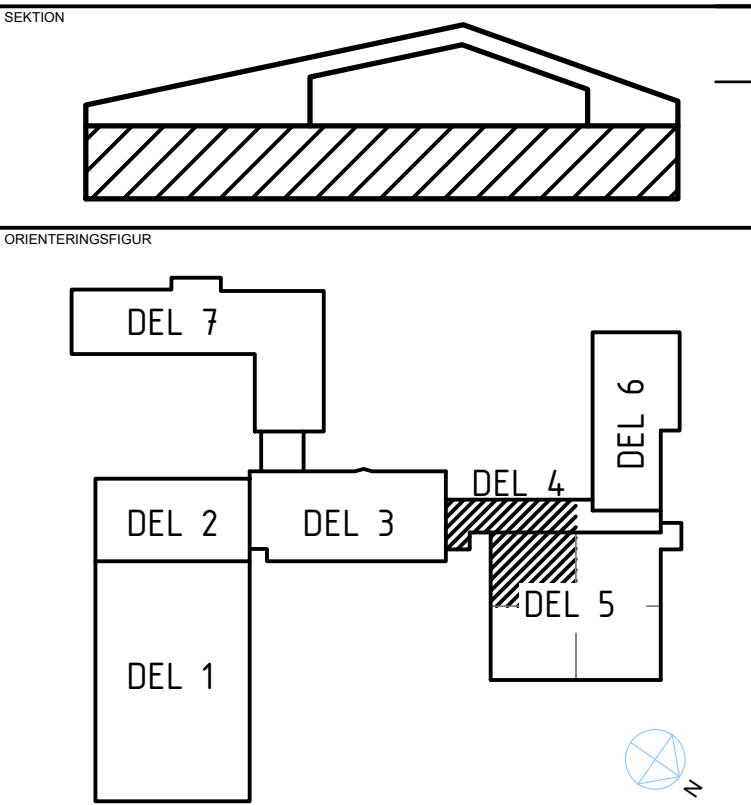

FORTS SE RITNING: V-50-1-152

FORTS, SE RITNING: V-50-1-153

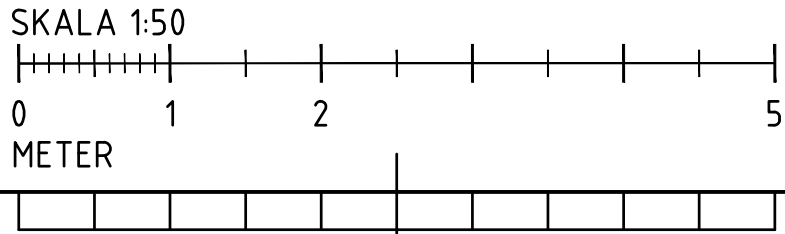

SEKTION		
ORIENTERINGSPOL		
STATUS		
HANDLING		
DATUM	GODKÄND AV	ÄNDRINGS PM
2024-12-20	T.BERGSTRÖM	
BESTÄLLARE		
PROJEKTNAMN		
OMRADE		
PROJEKTNUMMER		
DARIENUMMER		
DISCIPLIN		
OPPRÄGGSNUMMER		
TELEFON		
BYGGNADSVÄRDE		
VÄNINGSPLAN	VÄNINGSDEL	DELOMRÅDE
1		DEL 4.1, 5.1
SYSTEM		
RÖRINSTALLATION		
RITNINGSKATEGORI		
PLAN		
DOKUMENTNUMMER		
V-50-1-151		

FILNAMN: