
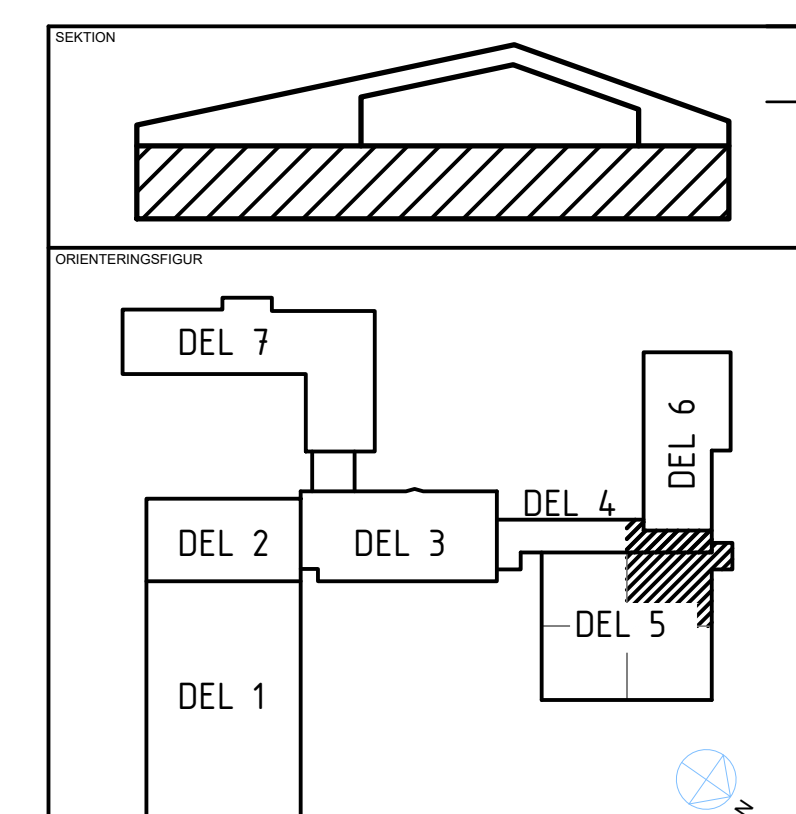


FÖRKLARINGSTEXT
SE RITNING V-50-0-001

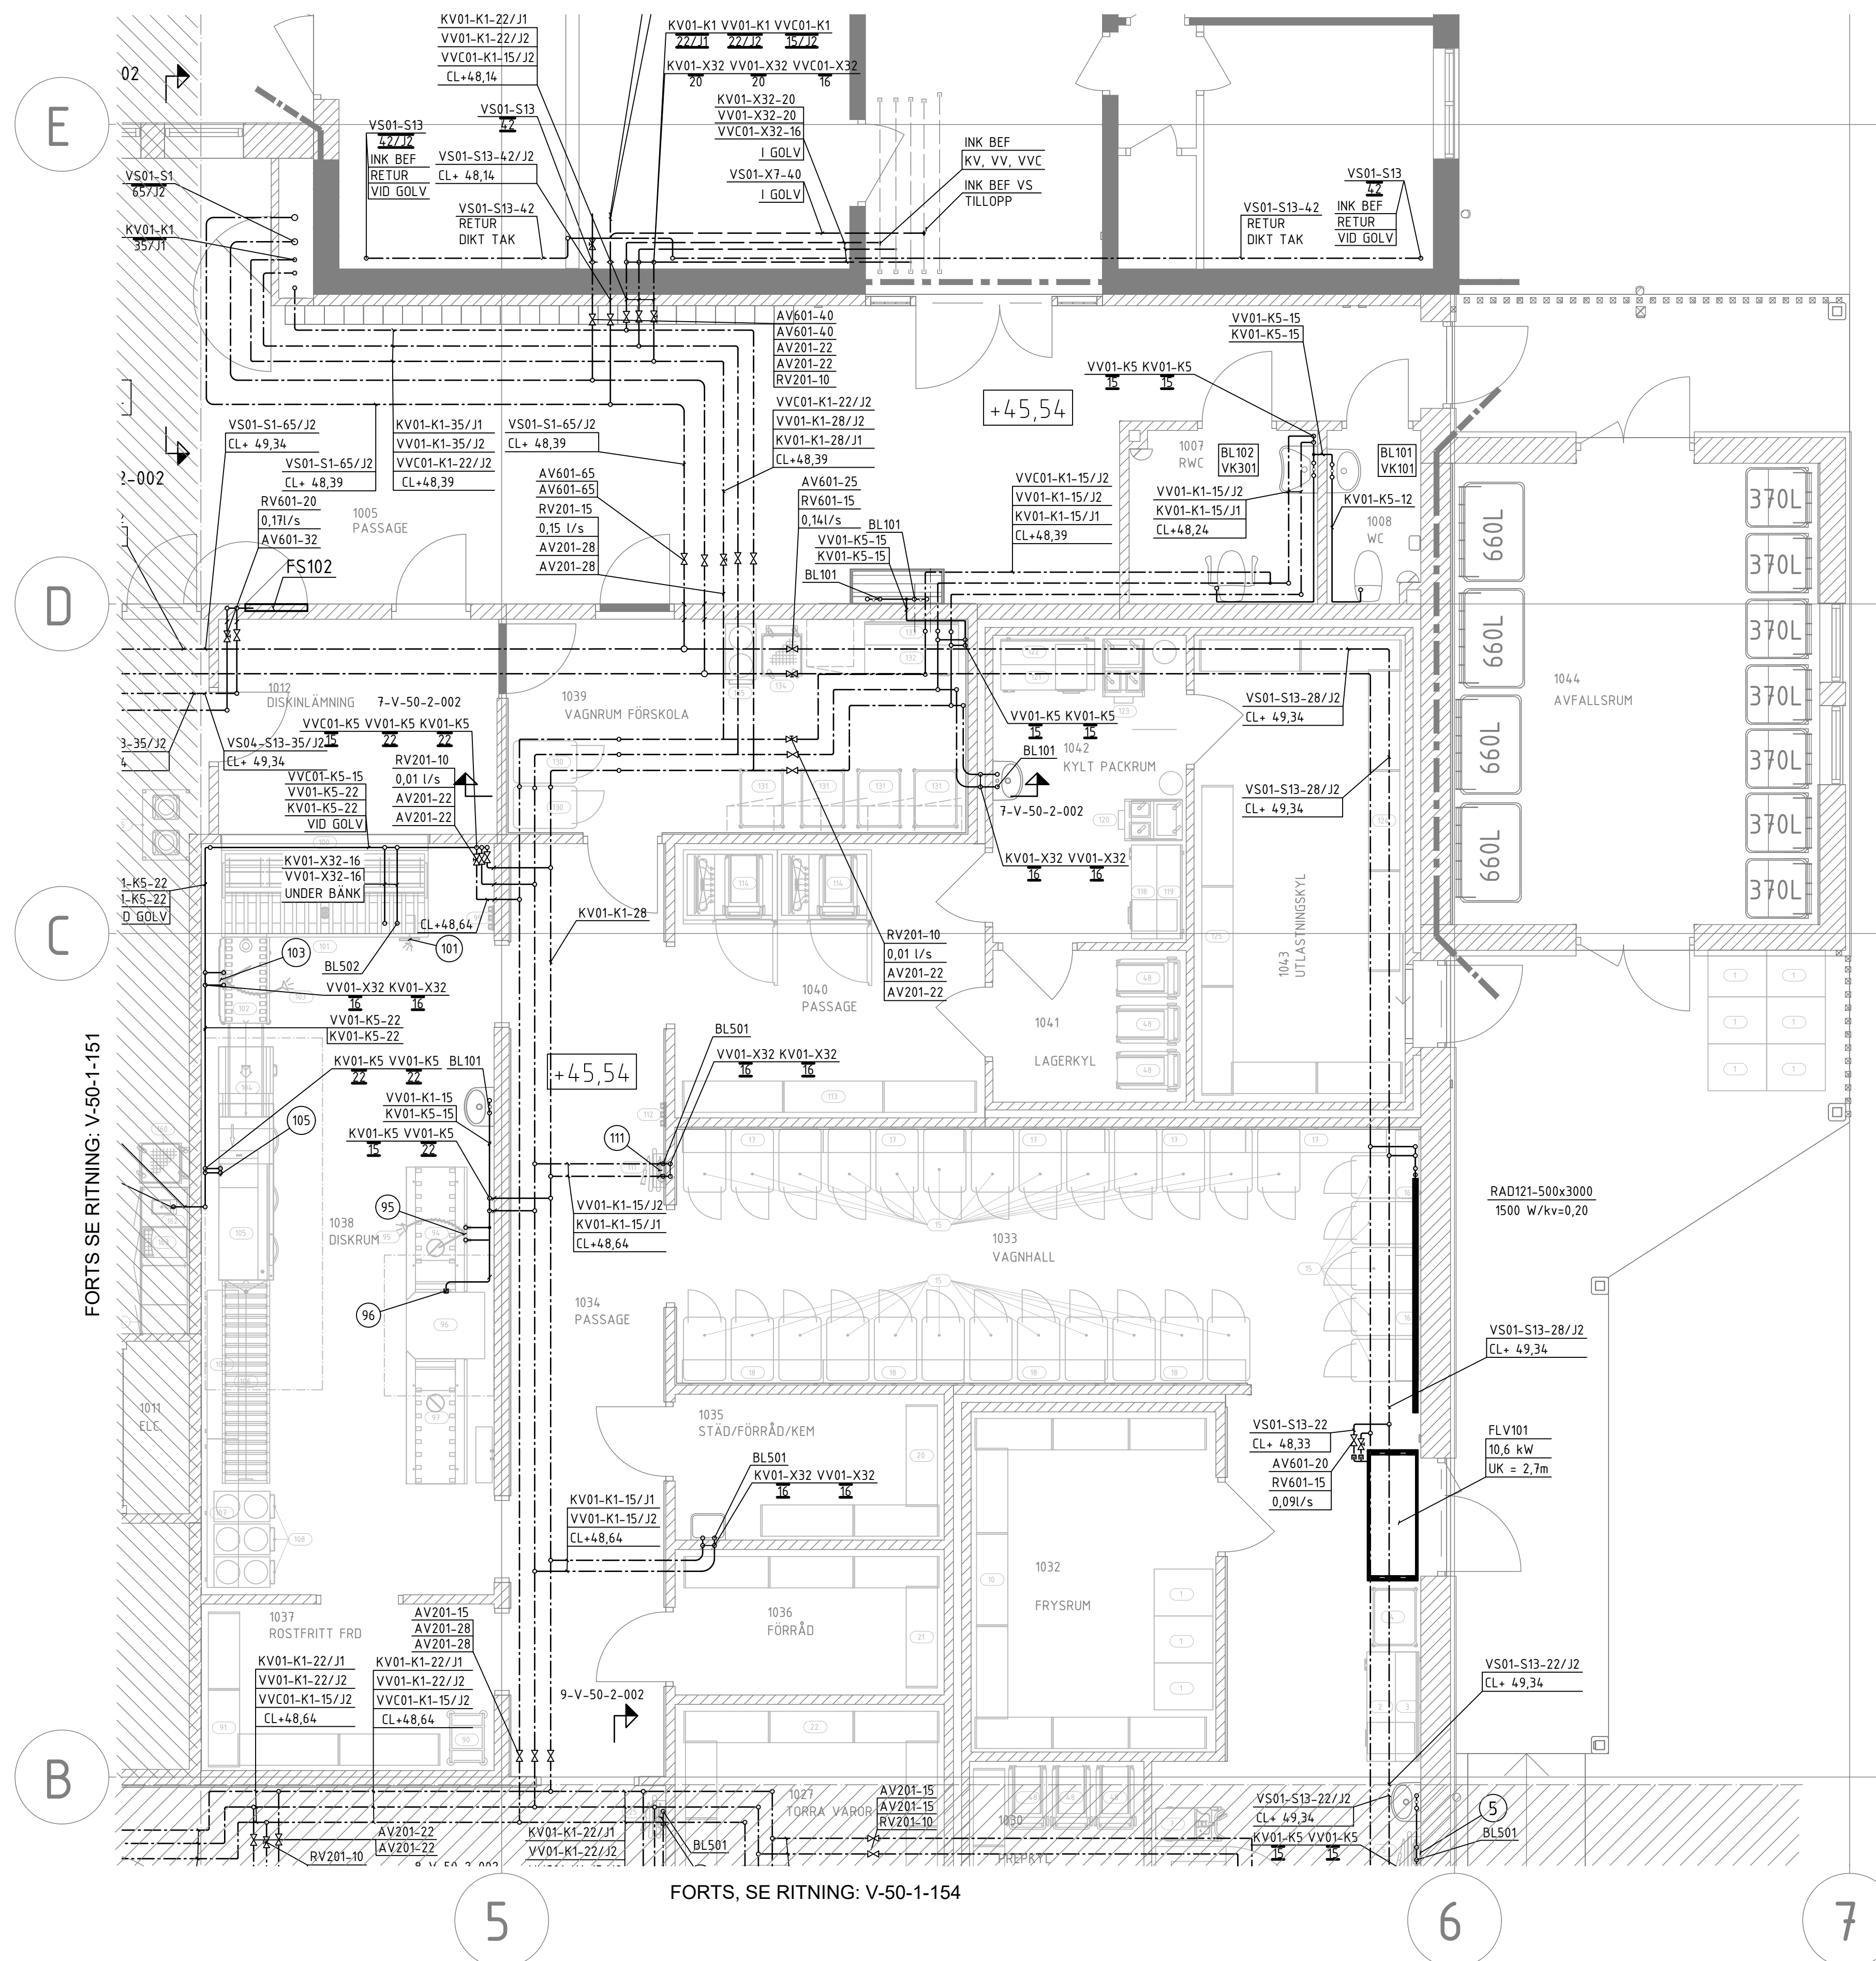

STATUS FÖRFRÅGNINGSUNDERLAG

HANDLING	BYGGHANDLING
----------	--------------

DATUM	GODKÄND AV	ÄNDRINGS PM
2024-12-20	T.BERGSTRÖM	

BESTÄLLARE		
------------	--	--



PROJEKTNAMN

CENTRAKKÖK

OMRADE
ROBERTSFORS KOMMUN

PROJEKTNUMMER	ADRESS
	YTTRE RINGVÄGEN 4

DIARIENUMMER	FASTIGHET FORDONET 1
EGGIDNUMMER	EGGIDTAG

DISCIPLIN	FÖRETAG
VS	NORCONSULT SVERIGE AB
LIPPDAGSNUMMER	SKAPAD AV

UPPDRAGSNUMMER 108 83 71	SKAPAD AV MAN
TELEFON	KONTAKTPERSON

TELEFON	KONTAKTPERSON
010 141 80 00	JONAS JOHANSSON
BYGGNADSVÄRK	PLUSHÖJD (RH 2000)

		+45,54 (FG)
VANINGSPLAN 1	VANINGSDEL	DELOMRÅDE DEL 1 2 5 3

1	DEL 4.2, 5.2
SYSTEM	
50 RÖRINSTALLATIONER	

50 RORINSTALLATIONER
SPECIFIKATION
PLAN 1 - DEL 4.2, 5.2

PLAN 1 - DEL 4.2, 5.2		
RITNINGSKATEGORI	SKALA	FORMAT
PLAN	1:50	A1

PLAN	1:50	AI
DOKUMENTNUMMER V-50-1-152		ÄNDRING

$V = 50 = 1 = 152$	
--------------------	--

SKALA 1:50

0 1 2 5

METER

FILNAMN: