
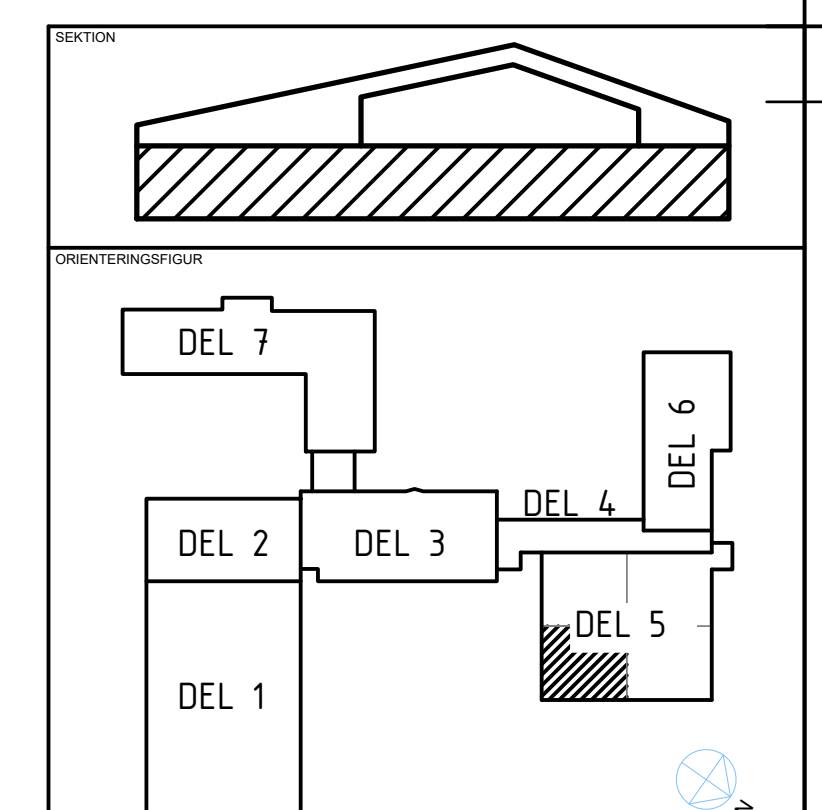


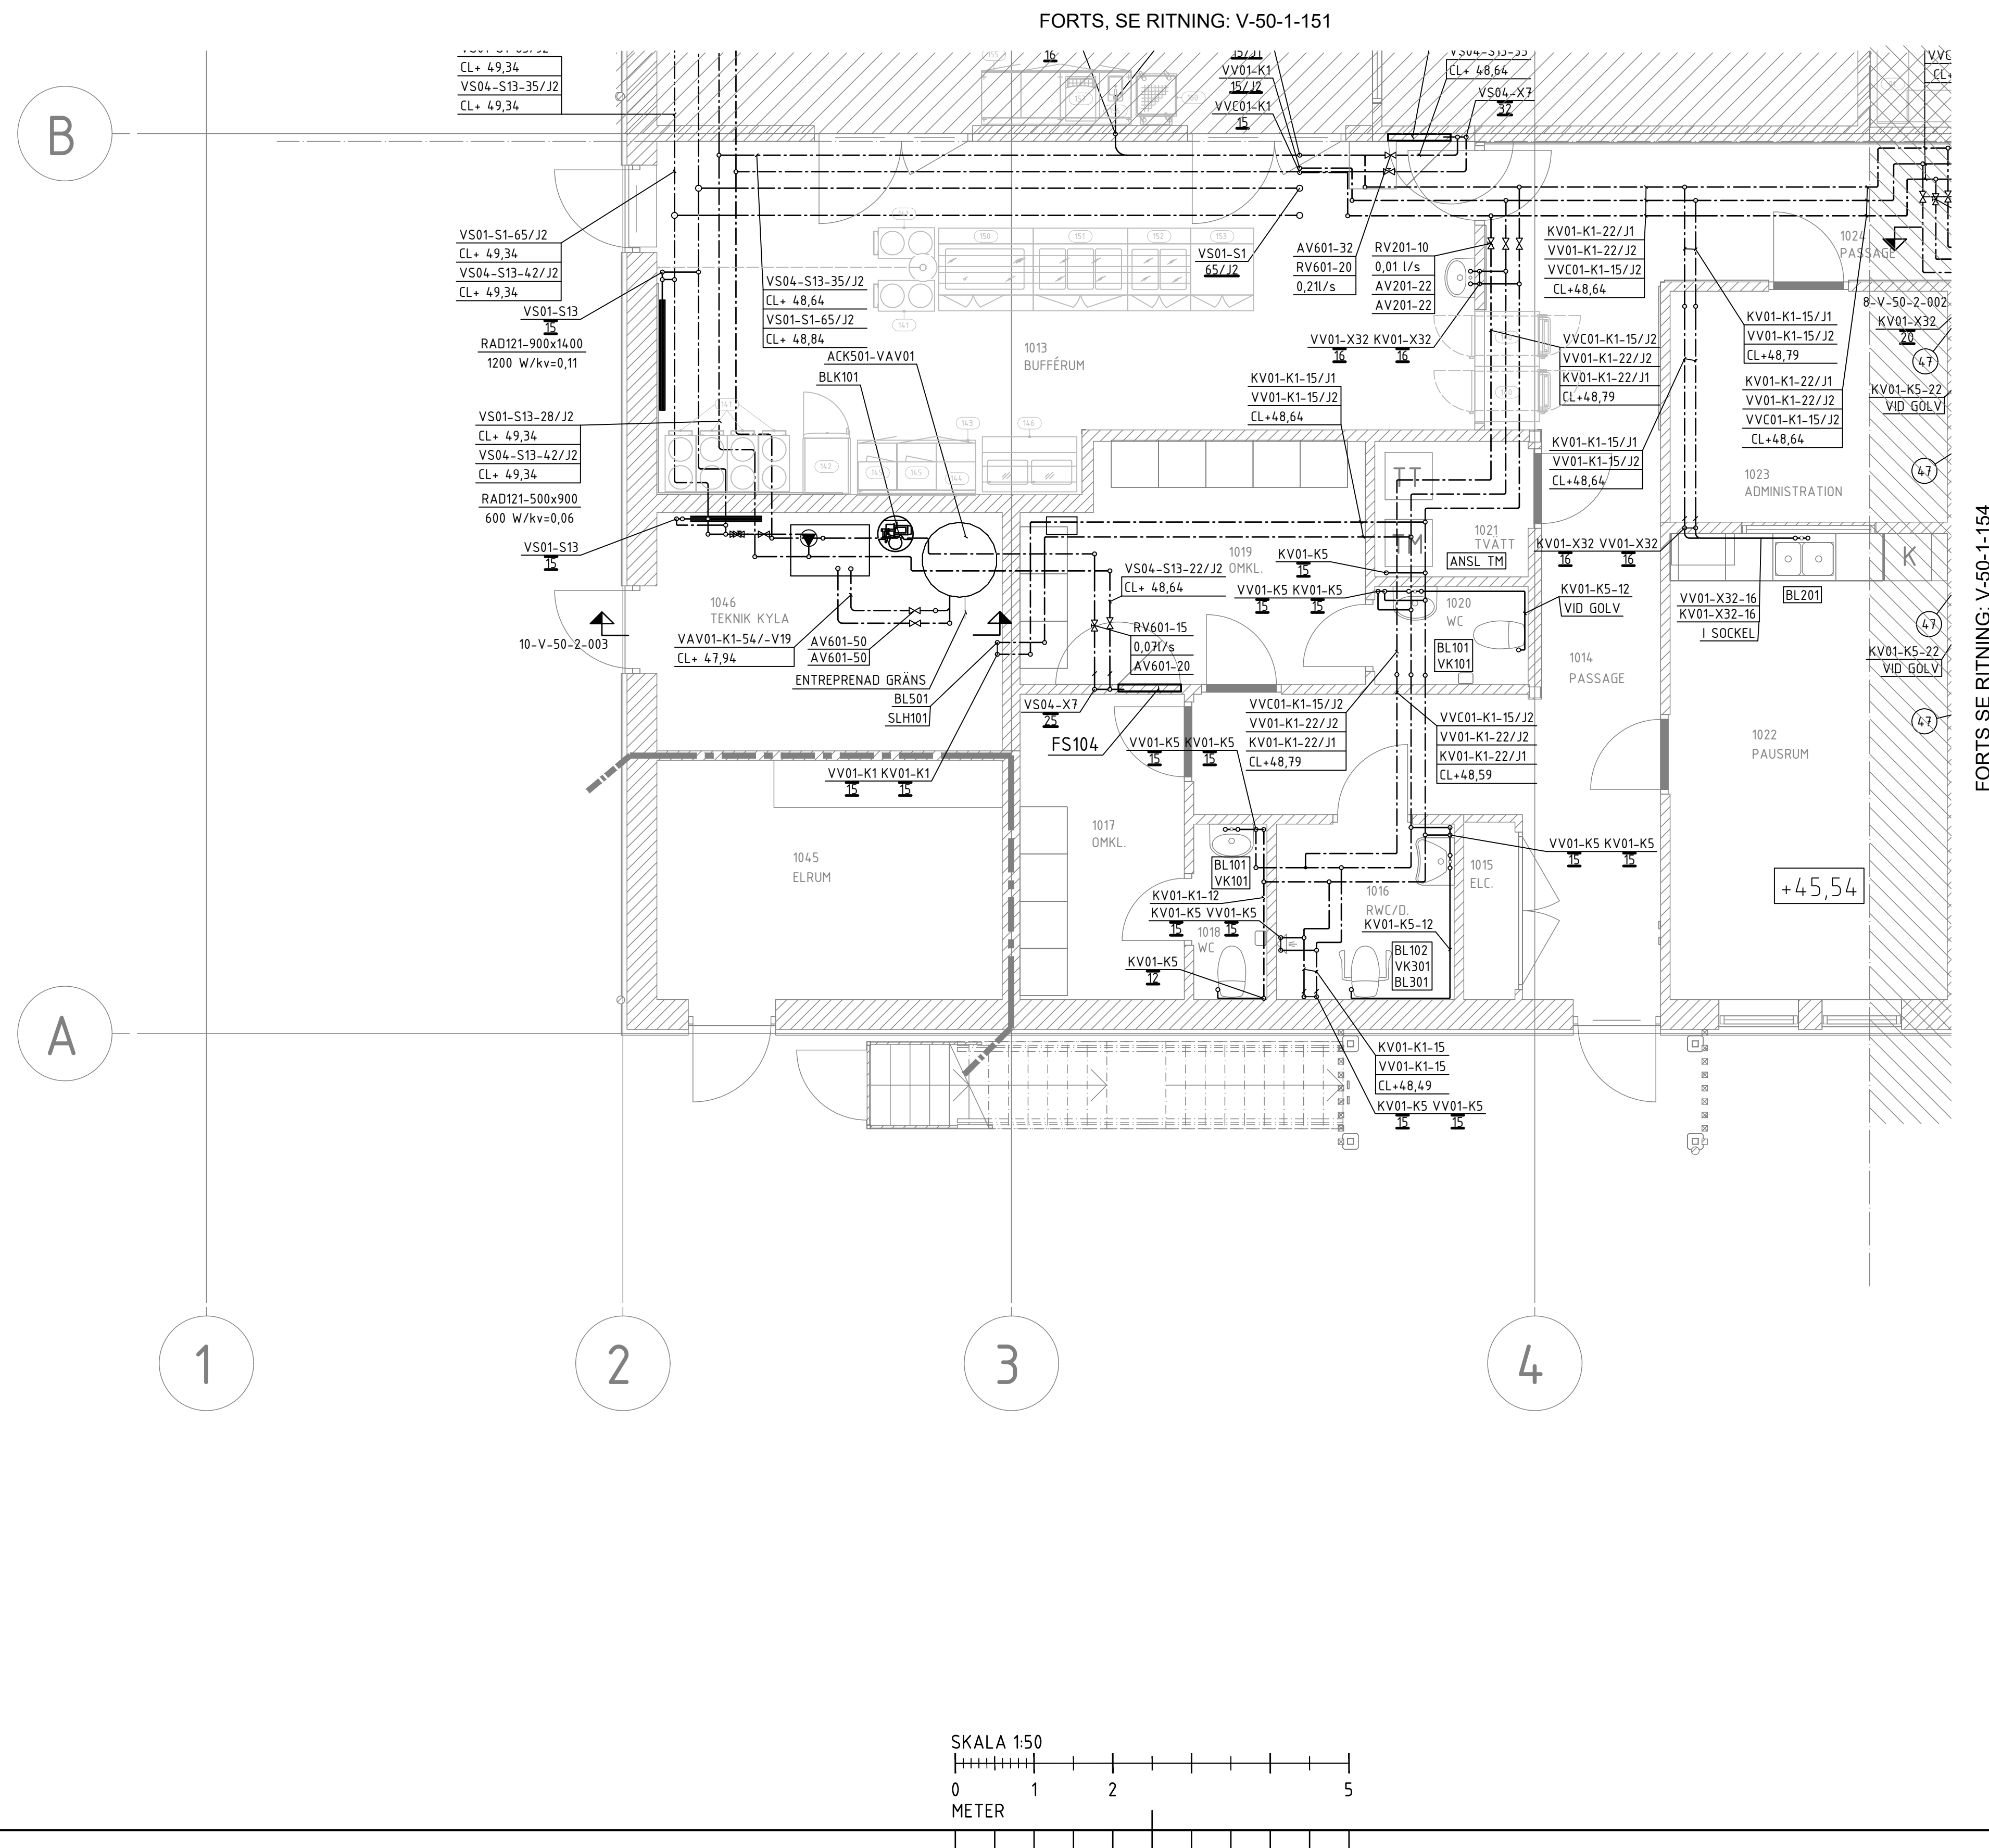

STATUS			
FÖRFRÅGNINGSUNDERLAG			
HANDLING			
DATUM 2023-12-20		GÖRKÄND AV T.BERGSTRÖM	
BESTÄLLARE		ÄNDRINGS FM	
		ROBERTSFORS KOMMUN	
PROJEKTNÄMN			
CENTRALKÖK			
OMRÅDE ROBERTSFORS KOMMUN			
PROJEKTNUMMER		ADRESS	
		YTTRE RINGVÄGEN 4	
DARIENUMMER		FÖRORDNET 1	
BESÖKUR VS		FÖRSTÄ NORCONSULT SVERIGE AB	
UTFÖRARNUMMER 108 83 71		SKAVAD AV MAN	
TELEFON 010 141 80 00		JONAS JOHANSSON	
BYGGNÄMNSVERK		PLUSKÖD (RM 2000) +45 54 (FG) DEL 5.3	
VÄNINGSPLAN 1	VÄNINGSDEL		
SYSTEM 50 RÖRINSTALLATIONER			
SPECIFICATION PLAN 1 - DEL 5.3			
RITNINGSGRUPP PLAN		SKALA 1:50	FORMAT A1
DOKUMENTNUMMER V-50-1-153			ÄNDRING