
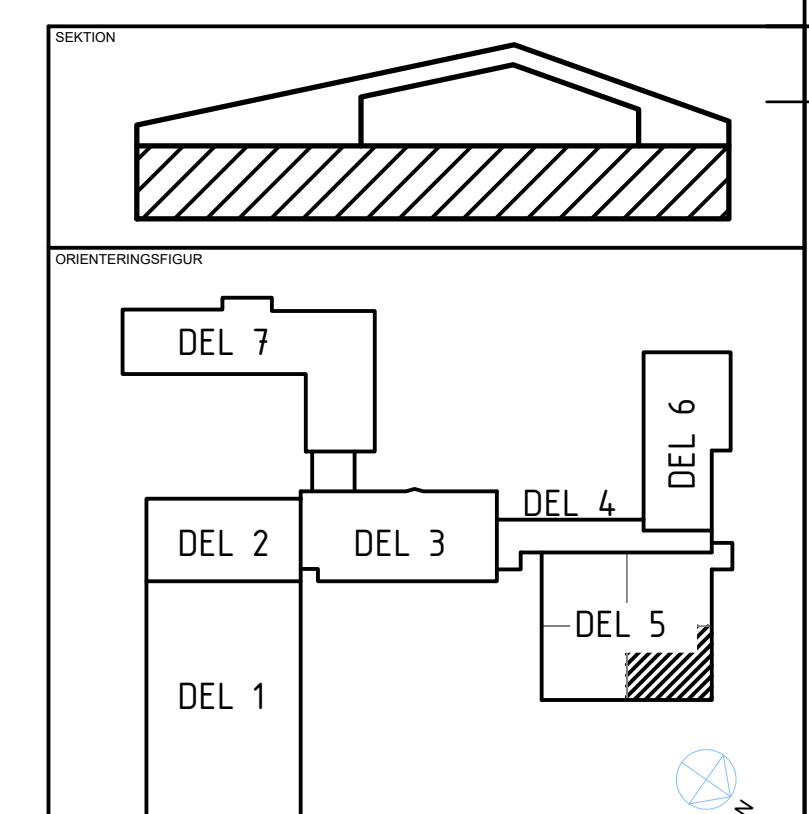
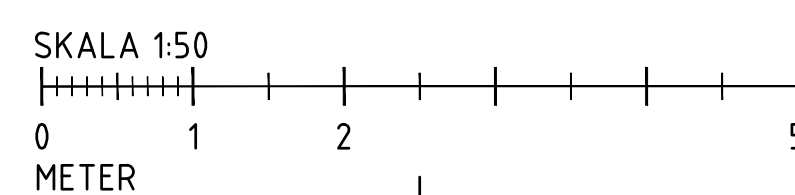


FÖRKLARINGSTEXT
SE RITNING V-50-0-001

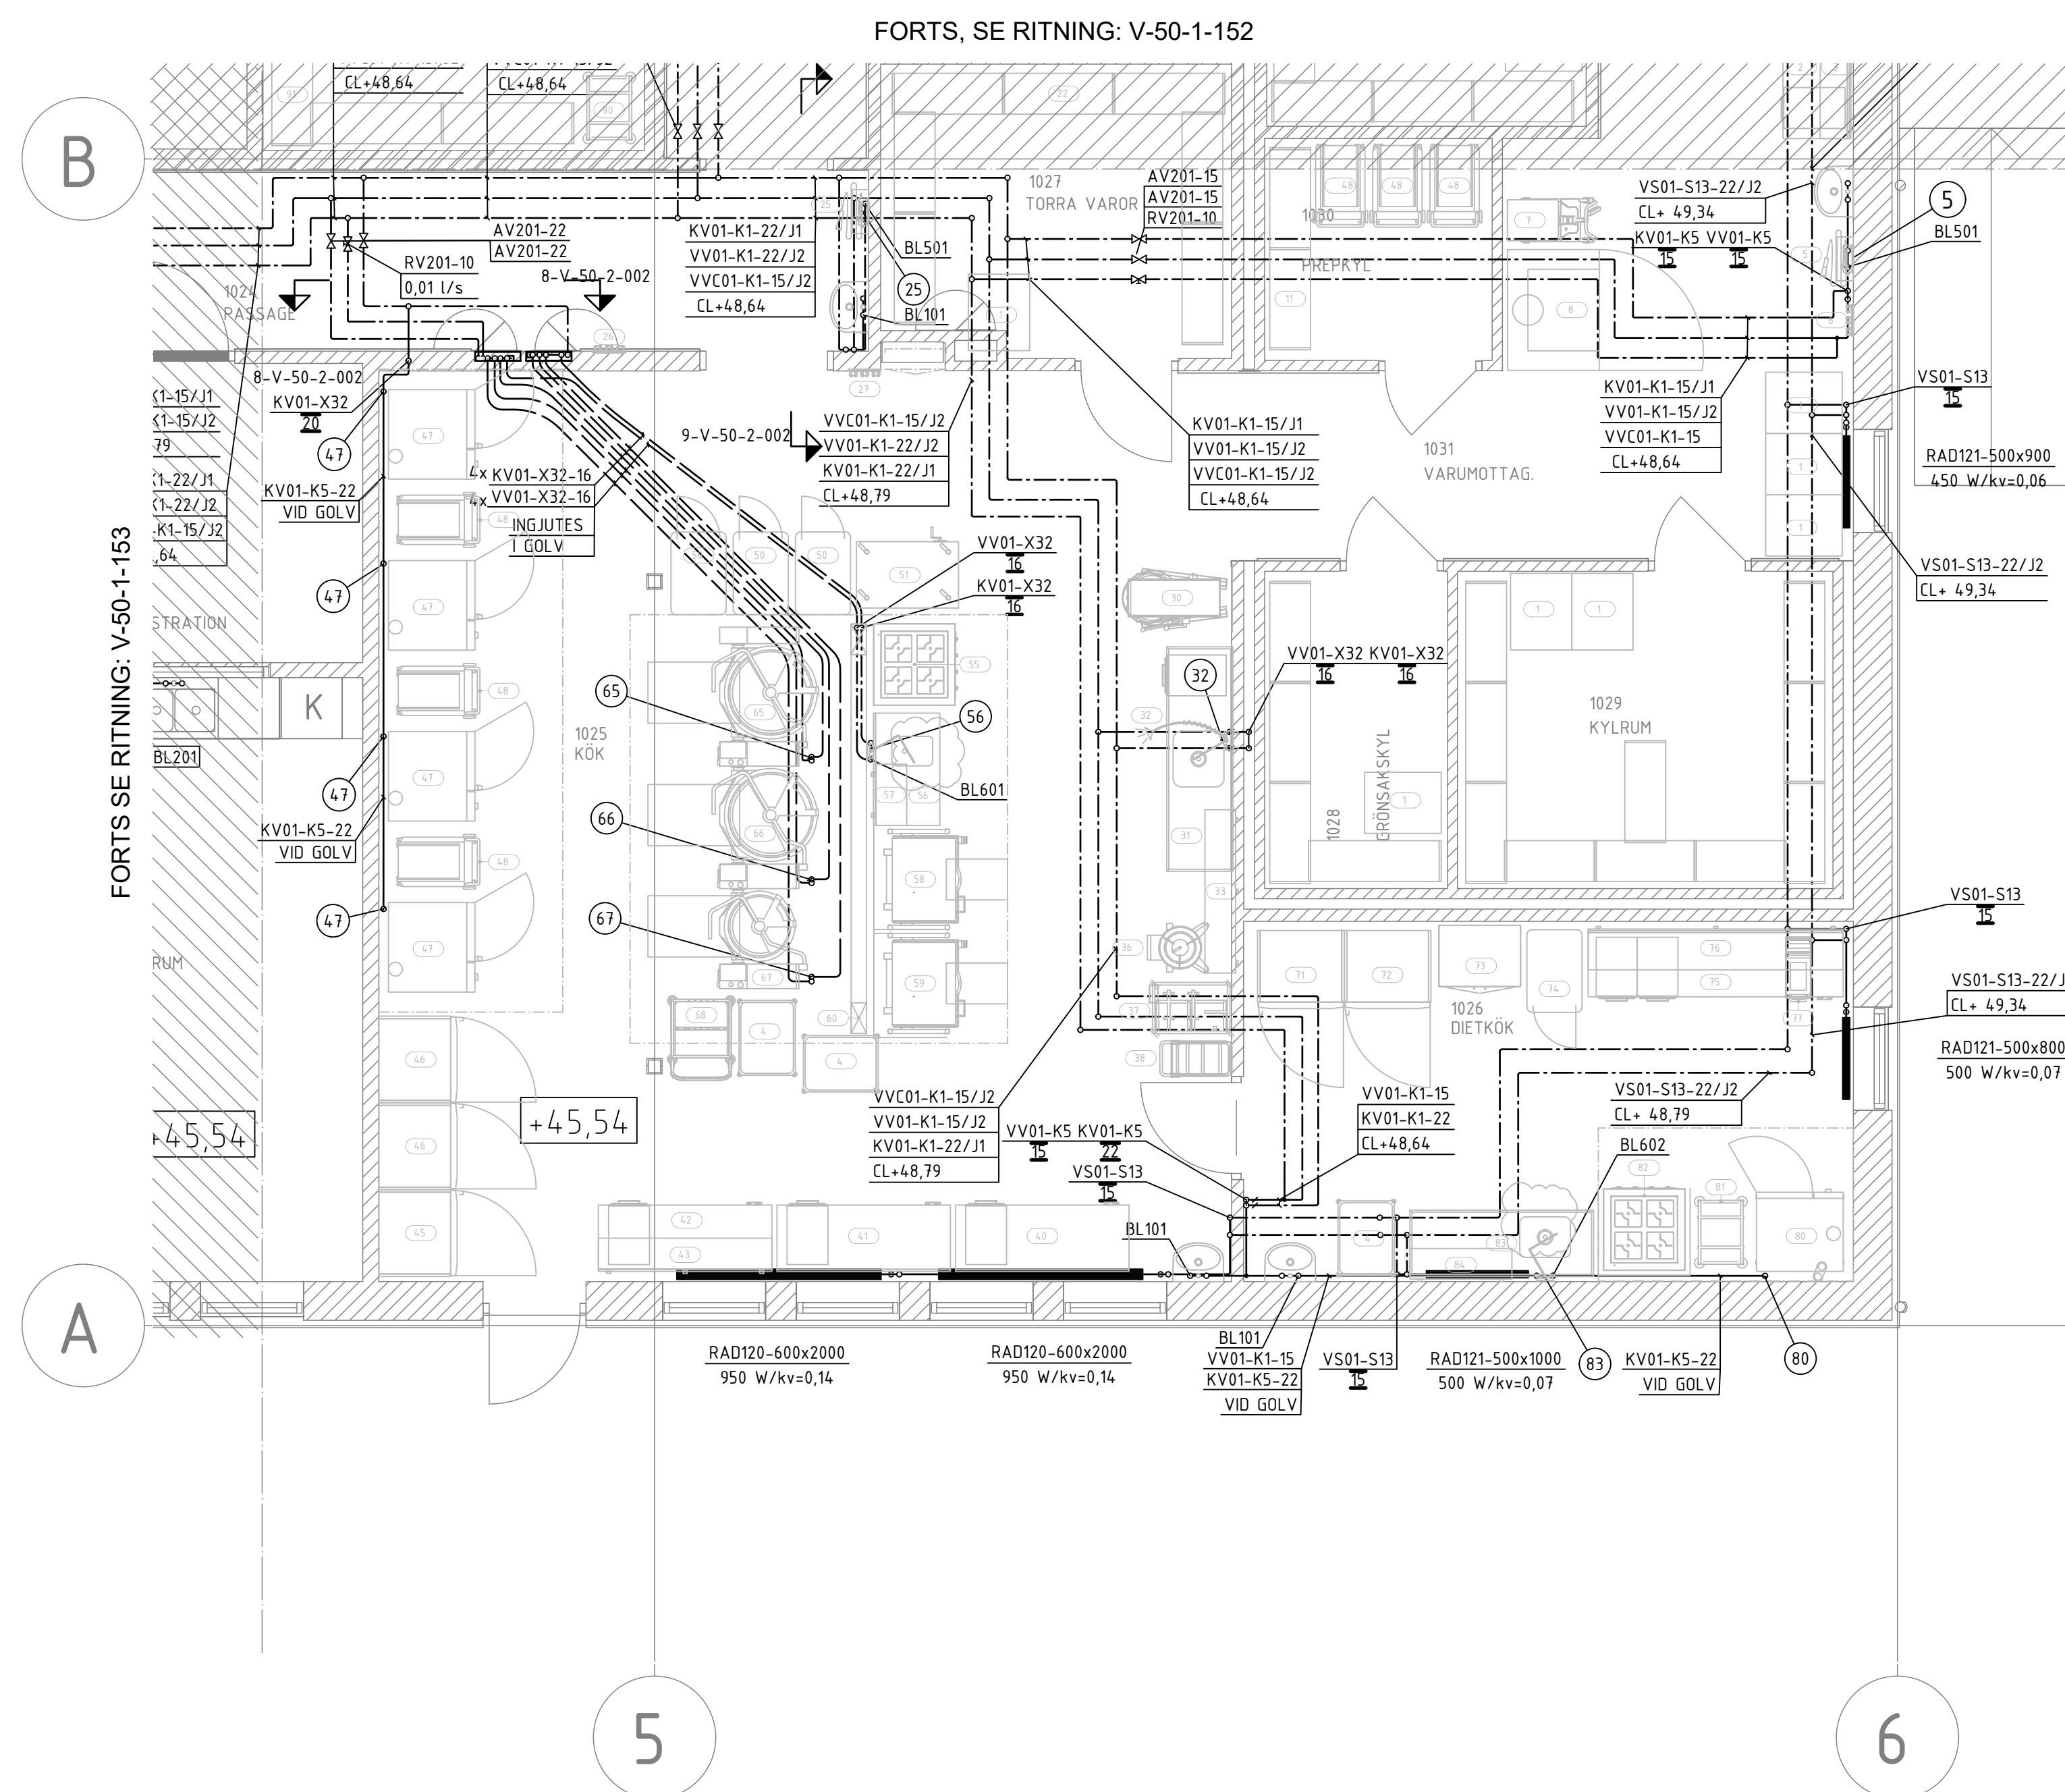

STATUS FÖRFRÅGNINGSUNDERLAG

HANDLING	BYGGHANDLING
----------	--------------

DATUM	GODKÄND AV	ÄNDRINGS PM
2024-12-20	T.BERGSTRÖM	

BESTÄLLARE



PROJEKTNAMN CENTRAALKÖK

OMRADE
ROBERTSFORS KOMMUN

PROJEKTNUMMER	ADRESS
	YTTRE RINGVÄGEN 4

DIARIENUMMER	FASTIGHET FORDONET 1
--------------	-------------------------

DISCIPLIN	FÖRETAG
VS	NORCONSULT SVERIGE AB

UPPDRAGSNUMMER 108 83 71	SKAPAD AV MAN
TELEFON	KONTAKTPERSON

TELEFON	KONTAKTPERSON
010 141 80 00	JONAS JOHANSSON
RYCKMÄSSIG	PL. 1000 10 (RM 2000)

BYGGNADSVÄRDE		PLUSHOJD (RH 2000)
		+45,54 (FG)
VÄNINGSDI AN	VÄNINGSDI EI	DEI OMRÅDE

VÄNINGSPLAN	VÄNINGSDEL	DELOMRÅDE
1		DEL 5.4
SYSTEM		

50 RÖRINSTALLATIONER

SPECIFICATION		
PLAN 1 - DEL 5.4		
RITNINGSKATEGORI	SKALA	FORMAT

ÄRNINGSGRUPP/EGENHET	SKALA	FORMAT
PLAN	1:50	A1
DOKUMENTNUMMER	ÄNDRING	

V-50-1-154	
------------	--

Full Name:	
------------	--