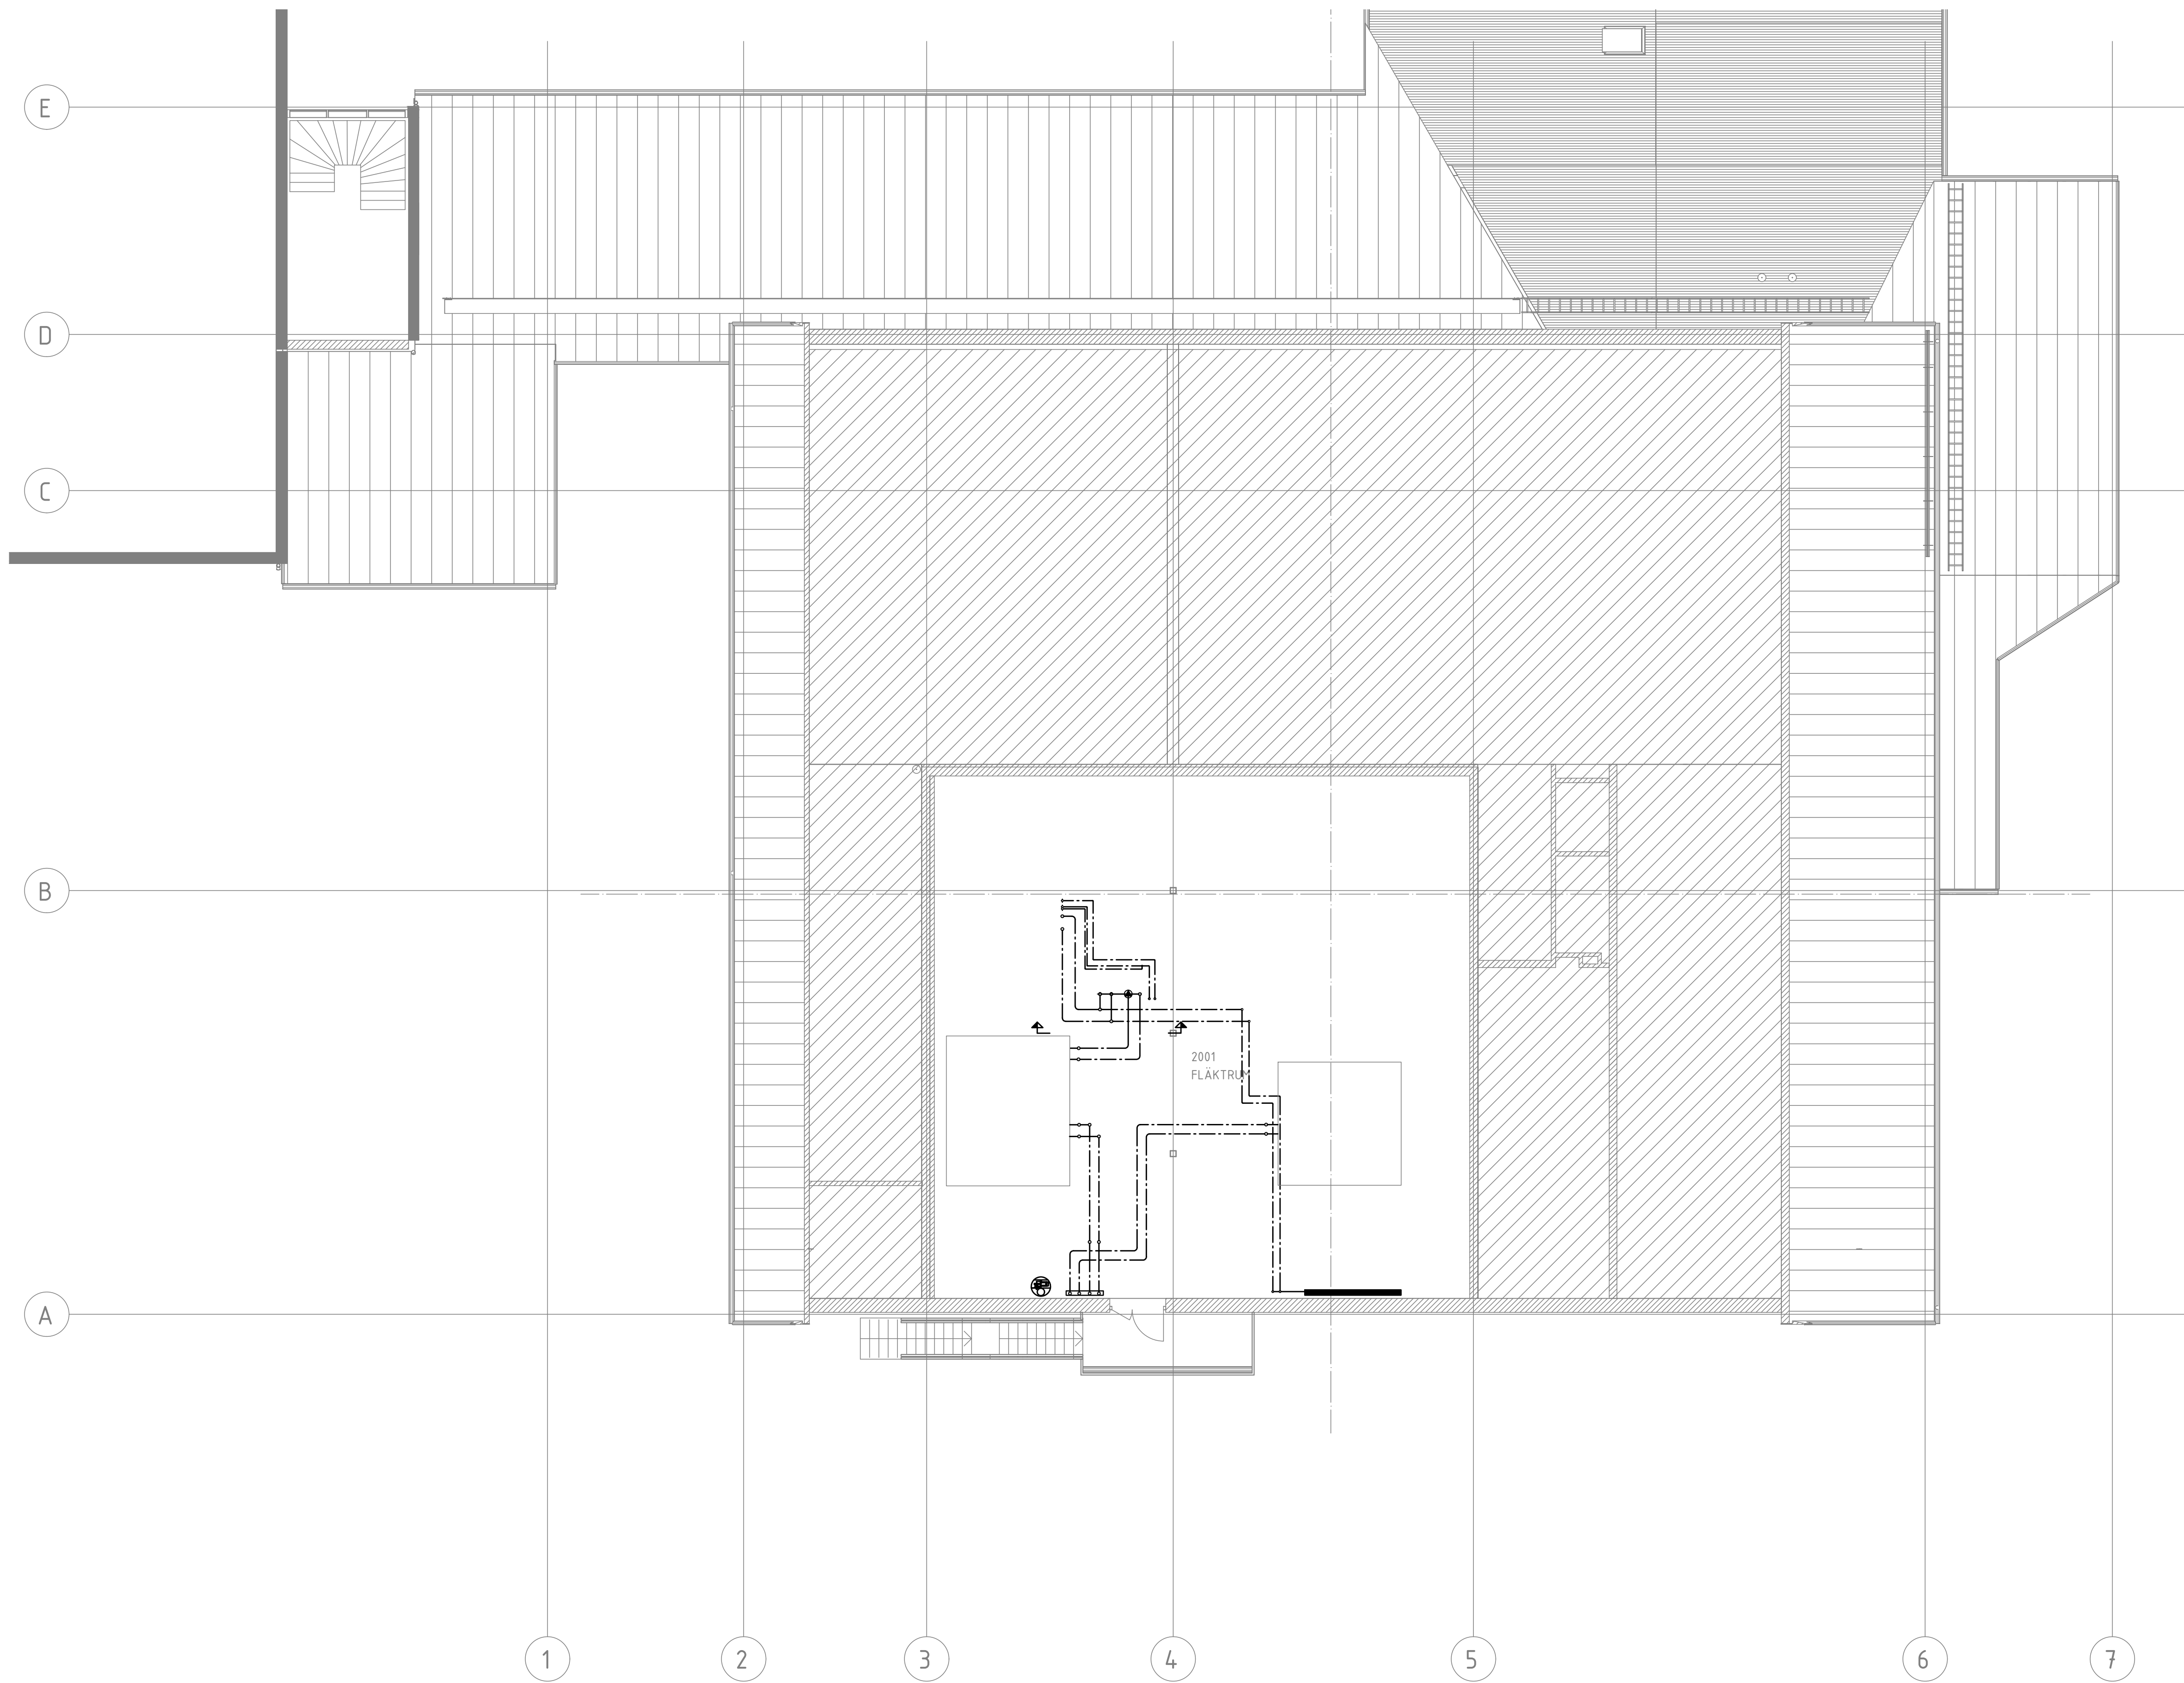


SEKTION

ORIENTERINGSPOL

STATUS

FÖRFRÅGNINGSUNDERLAG

HANDLING

BYGGHANDLING

DATUM 2024-12-20 GODKÄND AV T.BERGSTRÖM ANDRINGS PM

BESTÄLLARE

ROBERTSFORS
KOMMUN

PROJEKTNAMN

CENTRALKÖK

OMRADE

ROBERTSFORS KOMMUN

PROJEKTNUMMER FÖRETAG

YTTRE RINGVÄGEN 4

DIARIENUMMER FÄSTISHET FÖRDONET 1

DISCIPLIN FÖRETAG

VS NORCONSULT SVERIGE AB

ÖPPNINGSNUMMER SKAPAD AV

108 83 71 MAN

TELEFON: 010 141 80 00 HÖRSTADEN

JONAS JOHANSSON

BYGGNADSVÄRDE (KLIMATKORREKT)

+49 54 (FG)

YANINGSPLAN YANINGSDEL DELOMRÅDE

2 2 DEL 4, 5

SYSTEM

50 RÖRINSTALLATIONER

RESERVATION

PLAN 2 - ÖVERSIKT

RITNINGSKATEGORI SKALA FORMAT

PLAN 1:100 A1

DOKUMENTNUMMER ANDRNING

V-50-1-201