



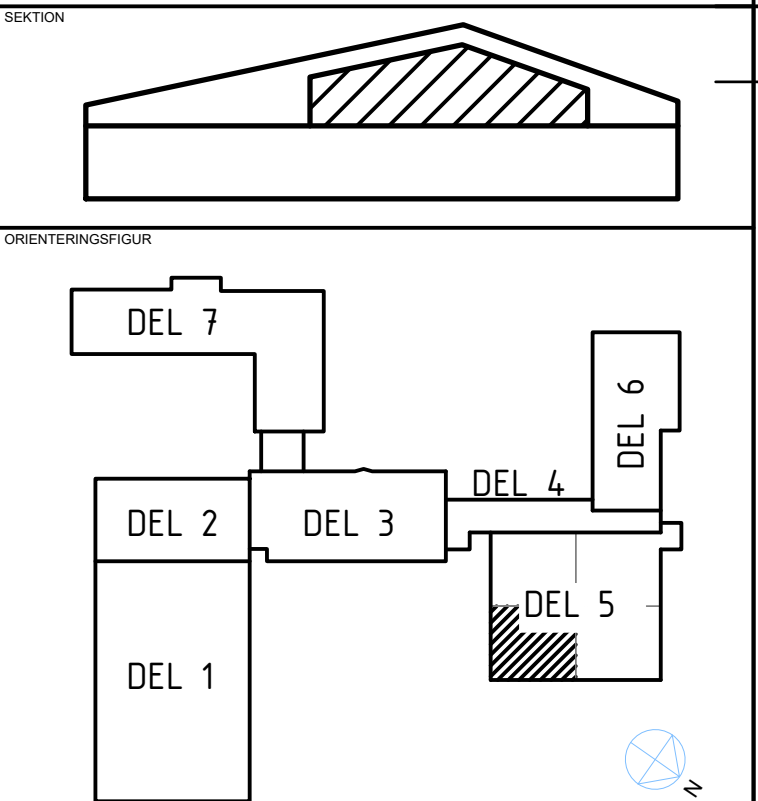

SEKTION		
ORIENTERINGSPÅR		
STATUS		
FÖRFRÅGNINGSUNDERLAG		
HANDLING		
BYGGHANDLING		
DATUM	GODKÄND AV	ÄNDRINGS PM
2024-12-20	T.BERGSTRÖM	
BESTÄLLARE		
ROBERTSFORS KOMMUN		
PROJEKTNAMN		
CENTRALKÖK		
OMRADE		
ROBERTSFORS KOMMUN		
PROJEKTNUMMER	FÖRRETT	
	YTIRE RINGVÄGEN 4	
DARIENUMMER	FASTIGHET	
	FORDONET 1	
DISCIPLIN	FÖRETAG	
VS	NORCONSULT SVERIGE AB	
OPPRÄGGSNUMMER	SKAPAD AV	
108 83 71	MAN	
TELEFON	KONTAKTPERSON	
010 141 80 00	JONAS JOHANSSON	
BYGGNADSVÄRDE	(KLIMATKORRIGERT)	
	+49,54 (FG)	
VÄNINGSPLAN	VÄNINGSDEL	DELOMRÅDE
2		DEL 5,3
SYSTEM		
50 RÖRINSTALLATIONER		
RITNINGSKATEGORI		
PLAN 2 - ÖVERSIKT		
RITNINGSKATEGORI	SKALA	FORMAT
PLAN	1:50	A1
DOKUMENTNUMMER	ÄNDRING	
V-50-1-253		

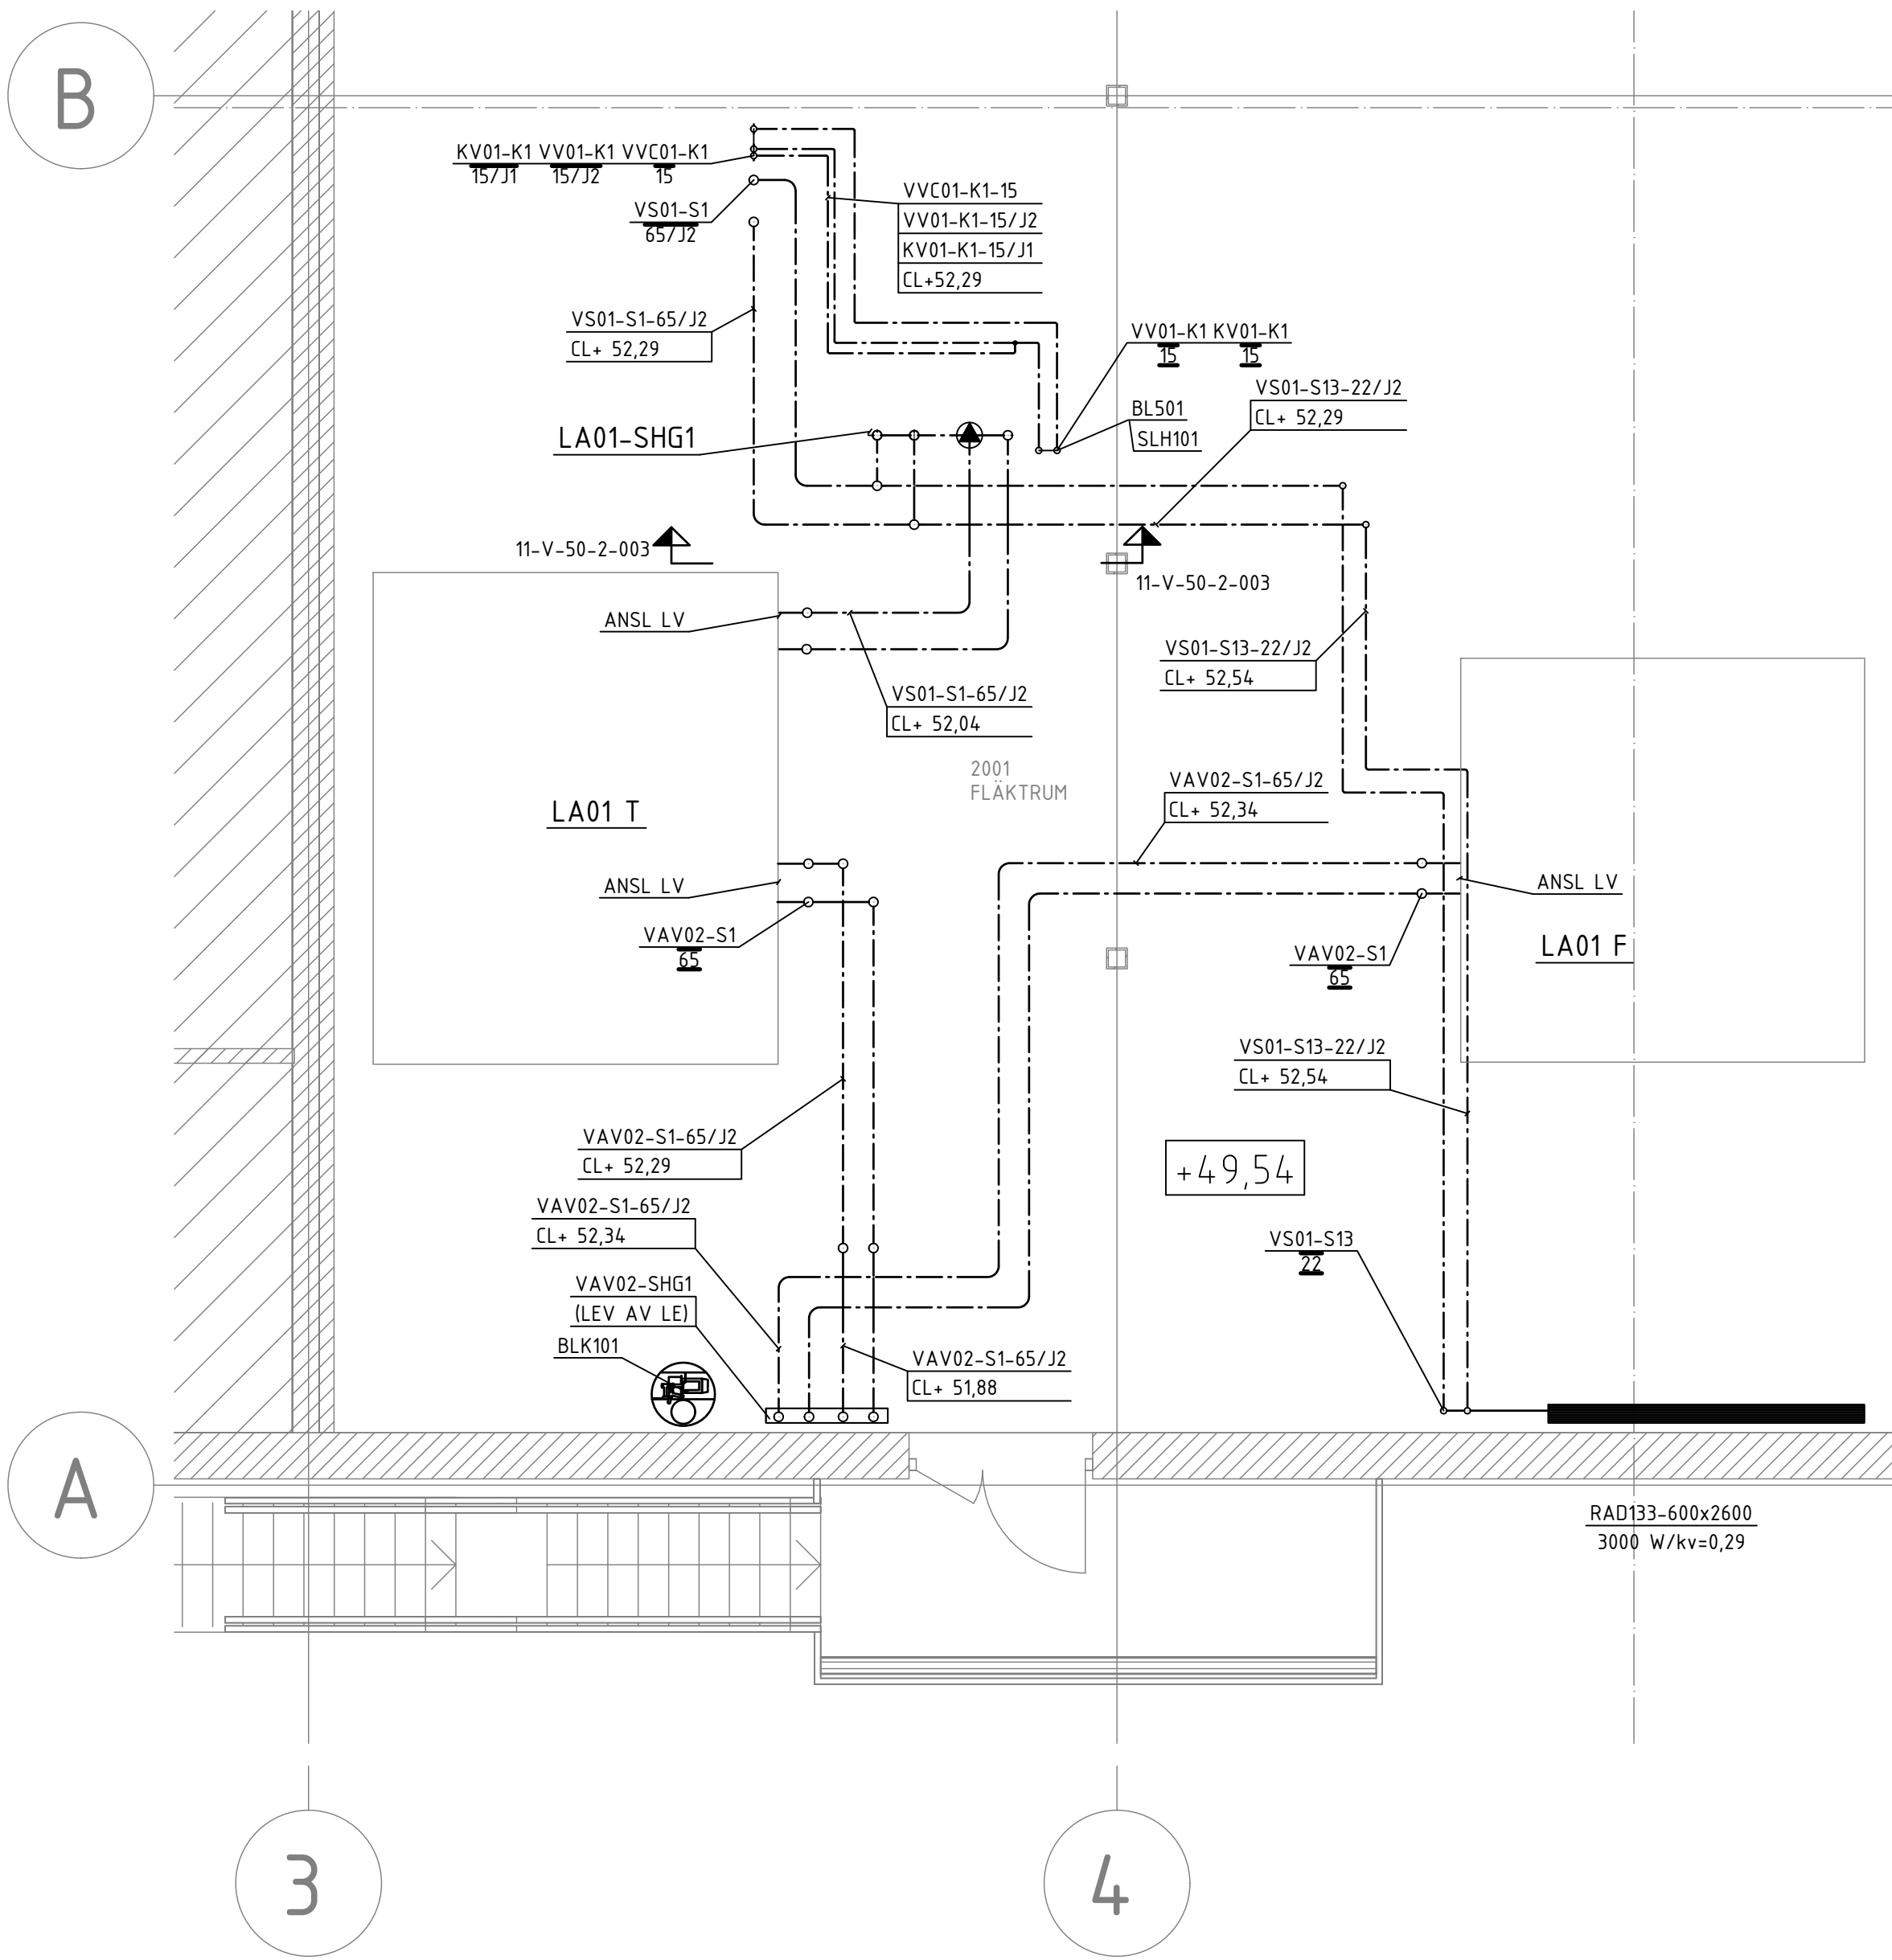