


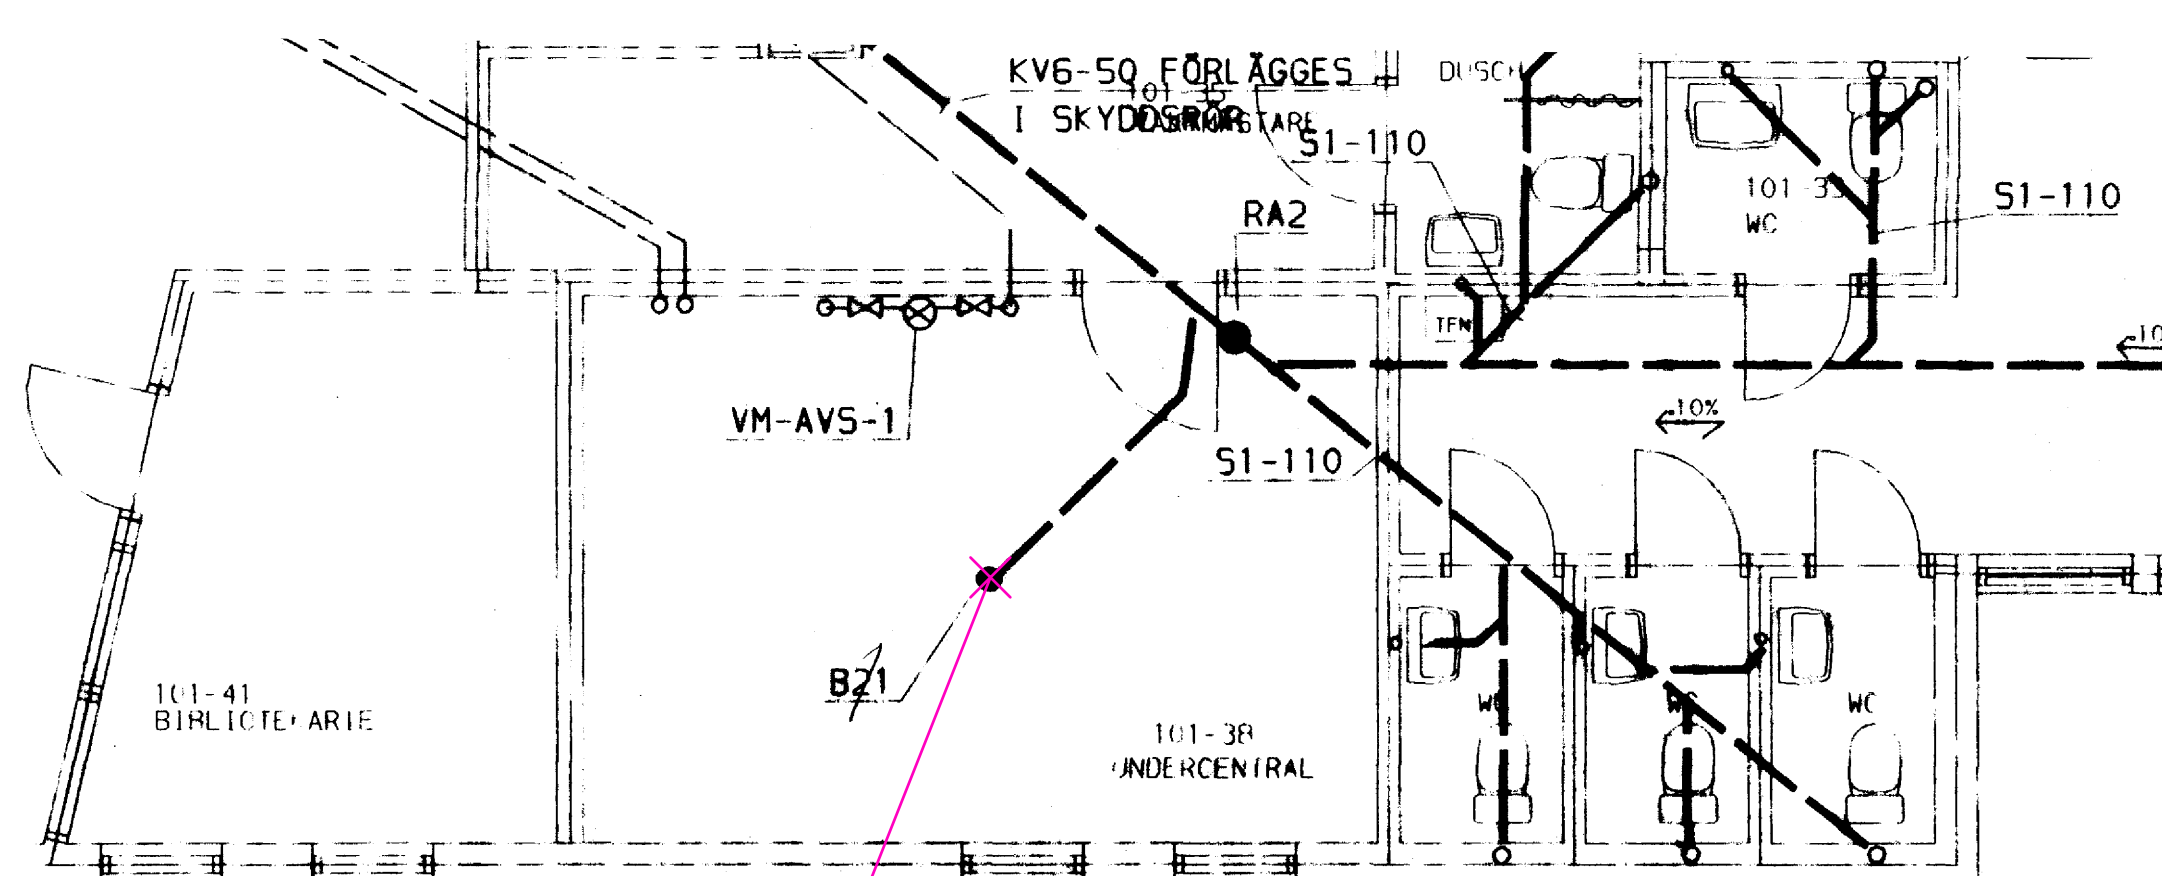

B	ARBETSRITNING		PK	941220
A	7	KFI	SB	941117
BET	ANT	ÄNDRINGEN AVSER	SVEN	DATUM

ARBETSRITNING				
GYMNASIESKOLA/SPORTHALL				
ROBERTSFORS KOMMUN				
				
VAB VVS		Husetten 408 53124 Skellefteå TEL. 0910-48600 FAX 0910-60400		
OPPLAG: 10	140-137	B	PK	SB
ARBET:	9394-11-07	1	SB	4
		ROLF BERGLUND ROLF BERGLUND		
GYMNASIESKOLA				
V5-ANLÄGGNING				
PLAN 1 DEL 3				
SKALA:	HÖJDER		IN	
1:50	V50:113		B	