


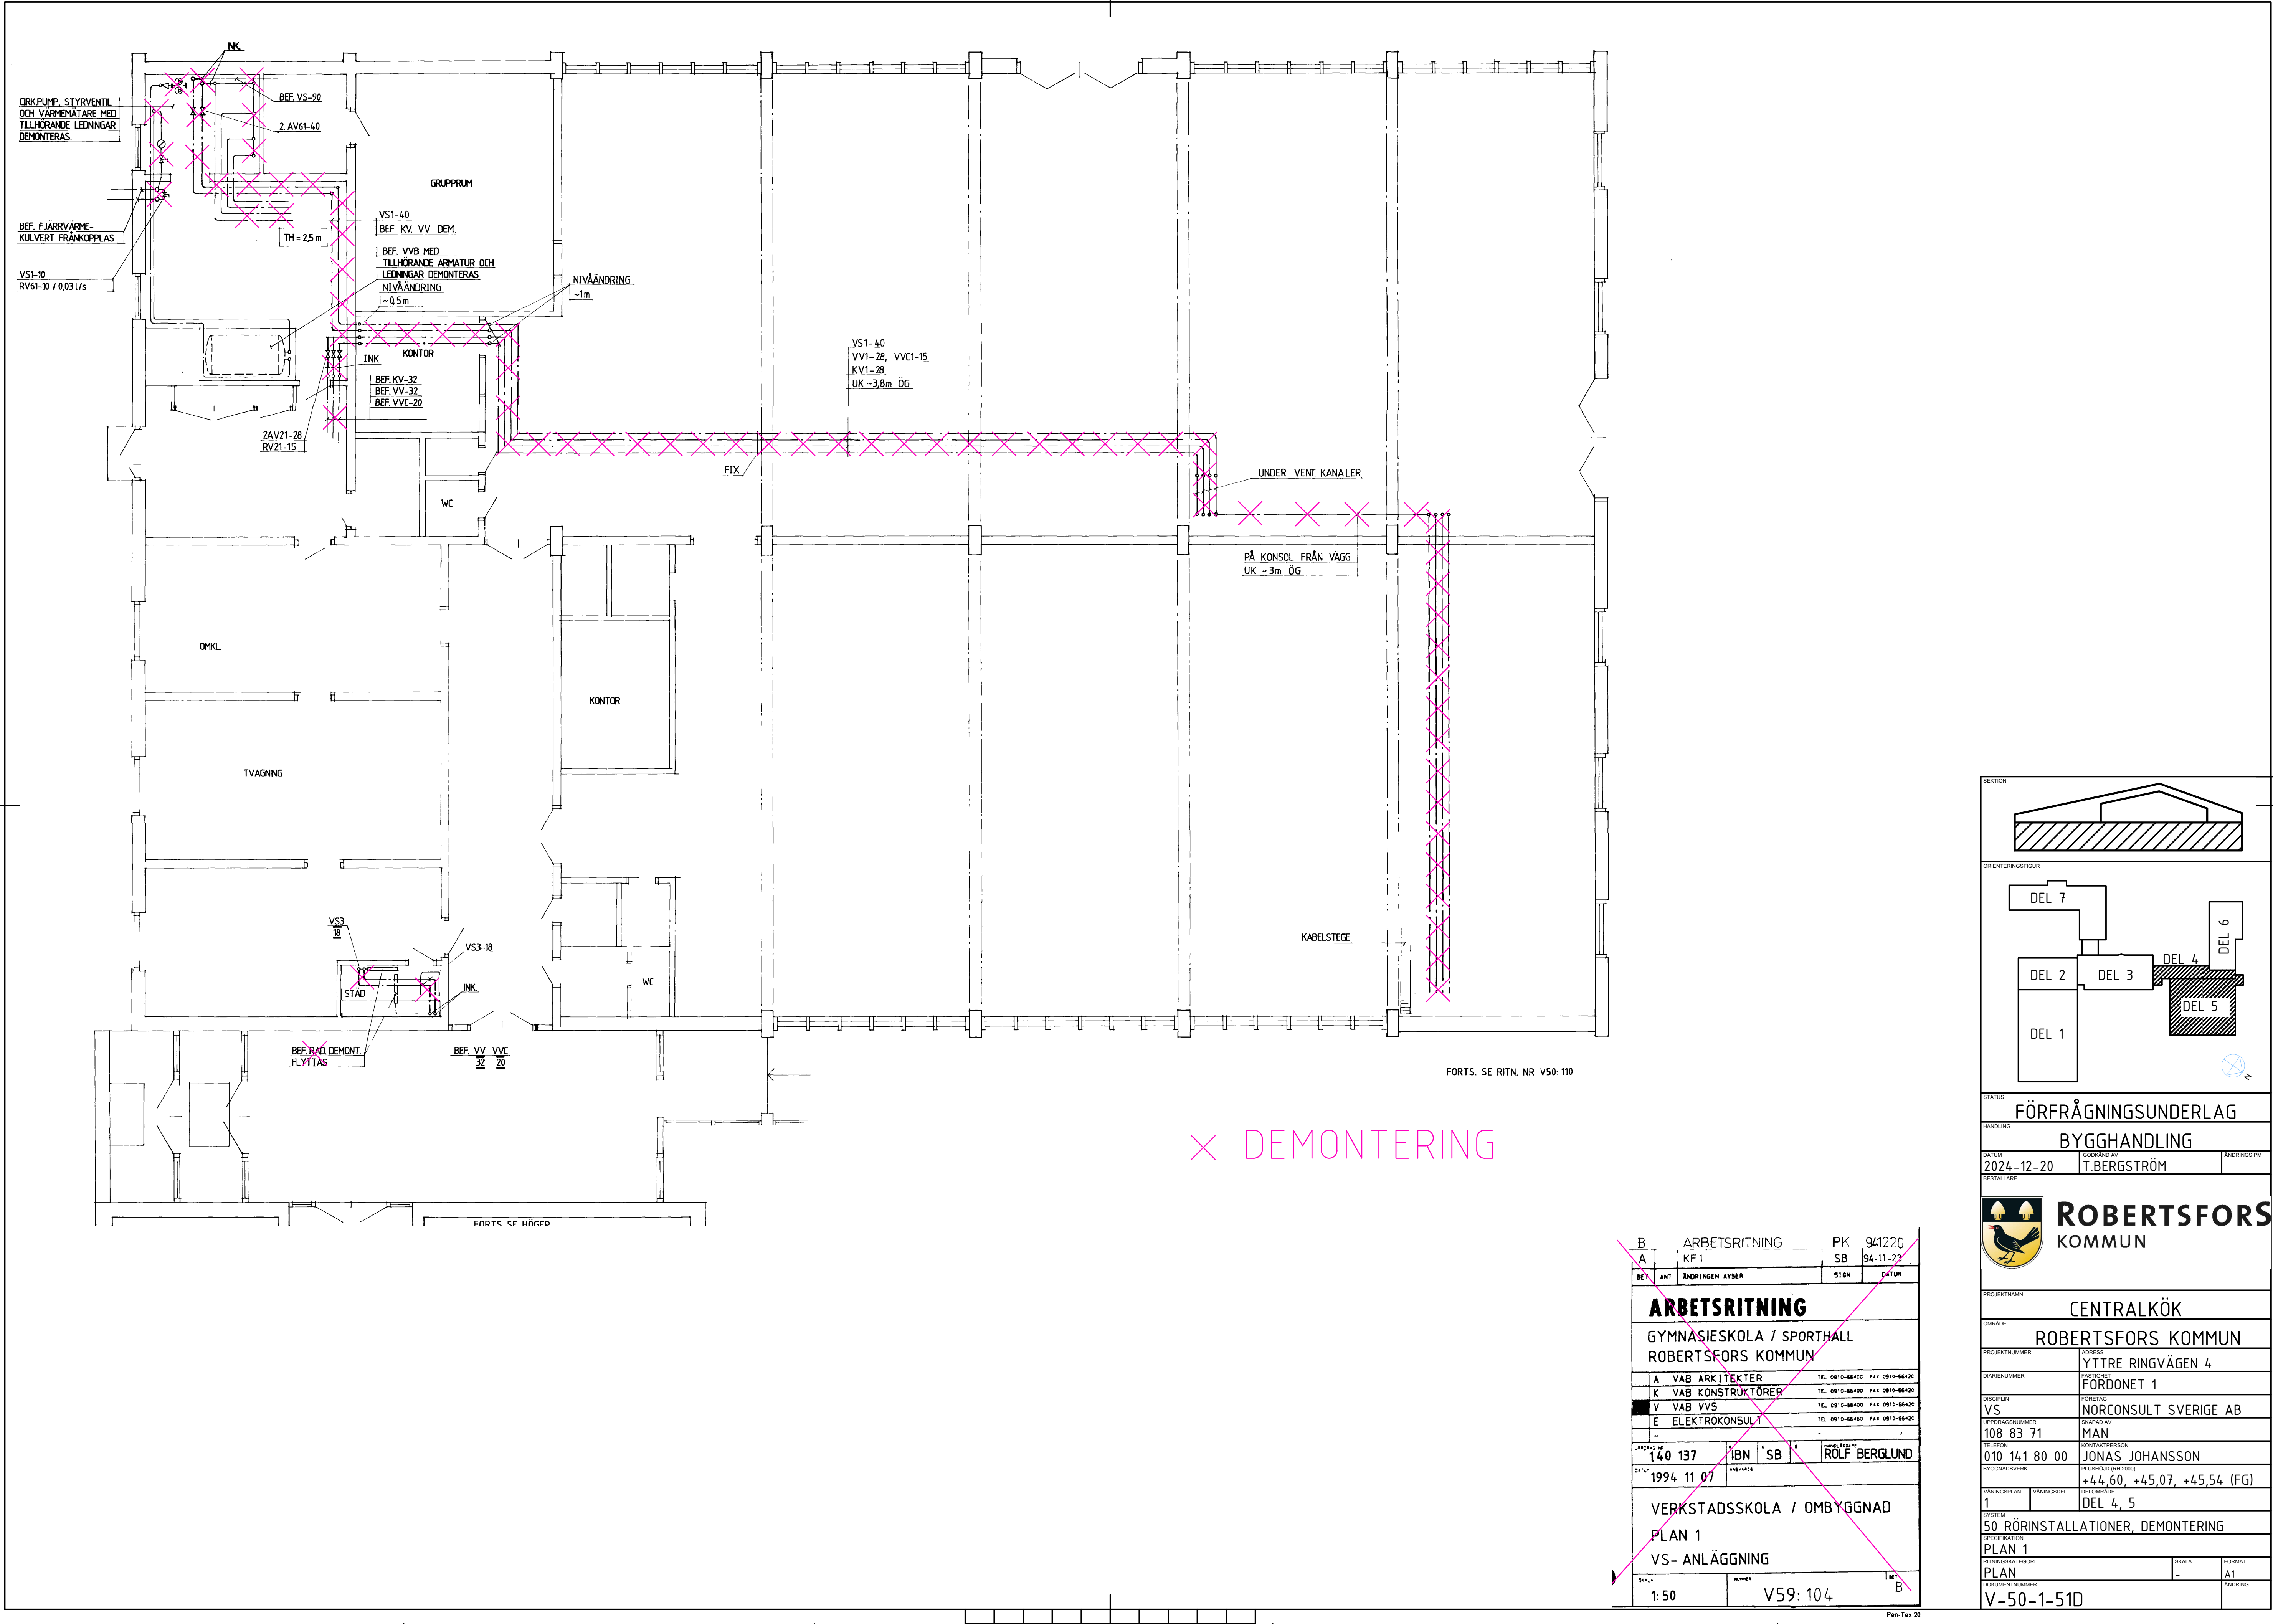

B		ARBETSRITNING		PK		941220	
A		KF 1		SB		94-11-23	
BEF.	ANT	ÄNDRINGEN ÄYSER			SIGN	DATUM	
ARBETSRITNING							
GYMNASIESKOLA / SPORSTALL							
ROBERTSFORS KOMMUN							
A		VAB ARKITEKTER		TE.	0910-66400	FAX	0910-66420
K		VAB KONSTRUKTÖRER		TE.	0910-66400	FAX	0910-66420
V		VAB VVS		TE.	0910-66400	FAX	0910-66420
E		ELEKTROKONSULT		TE.	0910-66400	FAX	0910-66420
..							
ARBETS- PLÅN		140	137	IBN	SB	RÖLF BERGLUND	
DÅTUM		1994 11 07					
VERKSTADSSKOLA / OMBYGGNAD							
PLAN 1							
VS- ANLÄGGNING							
MÅST.:		1:50		V59: 104		B	

SEKTION

ORIENTERINGSSKISS

STATUS

FÖRFRÅGNINGSUNDERLAG

HANDLING

BYGGHANDLING

DATUM

2024-12-20

SOCKLAND AV

T.BERGSTRÖM

ÄNDRINGS PR

BESTÄLLARE

ROBERTSFORS KOMMUN

PROJEKTNAMN

CENTRALEKÖK

OMRÅDE

ROBERTSFORS KOMMUN

PROJEKTNUMMER

YTTRE RINGVÄGEN 4

DIARIENUMMER

FÖRDONET 1

DISCIPLIN

NORCONSULT SVERIGE AB

UPPDRAGSNUMMER

108 83 71

TELEFON

010 141 80 00

BYGGNADSVÄRK

+44,60, +45,07, +45,54 (FG)

VÄNINGSPLAN

1

VÄNINGSDEL

DEL 4, 5

SYSTEM

50 RÖRINSTALLATIONER, DEMONTING

OPERATION

PLAN 1

RYTNINGSKATEGORI

PLAN

DOKUMENTNUMMER

V-50-1-51D

SKALA

A1

ÄNDRING

FILNAMN: C:\USERS\NAGMAN\ONE DRIVE - NORCONSULT\GROUP\DESKTOP\ROBERTSFORS\02 BYGGBYTTEN\BYGGBYTTEN\50-1-51D\DWG\PL01.DWG 2024-12-19 09:54 AV ANVÄNDARE NAGMAN