
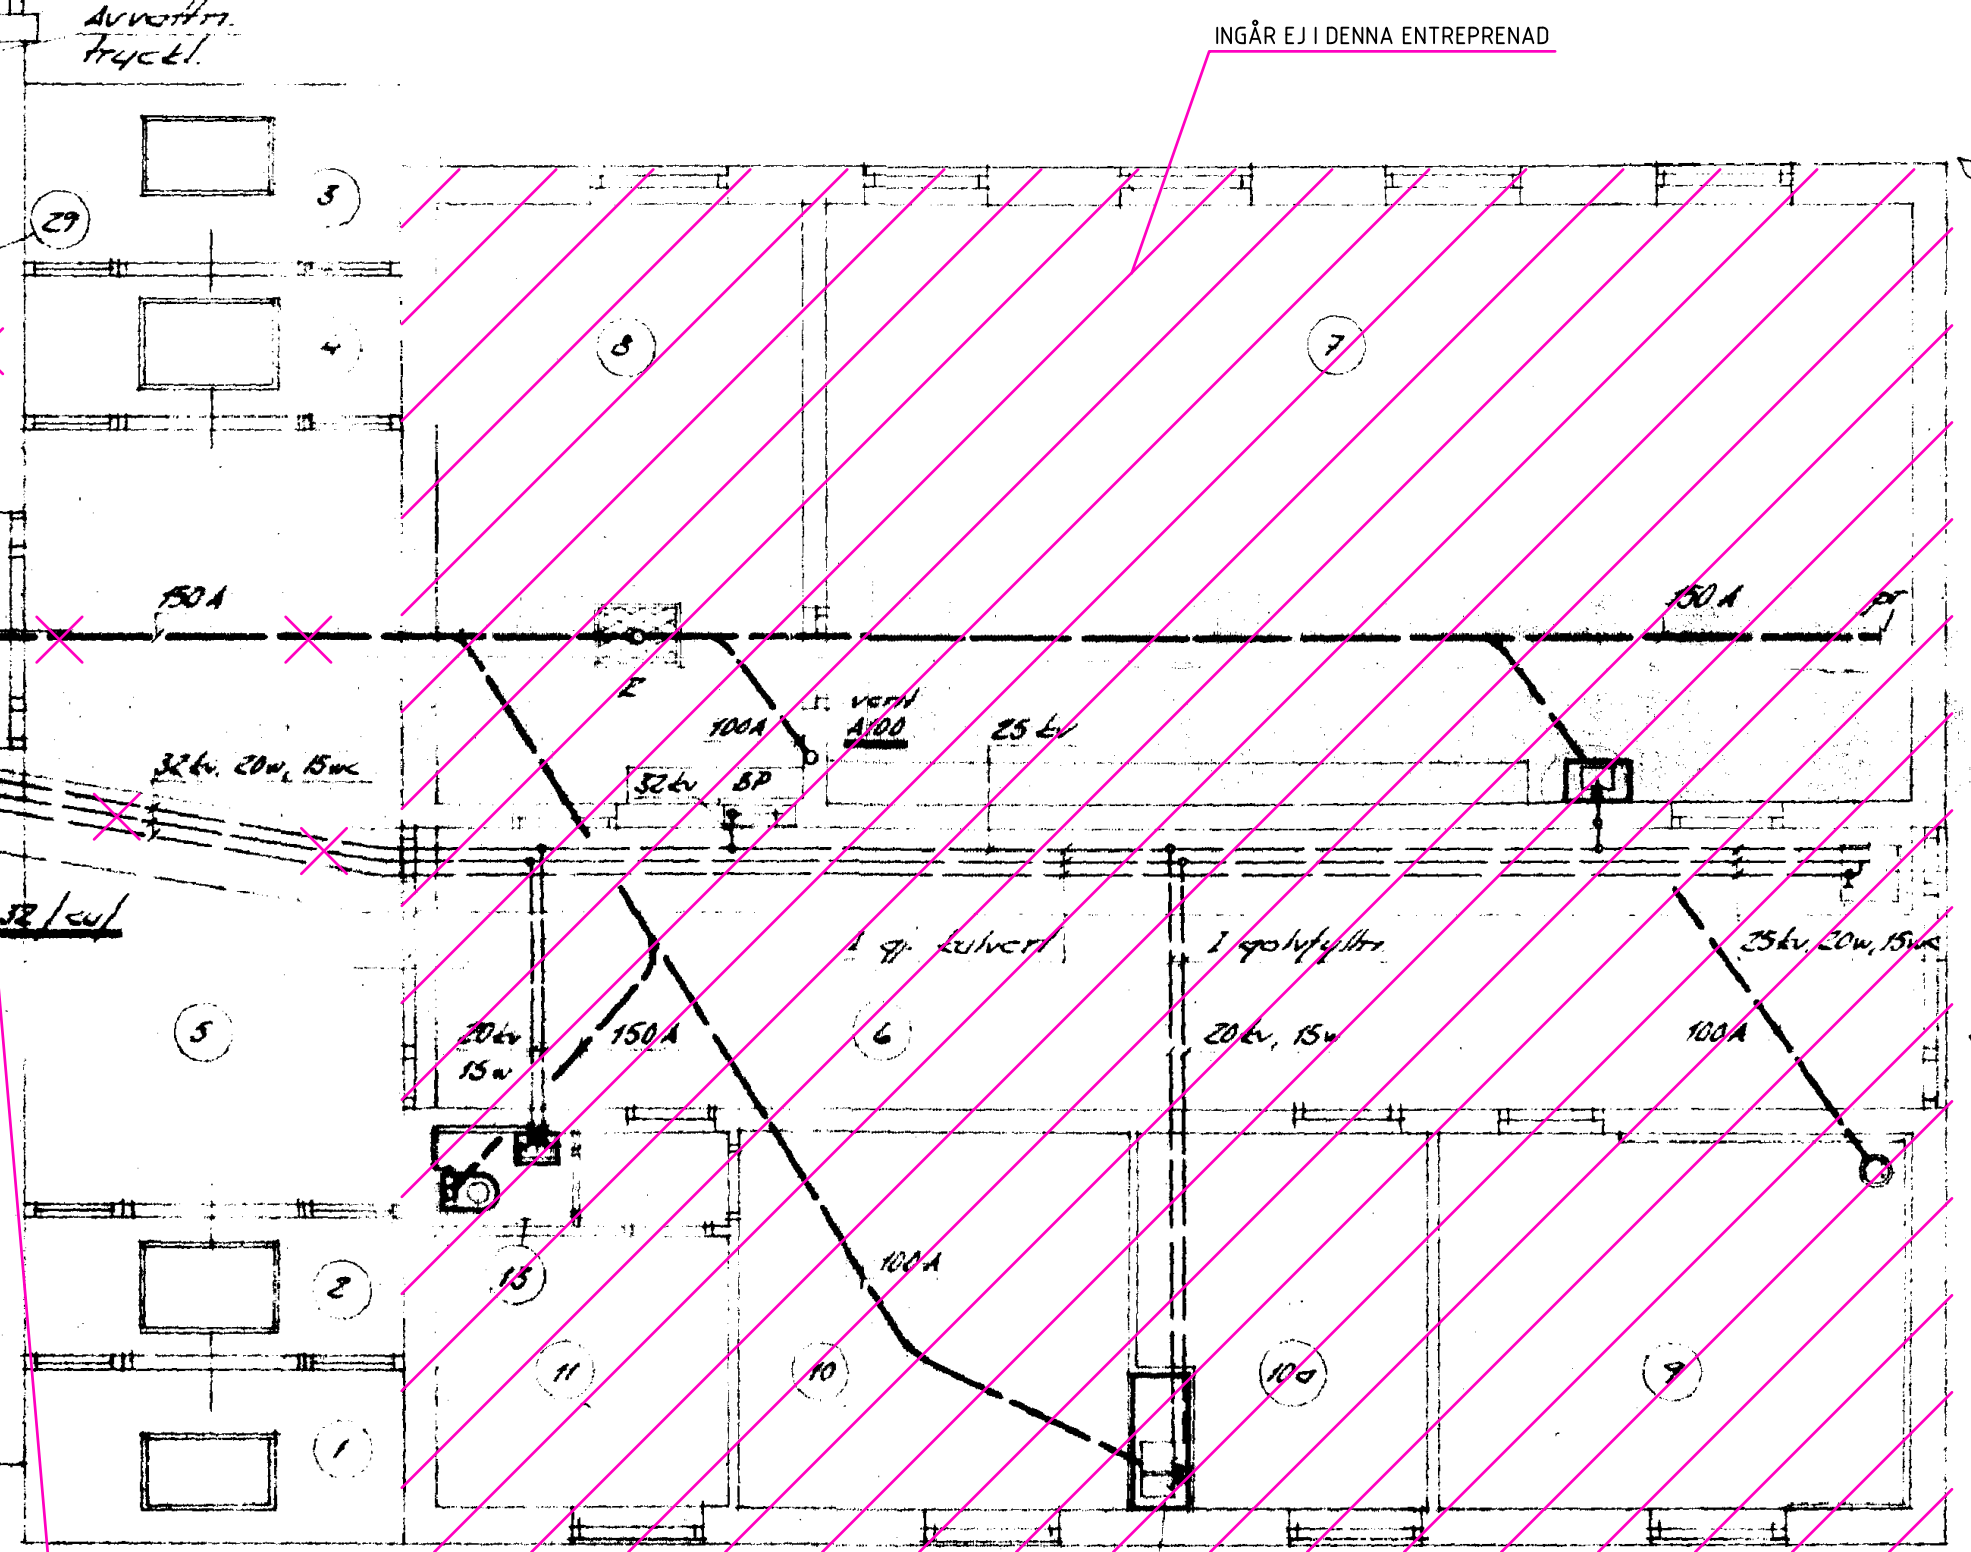
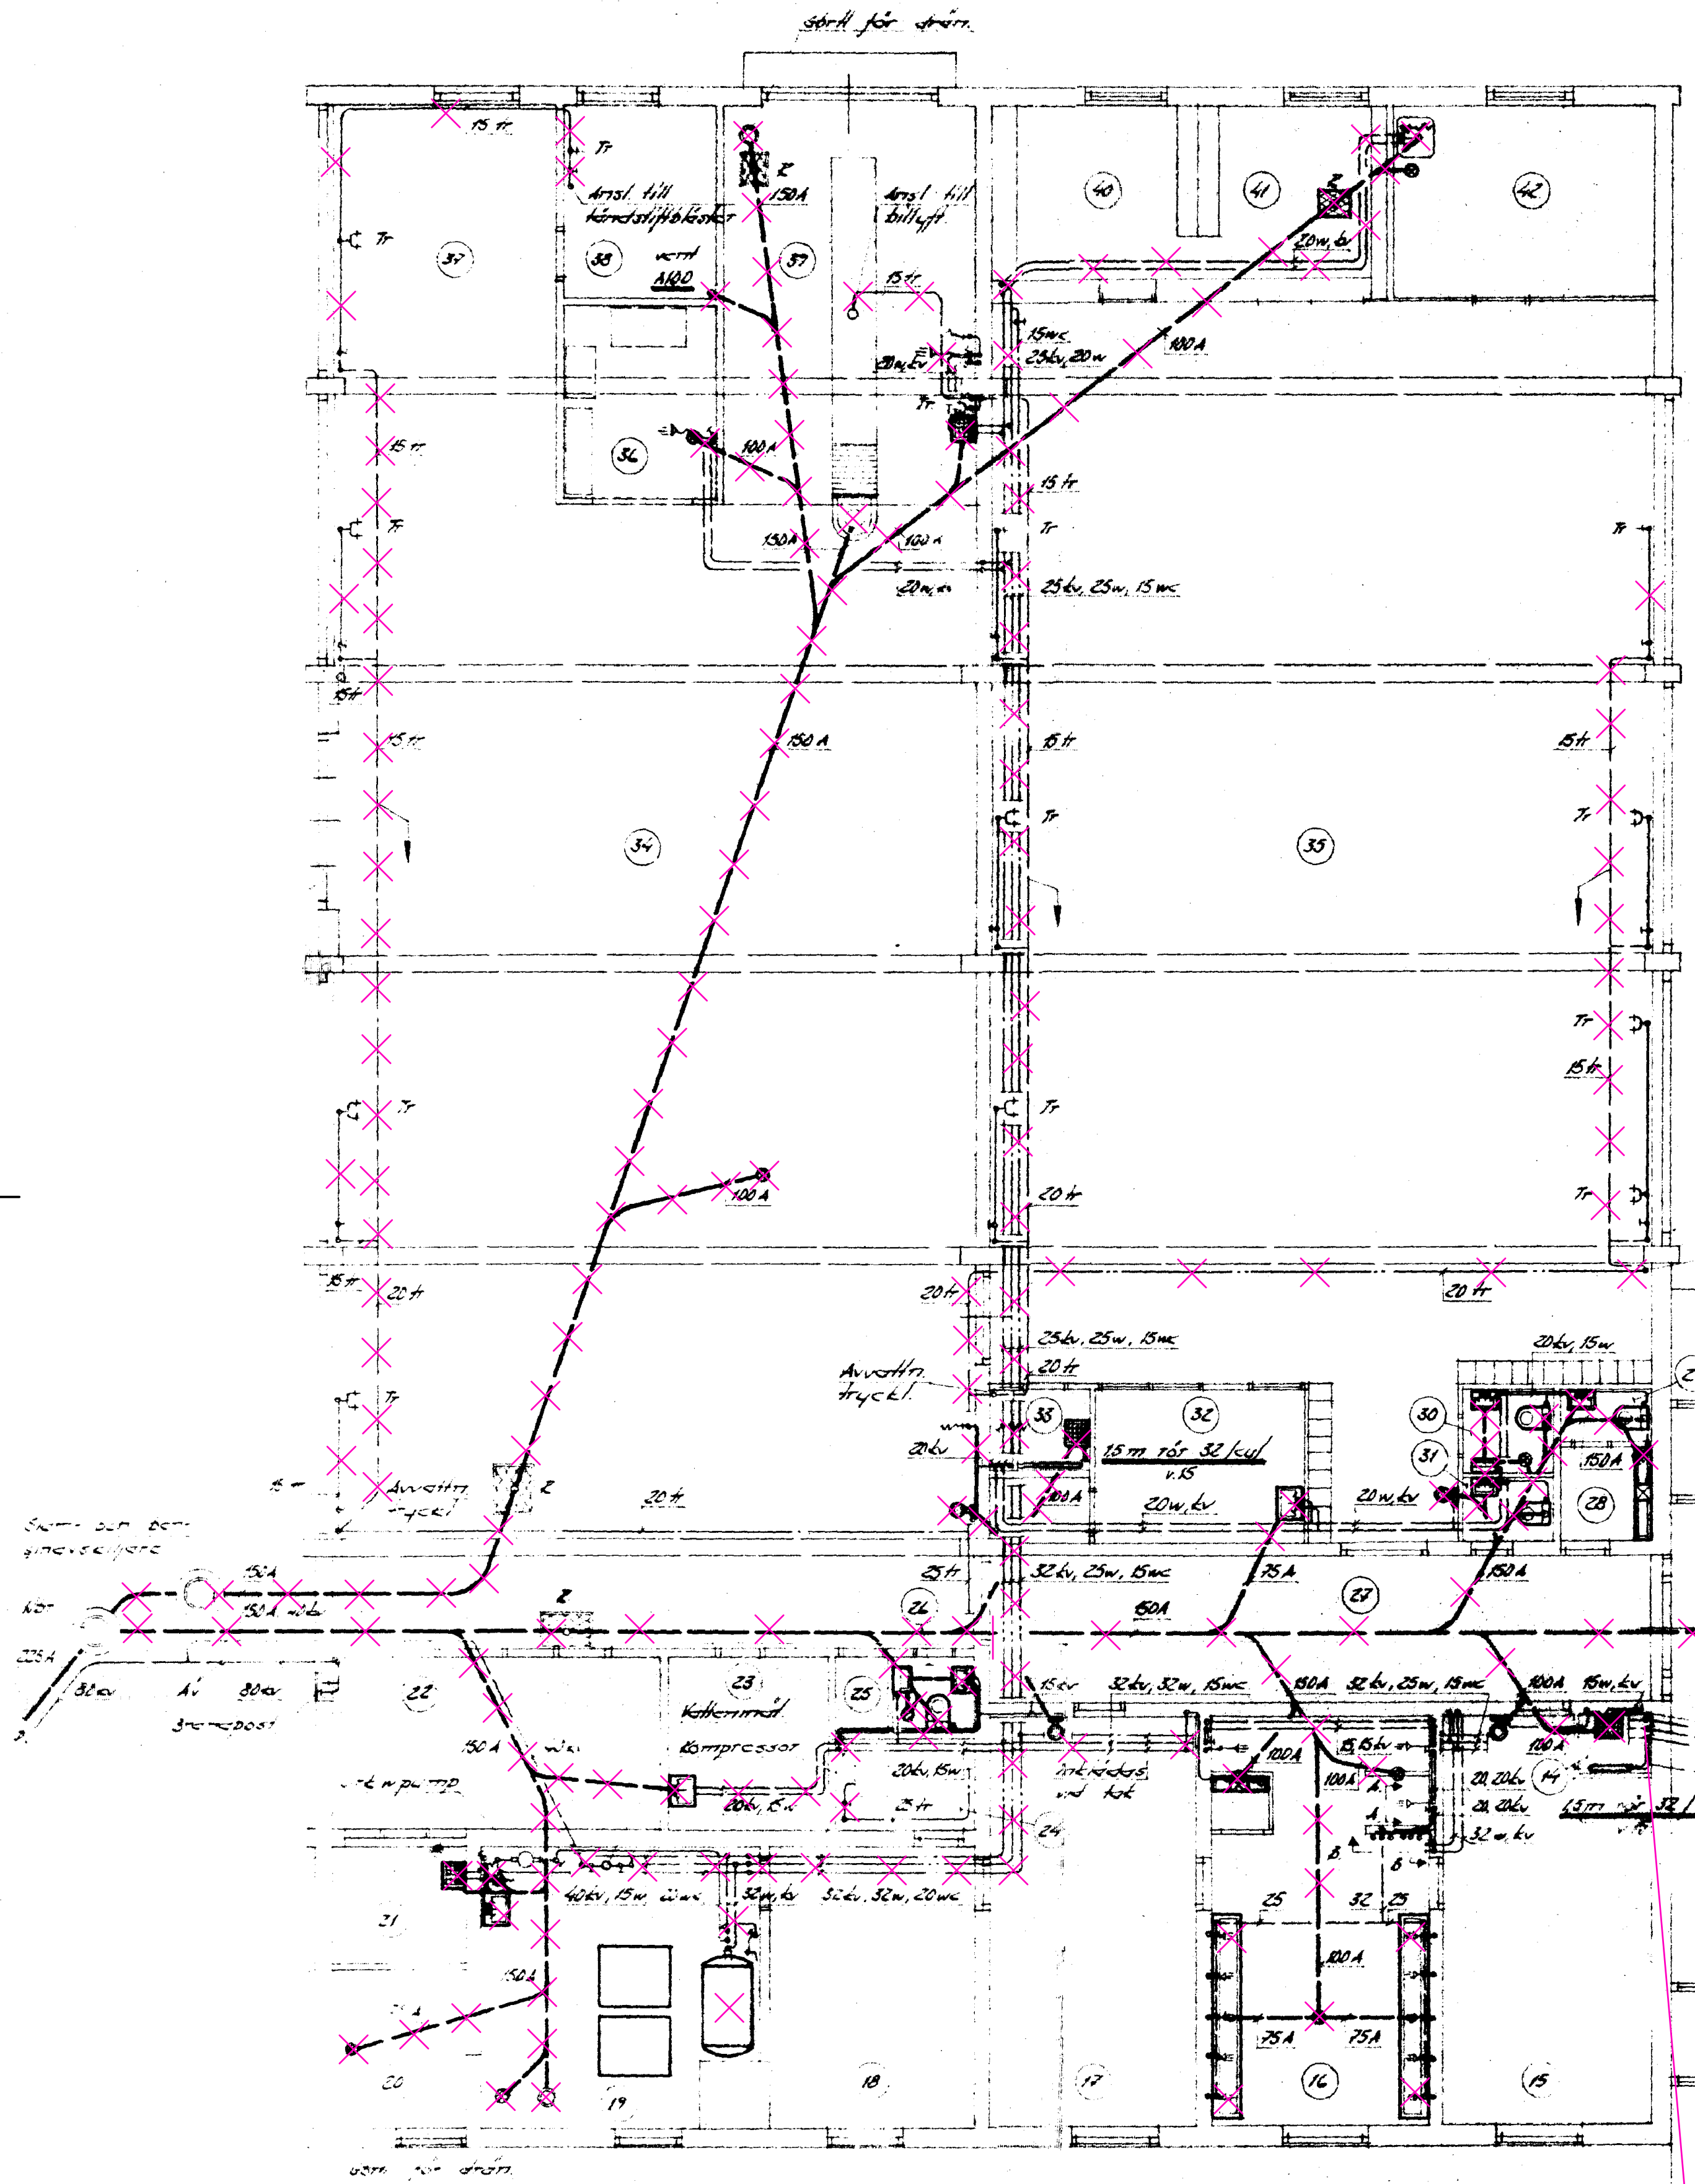


YRKESSKOLA I ROBERTSFORS
Sanitetsteknisk anläggning mm.
Plan - Detalj

S HEDENS INGENJÖRSBYRÅ			
Ing. R. Sandström			
Uppg.	Proj. 5410		
Granskad	Datum	Skala	Km. nr
24/5	1958	1:100	591-5
24/5	1958	1:20	

× DEMONTERING

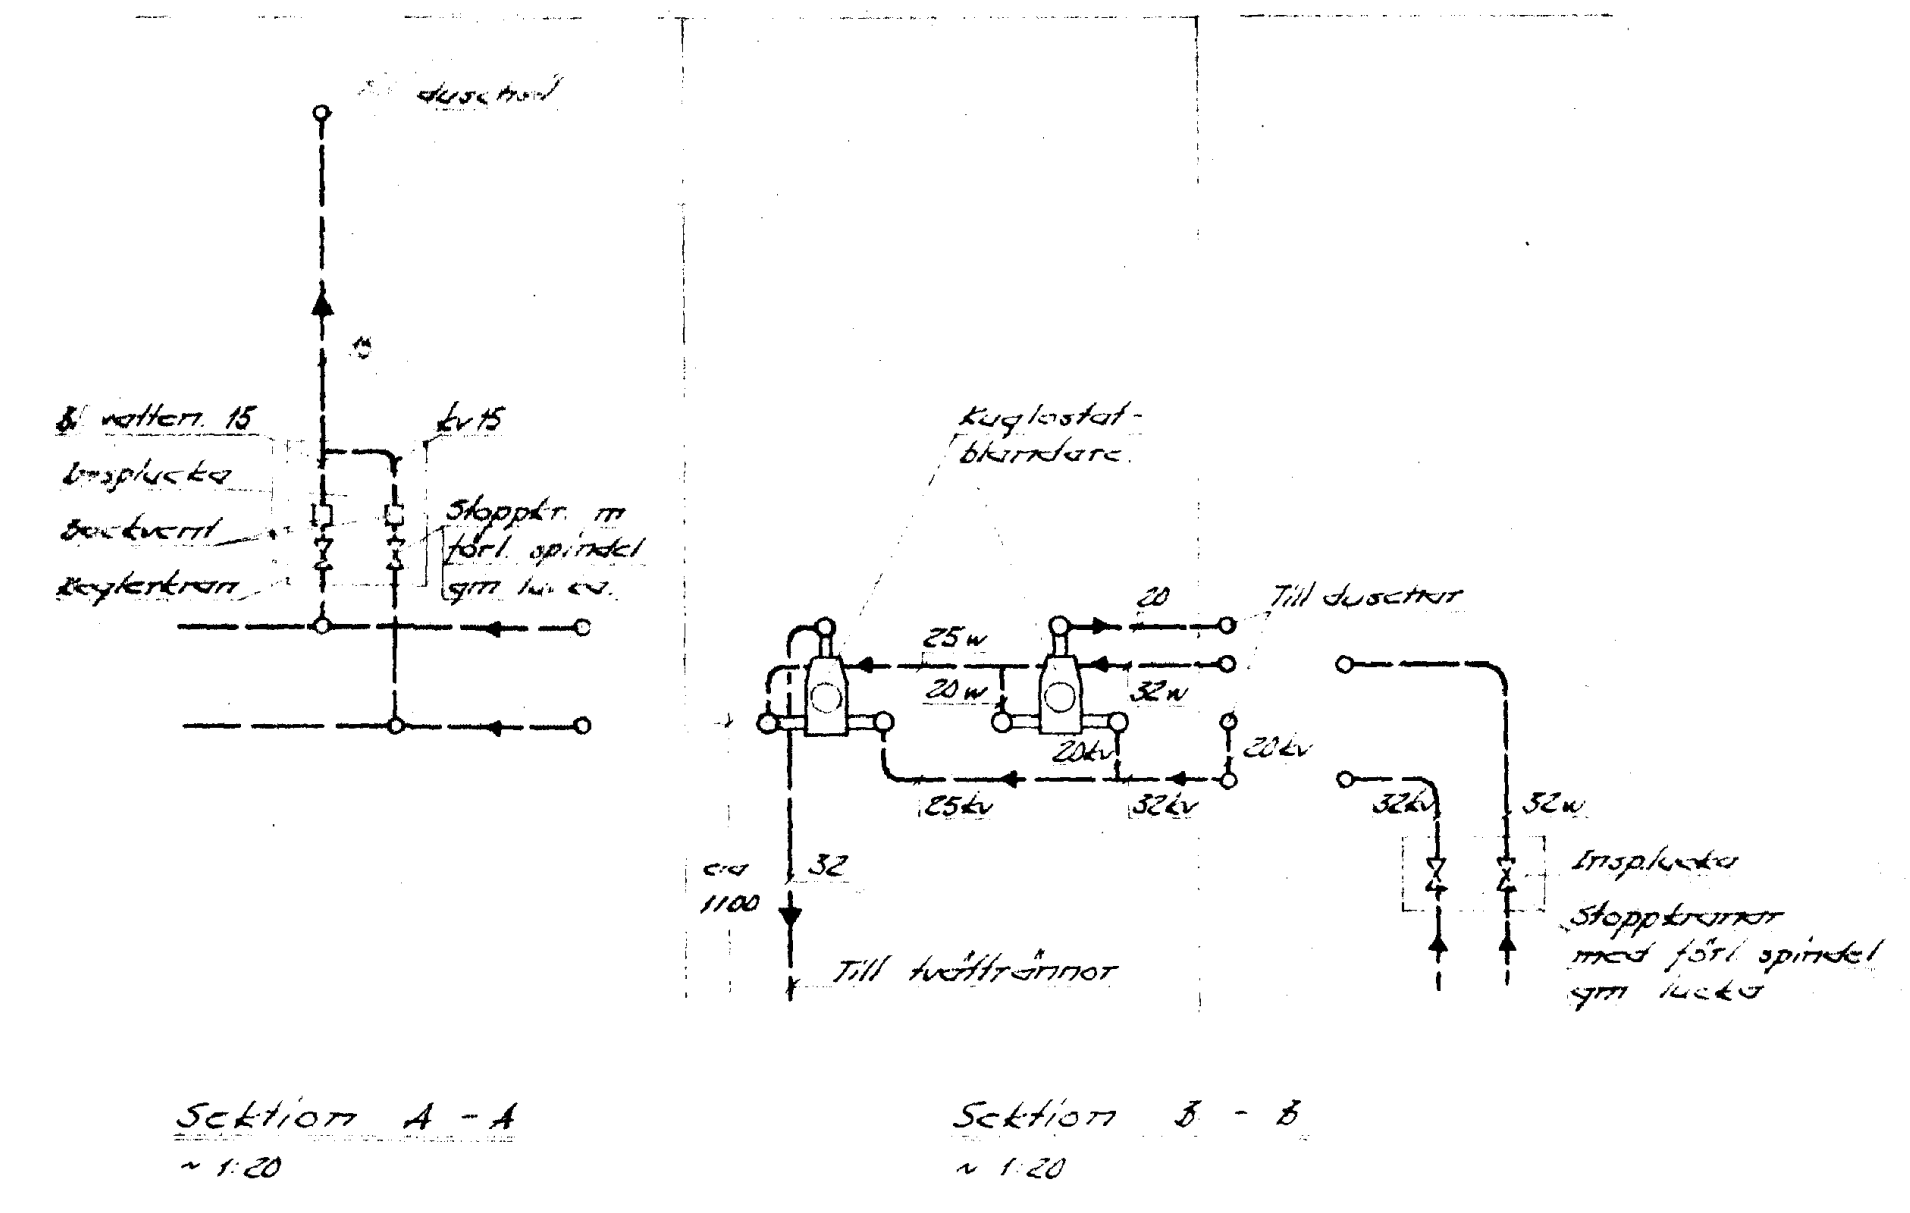

Befintlig KV/VV/VVC-ledning
demonteras. Nya ledningar ansluts
till befintliga vid golv

SEKTION

STATUS

FÖRFRÅGNINGSUNDERLAG

HANDLING

BYGGHANDLING

DATUM

2024-12-20

REVISOR

T.BERGSTRÖM

REVISOR

T.BERGSTRÖM

ROBERTSFORS
KOMMUN

PROJEKTNAMN

CENTRALEKÖK

OMRÅDE

ROBERTSFORS KOMMUN

PROJEKTNUMMER

YTTRE RINGVÄGEN 4

DIAGRAMNUMMER

FÖRORDNING 1

DISCIPLIN

VS

UPPDRAGSNUMMER

108 83 71

TELEFON

010 141 80 00

BYGGNADSVÄRKS

+44,60, +45,07, +45,54 (FG)

VÄNINGSPLAN

1

VÄNINGSDEL

DEL 4, 5

SYSTEM

50 RÖRINSTALLATIONER, DEMONTERING

OPERATION

PLAN 1

KATEGORI

PLAN

DOKUMENTNUMMER

V-50-1-52D