


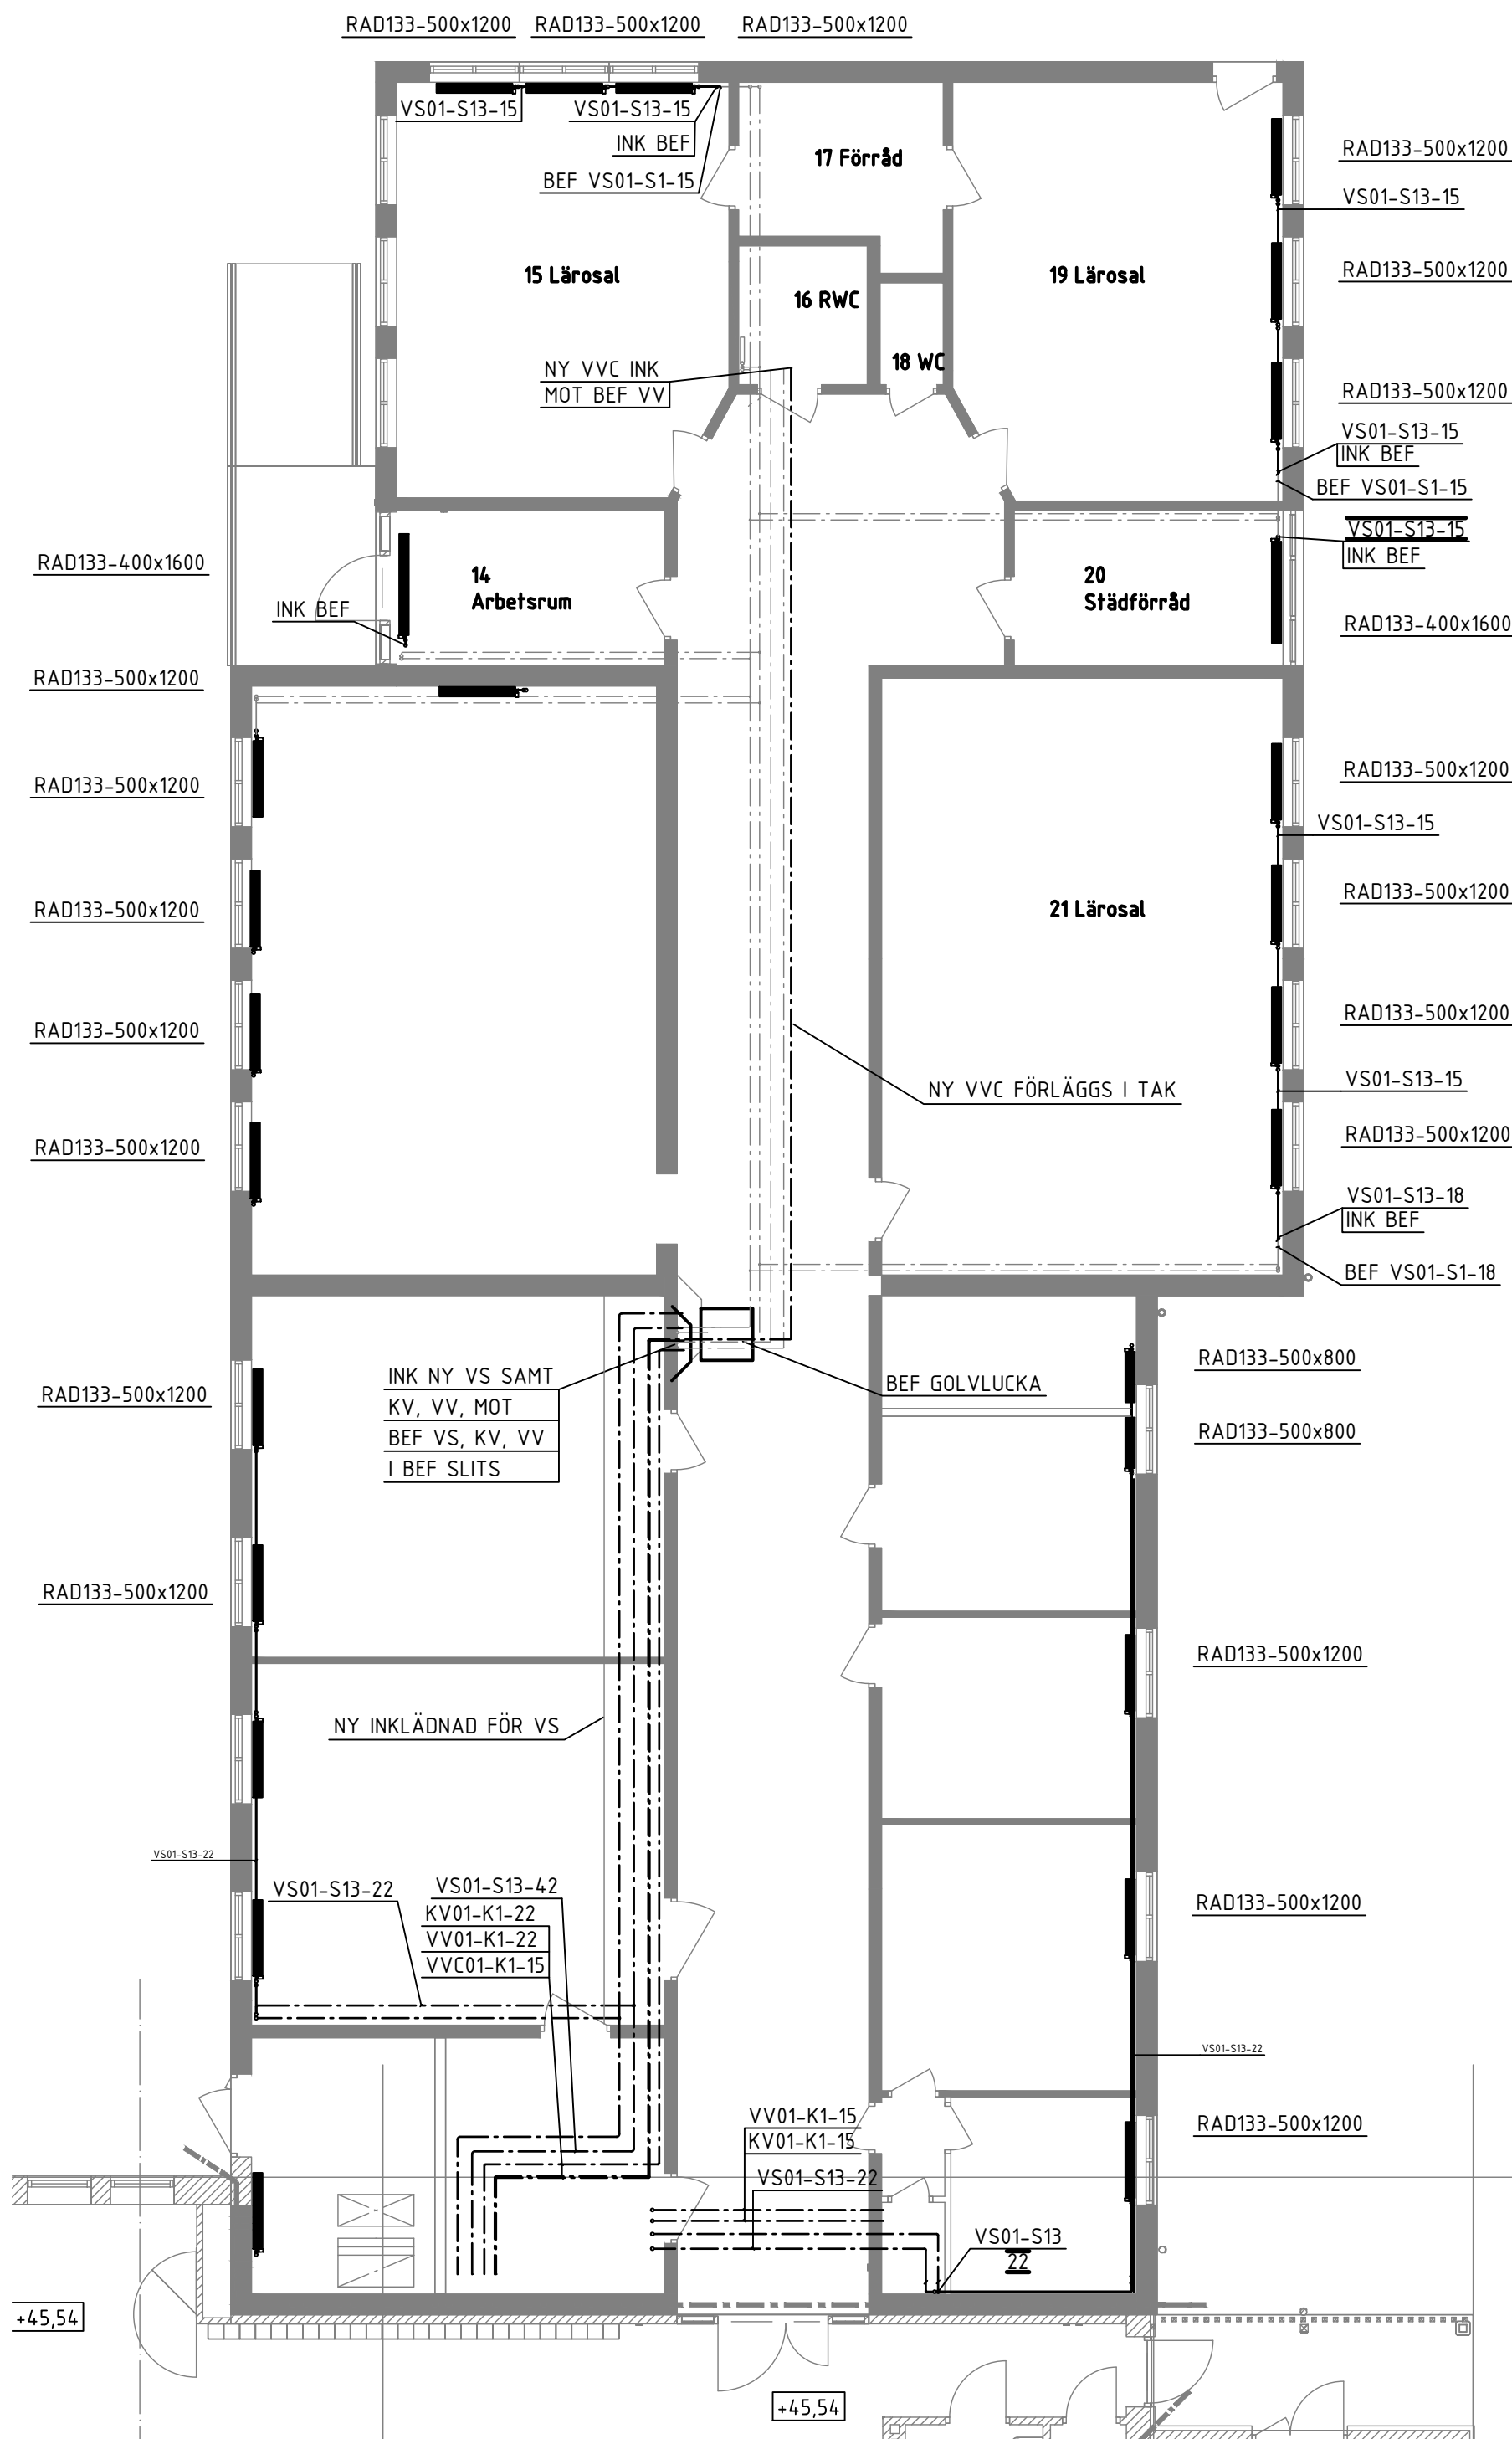

RÖRINSTALLATIONER
SKALA 1:100


NYA RADIATORER PÅ DENNA RITNING: SKA ERSÄTTA BEFINTLIGA FÖLJANDE RADIATORER:

BEFINTLIG BYGGNAD ÅR 1958
SEKTIONSRADIATOR 27-59-T: 5st
AEROVENT: 1st
SEKTIONSRADIATOR 27-59-NI: 1st
SEKTIONSRADIATOR 37-59-R: 1st
SEKTIONSRADIATOR 40-59-R: 1st



BEFINTLIG BYGGNAD ÅR 1968
SEKTIONSRADIATOR 27-59-D: 3st
SEKTIONSRADIATOR 99-30-MP: 1st
TP11-512: 1st

BEFINTLIG BYGGNAD ÅR 2001
TP11-512: 10st
TP11-416: 2st

DESSA BEFINTLIGA RADIATORER MED ANSLUTNINGSRÖR OCH KOPPEL SKA DEMONTERAS.
DESSA BEFINTLIGA RADIATORER FRAMGÅR ÄVEN I SEPARAT BILAGA, BILAGA 2

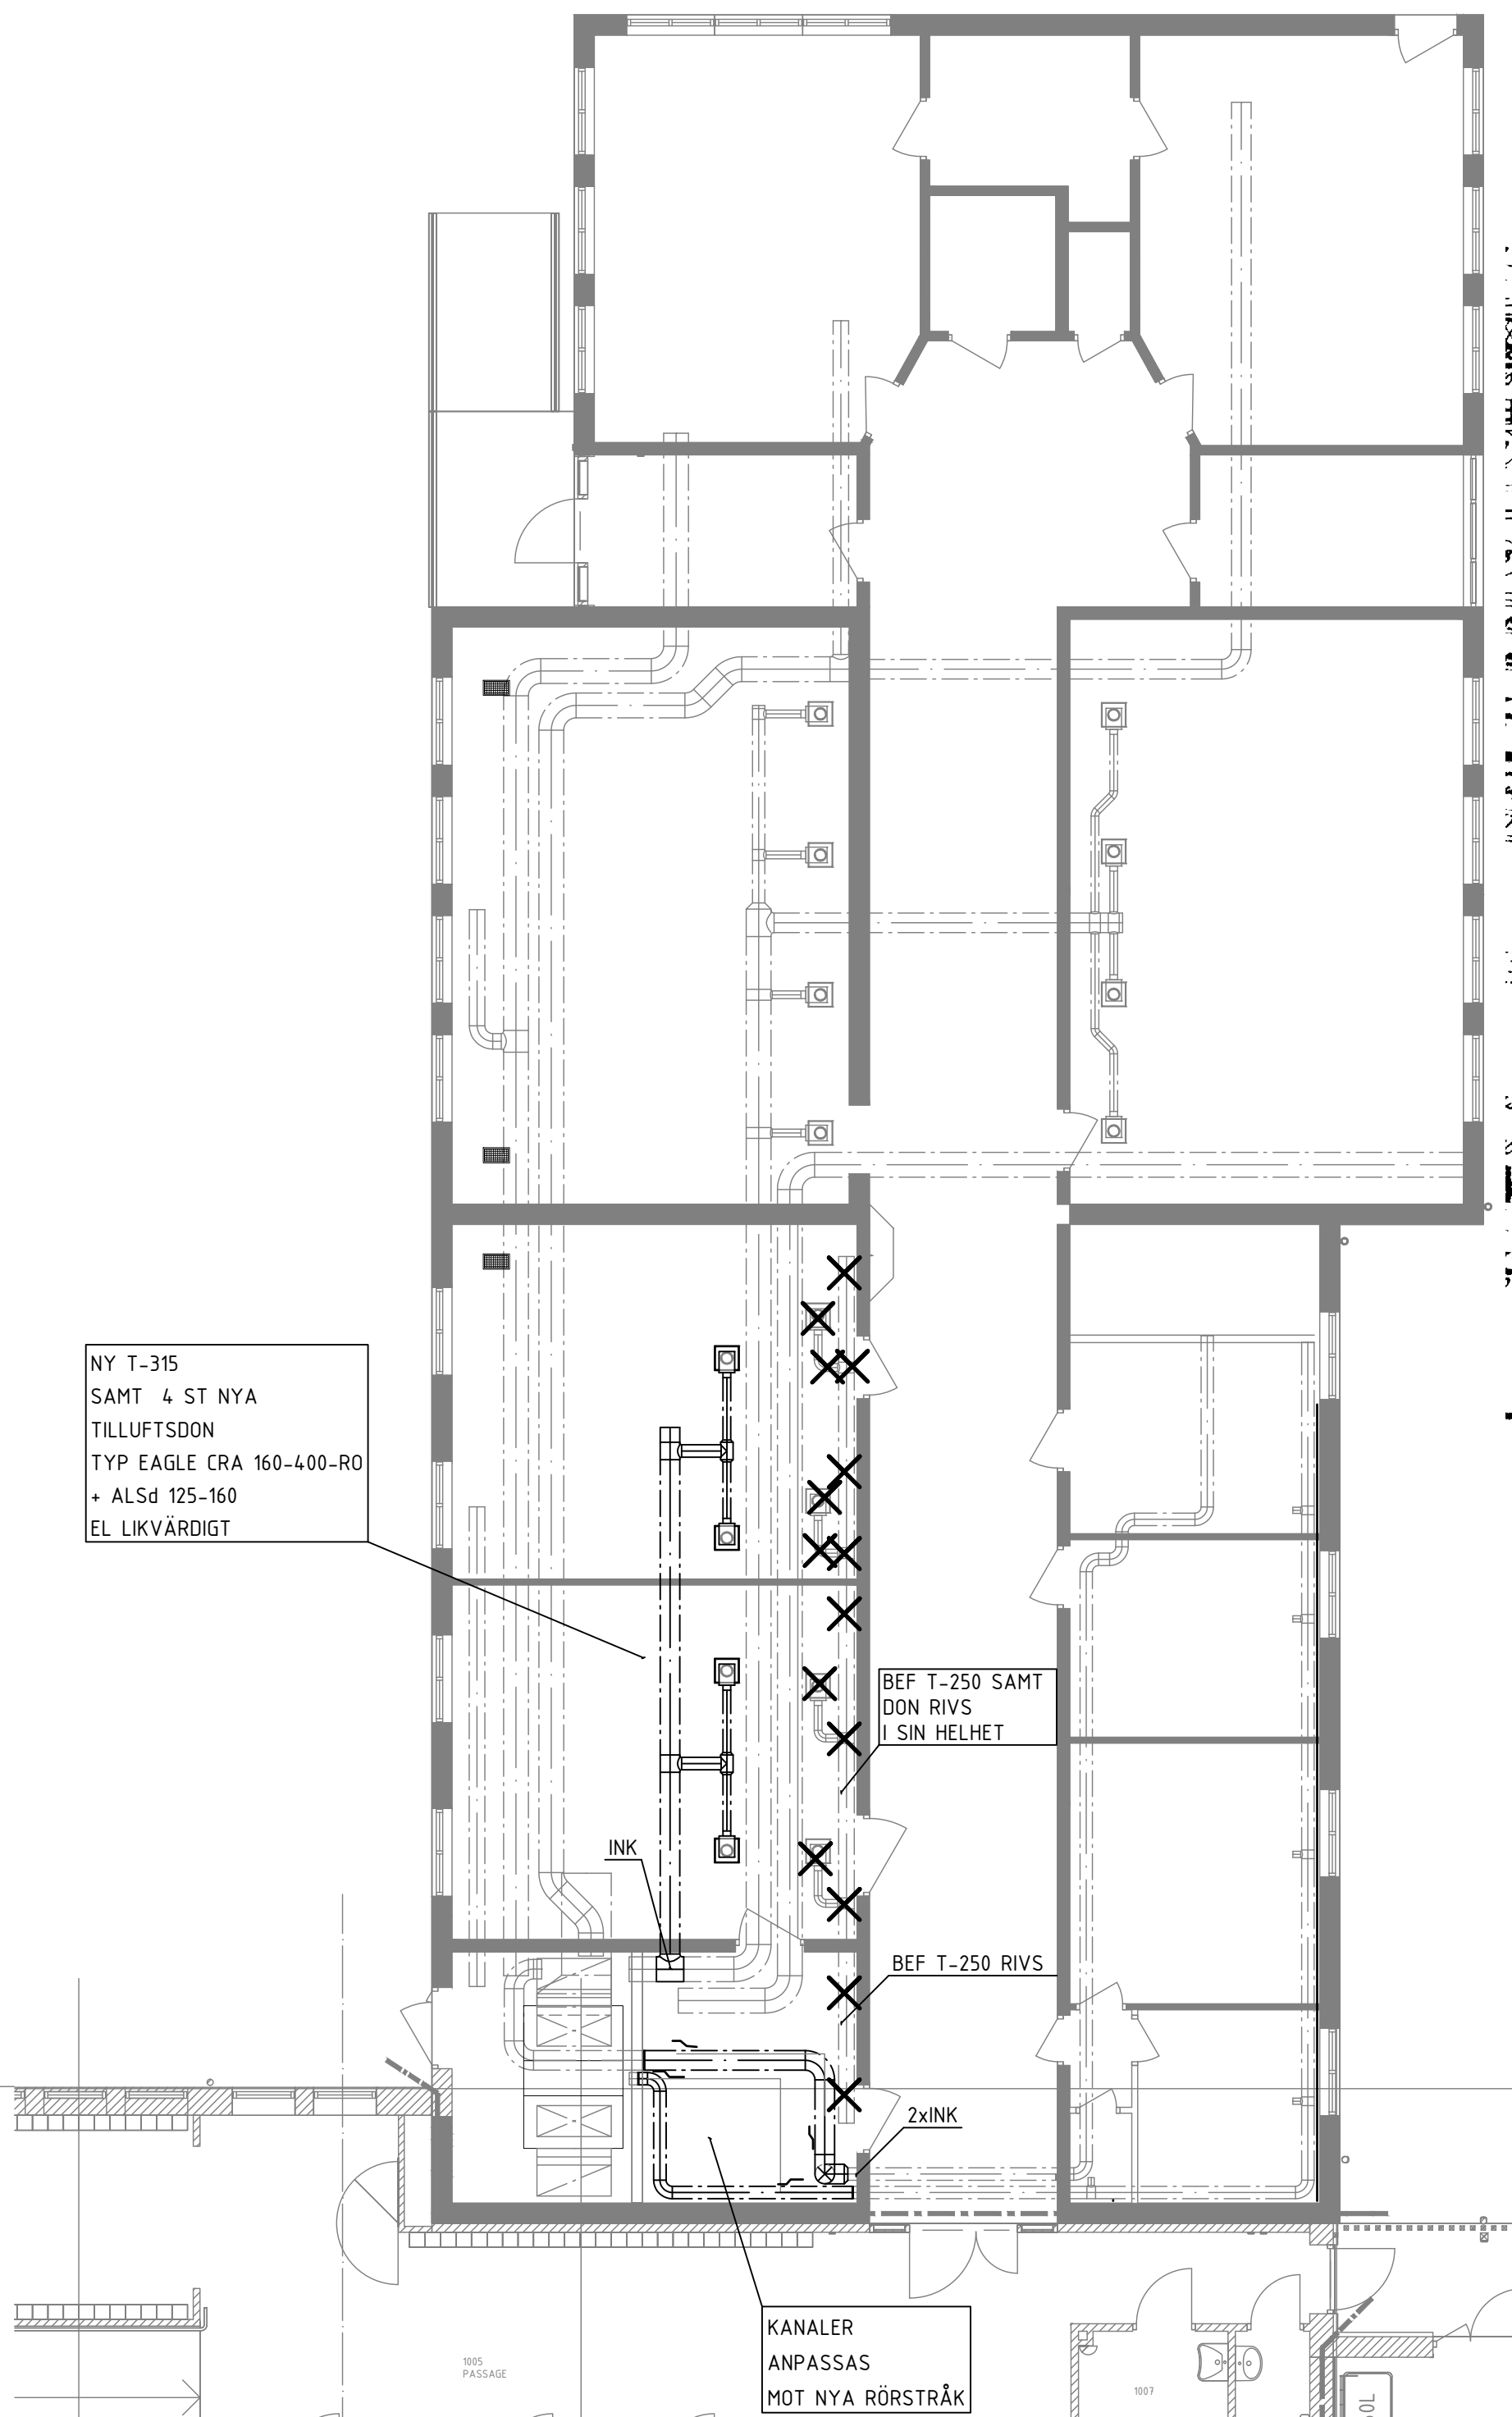

LUFTBEHANDLINGSINSTALLATIONER
SKALA 1:100

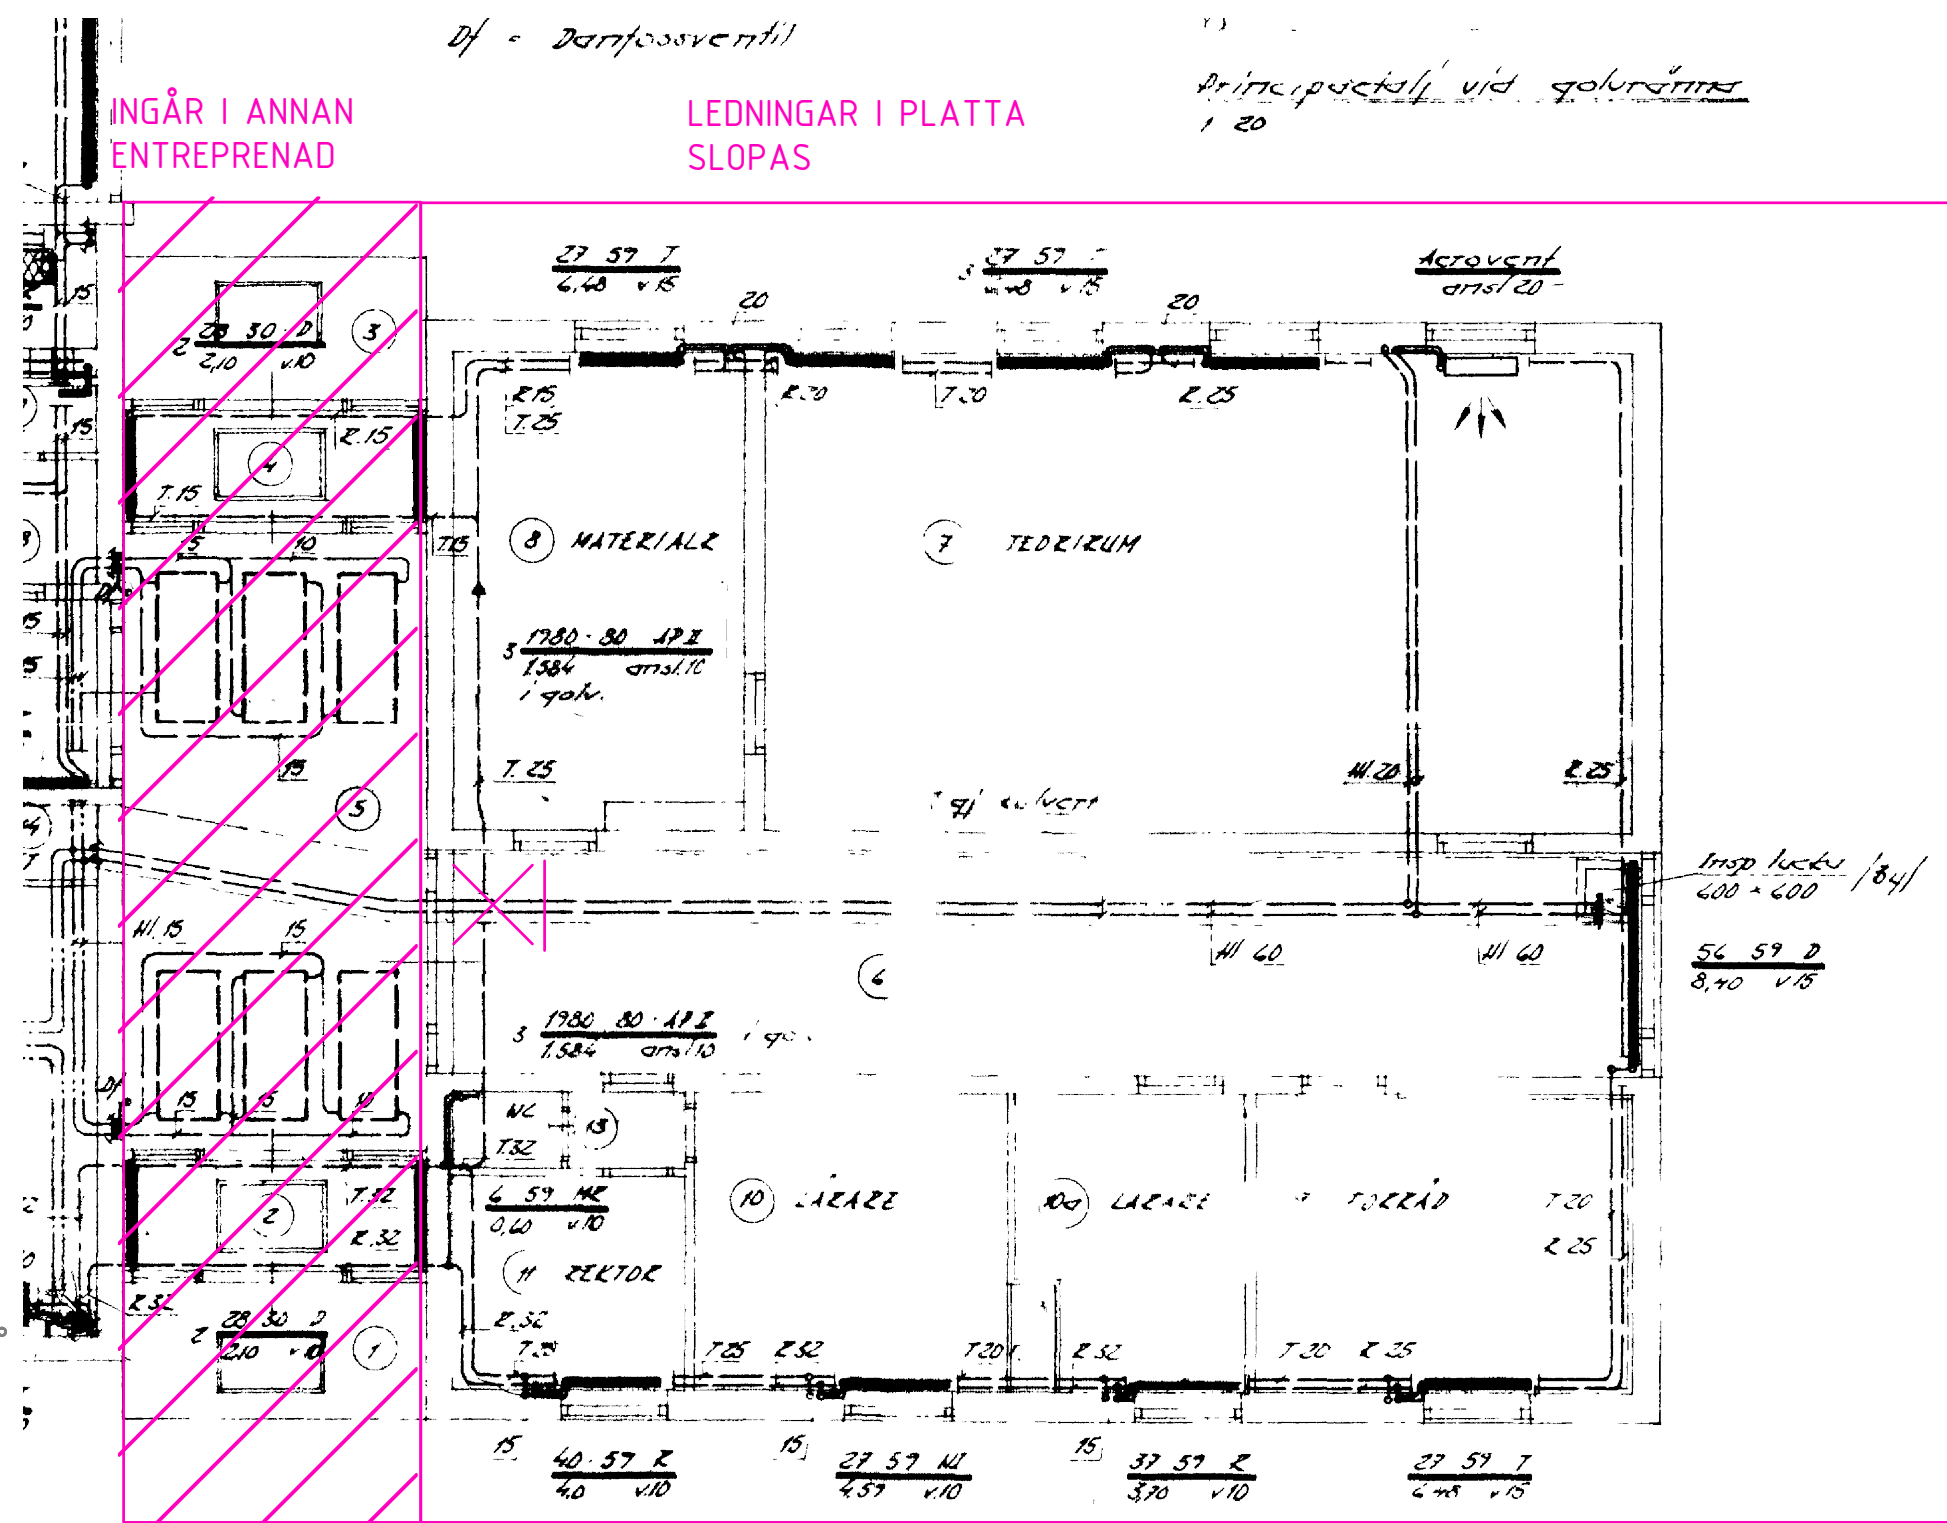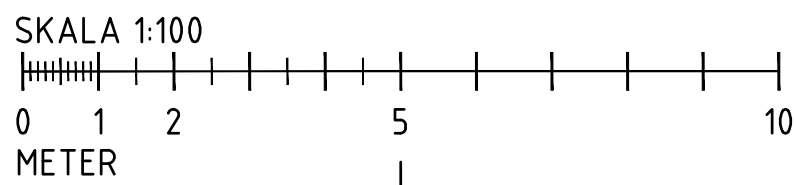

DEMONTERING
EJ I SKALA

SEKTION	
ORIENTERINGSPOL	
STATUS	
FÖRFRÅGNINGSUNDERLAG	
HANDLING	
BYGGHANDLING	
DATUM	2024-12-20
GODKÄND AV	T.BERGSTRÖM
ANDRINGS PM	
BESTÄLLARE	
ROBERTSFORS KOMMUN	
PROJEKTNAMN	
CENTRALEKÖK	
OMRADE	
ROBERTSFORS KOMMUN	
PROJEKTNUMMER	108 83 71
DARIENUMMER	108 83 71
DISCIPLIN	VE, VS
OPPTÄGNUMMER	MAN
TELEFON	010 141 80 00
BYGGNADSVÄRDE	+45,54 (FG)
VÄRNINGSPÅN	1
VÄRNINGSDI	DEL 5.4
SYSTEM	
50, 57 RÖR OCH LUFTBEHANDLING	
PLAN 1 - DEL 6	
SKALA	1:100
FORMAT	A1
DOKUMENTNUMMER	V-50-1-601