




FÖRKLARINGSTEXT
SE RITNING V-50-0-001

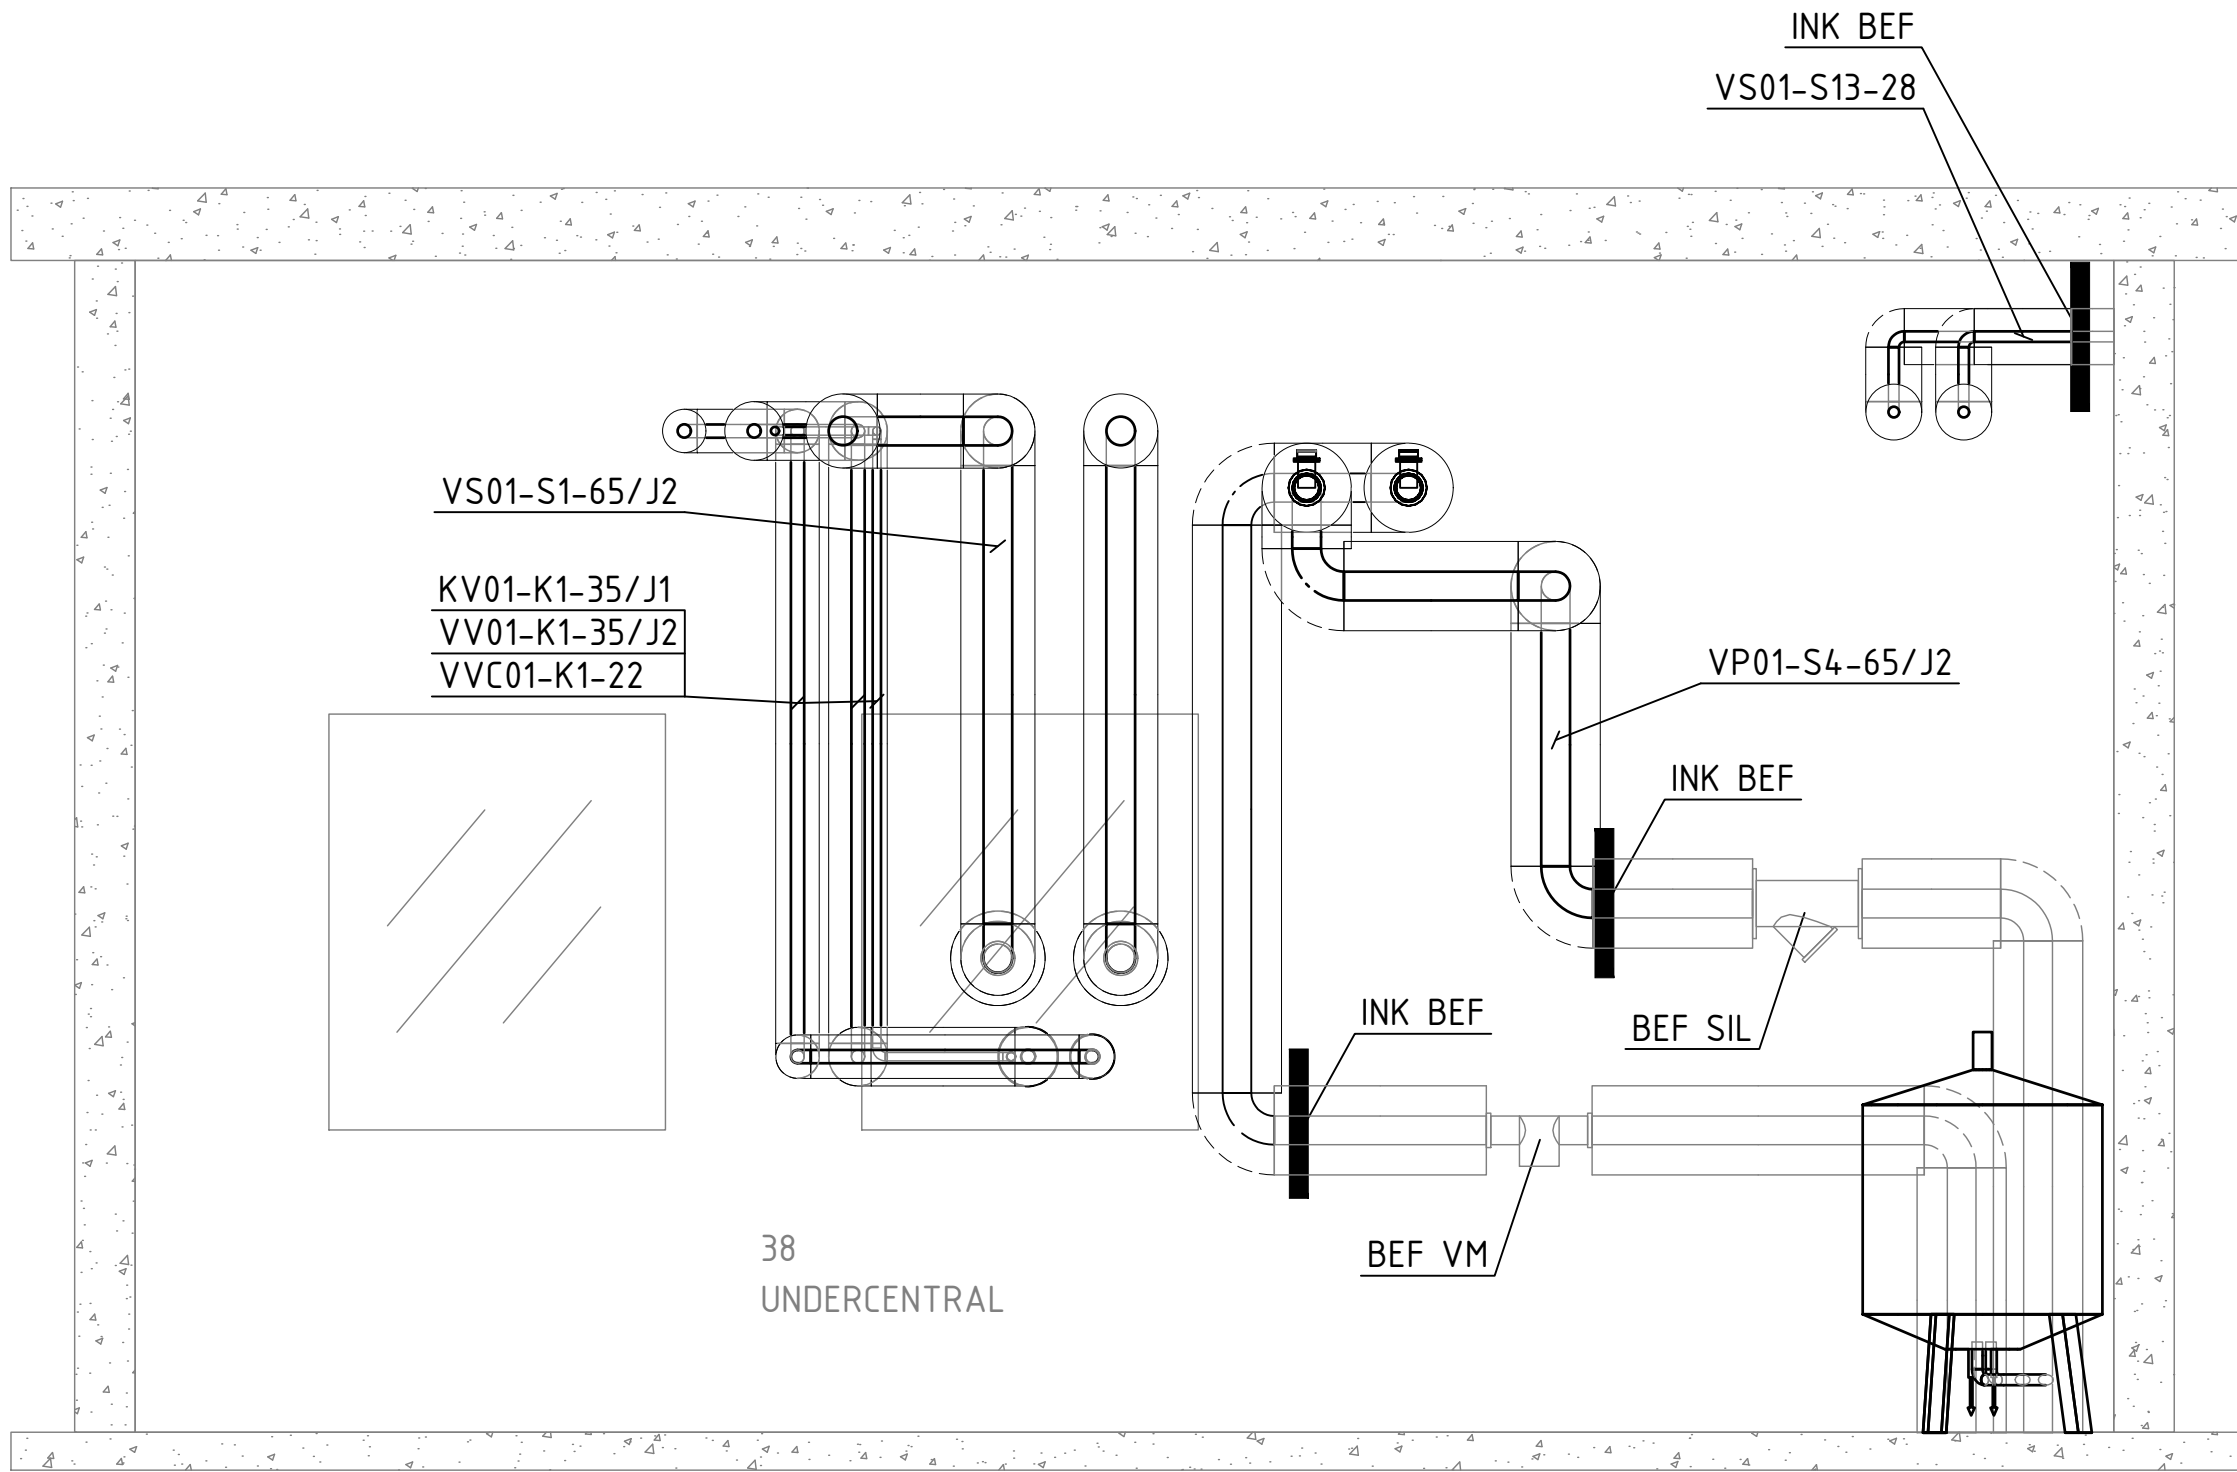


SEKTION 2
SKALA 1:20

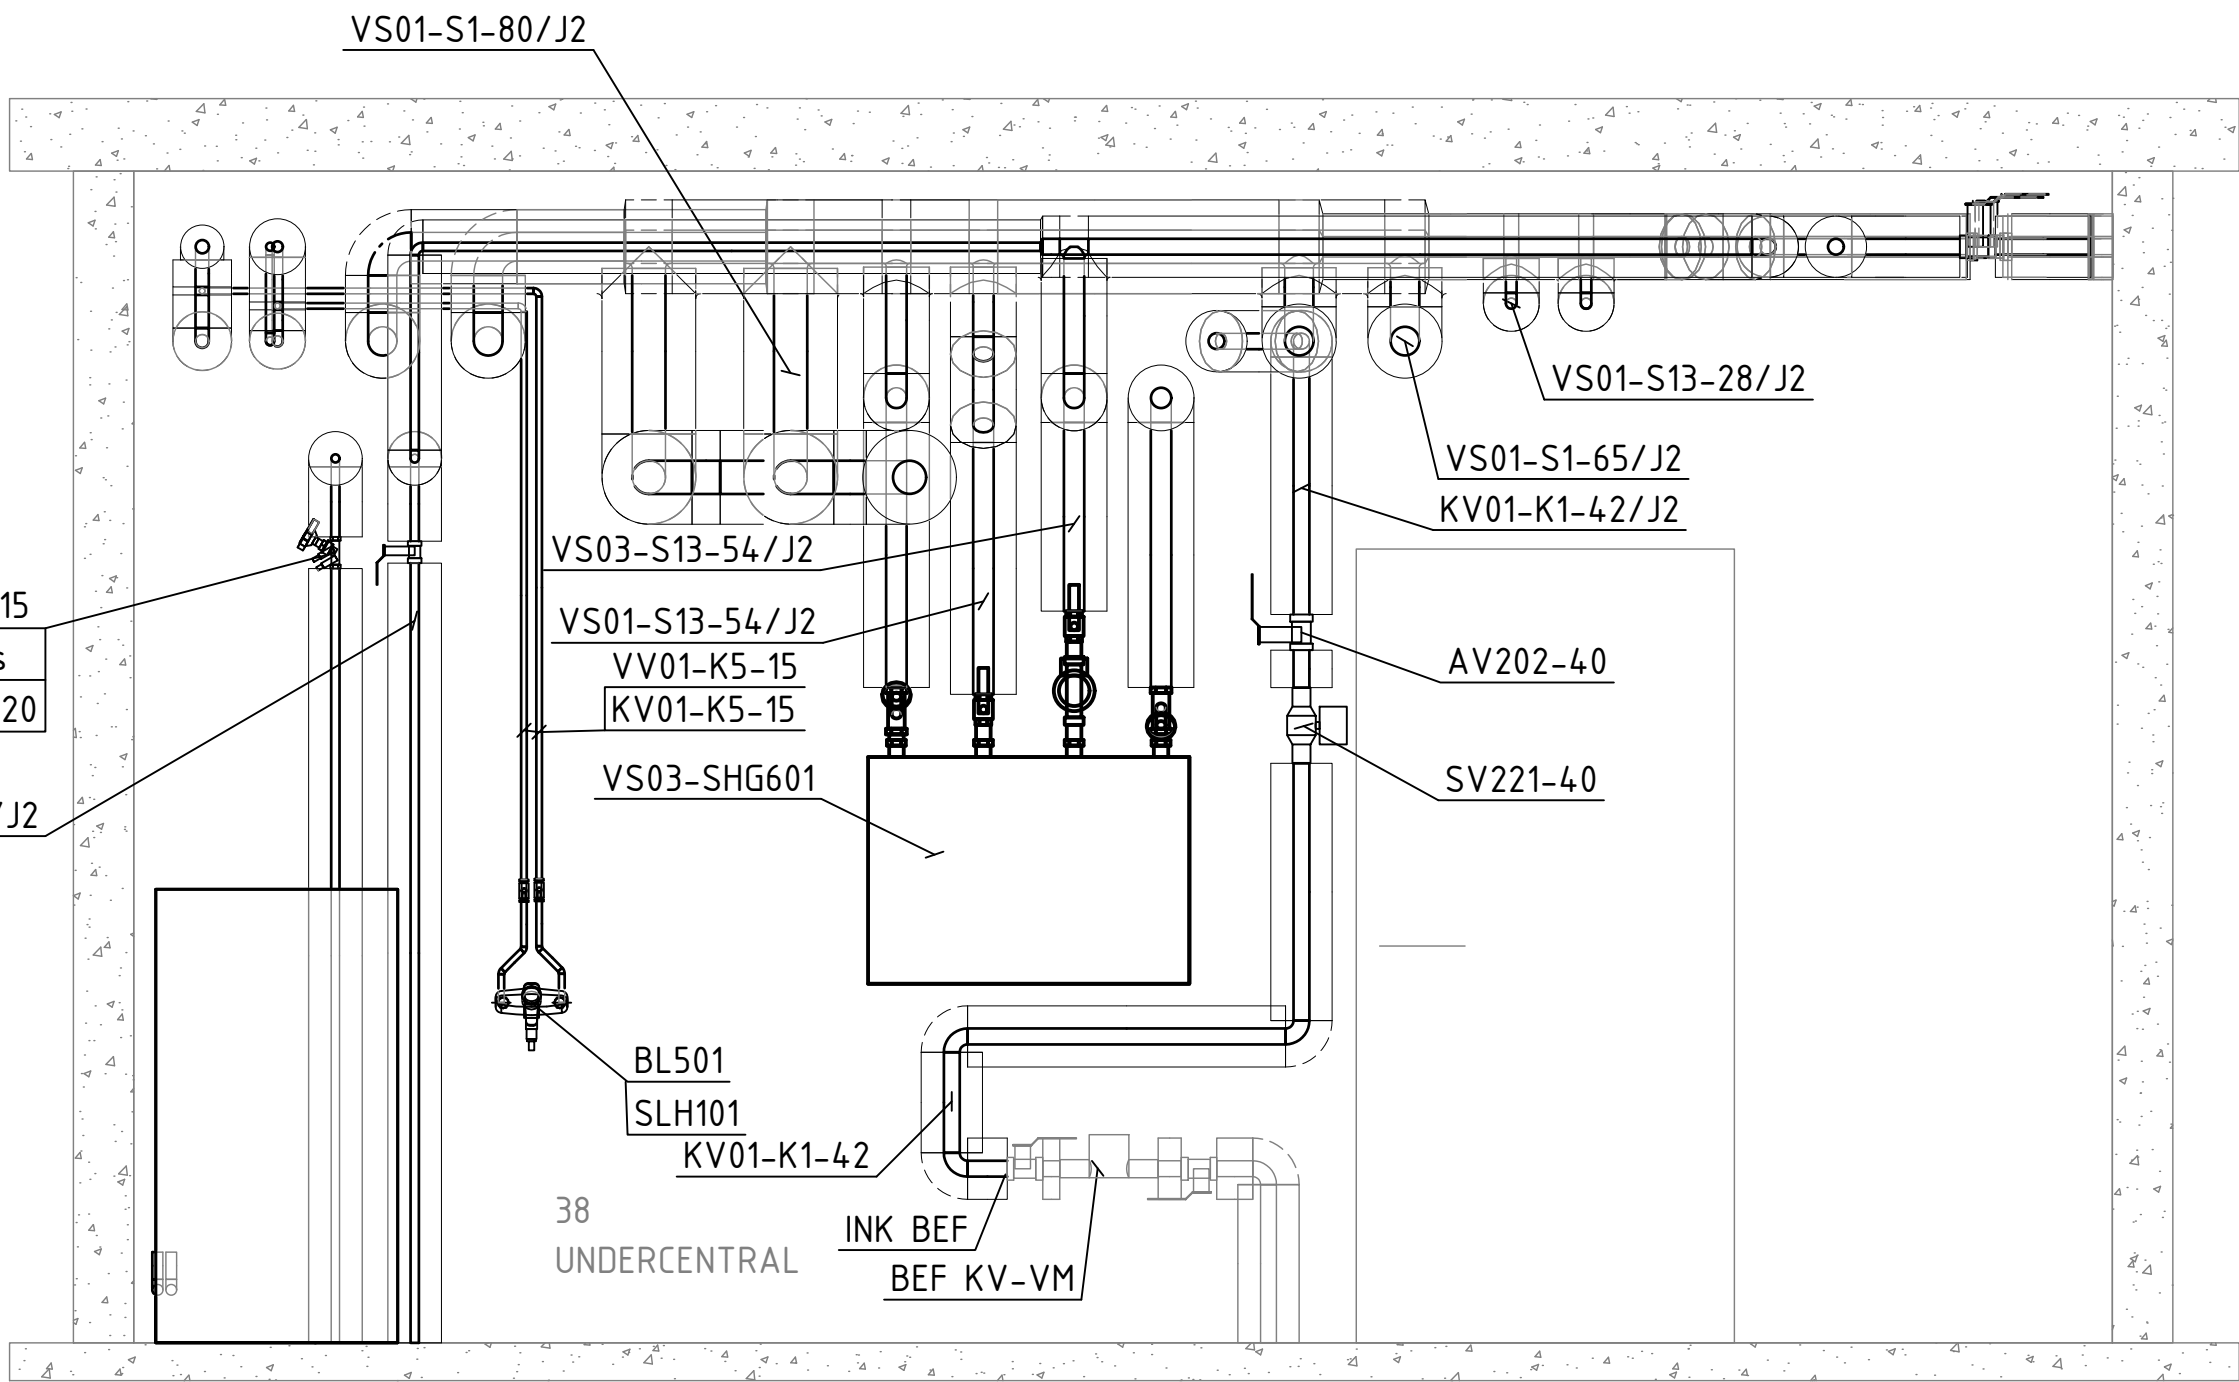



SEKTION 3
SKALA 1:20

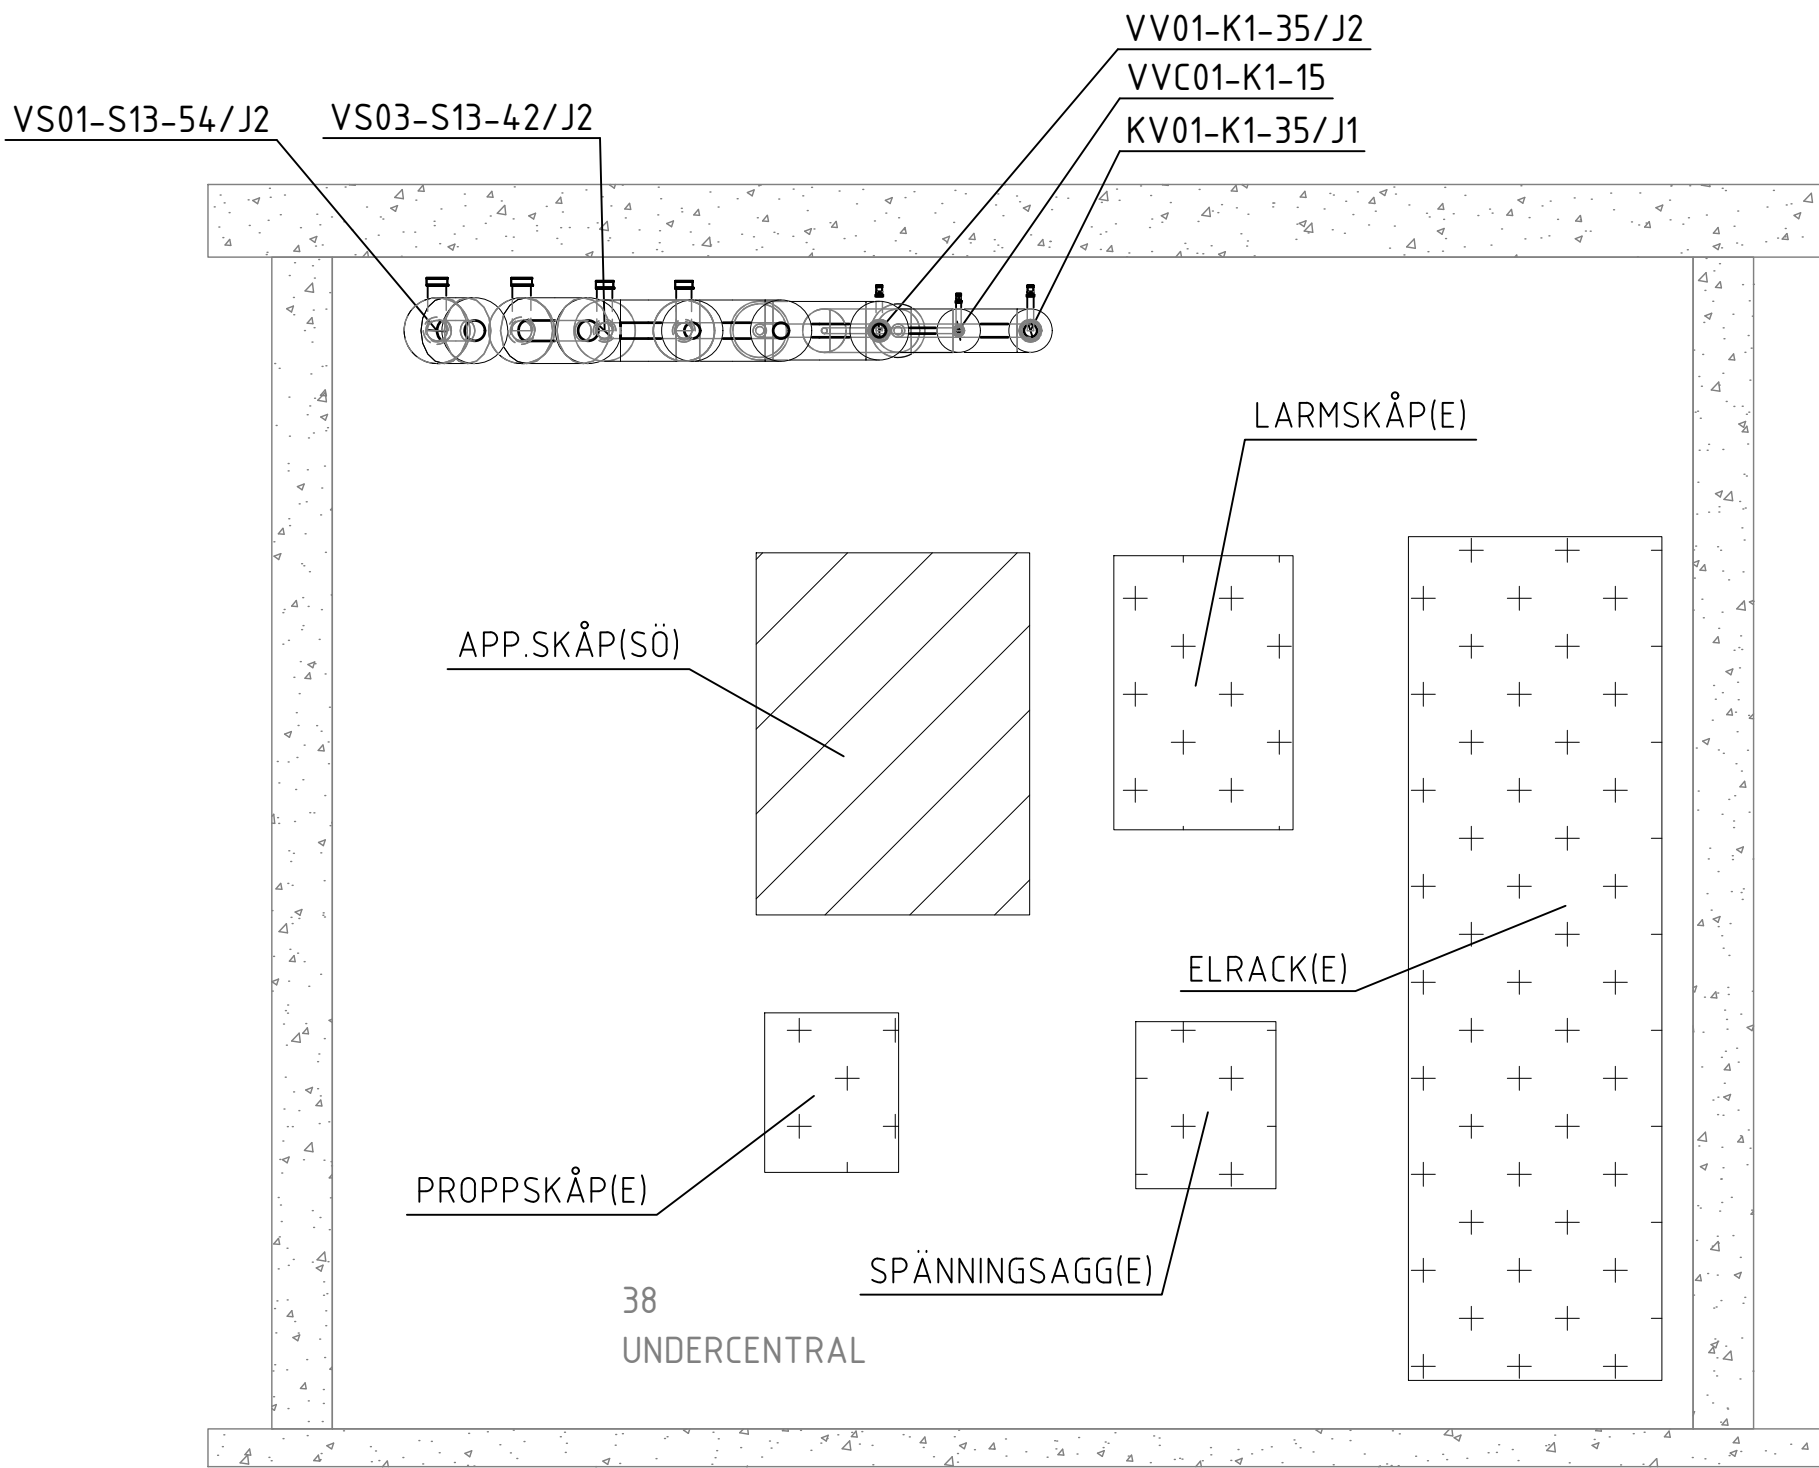

SEKTION 4
SKALA 1:20

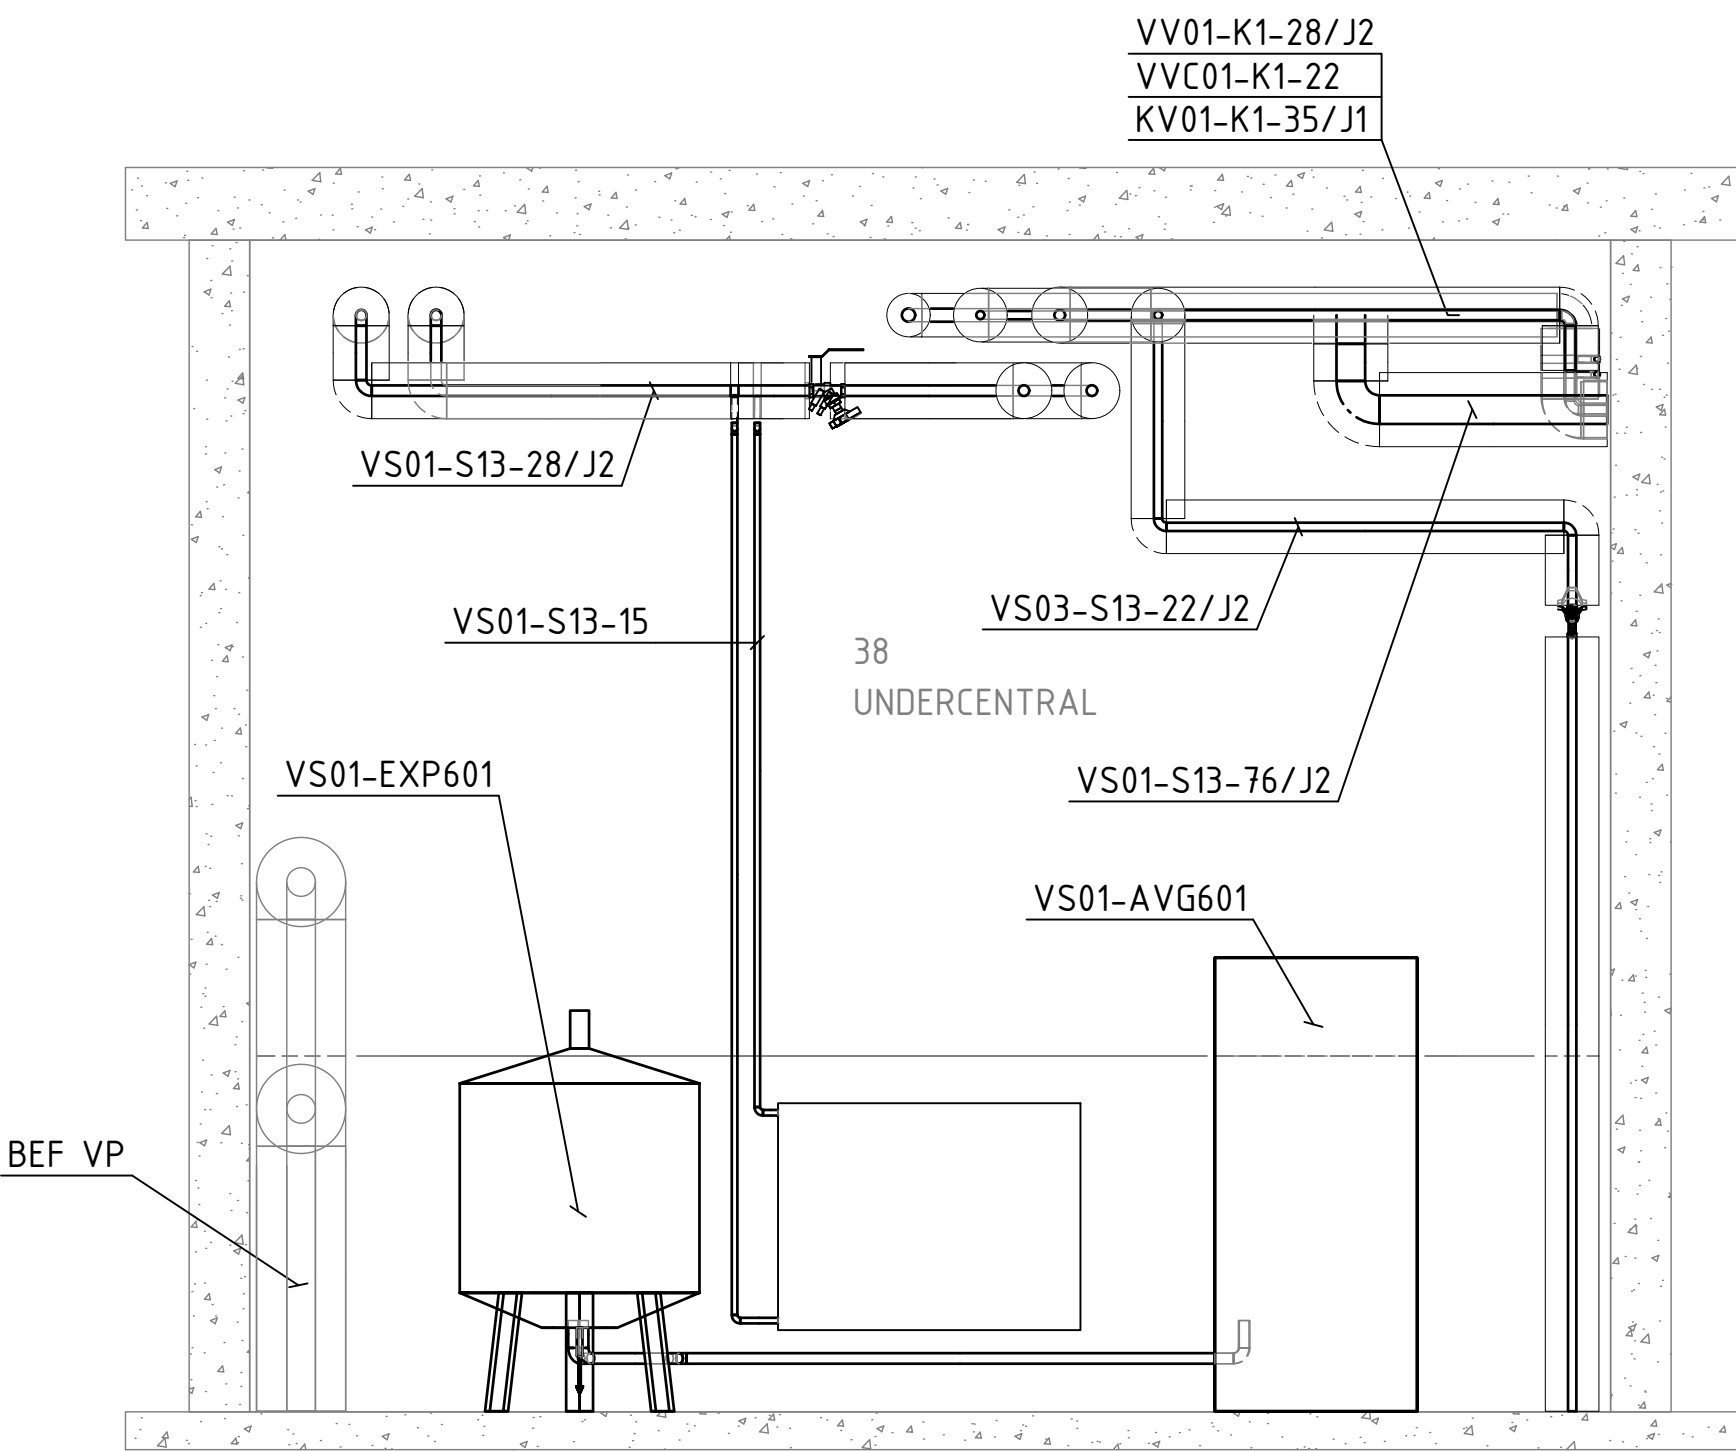

SEKTION 5
SKALA 1:20

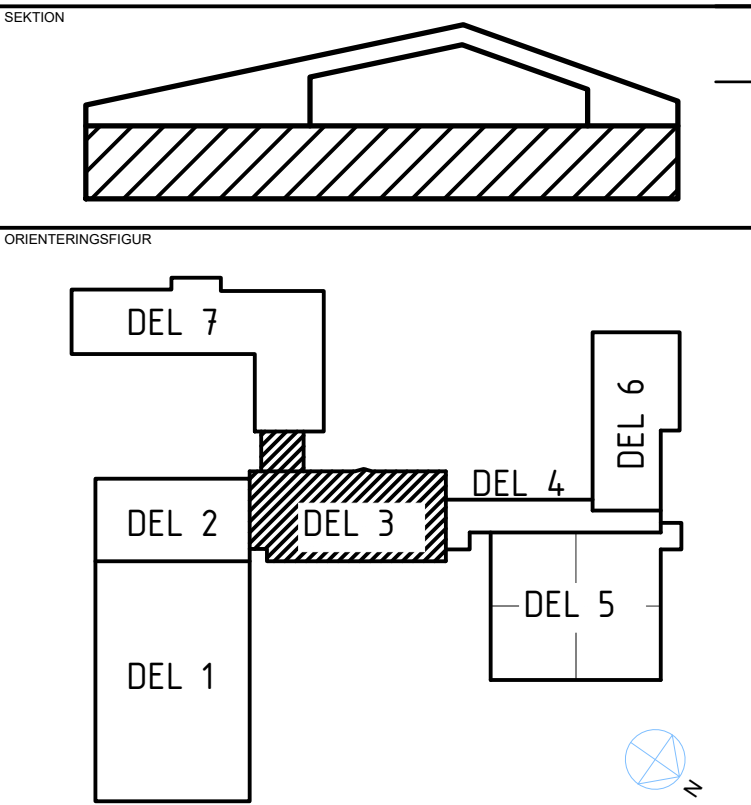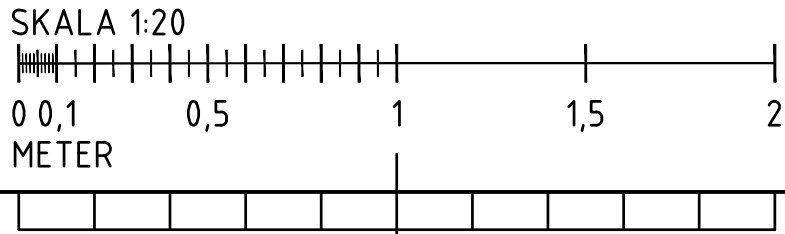

SEKTION		
ORIENTERINGSPÅR		
STATUS		
FÖRFRÅGNINGSUNDERLAG		
HANDLING		
BYGGHANDLING		
DATUM	GODKÄND AV	ÄNDRINGS PM
2024-12-20	T.BERGSTRÖM	
BESTÄLLARE		
ROBERTSFORS KOMMUN		
PROJEKTNAMN		
CENTRALKÖK		
OMRADE		
ROBERTSFORS KOMMUN		
PROJEKTNUMMER	ADRESS	
	YTTRE RINGVÄGEN 4	
DARIENUMMER	FASTIGHET	
	FÖRDONET 1	
DISCIPLIN	FÖRETAG	
VS	NORCONSULT SVERIGE AB	
OPPRAGSNUMMER	SKAPAD AV	
108 83 71	MAN	
TELEFON	KONTAKTPERSON	
010 141 80 00	JONAS JOHANSSON	
BYGGNADSVÄRDE	(KLIMATKORRIGERAT)	
	+44,60 (FG)	
VÄNINGSPLAN	VÄNINGSDEL	DELOMRÅDE
1		DEL 3
SYSTEM		
50 RÖRINSTALLATIONER, UC		
RESERVATION		
PLAN 1		
RITNINGSKATEGORI	SKALA	FORMAT
SEKTION	1:20	A1
DOKUMENTNUMMER	ÄNDRING	
V-50-2-001		