



FÖRKLARINGSTEXT
SE RITNING V-50-0-001

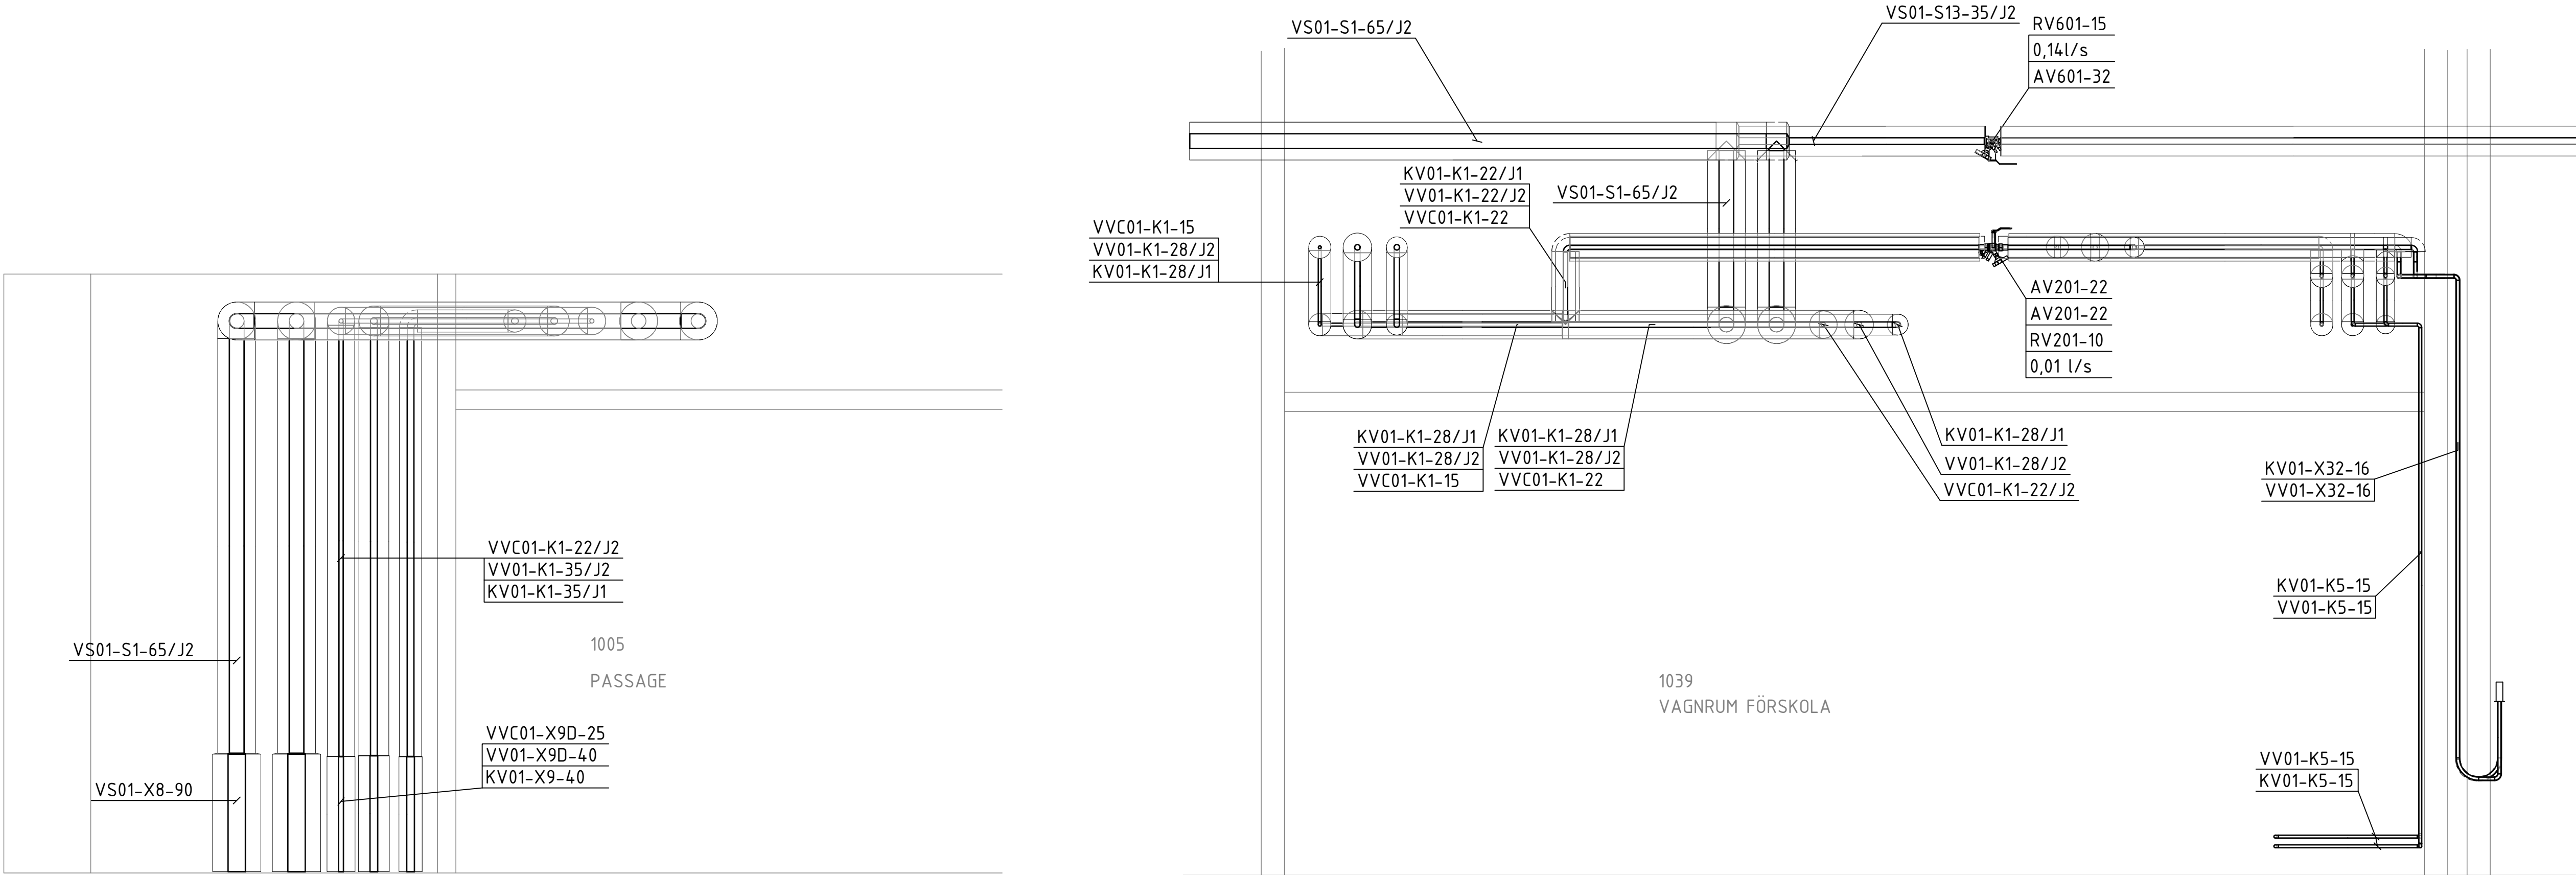


SEKTION 6
SKALA 1:20



SEKTION 7
SKALA 1:20

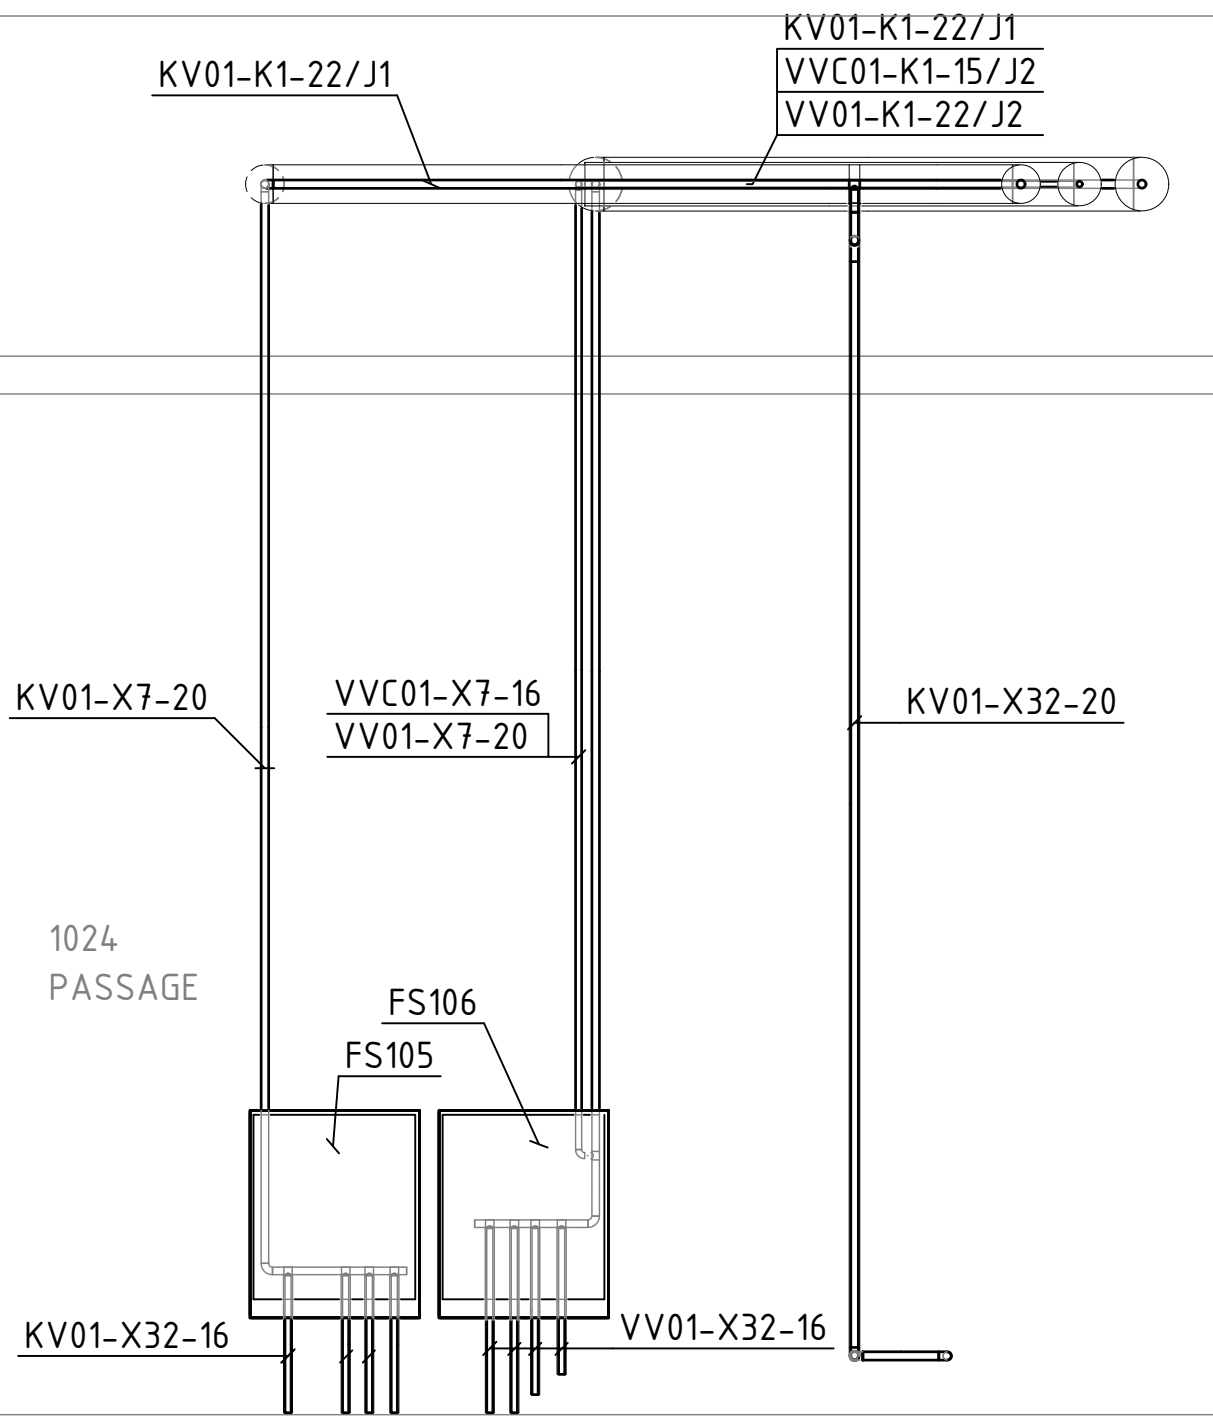

SEKTION 8
SKALA 1:20

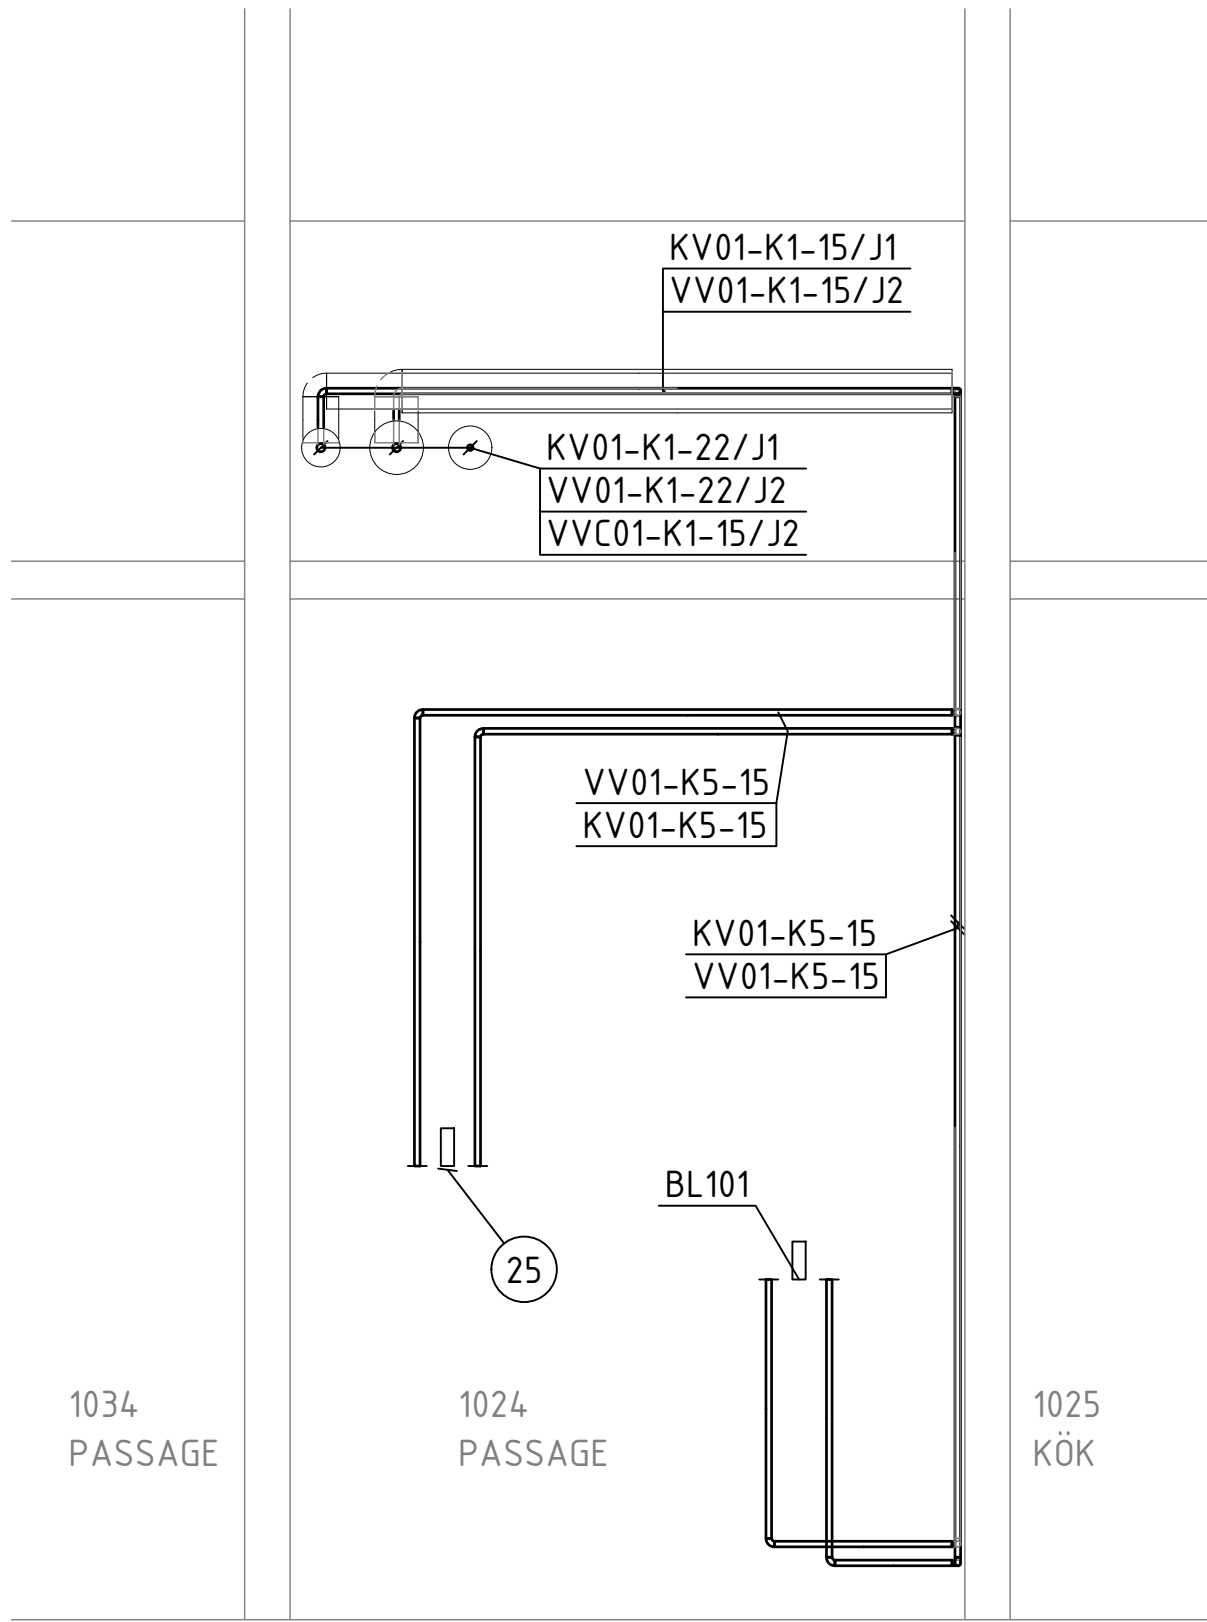

SEKTION 9
SKALA 1:20

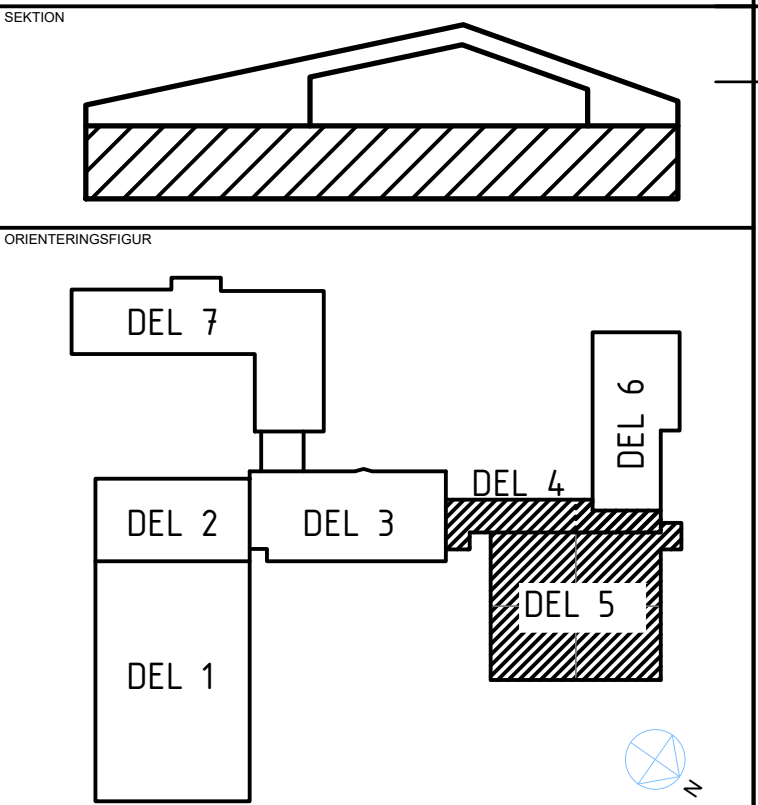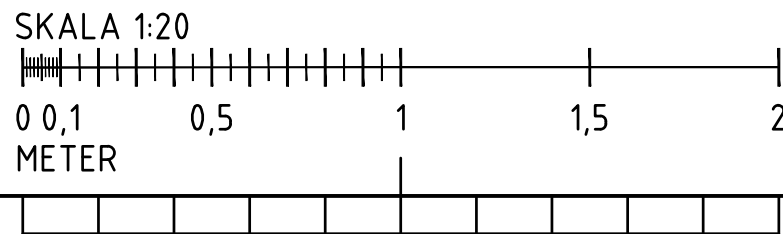

SEKTION		
ORIENTERINGSPÅR		
STATUS		
HANDLING		
DATUM		
BESTÄLLARE		
PROJEKTNAMN		
OMRÅDE		
PROJEKTNUMMER		
DISCIPLIN		
BYGGNADSVÄRK		
VÄNINGSPLAN		
SYSTEM		
RITNINGSKATEGORI		
DOKUMENTNUMMER		