




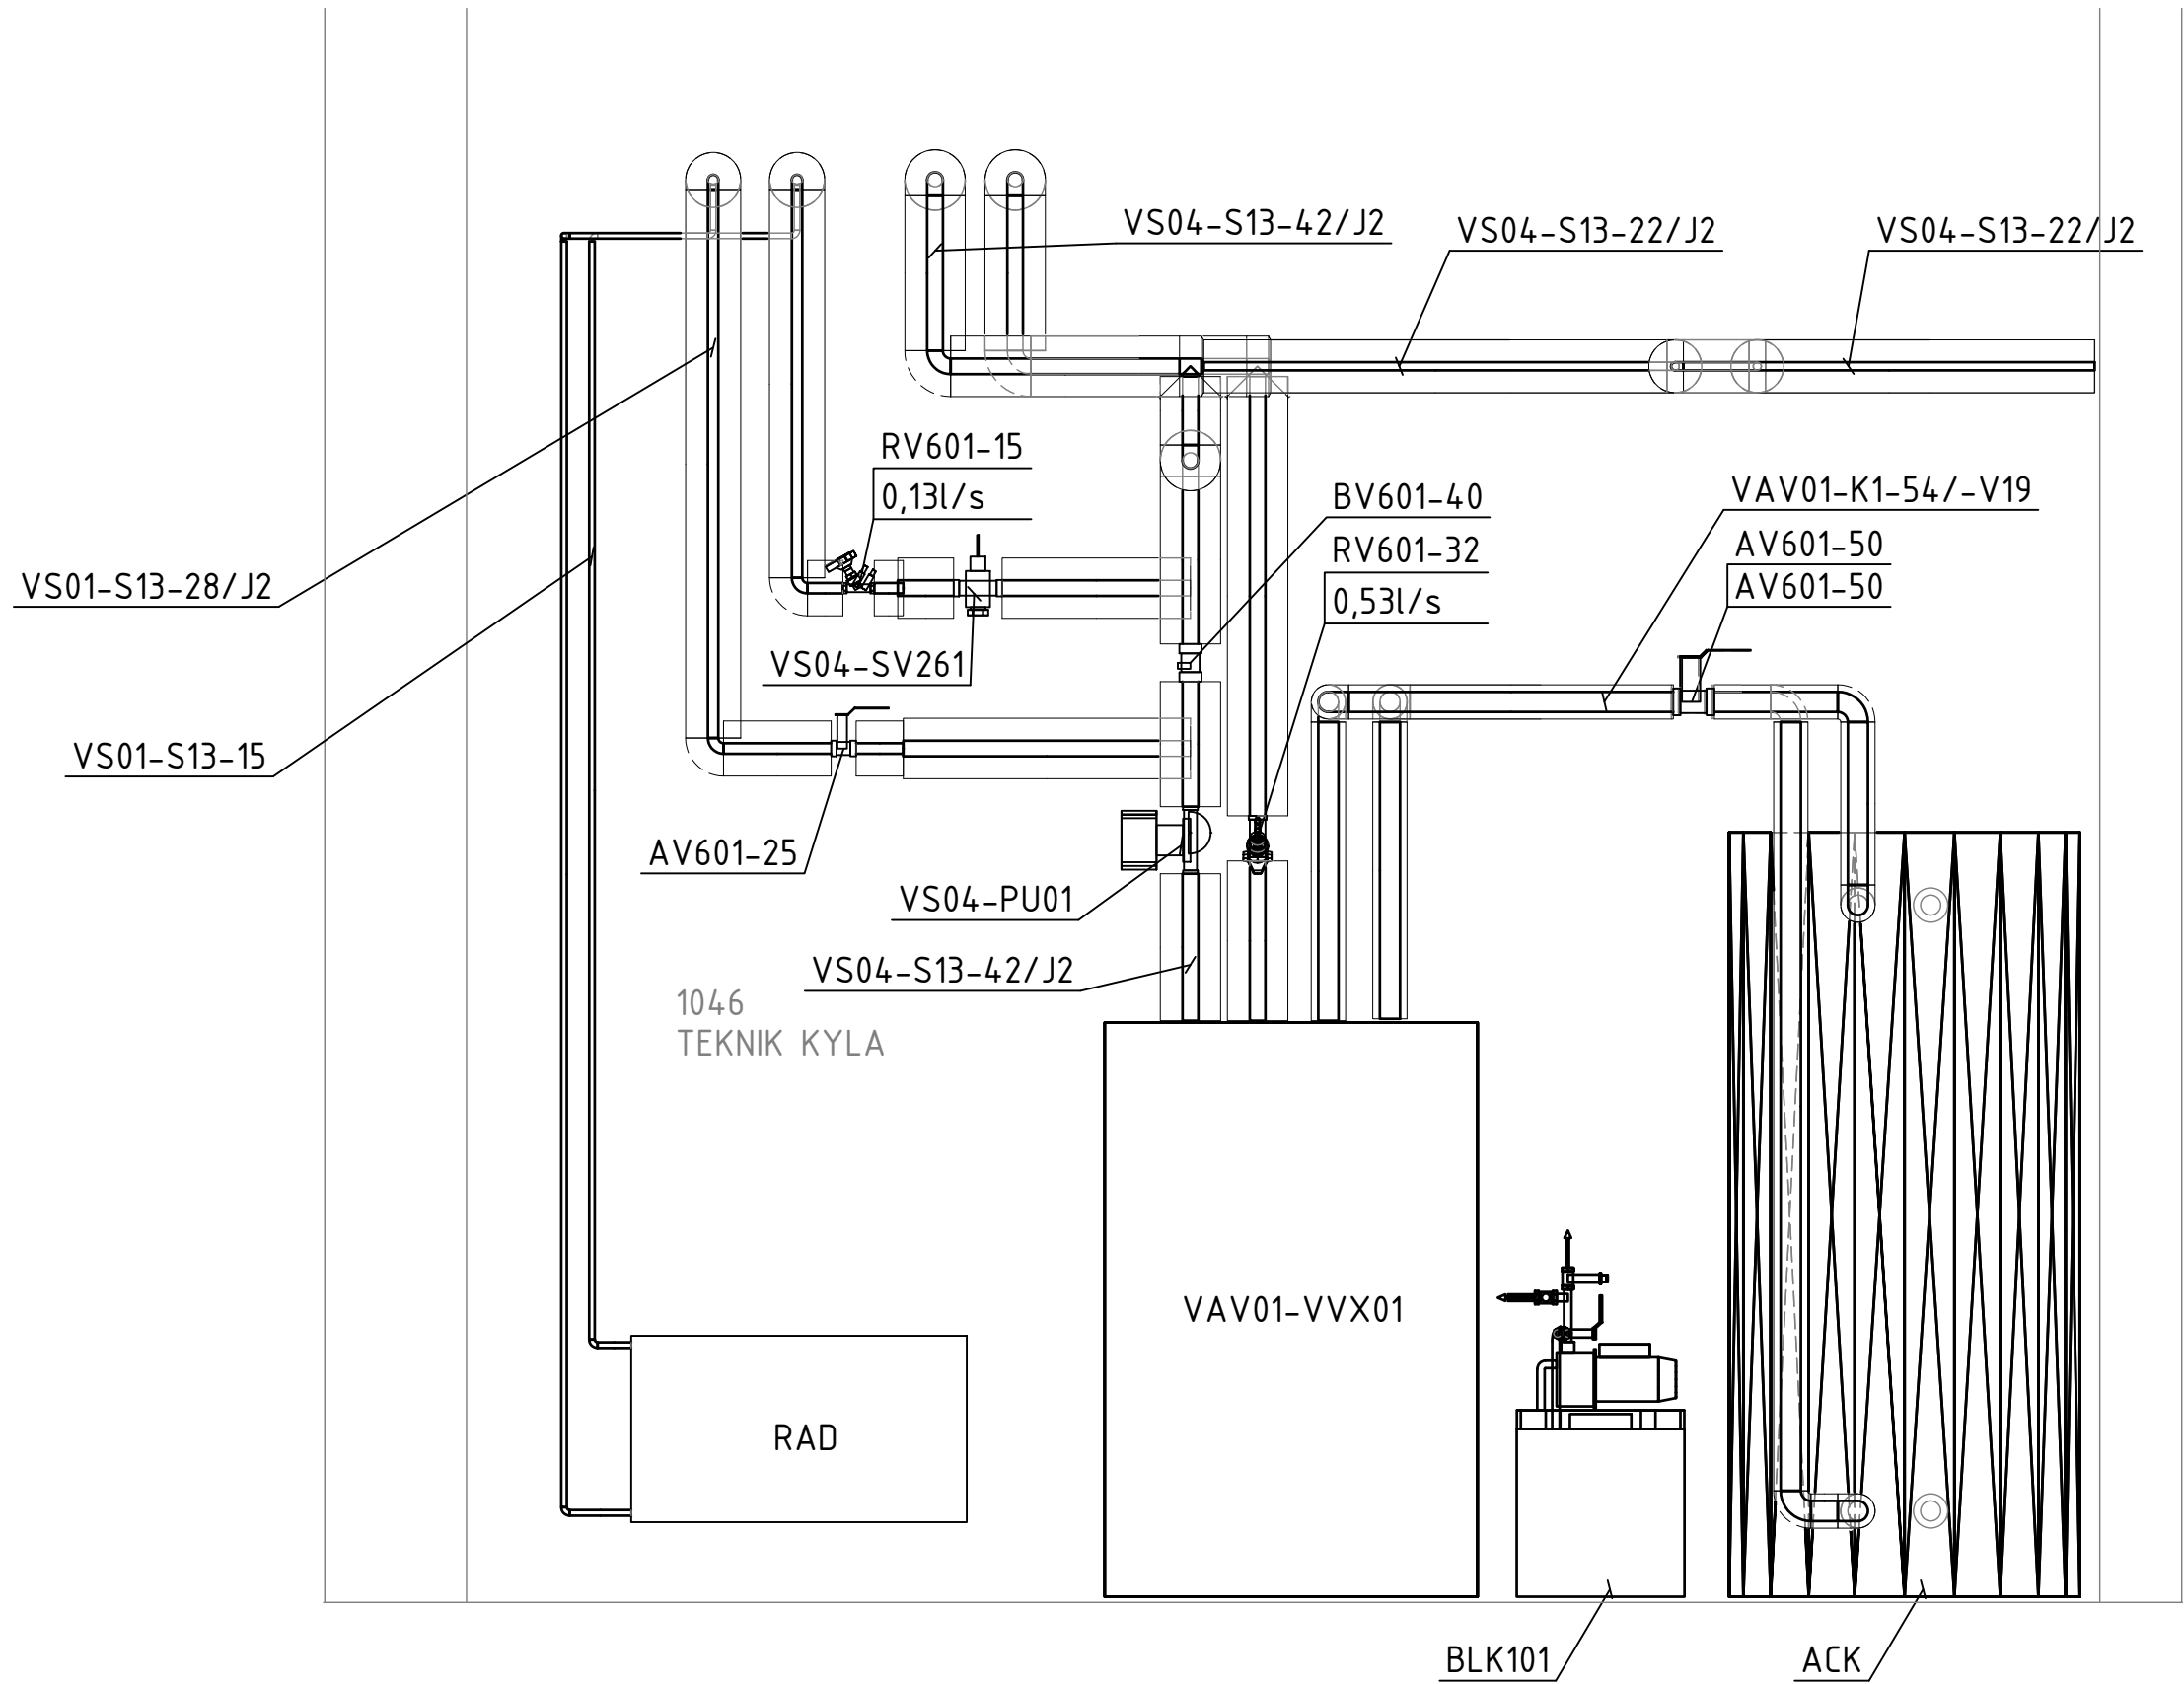

SEKTION 10 KYLCENTRAL
SKALA 1:20

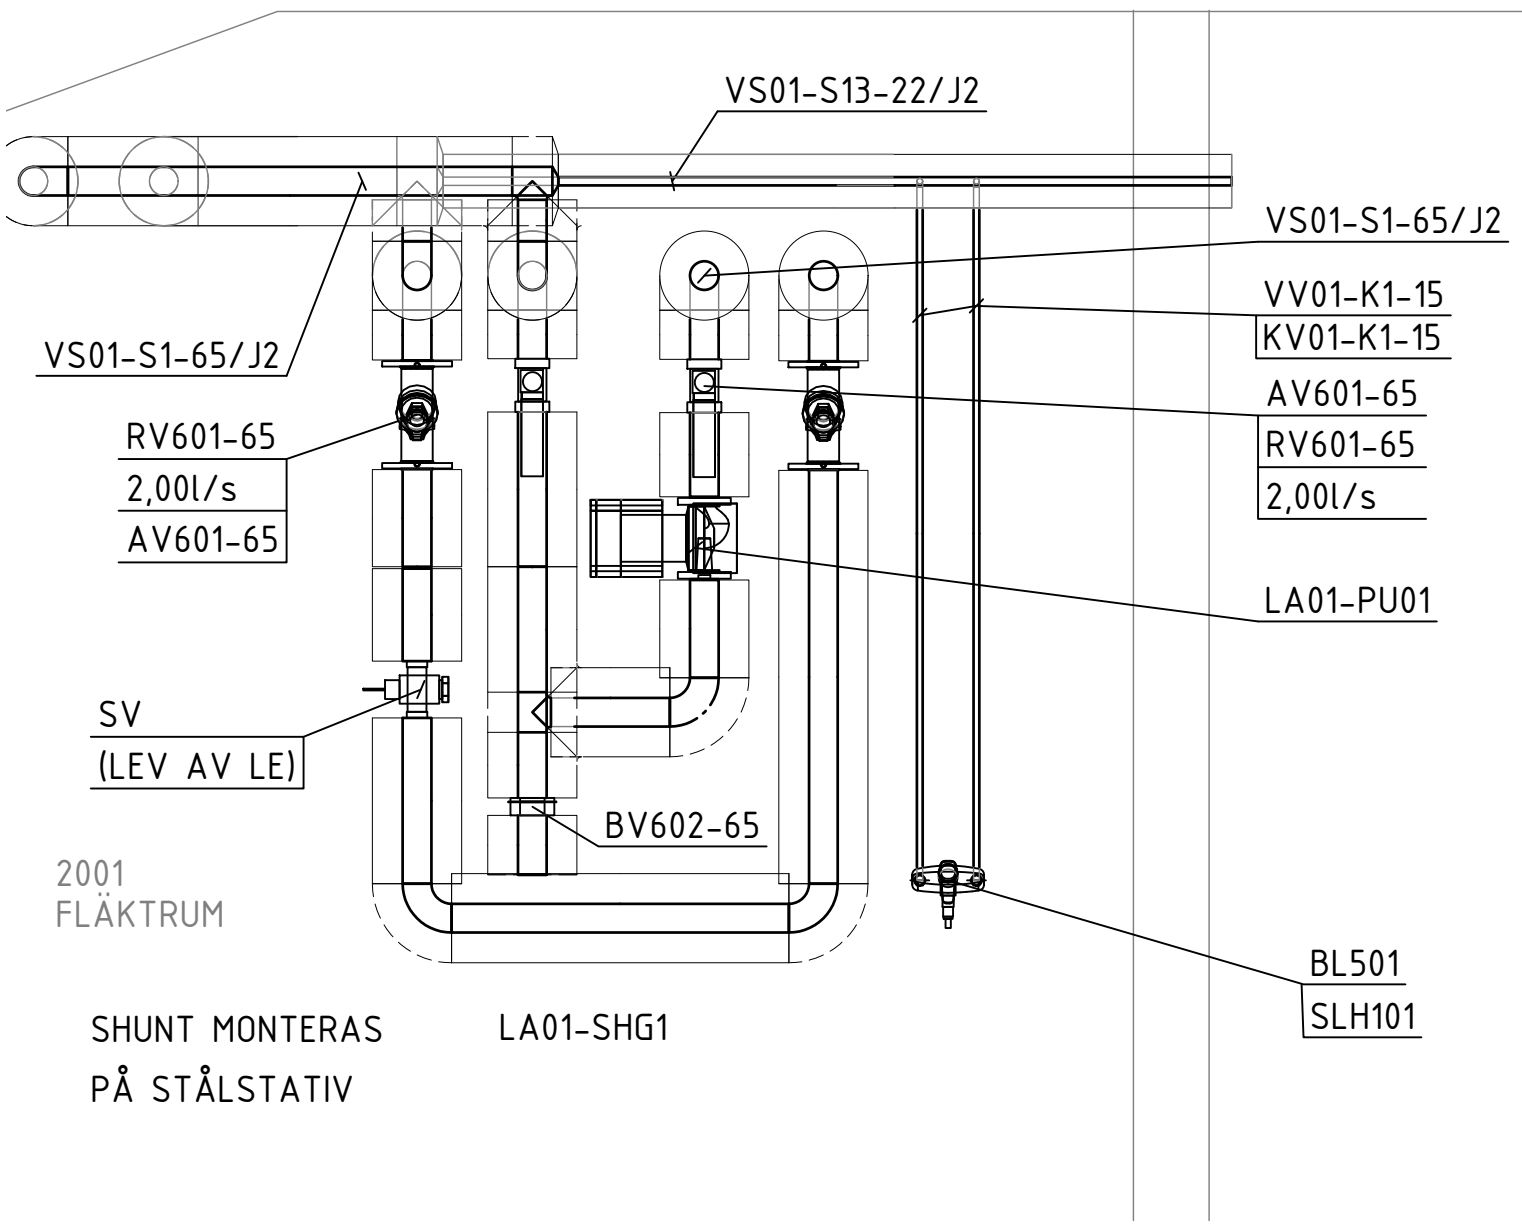

SEKTION 11 SHG
SKALA 1:20

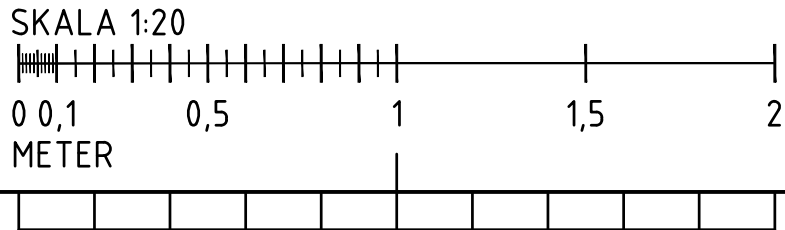

SEKTION

ORIENTERINGSPOLAR

STATUS

FÖRFRÅGNINGSUNDERLAG

HANDLING

BYGGHANDLING

DATUM

2024-12-20

ODOKAND AV

T.BERGSTRÖM

ANDRINGS PM

BESTÄLLARE

 **ROBERTSFORS**
KOMMUN

PROJEKTNAMN

CENTRALKÖK

OMRADE

ROBERTSFORS KOMMUN

PROJEKTNUMMER

ADRESS

YTIRE RINGVÄGEN 4

DARIENUMMER

FASTIGHET

FORDONET 1

DISCIPLIN

VS

FORETAG

NORCONSULT SVERIGE AB

OPPFÖRINGSNUMMER

108 83 71

SKAPAD AV

MAN

TELEFON

010 141 80 00

KONTAKTPERSON

JONAS JOHANSSON

BYGGNADSVÄRDE

(KLIMATKORRIGERT)

+45,54 +49,54 (FG)

VÄNINGSPLAN

1, 2

VÄNINGSDEL

DELOMRÅDE

DEL 5

SYSTEM

50 RÖRINSTALLATIONER

REPRESENTATION

PLAN 1, 2

RITNINGSKATEGORI

SEKTION

SKALA

1:20

FORMAT

A1

DOKUMENTNUMMER

V-50-2-003

ANDRING