





FÖRKLARINGSTEXT
SE RITNING V-50-0-001

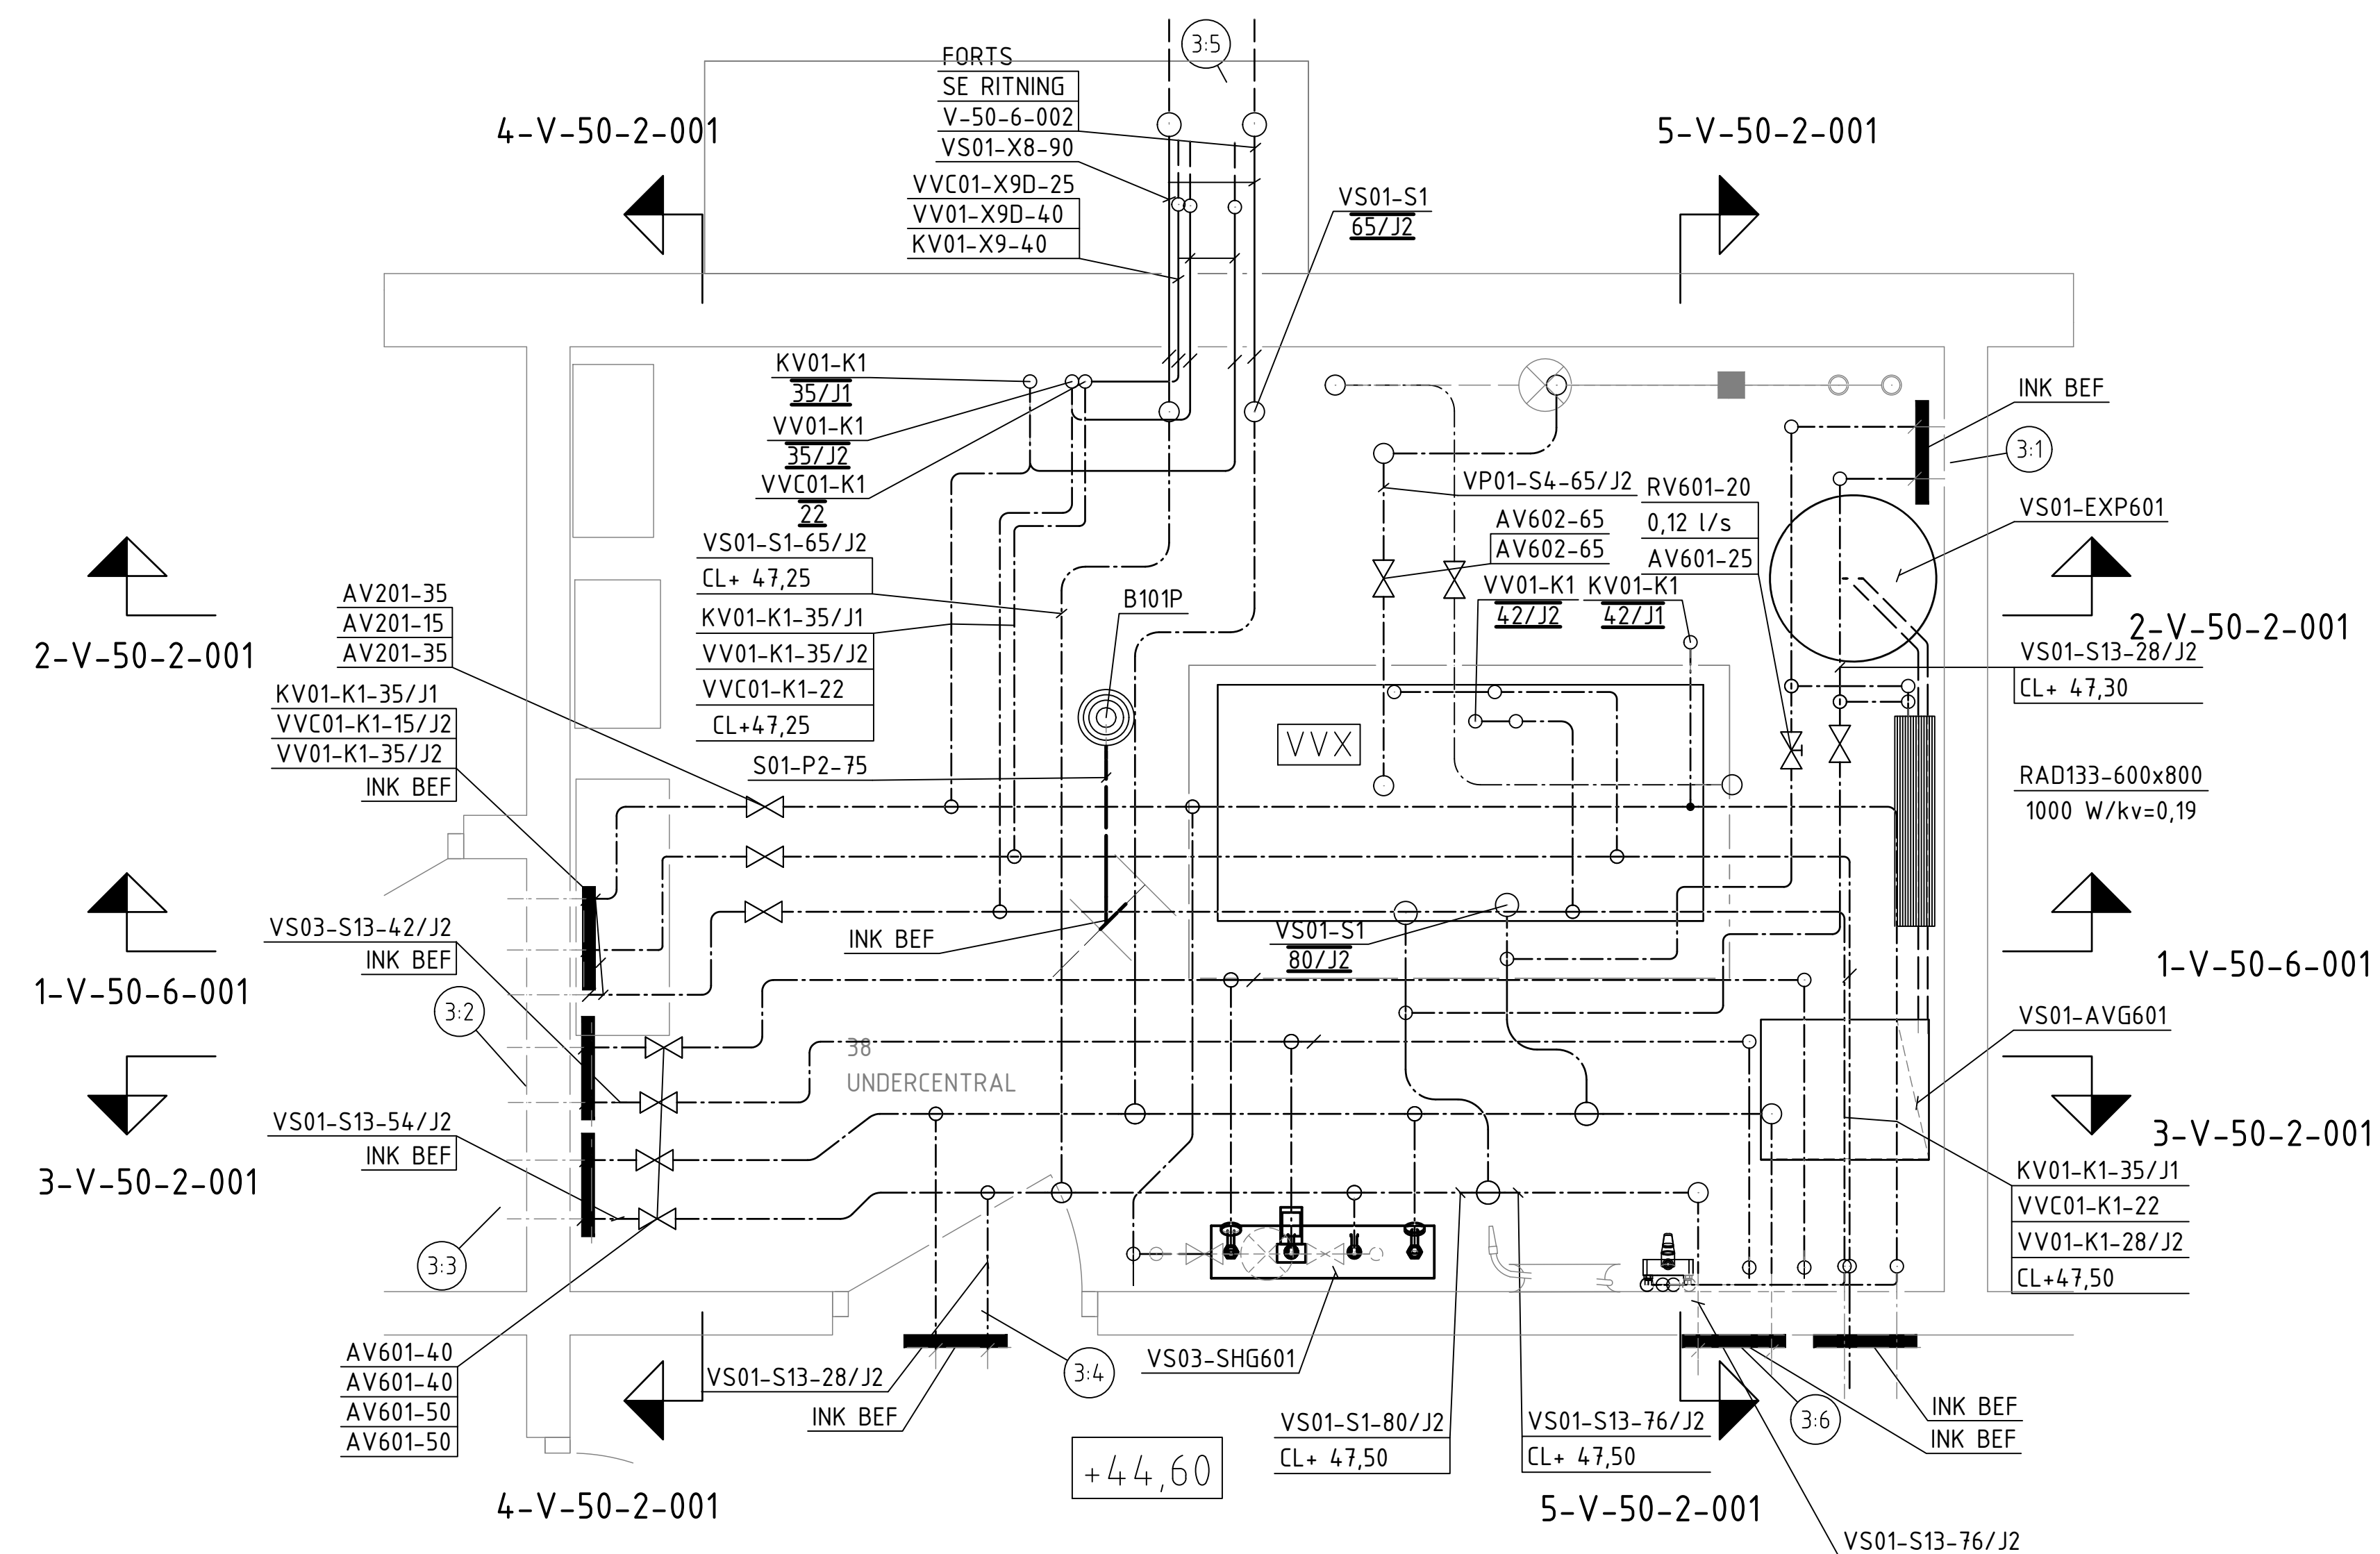

DELPLAN UNDERCENTRAL
SKALA 1:20

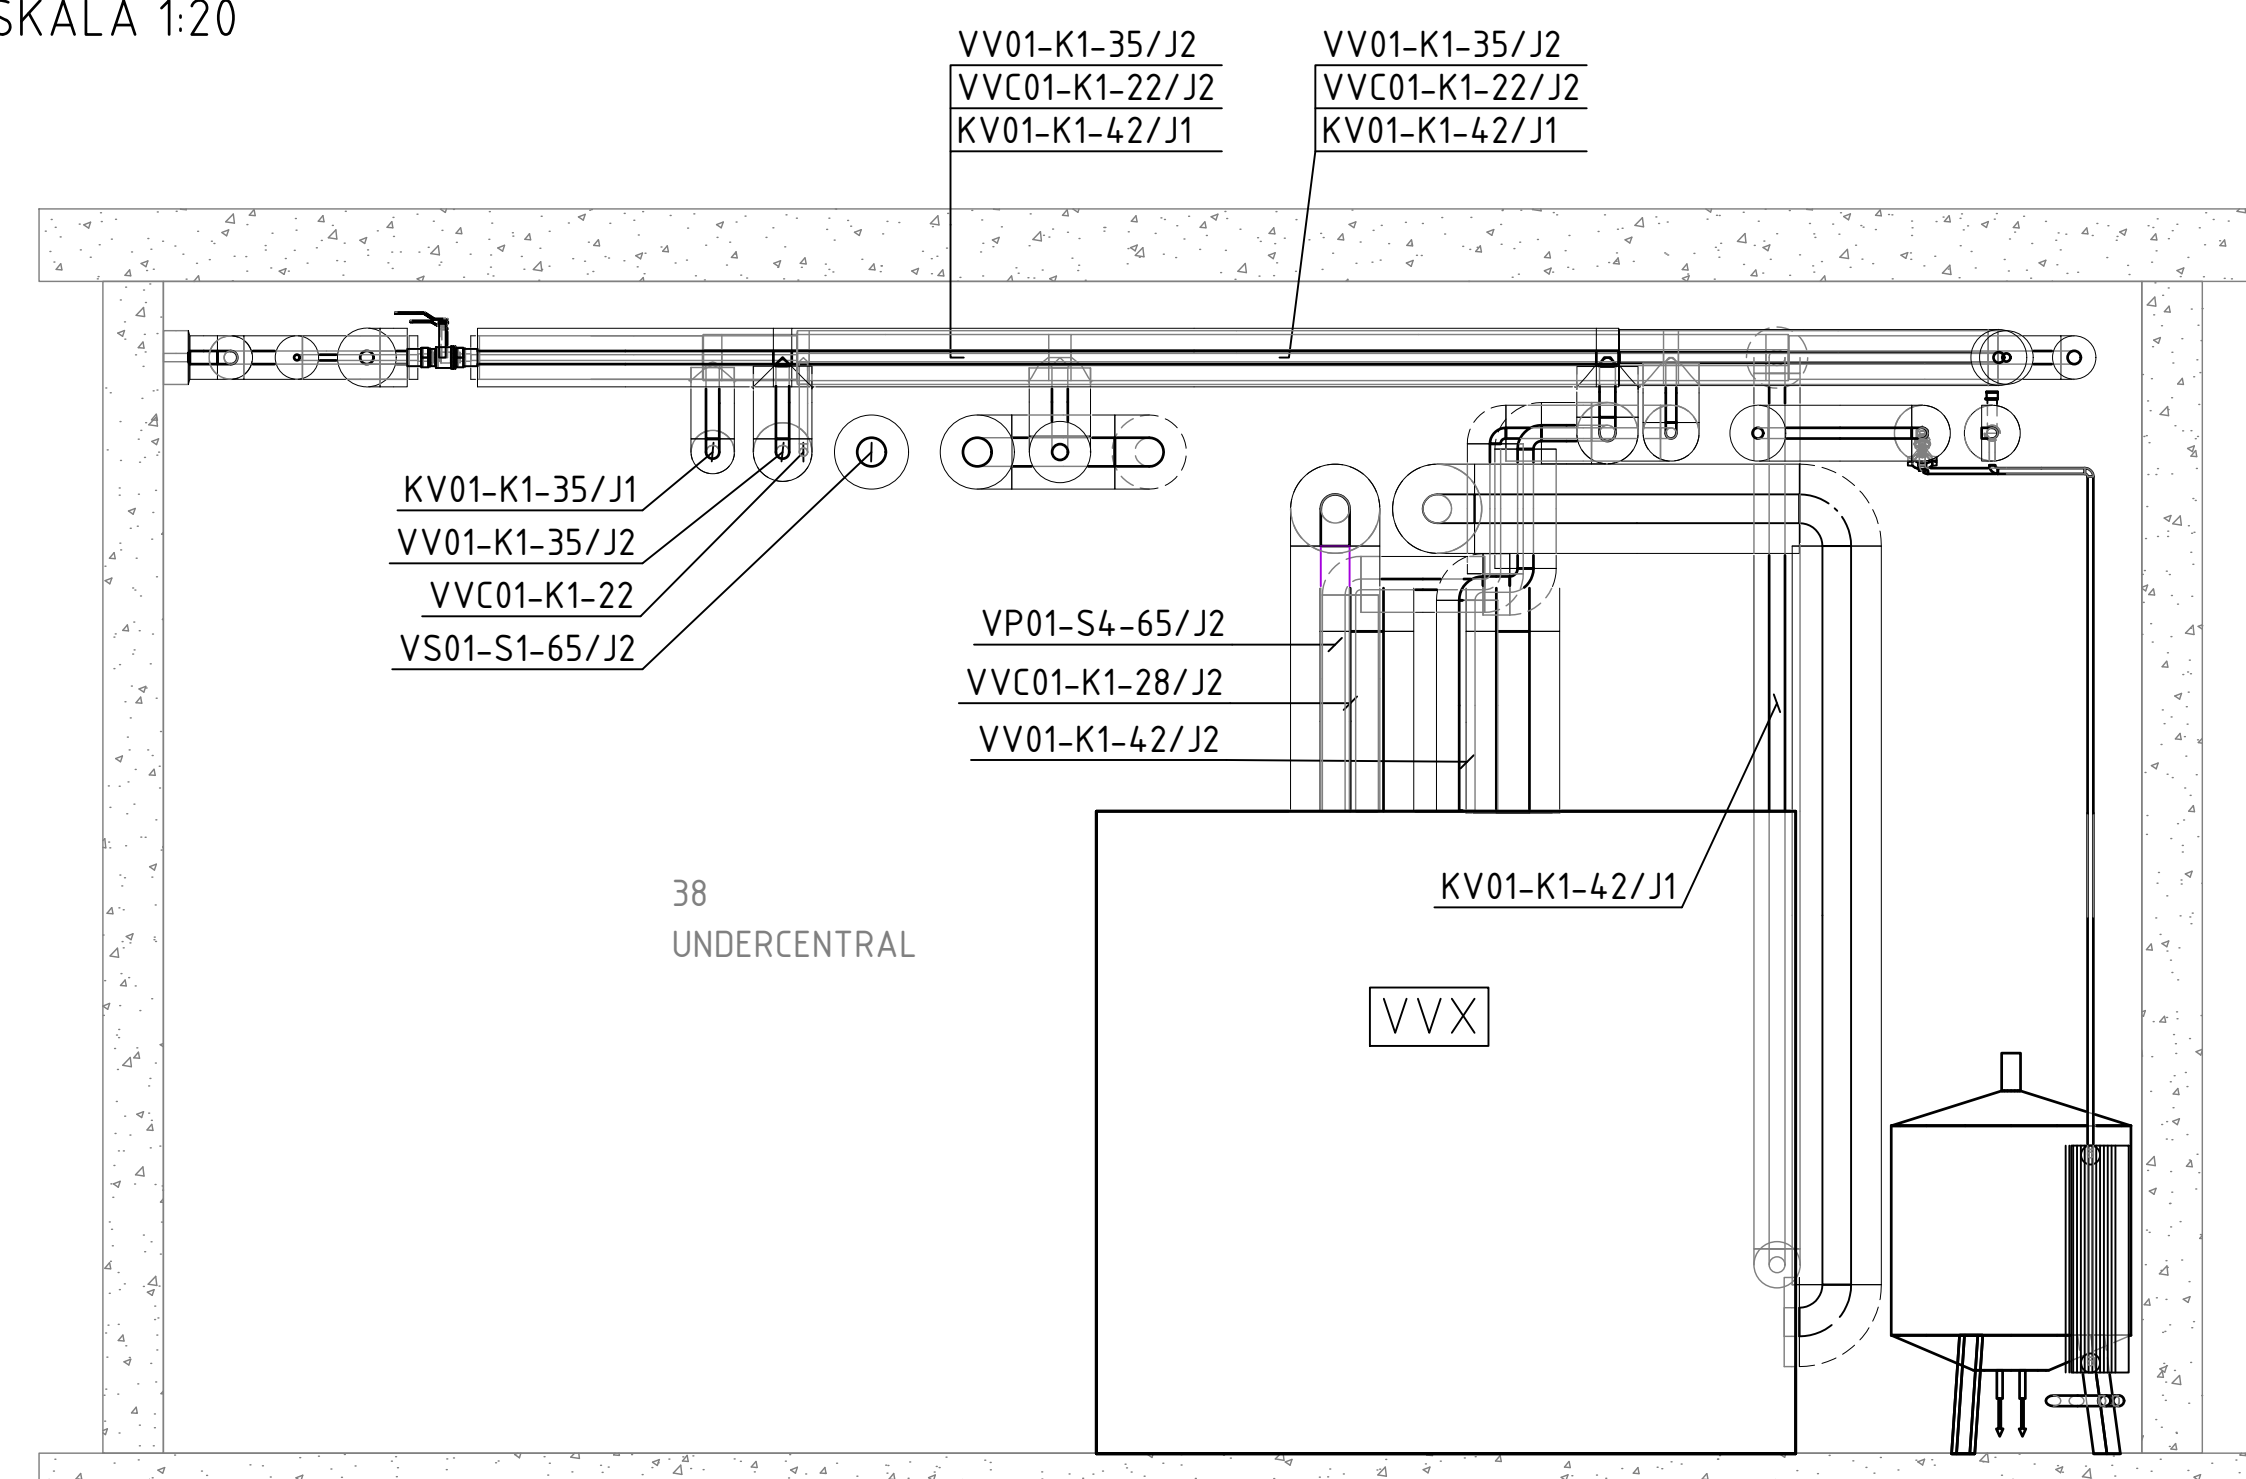

SEKTION 1
SKALA 1:20

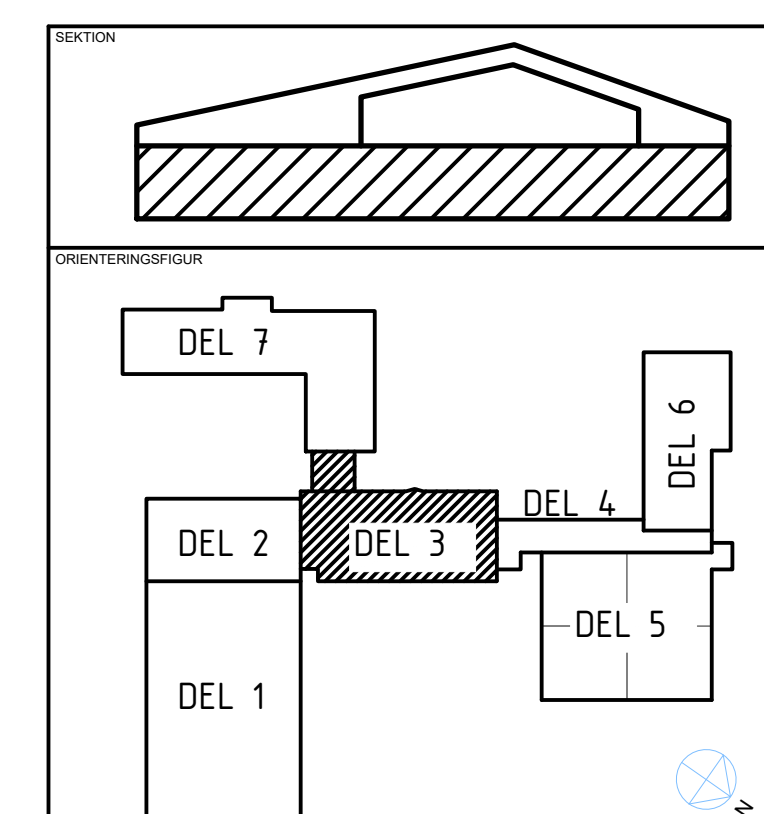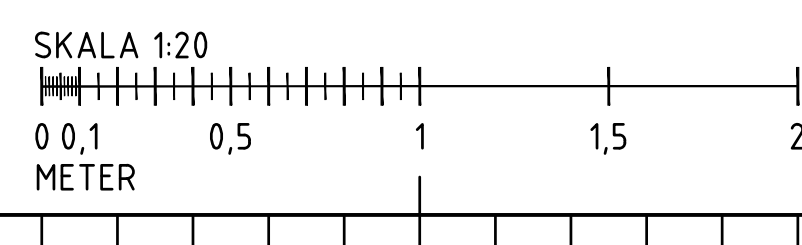

STATUS
FÖRFRÅGNINGSUNDERLAG

HANDLING	BYGGHANDLING
----------	--------------

DATUM	GODKÄND AV	ÄNDRINGS
2024-12-20	T.BERGSTRÖM	

BESTÄLLARE



PROJEKTNAMN

CENTRAALKÖK

OMRÅDE

PROJEKTNUMMER	ADRESS
	YTTRE RINGVÄGEN 4

DIARIENUMMER	FASTIGHET FORDONET 1
--------------	-------------------------

DISCIPLIN	FÖRETAG
VS	NORCONSULT SVERIGE AB

UPPDRAKTSNUMMER	SKAPAD AV
108 83 71	MAN

TELEFON	KONTAKTPERSON
010 141 80 00	JONAS JOHANSSON

BYGGNADSVÄRK	PLUSHÖJD (RH 2000)
	+44,60 (FG)

VÄNINGSPLAN 1	VÄNINGSDEL	DELOMRÅDE DEL 3
------------------	------------	--------------------

SYSTEM
50 RÖRINSTALLATIONER, UC

SPECIFICATION		
PLAN 1		
RETURN/CATEGORY	QVAL	FORMAT

RITNINGSKATEGORI	SKALA	FORMAT
DELPLAN	1:20	A1
DOKUMENTNUMMER	ÄNDRING	

DOKUMENTNUMMER	V-50-6-001	ÄNDERUNG
----------------	------------	----------

FILE NAME:	
------------	--