



FÖRKLARINGSTEXT  
SE RITNING V-50-0-001

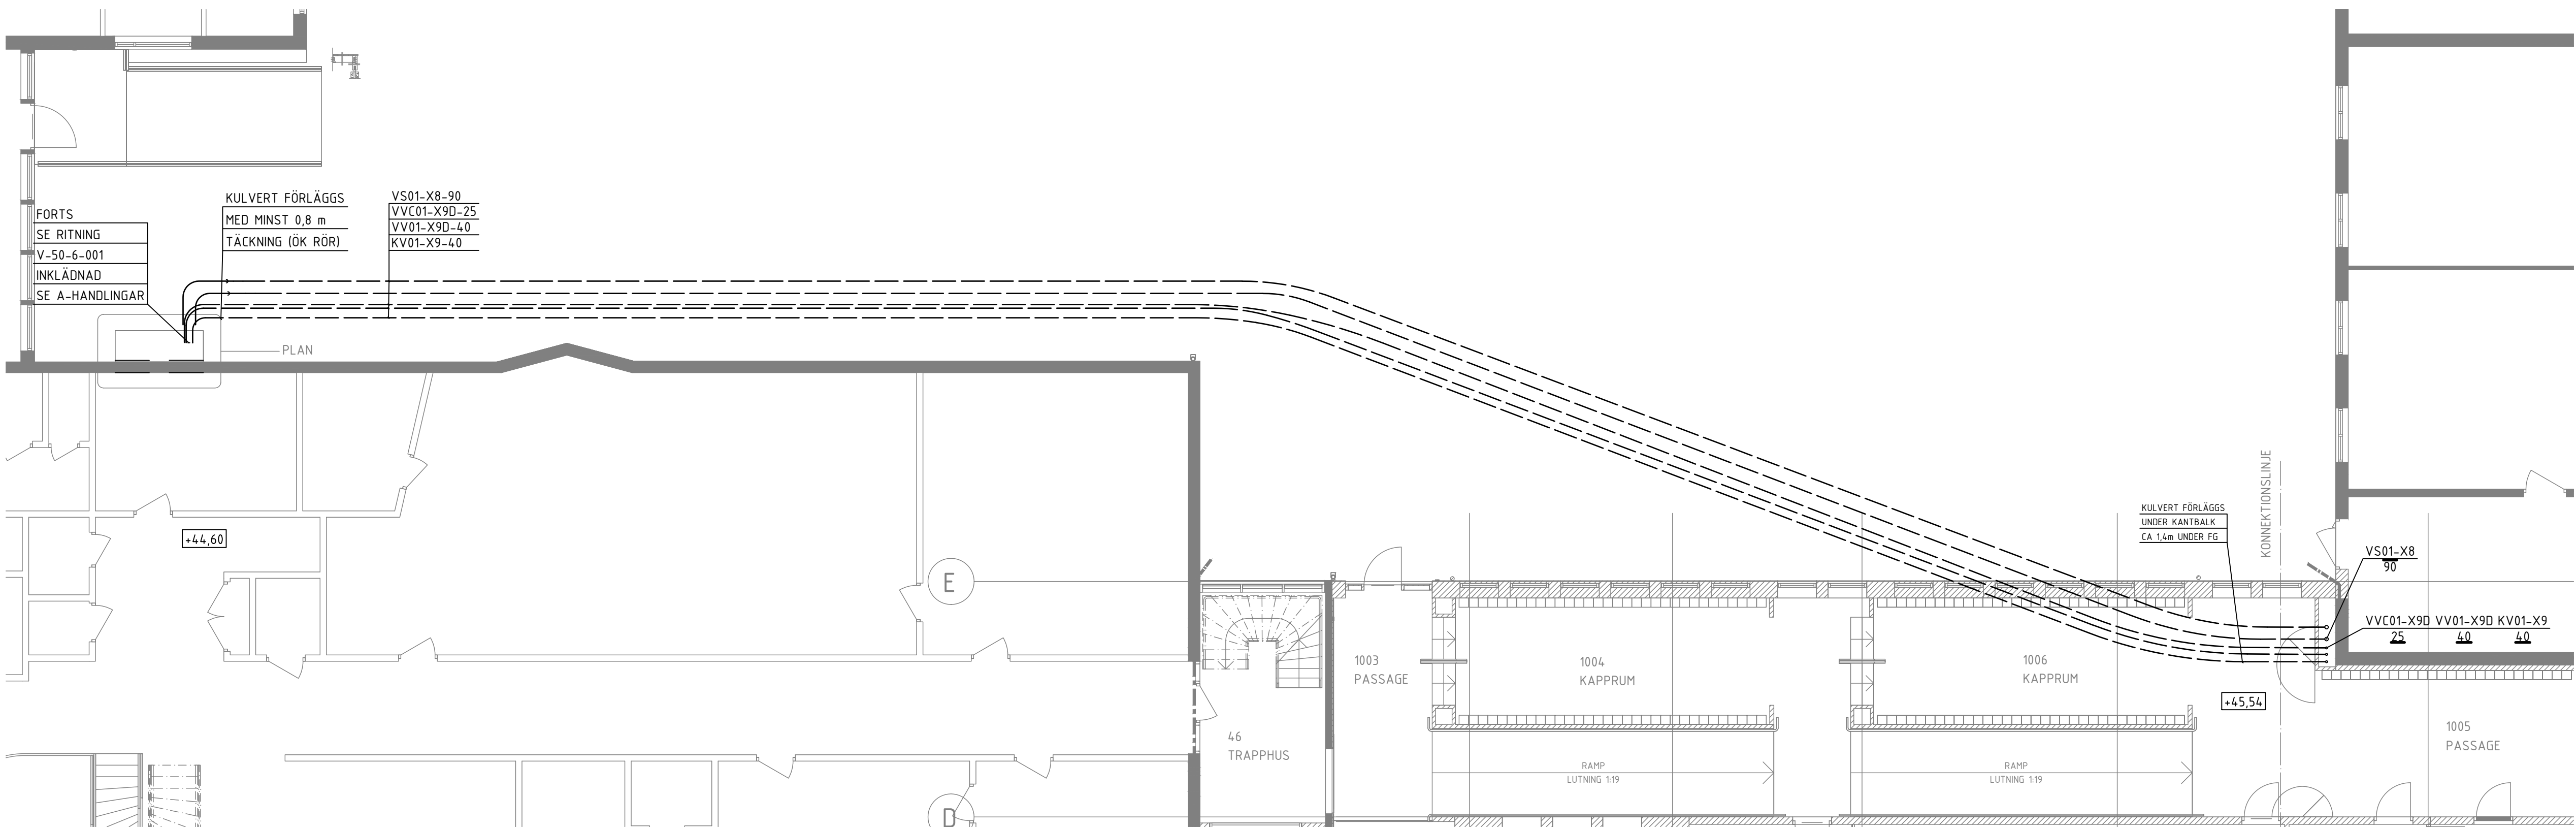

DELPLAN KULVERT  
SKALA 1:100

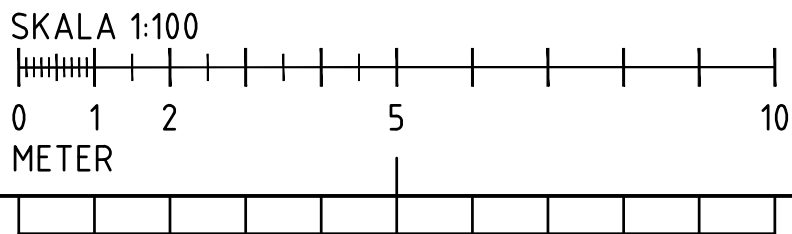

SEKTION

ORIENTERINGSPÅR

STATUS

FÖRFRÅGNINGSUNDERLAG

HANDLING

BYGGHANDLING

DATUM

2024-12-20

GODKÄND AV

T.BERGSTRÖM

BESTÄLLARE

ROBERTSFORS KOMMUN

PROJEKTNAMN

CENTRALKÖK

OMRADE

ROBERTSFORS KOMMUN

PROJEKTNUMMER

ADRESS

YTTRE RINGVÄGEN 4

DIARIENUMMER

FASTIGHET

FÖRDONET 1

DISCIPLIN

FÖRETAG

NORCONSULT SVERIGE AB

OPPFÖRINGSNUMMER

SKAPAD AV

MAN

TELEFON

KONTAKTPERSON

JONAS JOHANSSON

BYGGNADSVÄRK

(KLIMATID Rm 2000)

+44,60 (FG)

VÄNINGSPLAN

VÄNINGSDEL

DELOMRADE

DEL 3, 4

SYSTEM

50 RÖRINSTALLATIONER, KULVERT

PREPARATION

PLAN 1

RITNINGSKATEGORI

DELPLAN

DOKUMENTNUMMER

V-50-6-002

SKALA

1:100

FORMAT

A1

ÄNDRING