


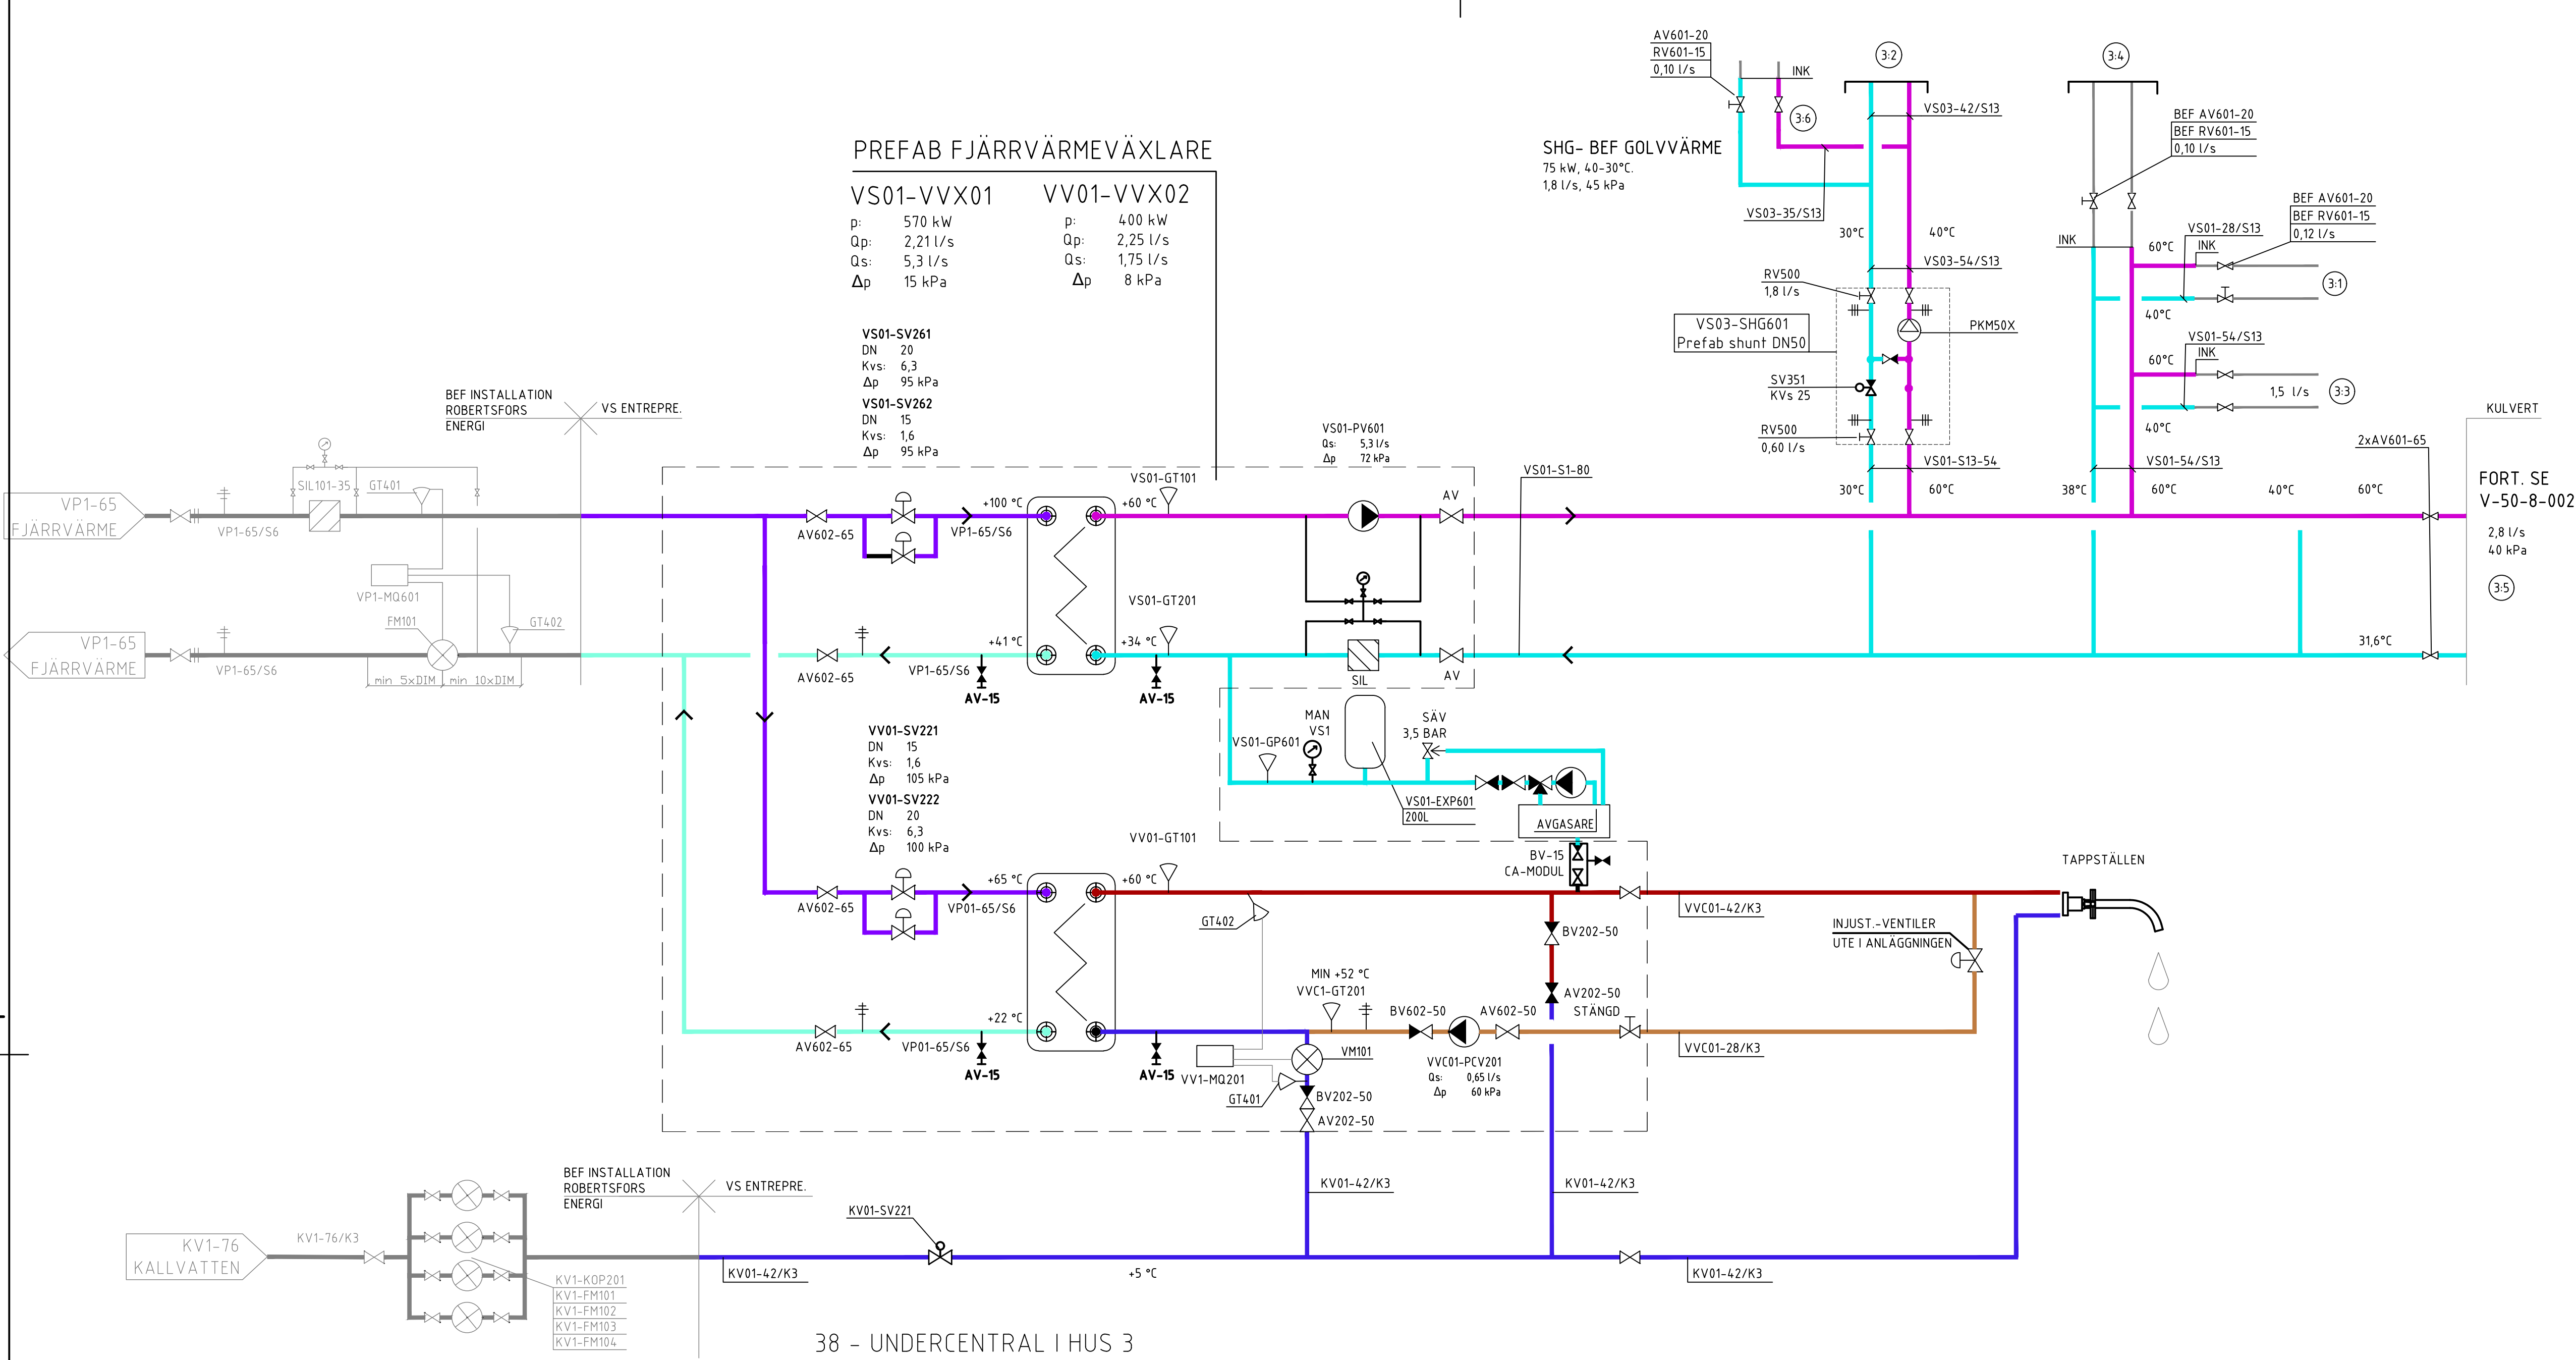

PREFAB FJÄRRVÄRMEVÄXLARE

VS01-VVX01	VV01-VVX02
p: 570 kW	p: 400 kW
Qp: 2,21 l/s	Qp: 2,25 l/s
Qs: 5,3 l/s	Qs: 1,75 l/s
Δp: 15 kPa	Δp: 8 kPa


VS01-SV261
DN 20
Kvs: 6,3
Δp 95 kPa
VS01-SV262
DN 15
Kvs: 1,6
Δp 95 kPa

VV01-SV221
DN 15
Kvs: 1,6
Δp 105 kPa
VV01-SV222
DN 20
Kvs: 6,3
Δp 100 kPa

SHG- BEF GOLVVÄRME
75 kW, 40-30°C
1,8 l/s, 45 kPa

VS03-SHG601
Prefab shunt DN50
SV351
KVs 25
RV500
0,60 l/s

FÖRKLARINGSTEXT
SE RITNING V-50-0-001

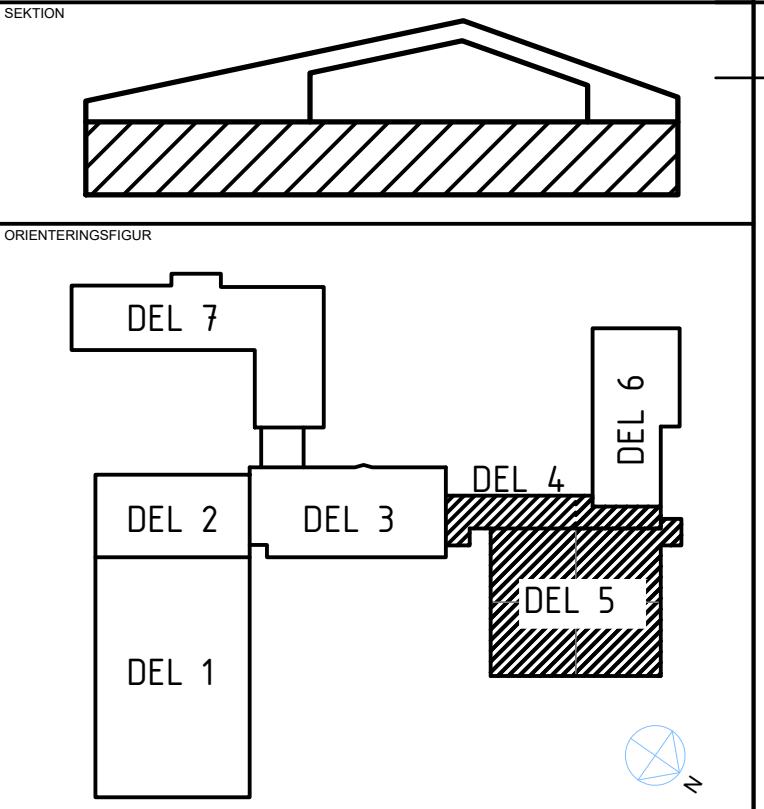

SEKTION		
ORIENTERINGSPÅR		
STATUS		
HÄNDLING		
DATUM	GODKÄND AV	ÄNDRINGS PM
2024-12-20	T.BERGSTRÖM	
BESTÄLLARE		
PROJEKTNAMN		
OMRADE		
PROJEKTNUMMER	FÖRRETT	
DARIENUMMER	FASTIGHET	
DISCIPLIN	FÖRETAG	
OPPFÖRINGSNUMMER	SKAPAD AV	
TELEFON	KONTAKTPERSON	
BYGGNADSVÄRME	(FLUSHÖJD RIM 2000)	
VÄNINGSPLAN	VÄNINGSDEL	DELOMRÅDE
1		DEL 3, 4, 5
SYSTEM		
BESKRIVNING		
FLÖDESSKEMA		
RITNINGSKATEGORI	SKALA	FORMAT
SCHEMA		A1
DOKUMENTNUMMER	ÄNDRING	
V-50-8-001		

FLÄMM: