
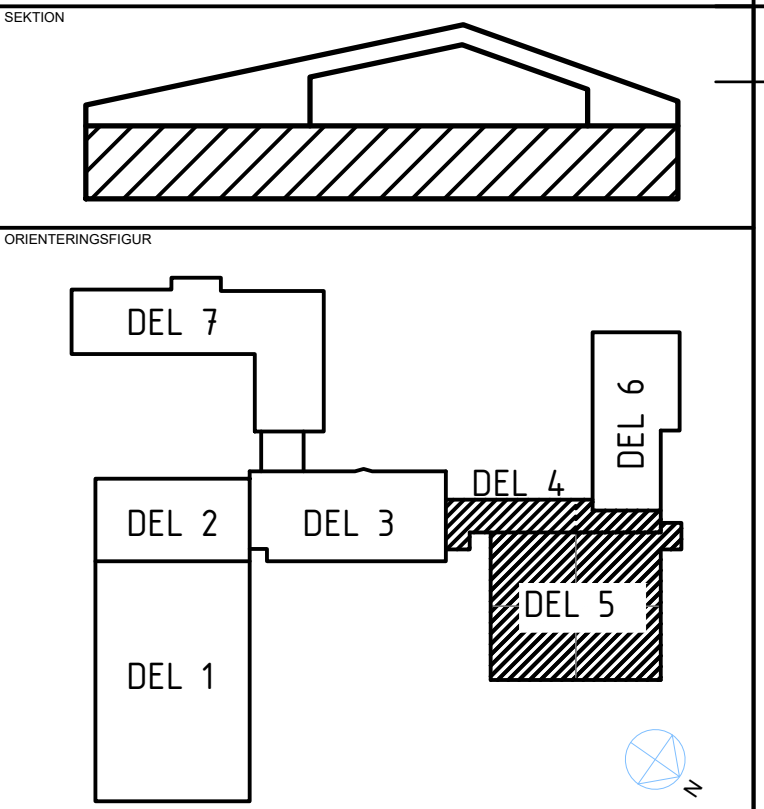


FÖRKLARINGSTEXT
SE RITNING V-50-0-001

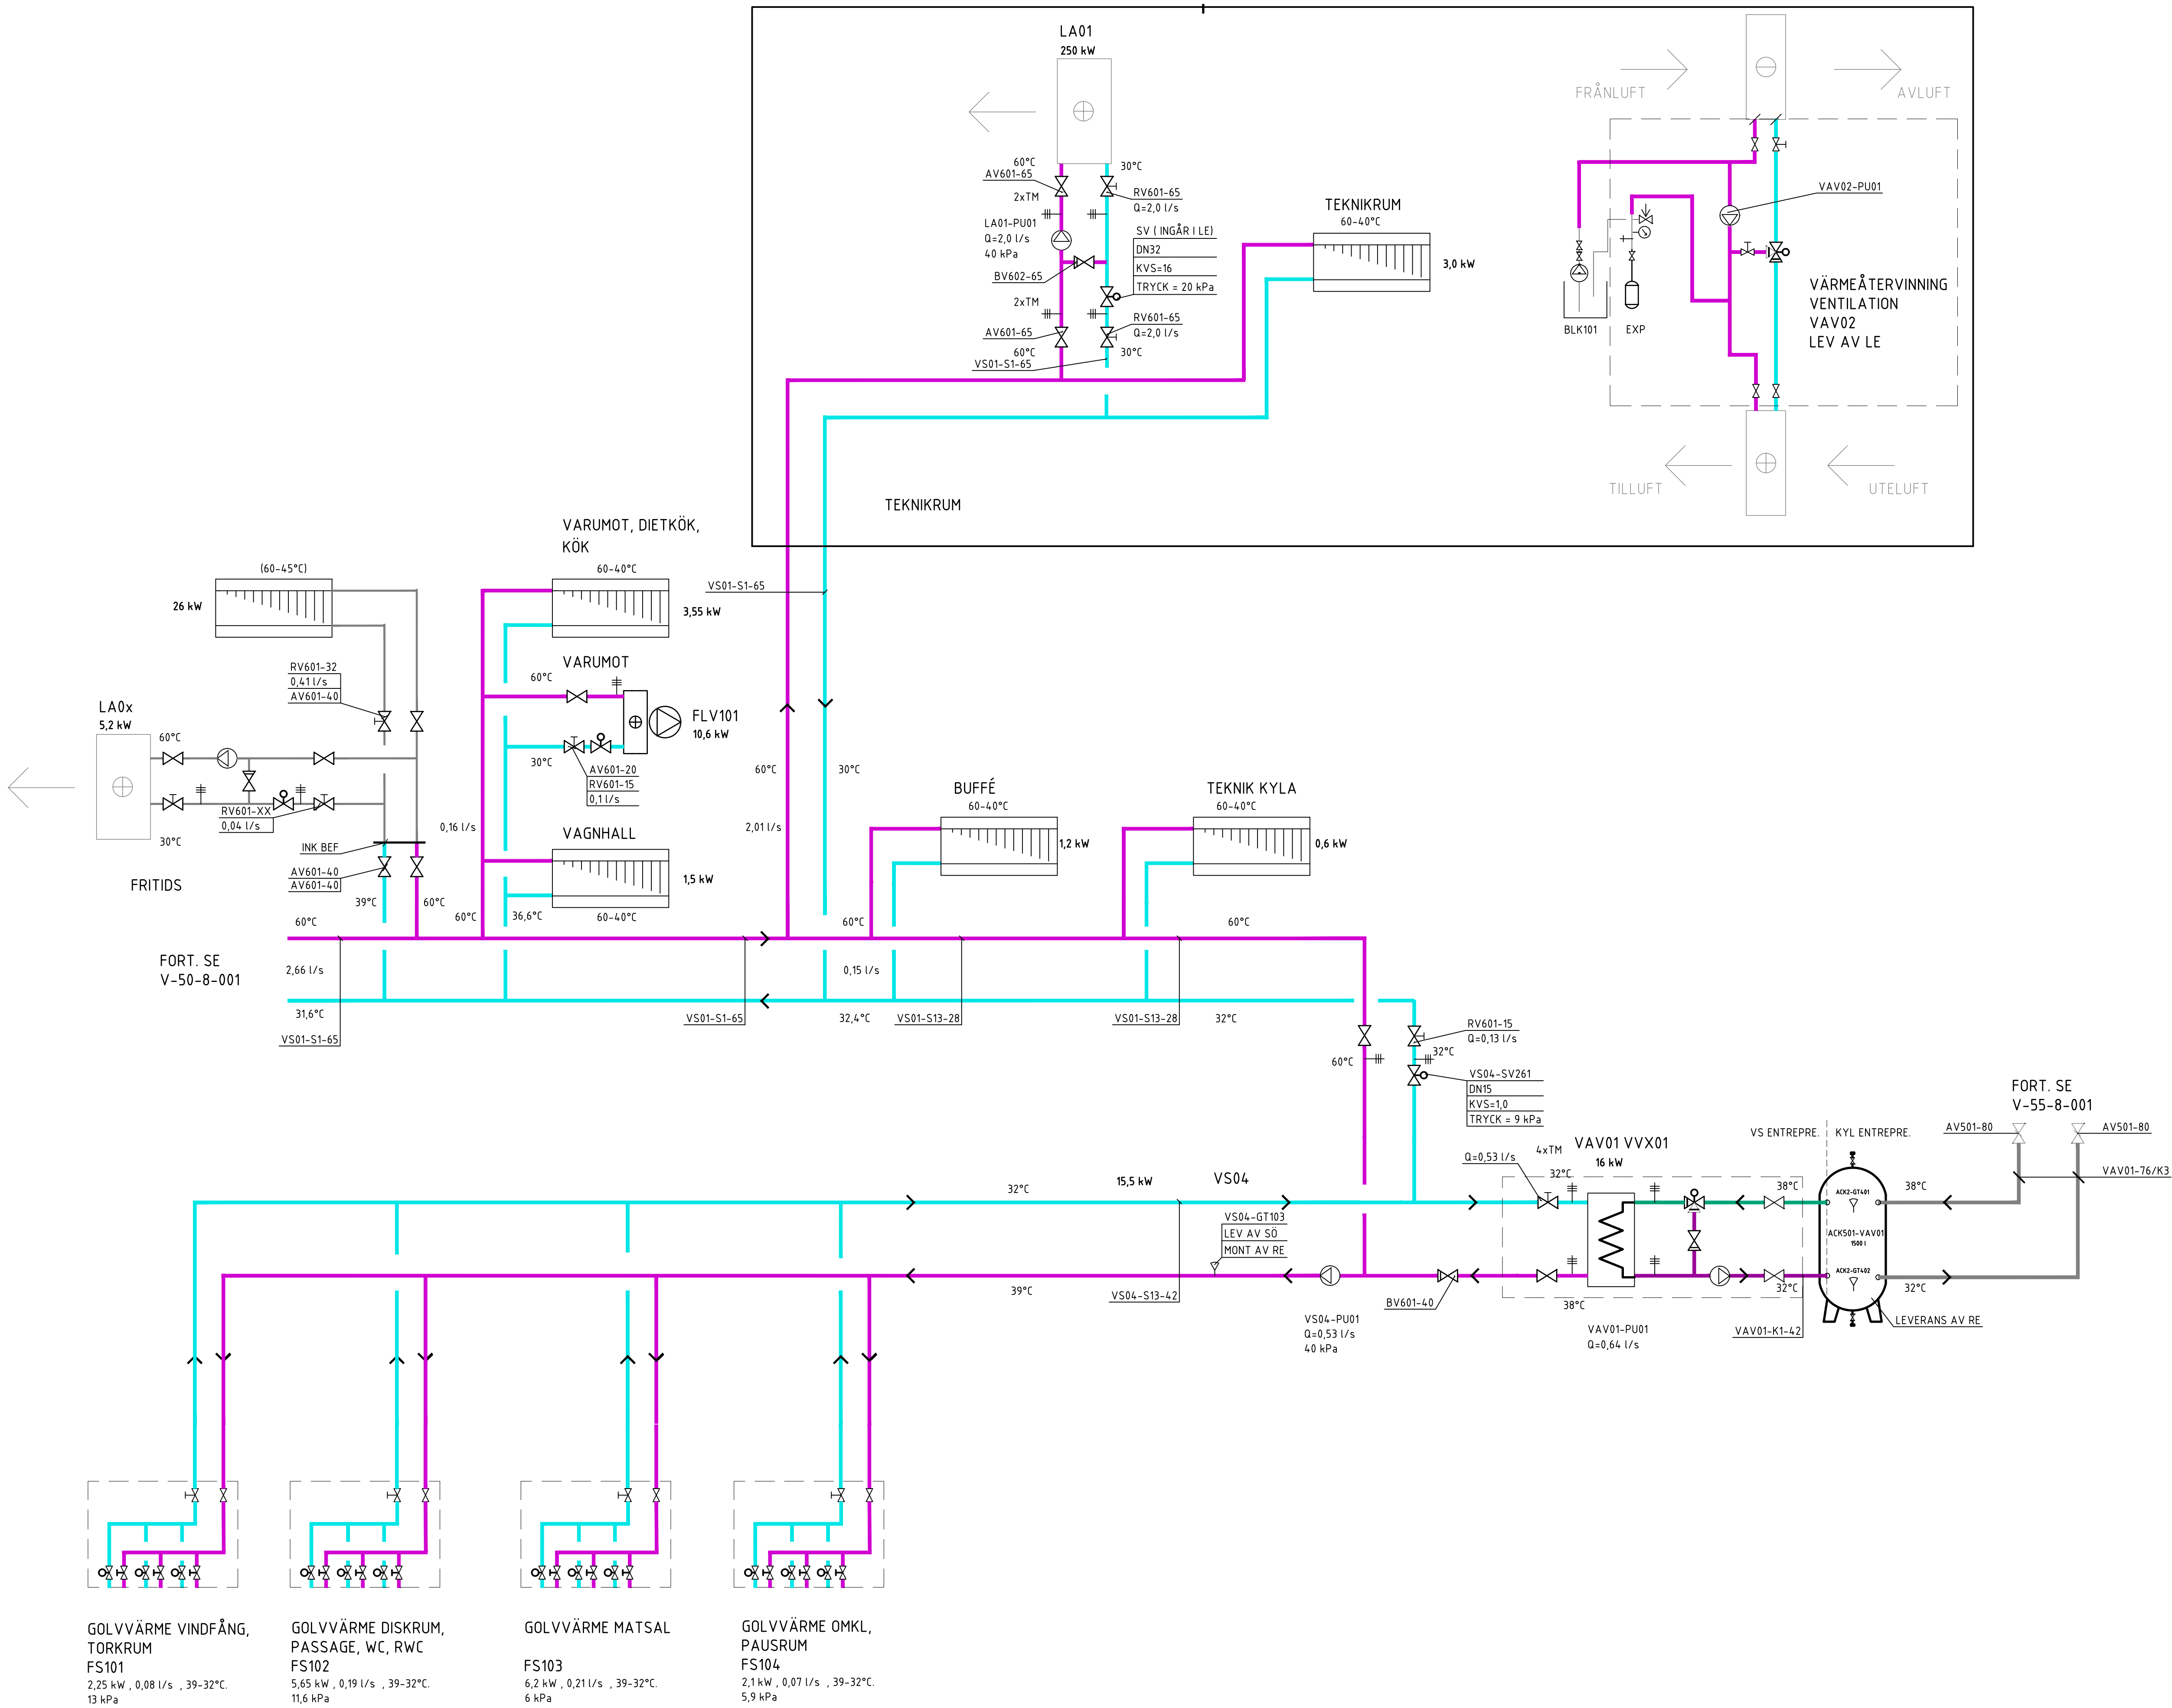

STATUS			
FÖRFRÅGNINGSUNDERLAG			
HANDLING			
BYGGHANDLING			
DATUM	2024-12-20	GODKÄND AV	T.BERGSTRÖM
BESTÄLLARE		ROBERTSFORS KOMMUN	
PROJEKTNAMN			
CENTRALEKÖK			
OMRÅDE			
ROBERTSFORS KOMMUN			
PROJEKTNUMMER	YTTRE RINGVÄGEN 4		
DARIENUMMER	FÖRORDNET 1		
DISCIPLIN	NORCONSULT SVERIGE AB		
OPPRORINGSNUMMER	MAN		
TELEFON	010 141 80 00		
BYGGNADSVÄRDE	+49 54 (FG)		
VÄRNINGSPÅN	1	VÄRNINGSDI	DEL 4, 5
SYSTEM			
50 RÖRINSTALLATIONER			
FLODESSCHEMA			
RITNINGSSKÄL		SKALA	FORMAT
SCHEMA			A1
DOKUMENTNUMMER		INRÖRING	
V-50-8-002			