
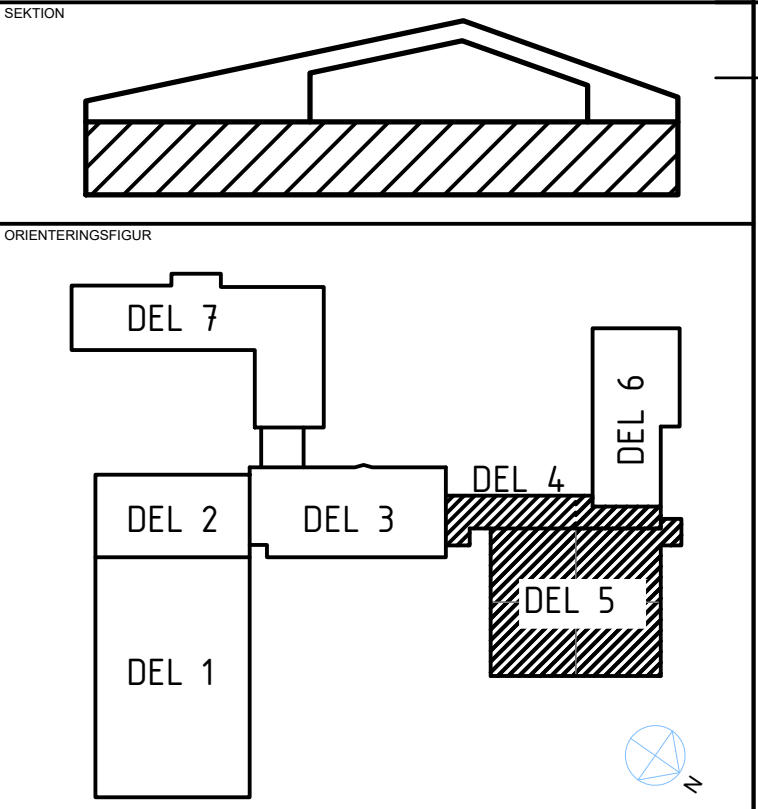
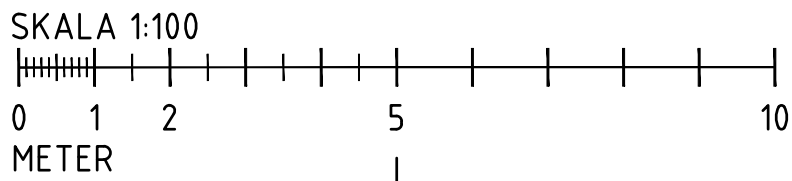


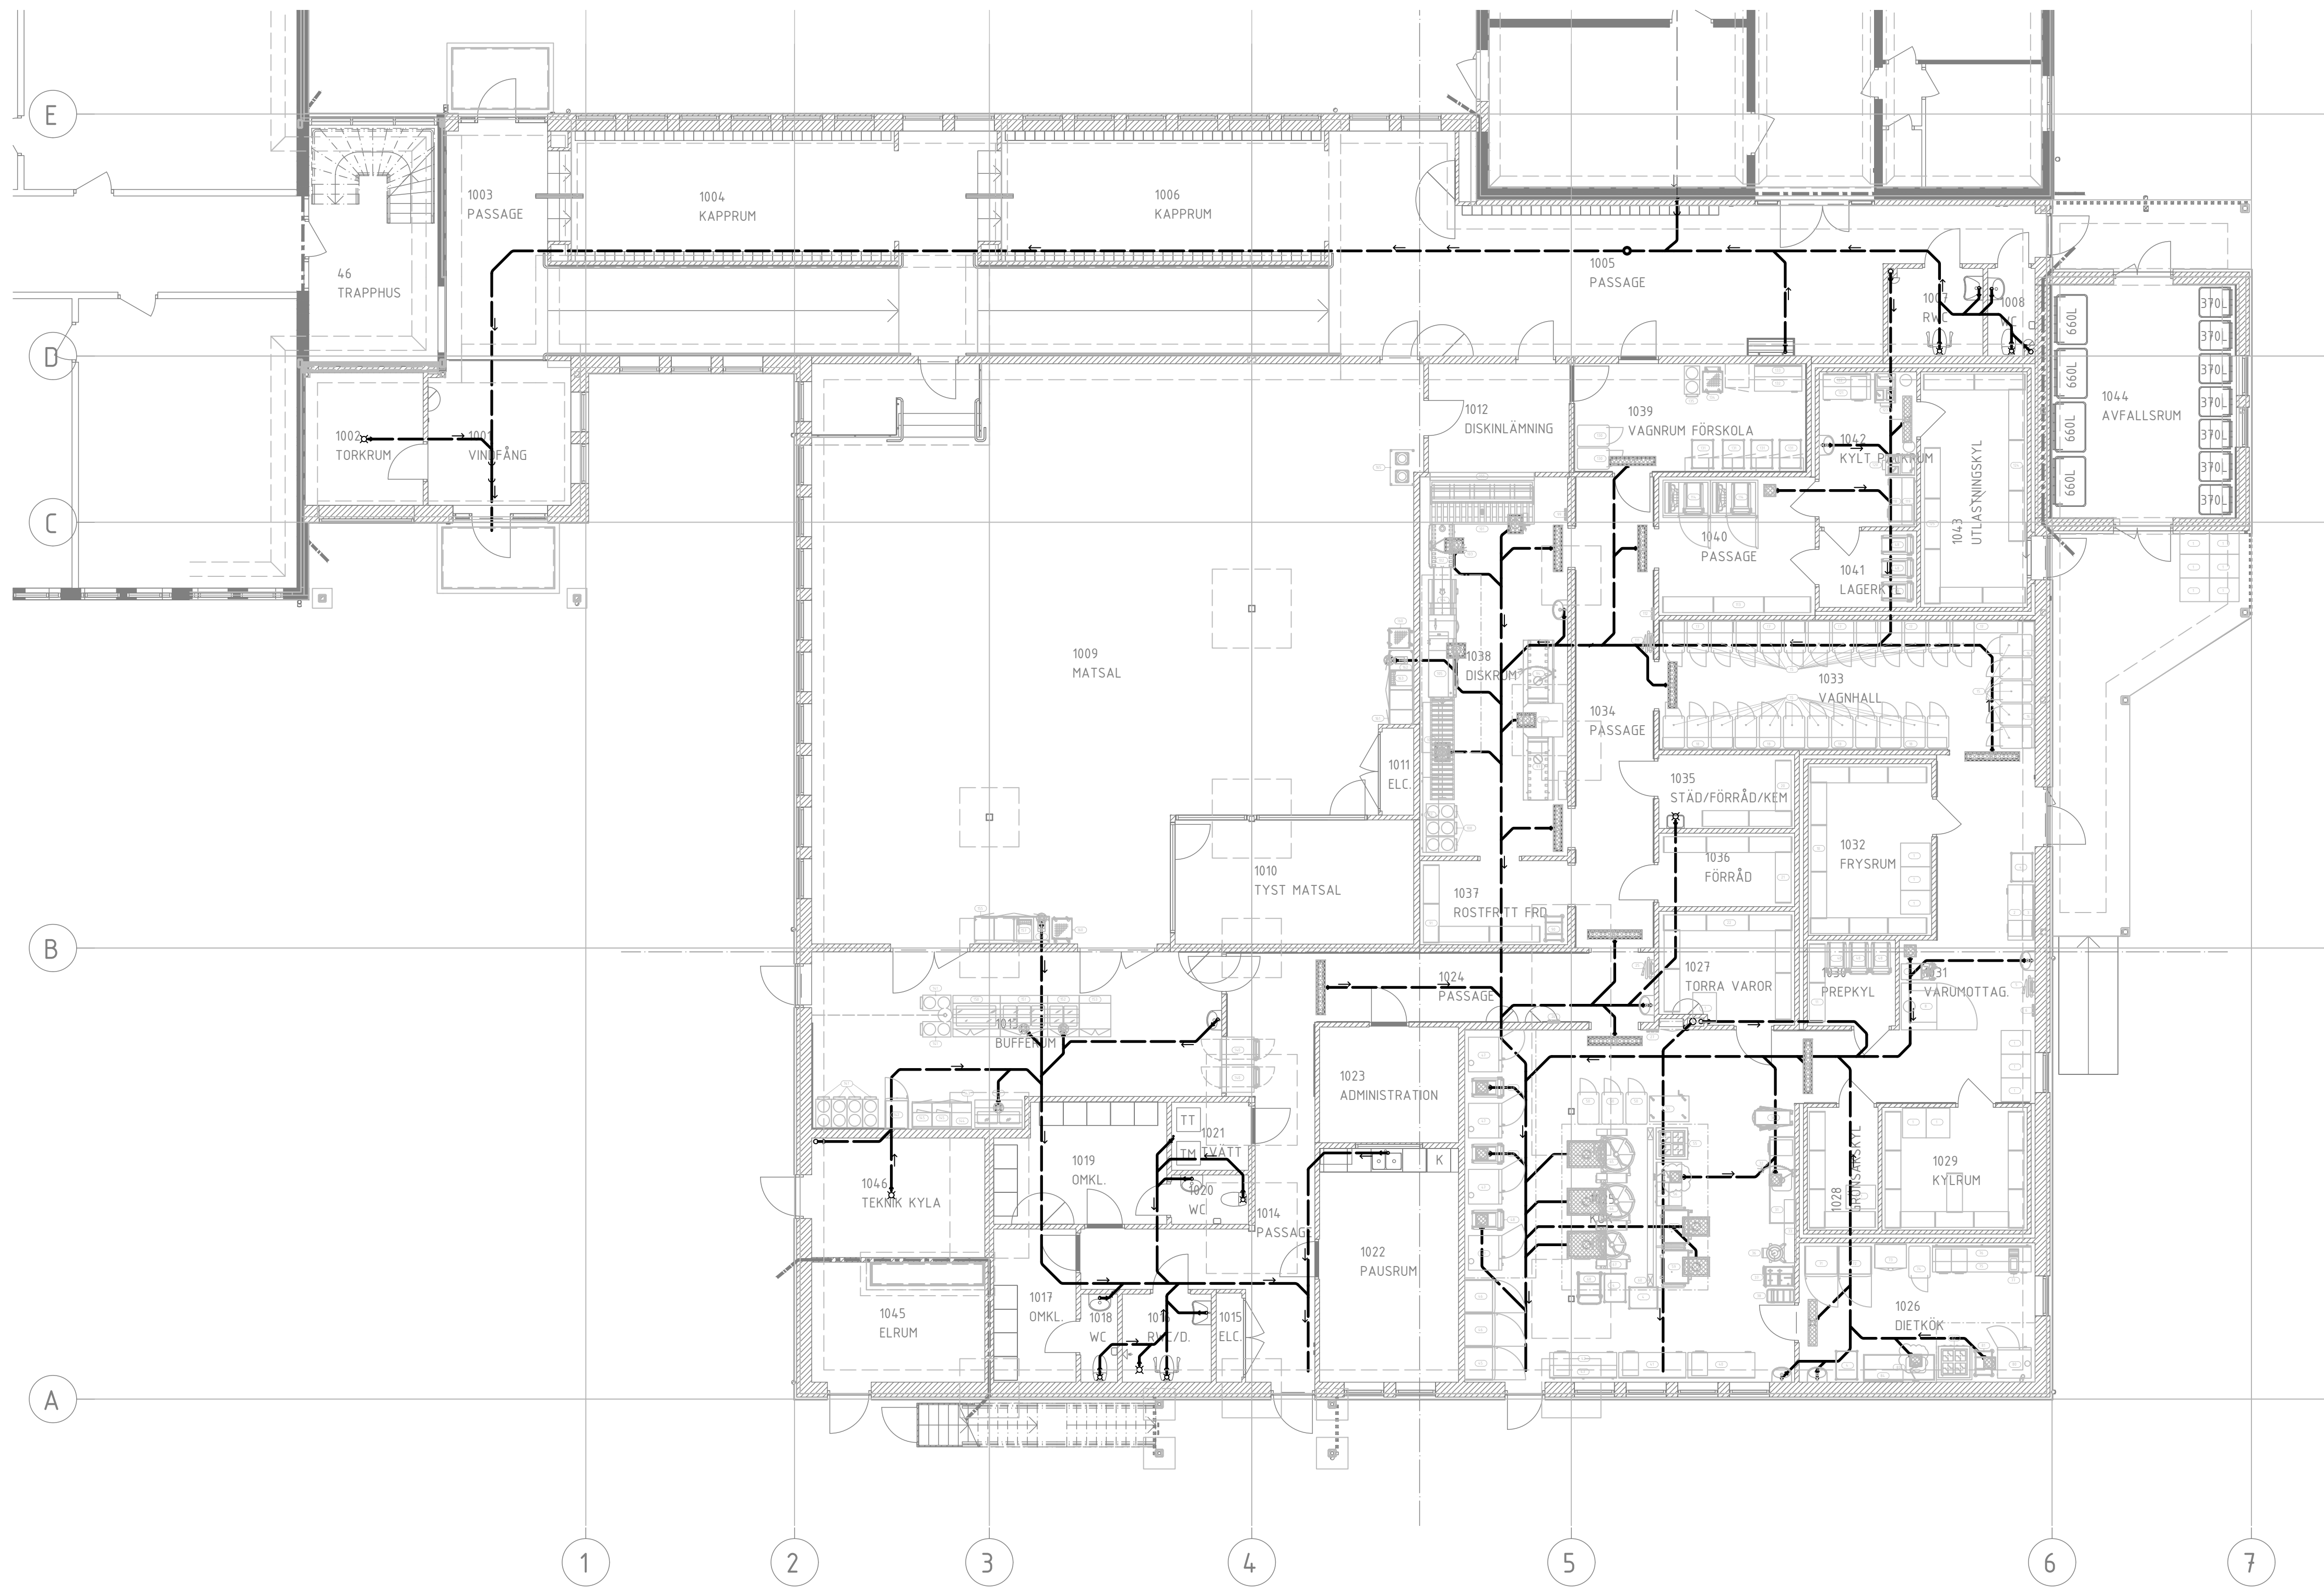

ORIENTERINGSPÅR		
DEL 1, DEL 2, DEL 3, DEL 4, DEL 5, DEL 6, DEL 7		
STATUS		
FÖRFRÅGNINGSUNDERLAG		
HANDLING		
BYGGHANDLING		
DATUM	GODKÄND AV	ÄNDRINGS PM
2024-12-20	T.BERGSTRÖM	
BESTÄLLARE		
ROBERTSFORS KOMMUN		
PROJEKTNAMN		
CENTRALKÖK		
OMRADE		
ROBERTSFORS KOMMUN		
PROJEKTNUMMER	FÖRETAG	
	YTIRE RINGVÄGEN 4	
DARIENUMMER	FÖRETAG	
	FORDONET 1	
DISCIPLIN	FÖRETAG	
VS	NORCONSULT SVERIGE AB	
OPPFÖRINGSNUMMER	SKAPAD AV	
108 83 71	MAN	
TELEFON	KONTAKTPERSON	
010 141 80 00	JONAS JOHANSSON	
BYGGNADSVÄRDE	(KLIMATKORREKTUR 2000)	
	+44,60, +45,07, +45,54 (FG)	
VÄNINGSPLAN	VÄNINGSDEL	DELOMRÅDE
1		DEL 4, 5
SYSTEM		
53 SPILLVATTENINSTALLATIONER		
PLAN 0 - ÖVERSIKT, UNDER PLATTA		
RITNINGSKATEGORI	SKALA	FORMAT
PLAN	1:100	A1
DOKUMENTNUMMER	ÄNDRING	
V-53-1-001		