
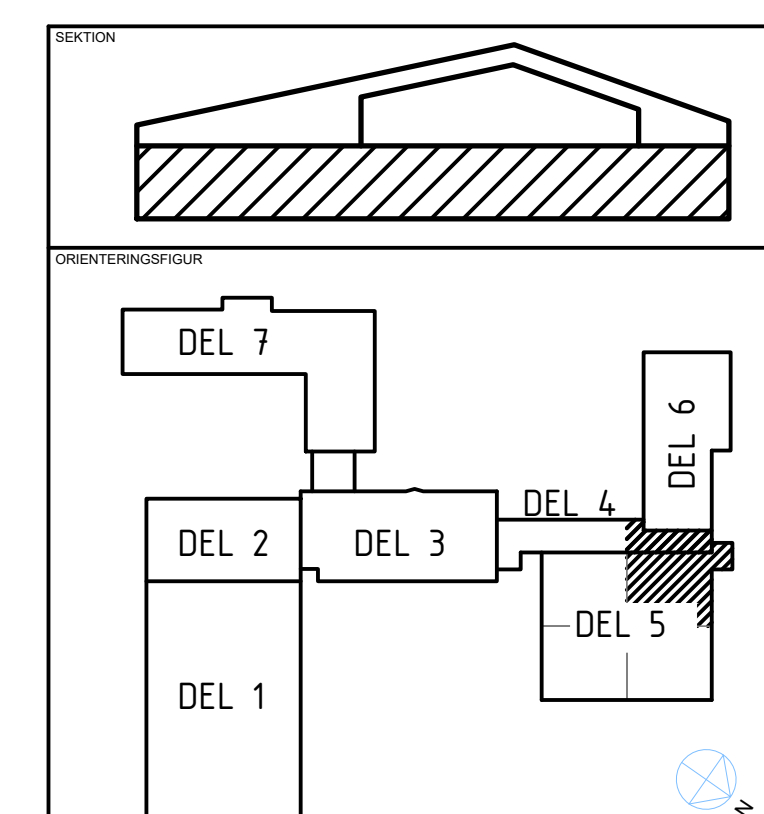


FÖRKLARINGSTEXT
SE RITNING V-50-0-001

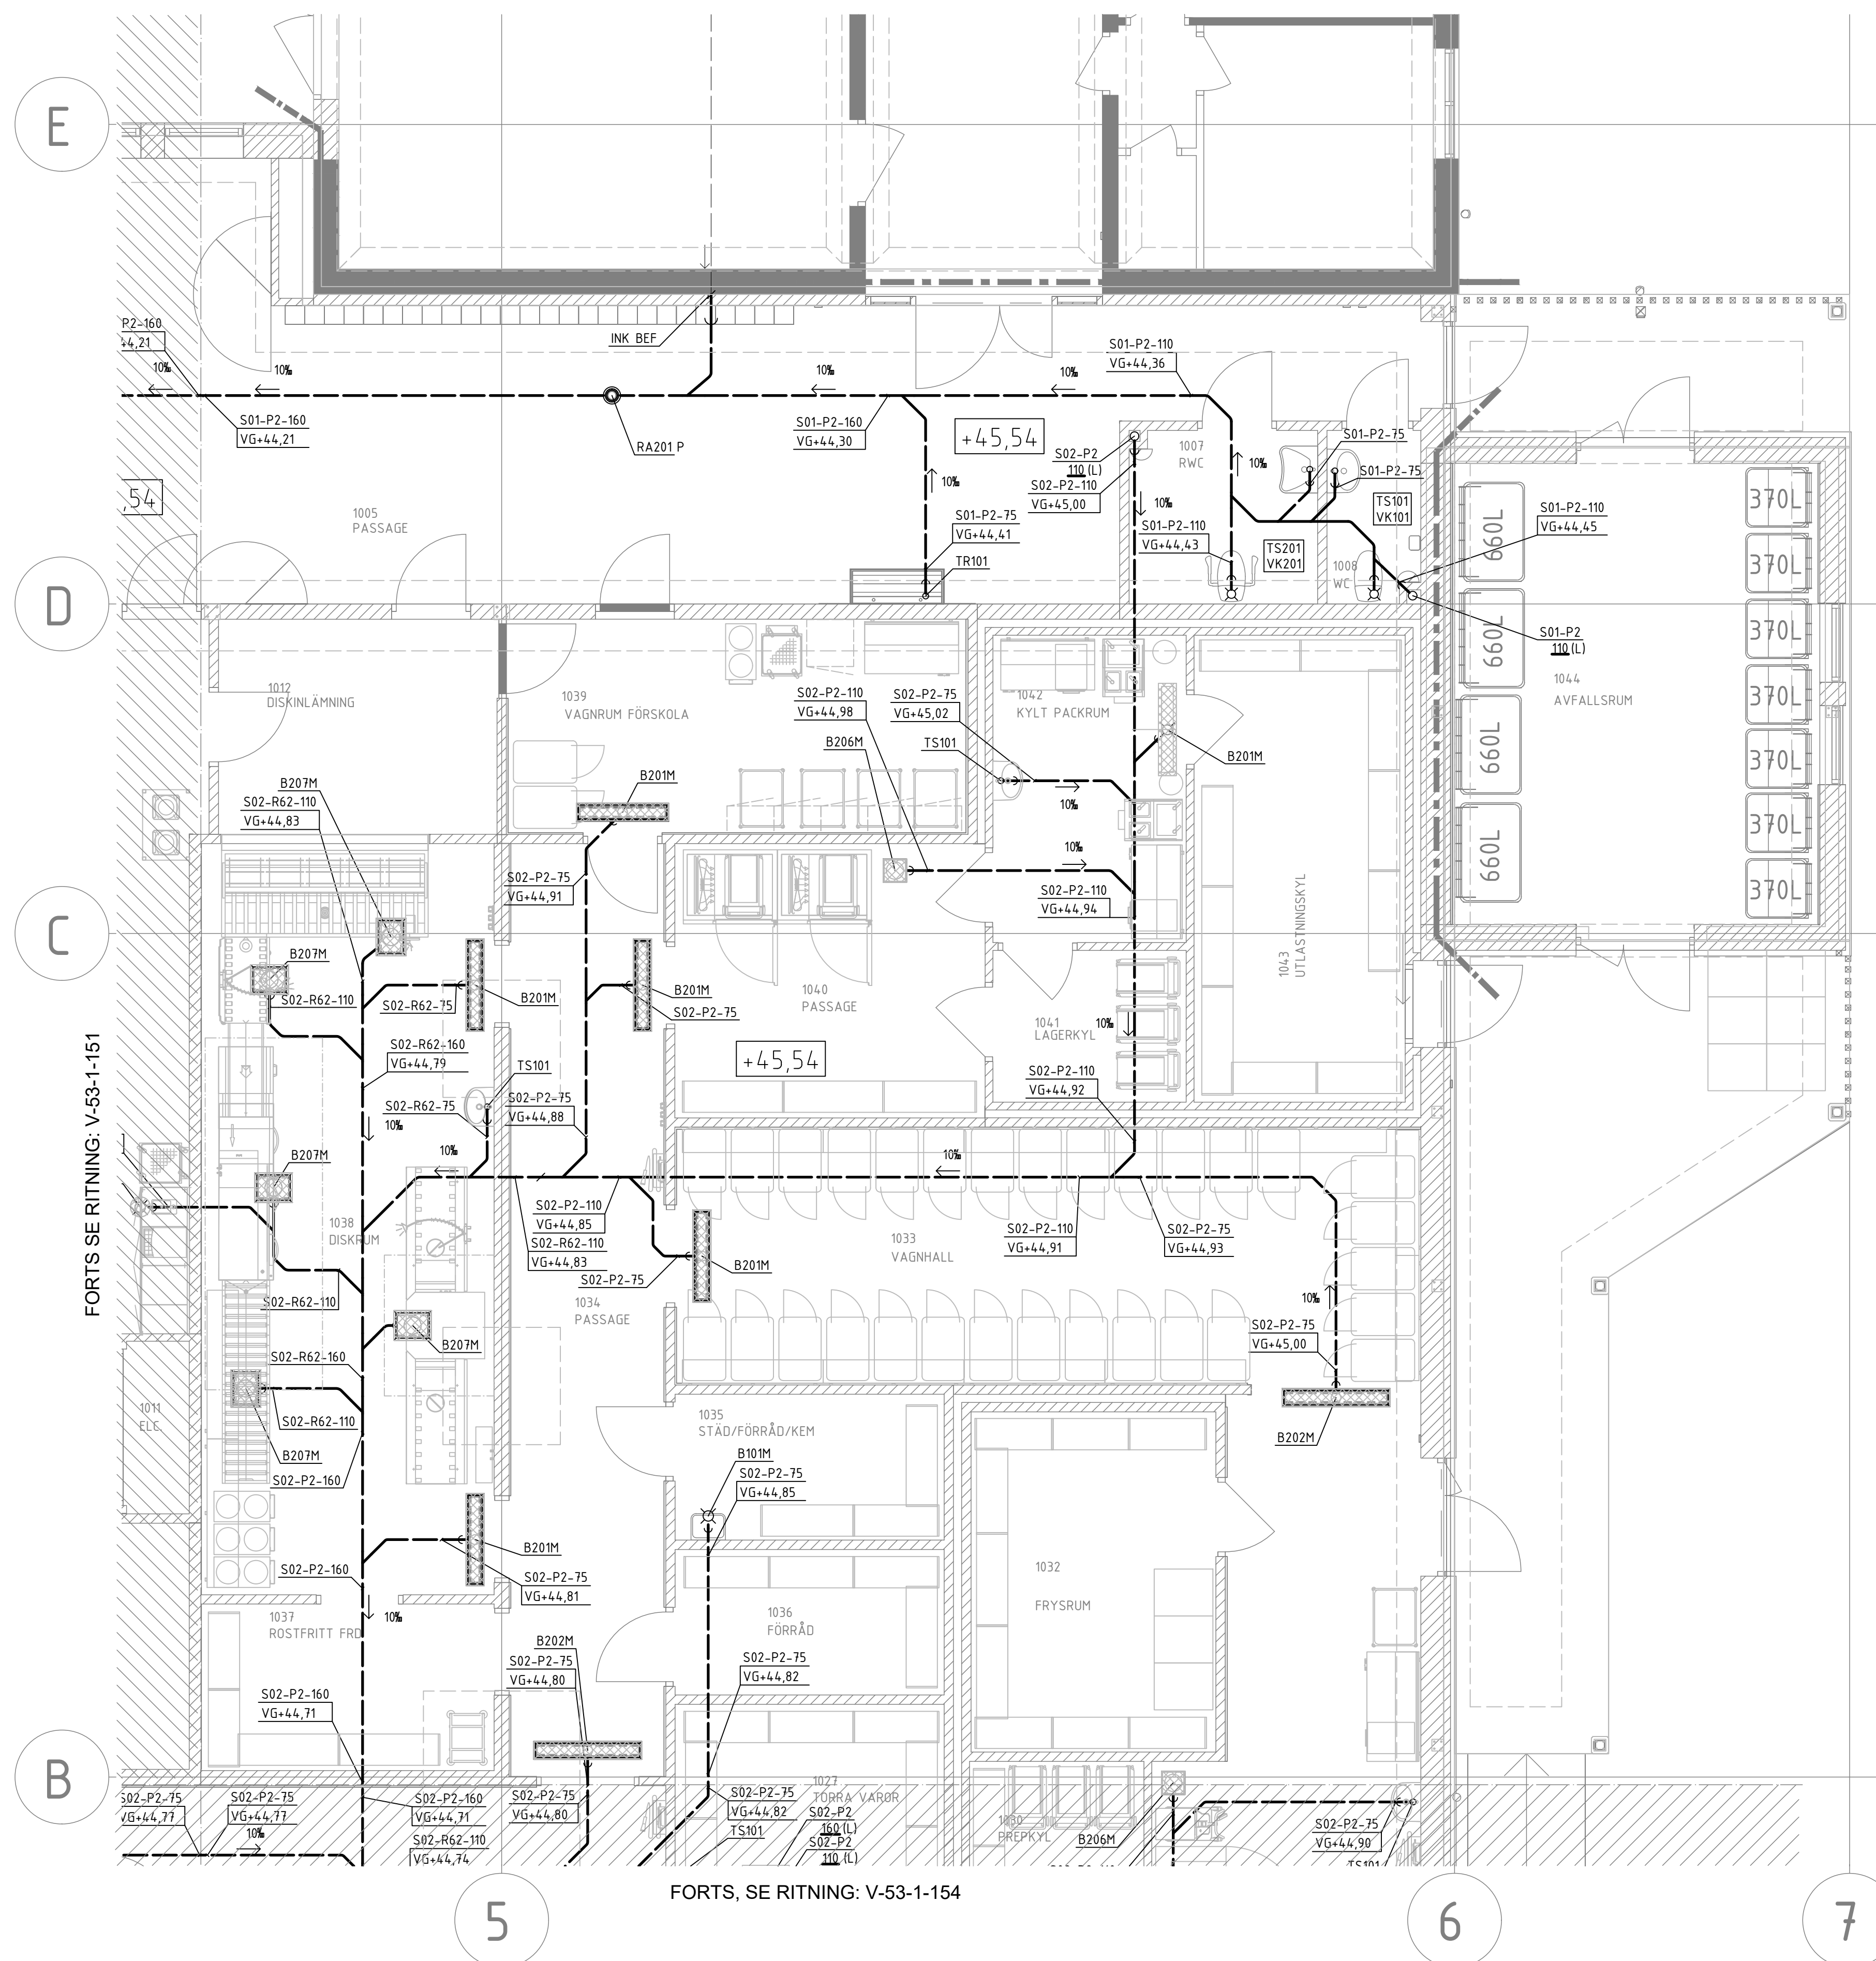

STATUS FÖRFRÅGNINGSUNDERLAG

HANDLING	BYGGHANDLING
----------	--------------

DATUM	GODKÄND AV	ÄNDRINGS
2024-12-20	T.BERGSTRÖM	

2024-12-20	FIBERGLASS	
BESTÄLLARE		



PROJEKTNAMN

CENTRALEKÖK

OMRÅDE

PROJEKTNUMMER	ADRESS
	YTTRE RINGVÄGEN 4

DIARIENUMMER	FASTIGHET FORDONET 1
--------------	-------------------------

DISCIPLIN	FÖRETAG
VS	NORCONSULT SVERIGE AB

UPPDRAGSNUMMER 108 83 71	SKAPAD AV MAN
TELEFON	KONTAKTPERSON

TELEFON	KONTAKTPERSON
010 141 80 00	JONAS JOHANSSON
BYGGNADSVÄRK	011 884 10 00 (RM 3000)

BYGGNADSVÄRK		PLUSHÖJD (RH 2000)
		+45,54 (FG)
VÄNINGSPLAN	VÄNINGSDEI	DELOMRÅDE

VÄNINGSPLAN	VÄNINGSDEL	DELOMRÅDE
1		DEL 4.2, 5.2
SYSTEM		

53 SPILLVATTENINSTALLATIONER

SPECIFIKATION		
PLAN 0 - DEL 4.2, 5.2, UNDER PLATTA		
RITNINGSKATEGORI	SKALA	FORMAT

RTNINGSKATEGORI	SKALA	FORMAT
PLAN	1:50	A1
DOKUMENTNUMMER	ÄNDRING	

DOCUMENT NUMBER	V-53-1-052	REVISION
-----------------	------------	----------

SKALA 1:50

0 1 2 3 4 5

METER

THE BOARD: